



| BILL OF MATERIAL     |       |           |      |                                                   |                    |                          |         |
|----------------------|-------|-----------|------|---------------------------------------------------|--------------------|--------------------------|---------|
| LINE #               | QTY   | PC        | MARK | DESCRIPTION                                       | LENGTH             | WEIGHT                   | ADVANCE |
|                      | TOTAL |           | MARK |                                                   |                    | TOTAL                    | MILL #  |
| ONE F-08.00C1        |       |           |      |                                                   |                    |                          |         |
| 1                    |       | F-08.00C1 |      | COLUMN                                            |                    | 390                      |         |
|                      |       |           |      | HSS6x6x $\frac{3}{8}$                             | 12 9               | S/E A500C                | 350     |
| 1                    |       | bp1002    |      | PL $\frac{1}{4}$ x8                               | 1 2                | A36                      | 40      |
| ONE F-08.00C2        |       |           |      |                                                   |                    |                          |         |
| 1                    |       | F-08.00C2 |      | COLUMN                                            |                    | 329                      |         |
|                      |       |           |      | HSS6x6x $\frac{3}{8}$                             | 10 4               | S/E A500C                | 284     |
| 1                    |       | p1964     |      | PL $\frac{1}{4}$ x7                               | 1 6                | A36                      | 45      |
| FIELD BOLTS          |       |           |      |                                                   |                    |                          |         |
| 2                    |       |           |      | $\frac{3}{4}$ Dia HILTI HAS V-36                  | 0 8                | ( $\frac{3}{4}$ " EMBED) |         |
| w/HILTI HY-200 EPOXY |       |           |      |                                                   |                    |                          |         |
| ONE F-08.00C3        |       |           |      |                                                   |                    |                          |         |
| 1                    |       | F-08.00C3 |      | COLUMN                                            |                    | 396                      |         |
|                      |       |           |      | HSS6x6x $\frac{3}{8}$                             | 13 0 $\frac{3}{4}$ | SIZE A500C               | 359     |
| 1                    |       | p3367     |      | PL $\frac{3}{8}$ x6 $\frac{1}{2}$                 | 1 6                | A36                      | 21      |
| 1                    |       | p230      |      | PL $\frac{3}{8}$ x6 $\frac{1}{2}$                 | 1 2                | A36                      | 16      |
| FIELD BOLTS          |       |           |      |                                                   |                    |                          |         |
| 2                    |       |           |      | $\frac{3}{4}$ Dia HILTI HAS V-36                  | 0 8                | (4" EMBED)               |         |
| THREADED ROD         |       |           |      |                                                   |                    |                          |         |
| 2                    |       |           |      | $\frac{1}{2}$ Dia HILTI KWIK HUS-EZ               | 0 4 $\frac{1}{2}$  | ( $\frac{3}{4}$ " EMBED) |         |
| SCREW ANCHOR         |       |           |      |                                                   |                    |                          |         |
| ONE F-08.00C4        |       |           |      |                                                   |                    |                          |         |
| 1                    |       | F-08.00C4 |      | COLUMN                                            |                    | 354                      |         |
|                      |       |           |      | HSS6x6x $\frac{3}{8}$                             | 9 10 $\frac{1}{2}$ | A500C                    | 271     |
| 1                    |       | hss70     |      | HSS4x4x $\frac{3}{16}$                            | 1 6 $\frac{3}{4}$  | A500C                    | 23      |
| 1                    |       | hss69     |      | HSS4x4x $\frac{3}{16}$                            | 1 1                | A500C                    | 16      |
| 1                    |       | a155      |      | LL $\frac{1}{2}$ x $\frac{1}{2}$ x $\frac{3}{16}$ | 0 5                | A36                      | 1       |
| 1                    |       | p404      |      | PL $\frac{3}{8}$ x6 $\frac{1}{2}$                 | 1 6                | A36                      | 21      |
| 1                    |       | p3367     |      | PL $\frac{3}{8}$ x6 $\frac{1}{2}$                 | 1 6                | A36                      | 21      |
| 1                    |       | p3632     |      | PL $\frac{1}{4}$ x4                               | 0 4                | A36                      | 1       |
| FIELD BOLTS          |       |           |      |                                                   |                    |                          |         |
| 2                    |       |           |      | $\frac{3}{4}$ Dia HILTI KWIK HUS-EZ               | 0 4 $\frac{1}{2}$  | ( $\frac{3}{4}$ " EMBED) |         |
| SCREW ANCHOR         |       |           |      |                                                   |                    |                          |         |
| ONE F-08.00B1        |       |           |      |                                                   |                    |                          |         |
| 1                    |       | F-08.00B1 |      | BEAM                                              |                    | 688                      |         |
|                      |       |           |      | HSS10x8x $\frac{1}{2}$                            | 12 1 $\frac{7}{8}$ | A500C                    | 677     |
| 2                    |       | p3657     |      | PL $\frac{1}{4}$ x8                               | 0 10               | A36                      | 11      |

Total weight : 2156

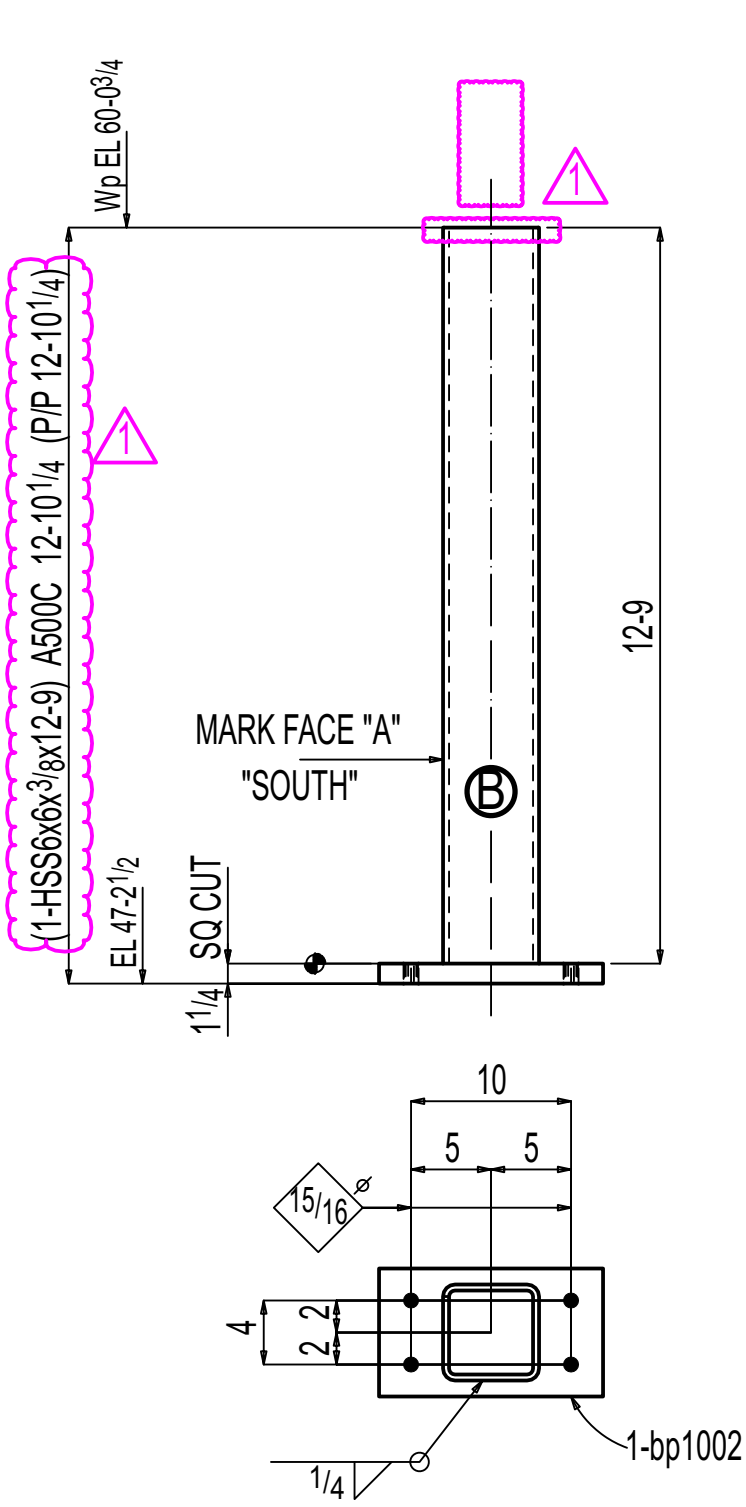


ONE COLUMN F-08.00C1

AT GRID:  
EE & A

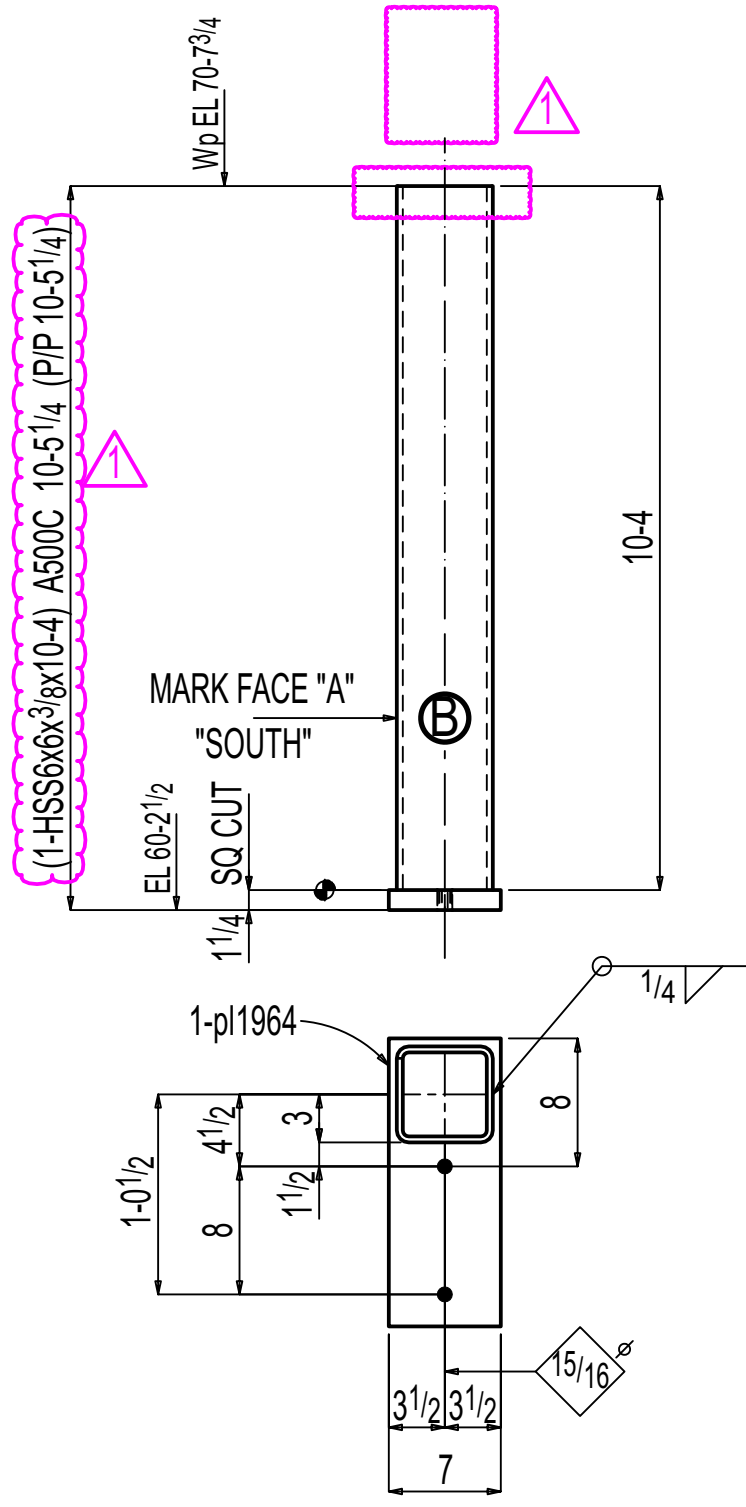


ONE COLUMN F-08.00C2

AT GRID:  
EE & A

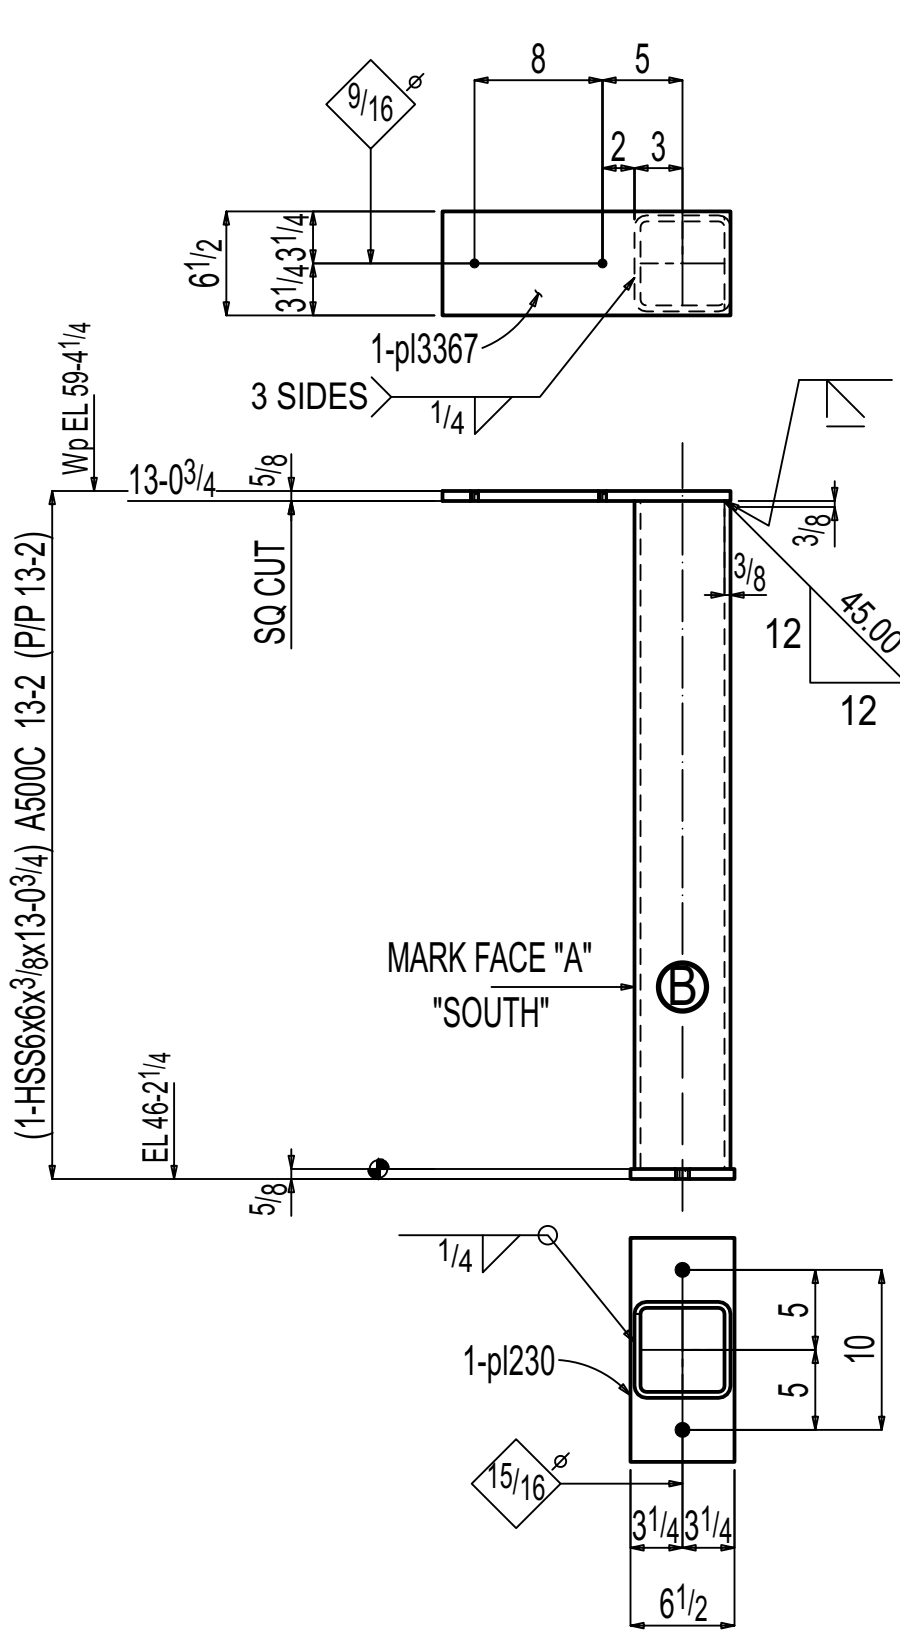


ONE COLUMN F-08.00C3

AT GRID:  
AA & K

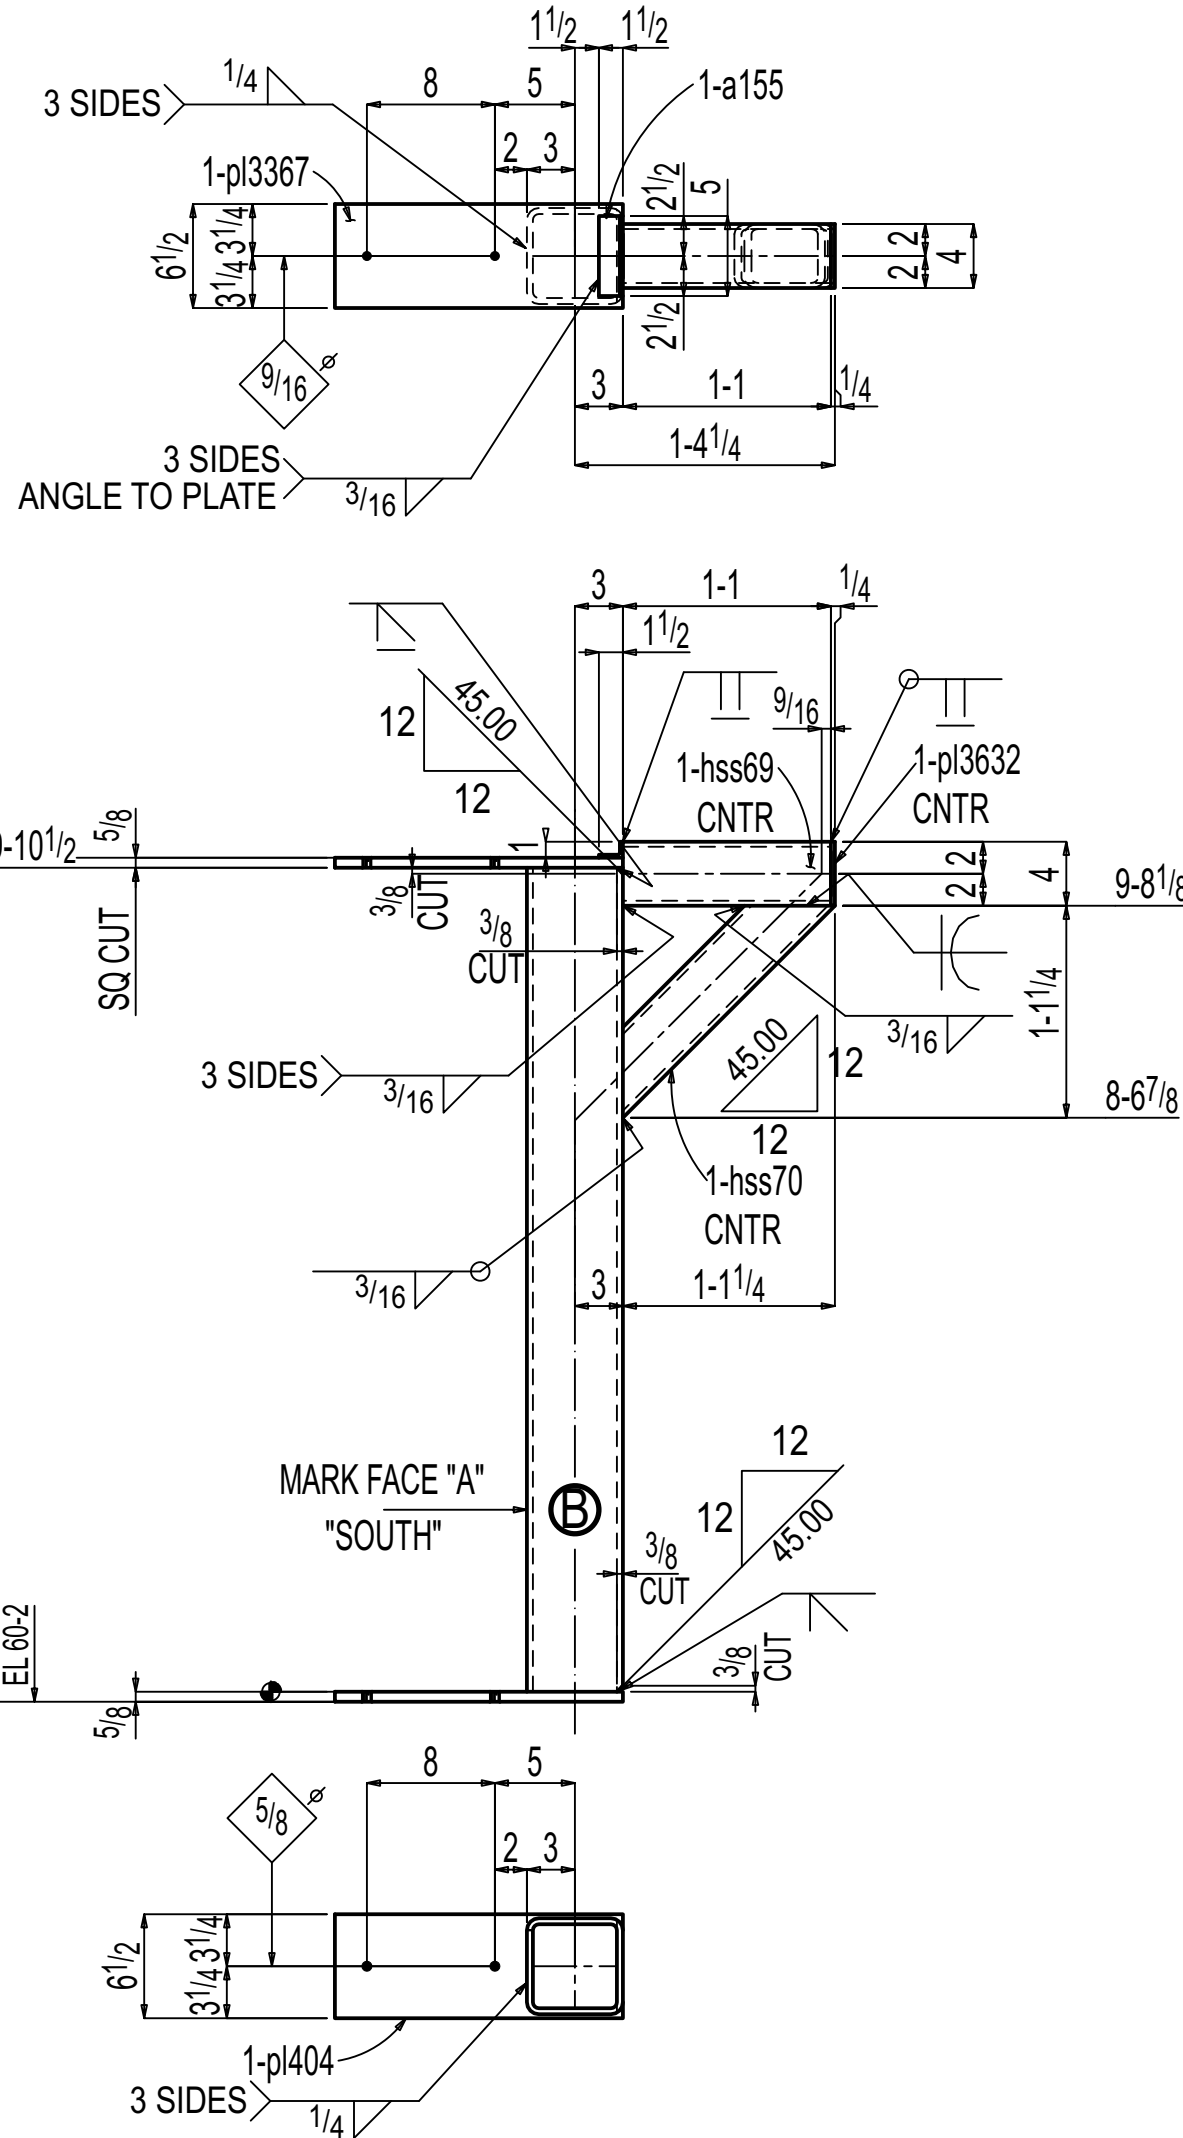

ONE COLUMN F-08.00C4

AT GRID:  
AA & K

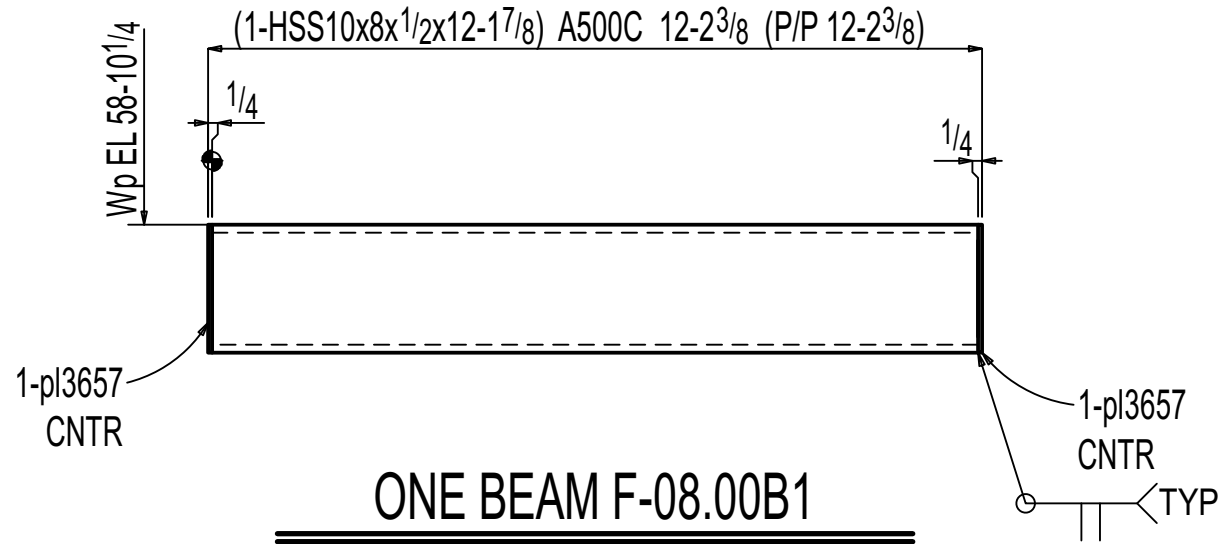

ONE BEAM F-08.00B1

PAINT :NO PAINT  
PREPARATION :SSPC-SP3

| General Notes                                                                        |                 |                  |            |
|--------------------------------------------------------------------------------------|-----------------|------------------|------------|
| *Structural steel shall conform to ASTM-A992.                                        |                 |                  |            |
| *Structural SQR/RND,tubing conform to ASTM A500 Grade C.                             |                 |                  |            |
| *Pipe shall conform to ASTM A53, Grade B.                                            |                 |                  |            |
| *Channels, Angles and plates shall conform to A36.                                   |                 |                  |            |
| *All bolts shall be $\frac{3}{4}$ " High strength in accordance with ASTM A325 (UNO) |                 |                  |            |
| *Welding Electrodes for Carbon steel :E70xx                                          |                 |                  |            |
| 6                                                                                    | 1               | Revised as noted | 11-11-2025 |
| 5                                                                                    | 0               | For Fabrication  | 11-03-2025 |
| 4                                                                                    | D               | For Re-Approval  | 10-24-2025 |
| 3                                                                                    | C               | For Re-Approval  | 09-19-2025 |
| 2                                                                                    | B               | For Re-Approval  | 06-23-2025 |
| 1                                                                                    | A               | For Approval     | 02-25-2025 |
| # of Copies                                                                          | Revision/ Issue | Destination      | Date       |

IRON FABRICATION SERVICES, LLC.

3029 M. Street, NW, Suite 202  
Washington, DC 20007  
Tel: 202-800-5599  
Fax: 202-478-0303

Project Name and Address  
**MARYLAND AVENUE**  
Location: **1250 MARYLAND AVENUE SW**  
**WASHINGTON, DC 20024**

Contractor:  
**BALFOUR BEATTY**

Approved for Fabrication by: Signature

|                |                                    |                |                                 |
|----------------|------------------------------------|----------------|---------------------------------|
| Contract #     | <b>224009</b>                      | Drawing #      | <b>F-08.00</b>                  |
| Contract Item: | <b>COLUMN ,BEAM</b>                |                |                                 |
| Ref:           | <b>SOW - 08: E-08.00 - E-08.04</b> |                |                                 |
| Date           | 01/ 23/ 2025                       | Drawing Title: | <b>COLUMN &amp; BEAM DETAIL</b> |
| Scale          | VARIES                             |                |                                 |



| BILL OF MATERIAL |       |            |             |        |         |        |         |
|------------------|-------|------------|-------------|--------|---------|--------|---------|
| LINE             | QTY   | PC         |             | LENGTH |         | WEIGHT | ADVANCE |
| #                | TOTAL | MARK       | DESCRIPTION |        | REMARKS | TOTAL  | MILL #  |
|                  | ONE   | F-08.01FR1 | FRAME       |        |         | 248    |         |
|                  | 1     | F-08.01FR1 | HSS6x6x3/16 | 3      | 53/4    | A500C  | 81      |
|                  | 1     | w2762      | W8x31       | 1      | 4       | A992   | 41      |
|                  | 1     | p403       | PL1/2x16    | 4      | 6       | A36    | 123     |
|                  | 1     | p685       | PL1/4x6     | 0      | 6       | A36    | 3       |
|                  | ONE   | F-08.01FR2 | FRAME       |        |         | 296    |         |
|                  | 1     | F-08.01FR2 | HSS6x6x3/16 | 3      | 73/4    | A500C  | 85      |
|                  | 1     | hss3616    | HSS6x6x3/16 | 1      | 103/4   | A500C  | 44      |
|                  | 1     | hss3605    | HSS6x6x3/16 | 1      | 77/8    | A500C  | 39      |
|                  | 1     | p403       | PL1/2x16    | 4      | 6       | A36    | 123     |
|                  | 2     | p685       | PL1/4x6     | 0      | 6       | A36    | 5       |
|                  | ONE   | F-08.01FR3 | FRAME       |        |         | 515    |         |
|                  | 1     | F-08.01FR3 | HSS6x6x3/16 | 3      | 73/4    | A500C  | 85      |
|                  | 1     | hss284     | HSS6x6x3/16 | 6      | 81/8    | A500C  | 156     |
|                  | 1     | hss288     | HSS6x6x3/16 | 6      | 33/16   | A500C  | 146     |
|                  | 1     | p403       | PL1/2x16    | 4      | 6       | A36    | 123     |
|                  | 1     | p3187      | PL1/4x6     | 0      | 77/16   | A36    | 3       |
|                  | 1     | p685       | PL1/4x6     | 0      | 6       | A36    | 3       |
|                  | ONE   | F-08.01FR4 | FRAME       |        |         | 641    |         |
|                  | 1     | F-08.01FR4 | HSS6x6x3/16 | 3      | 73/4    | A500C  | 85      |
|                  | 1     | hss3982    | HSS6x6x3/16 | 2      | 511/16  | A500C  | 58      |
|                  | 1     | hss3981    | HSS6x6x3/16 | 2      | 3       | A500C  | 53      |
|                  | 1     | p410       | PL3/4x15    | 11     | 6       | A36    | 440     |
|                  | 2     | p685       | PL1/4x6     | 0      | 6       | A36    | 5       |

Total weight : 1699



:NO PAINT  
:SSPC-SP3


### FRAME DETAIL

Scale  
VARIES




| BILL OF MATERIAL |     |            |                                                        |        |       |              |              |                |
|------------------|-----|------------|--------------------------------------------------------|--------|-------|--------------|--------------|----------------|
| LINE #           | QTY | PC MARK    | DESCRIPTION                                            | LENGTH |       | REMARKS      | WEIGHT TOTAL | ADVANCE MILL # |
|                  | ONE | F-08.02LP1 | LEVELING PLATE                                         |        |       |              | 9            |                |
|                  | 1   | F-08.02LP1 | PL 1'x7'                                               | 1      | 6     | A36          | 9            |                |
|                  | ONE | F-08.02LP2 | LEVELING PLATE                                         |        |       |              | 6            |                |
|                  | 1   | F-08.02LP2 | PL 1'x6 1/2'                                           | 1      | 2     | A36          | 6            |                |
|                  | ONE | F-08.02LP3 | LEVELING PLATE                                         |        |       |              | 8            |                |
|                  | 1   | F-08.02LP3 | PL 1'x8'                                               | 1      | 2     | A36          | 8            |                |
|                  | ONE | F-08.02LP4 | LEVELING PLATE                                         |        |       |              | 8            |                |
|                  | 1   | F-08.02LP4 | PL 1'x6 1/2'                                           | 1      | 6     | A36          | 8            |                |
|                  | ONE | F-08.02M1  | HSS                                                    |        |       |              | 54           |                |
|                  | 1   | F-08.02M1  | HSS 7/8"x1/2"                                          | 1      | 1 1/2 | A500C        | 47           |                |
|                  | 2   | p3667      | PL 1'x7'                                               | 0      | 7     | A36          | 7            |                |
|                  | ONE | F-08.02M2  | SHIM PLATE                                             |        |       |              | 13           |                |
|                  | 1   | F-08.02M2  | PL 1/2"x7'                                             | 1      | 1 1/2 | A36          | 13           |                |
|                  | ONE | F-08.02M3  | PLATE                                                  |        |       |              | 37           |                |
|                  | 1   | F-08.02M3  | PL 3/4"x6'                                             | 1      | 3     | A36          | 19           |                |
|                  | 2   | p3659      | PL 3/4"x6'                                             | 0      | 7     | A36          | 18           |                |
|                  | 8   | F-08.02M4  | THREADED ROD                                           |        |       |              | 12           |                |
|                  | 8   | F-08.02M4  | 1"Ø FULLY THREADED ROD w/ HILTI HIT-HY 200 V3 ADHESIVE | 0      | 6 1/2 | F1554 GR. 55 | 12           |                |
|                  | 8   |            | 1 NUT                                                  |        |       | HHNT A563    |              |                |
|                  | 8   |            | 1 WASHER                                               |        |       | HD F436      |              |                |
|                  | 4   | F-08.02M5  | THREADED ROD                                           |        |       |              | 5            |                |
|                  | 4   | F-08.02M5  | 3/4" Ø THREADED ROD w/ HILTI HY-200 ADHESIVE           | 0      | 9     | F1554 GR. 55 | 5            |                |
|                  | 4   |            | 3/4 NUT                                                |        |       | HHNT A563    |              |                |
|                  | 4   |            | 3/4 WASHER                                             |        |       | HD F436      |              |                |
|                  | 24  | F-08.02M6  | THREADED ROD                                           |        |       |              | 166          |                |
|                  | 24  | F-08.02M6  | 1"Ø THREADED ROD                                       | 2      | 7     | F1554 GR. 55 | 166          |                |
|                  | 48  |            | 1 NUT                                                  |        |       | HHNT A563    |              |                |
|                  | 48  |            | 1 WASHER                                               |        |       | HD F436      |              |                |
|                  | 16  | F-08.02M7  | THREADED ROD                                           |        |       |              | 30           |                |
|                  | 16  | F-08.02M7  | 1"Ø THREADED ROD w/ HILTI HIT-HY 200 V3 ADHESIVE       | 0      | 8 1/2 | F1554 GR. 55 | 30           |                |
|                  | 16  |            | 1 NUT                                                  |        |       | HHNT A563    |              |                |
|                  | 16  |            | 1 WASHER                                               |        |       | HD F436      |              |                |
|                  | 2   | F-08.02M8  | THREADED ROD                                           |        |       |              | 1            |                |
|                  | 2   | F-08.02M8  | 1/2" Ø THREADED ROD w/HILTI HY 200 V3 ADHESIVE         | 0      | 6     | F1554 GR. 55 | 1            |                |
|                  | 2   |            | 1/2 NUT                                                |        |       | HHNT A563    |              |                |
|                  | ONE | F-08.02M9  | HSS                                                    |        |       |              | 208          |                |
|                  | 1   | F-08.02M9  | HSS 5 1/2"x5 1/2"x5 1/16                               | 9      | 7 1/2 | A500C        | 204          |                |
|                  | 2   | p407       | PL 1'x5 1/2'                                           | 0      | 5 1/2 | A36          | 4            |                |


Total weight : 557

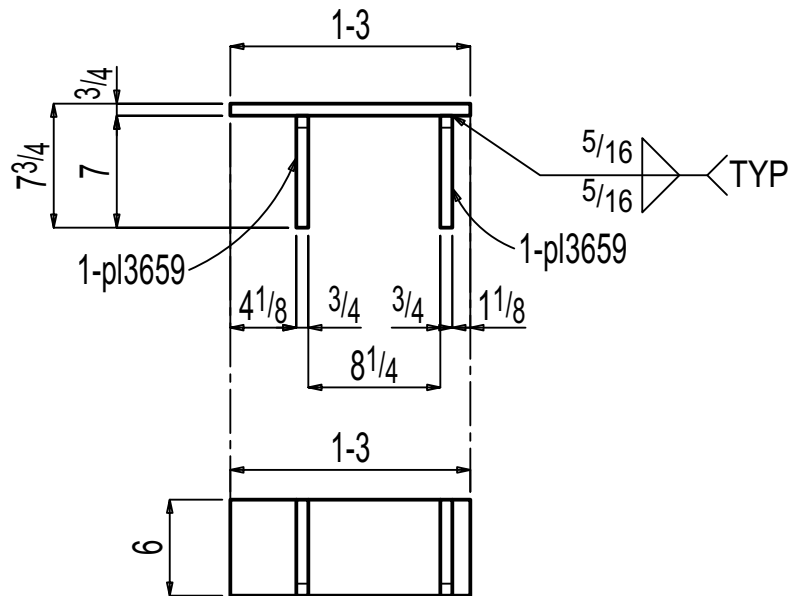


ONE PLATE F-08.02M3

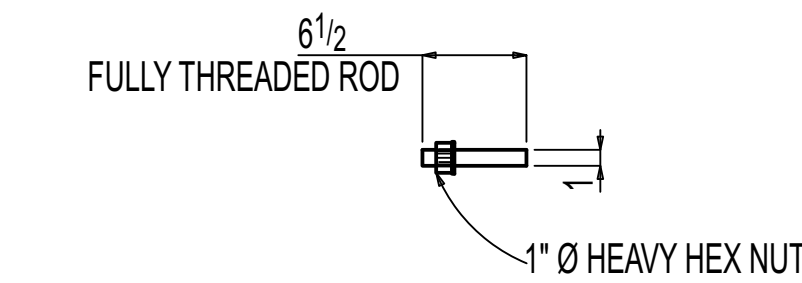


8 THREADED RODS F-08.02M4

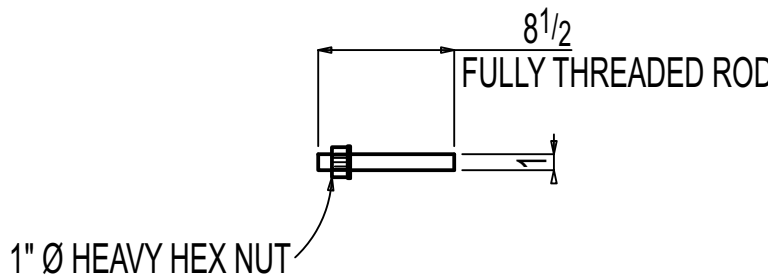


16 THREADED RODS F-08.02M7

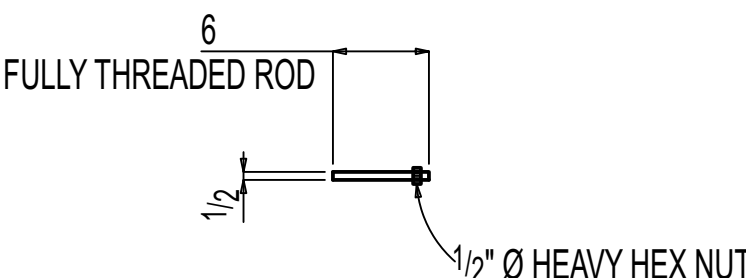


2 THREADED RODS F-08.02M8

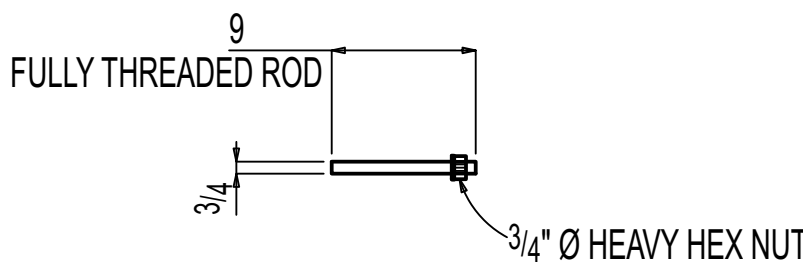


4 THREADED RODS F-08.02M5

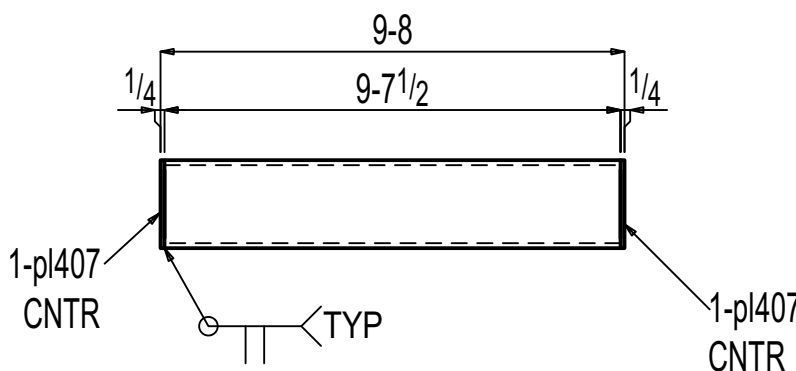


ONE HSS F-08.02M9

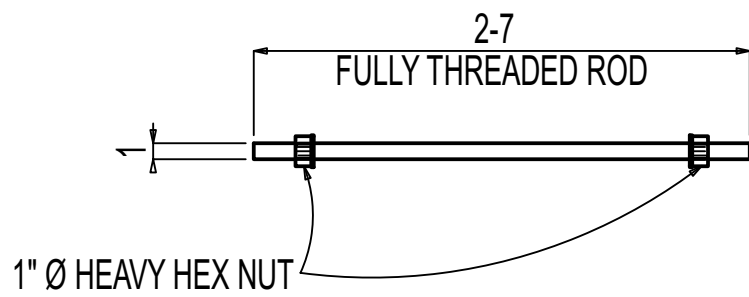


24 THREADED RODS F-08.02M6

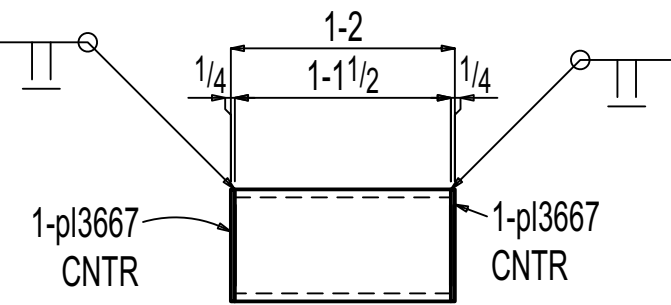


ONE HSS F-08.02M1

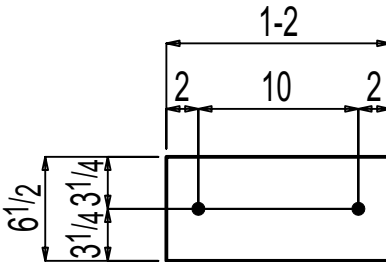


ONE LEVELING PLATE F-08.02LP2

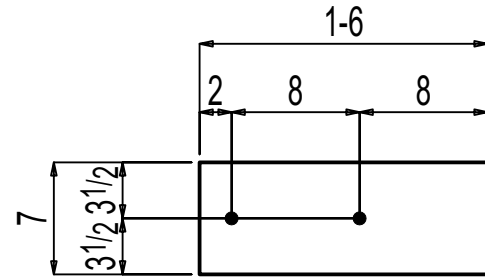

ONE LEVELING PLATE F-08.02LP1

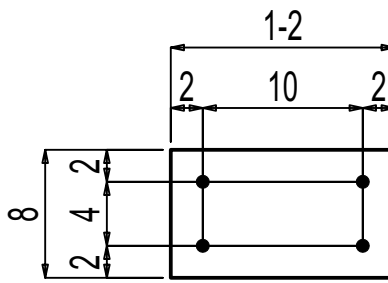

ONE LEVELING PLATE F-08.02LP3

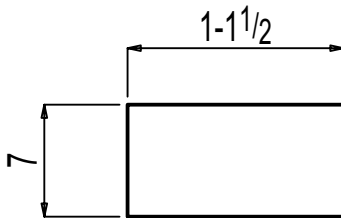

ONE SHIM PLATE F-08.02M2

PAINT :NO PAINT  
PREPARATION :SSPC-SP3

| General Notes                                                             |                 |                 |            |
|---------------------------------------------------------------------------|-----------------|-----------------|------------|
| *Structural steel shall conform to ASTM-A992.                             |                 |                 |            |
| *Structural SQR/RND,tubing conform to ASTM A500 Grade C                   |                 |                 |            |
| *Pipe shall conform to ASTM A53, Grade B.                                 |                 |                 |            |
| *Channels, Angles and plates shall conform to A36.                        |                 |                 |            |
| *All bolts shall be 3/4" High strength in accordance with ASTM A325 (UNO) |                 |                 |            |
| *Welding Electrodes for Carbon steel :E70xx                               |                 |                 |            |
| 5                                                                         | 0               | For Fabrication | 11-03-2025 |
| 4                                                                         | D               | For Re-Approval | 10-24-2025 |
| 3                                                                         | C               | For Re-Approval | 09-19-2025 |
| 2                                                                         | B               | For Re-Approval | 06-23-2025 |
| 1                                                                         | A               | For Approval    | 02-25-2025 |
| # of Copies                                                               | Revision/ Issue | Destination     | Date       |

IRON FABRICATION SERVICES, LLC.

3029 M. Street, NW, Suite 202  
Washington, DC 20007  
Tel: 202-800-5599  
Fax: 202-478-0303

Project Name and Address

MARYLAND AVENUE

Location: 1250 MARYLAND AVENUE SW  
WASHINGTON, DC 20024

Contractor:

BALFOUR BEATTY

|                              |           |
|------------------------------|-----------|
| Approved for Fabrication by: | Signature |
|------------------------------|-----------|

|            |        |           |         |
|------------|--------|-----------|---------|
| Contract # | 224009 | Drawing # | F-08.02 |
|------------|--------|-----------|---------|

Contract Item: MISC DETAIL

Ref:


SOW - 08: E-08.00 - E-08.04

|              |                      |
|--------------|----------------------|
| Date         | Drawing Title:       |
| 01/ 23/ 2025 | MISCELLANEOUS DETAIL |
| Scale        |                      |
| VARIES       |                      |




| BILL OF MATERIAL |            |                          |             |        |                   |              |                |
|------------------|------------|--------------------------|-------------|--------|-------------------|--------------|----------------|
| LINE #           | QTY        | PC MARK                  | DESCRIPTION | LENGTH | REMARKS           | WEIGHT TOTAL | ADVANCE MILL # |
| ONE              | F-08.03M1  | BENT PLATE               |             |        |                   | 53           |                |
| 1                | F-08.03M1  | PL1/2x1511/16            |             | 2 0    | BENT A36          | 53           |                |
|                  |            | FIELD BOLTS              |             |        |                   |              |                |
| 3                |            | 3/4 Dia HILTI HAS V-36   |             | 0 8    | (6" EMBED)        |              |                |
|                  |            | THREADED ROD             |             |        |                   |              |                |
|                  |            | w/HILTI HY-200           |             |        |                   |              |                |
| 3                | F-08.03M2  | BENT PLATE               |             |        |                   | 196          |                |
| 3                | F-08.03M2  | PL1/2x1931/16            |             | 2 0    | BENT A36          | 196          |                |
|                  |            | FIELD BOLTS              |             |        |                   |              |                |
| 9                |            | 3/4 Dia HILTI HAS V-36   |             | 0 8    | 6" EMBED          |              |                |
|                  |            | THREADED ROD             |             |        |                   |              |                |
|                  |            | w/HILTI HY-200           |             |        |                   |              |                |
| 3                | F-08.03M3  | HSS                      |             |        |                   | 29           |                |
| 3                | F-08.03M3  | HSS31/2x31/2x5/16        |             | 0 71/2 | A500C             | 24           |                |
| 6                | p3257      | PL1/4x31/2               |             | 0 31/2 | A36               | 5            |                |
| 4                | F-08.03M4  | HSS                      |             |        |                   | 431          |                |
| 4                | F-08.03M4  | HSS5x5x3/8               |             | 4 2    | A500C             | 373          |                |
| 4                | a154       | L5x5x3/16                |             | 0 10   | A36               | 34           |                |
| 8                | p3256      | PL1/4x5                  |             | 0 5    | A36               | 14           |                |
| 8                |            | 3/4 Dia A325N            |             | 0 61/2 | +1HD WASH         | 10           |                |
|                  |            | FIELD BOLTS              |             |        |                   |              |                |
| 8                |            | 1/2 Dia HILTI K8-TZ2     |             | 0 7    |                   |              |                |
|                  |            | EXPANSION ANCHOR         |             |        | (51/2" EMBEDMENT) |              |                |
| ONE              | F-08.03M5  | ANGLE                    |             |        |                   | 2            |                |
| 1                | F-08.03M5  | L4x4x1/4                 |             | 0 4    | A36               | 2            |                |
| ONE              | F-08.03M6  | PLATE                    |             |        |                   | 7            |                |
| 1                | F-08.03M6  | PL1/4x7                  |             | 1 11/2 | A36               | 7            |                |
| 2                | F-08.03M7  | PLATE                    |             |        |                   | 109          |                |
| 2                | F-08.03M7  | PL11/4x7                 |             | 1 10   | A36               | 109          |                |
|                  |            | FIELD BOLTS              |             |        |                   |              |                |
| 4                |            | 3/4" Ø HILTI KWIK-HUS-EZ |             | 0 7    | (31/4" EMBED)     |              |                |
|                  |            | SCREW ANCHOR             |             |        |                   |              |                |
| ONE              | F-08.03EP1 | EMBED PLATE              |             |        |                   | 440          |                |
| 1                | F-08.03EP1 | PL3/4x15                 |             | 11 6   | A36               | 440          |                |
| ONE              | F-08.03EP2 | EMBED PLATE              |             |        |                   | 177          |                |
| 1                | F-08.03EP2 | PL5/8x20                 |             | 4 2    | A36               | 177          |                |
|                  |            | FIELD BOLTS              |             |        |                   |              |                |
| 8                |            | 3/4 Dia HILTI HAS V-36   |             | 0 8    | (5" EMBEDMENT)    |              |                |
|                  |            | w/ HILTI HY-200 EPOXY    |             |        |                   |              |                |

Total weight : 1445

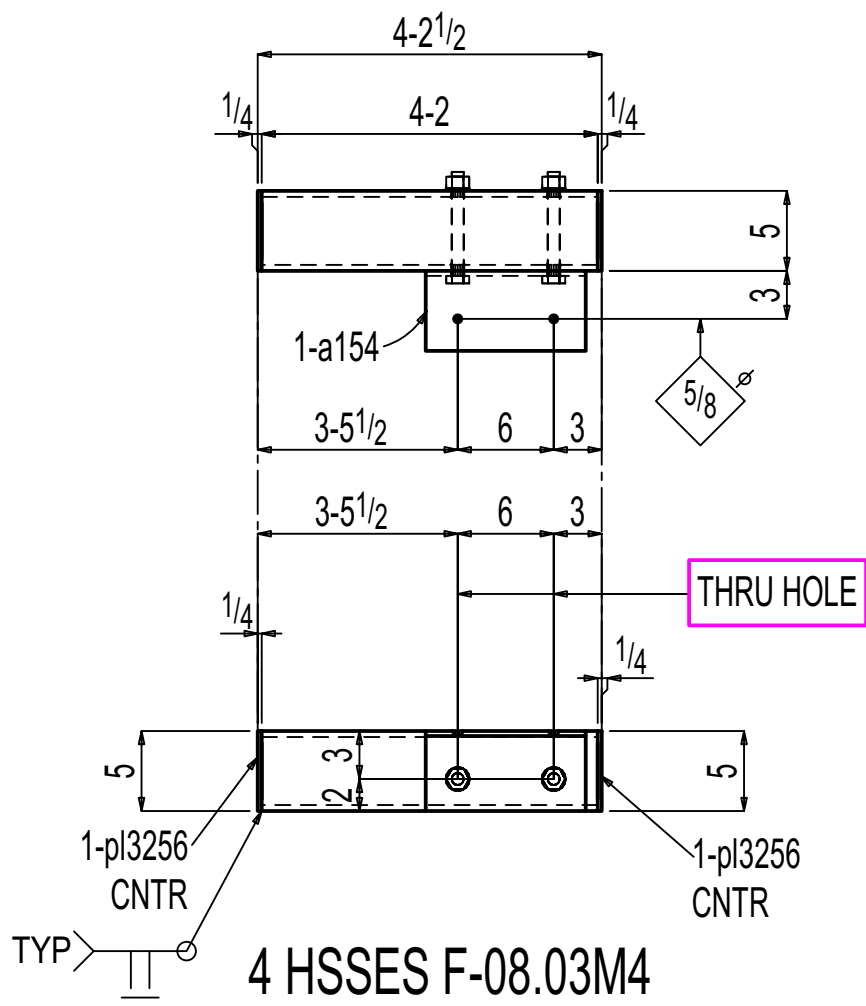


4 HSSes F-08.03M4


SHOP BOLTS:  
2-3/4Diax61/2 A325N

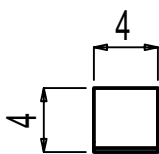


ONE ANGLE F-08.03M5

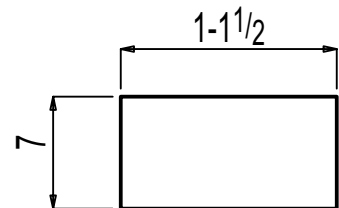


ONE PLATE F-08.03M6

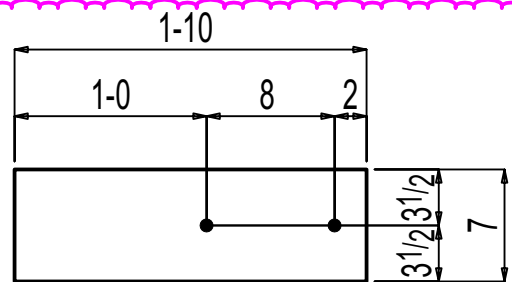

2 PLATES F-08.03M7

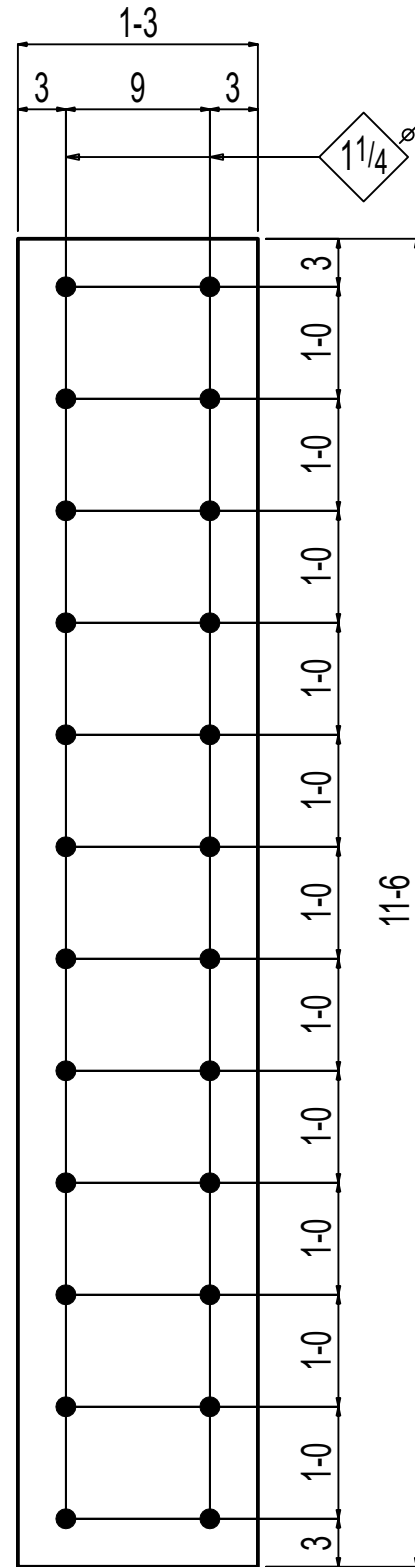


ONE EMBED PLATE F-08.03EP1

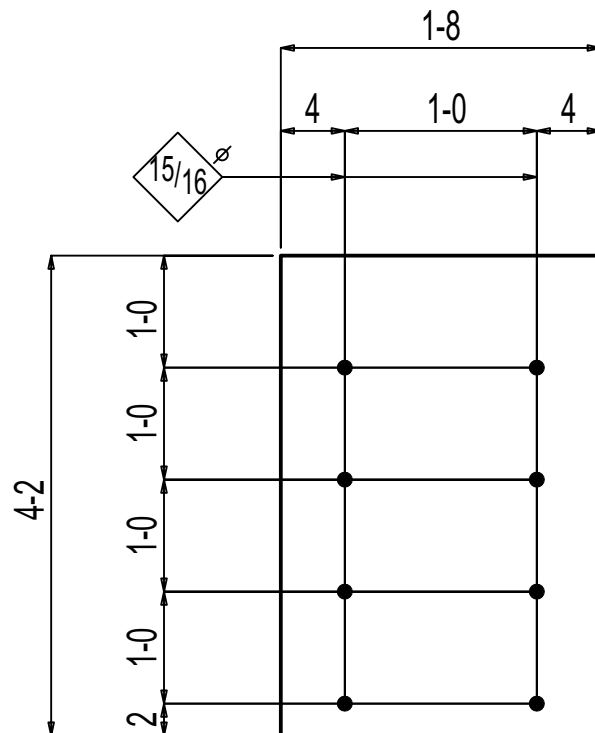


ONE EMBED PLATE F-08.03EP2


PAINT :NO PAINT  
PREPARATION :SSPC-SP3

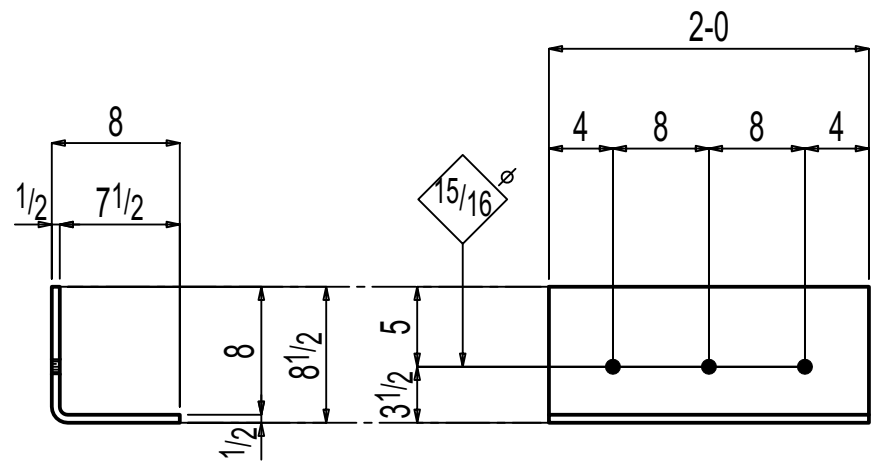

ONE BENT PLATE F-08.03M1

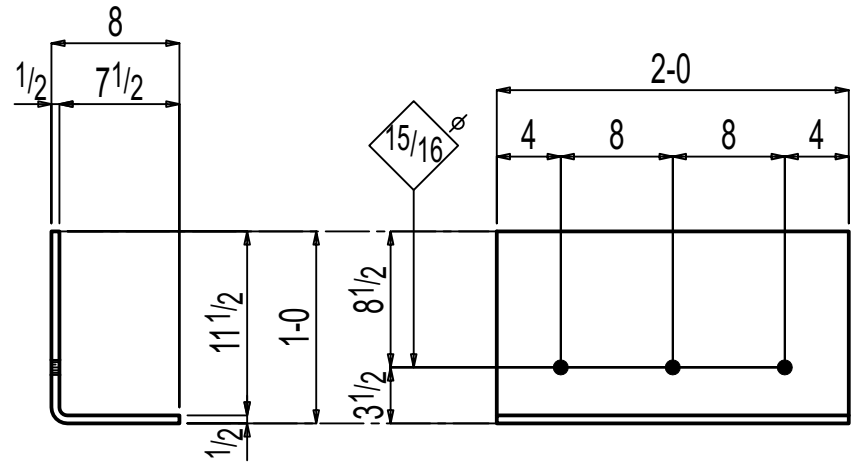

3 BENT PLATES F-08.03M2

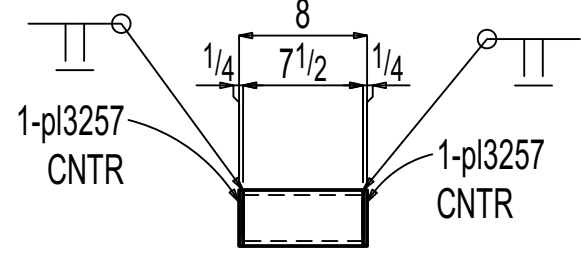

3 HSSes F-08.03M3

| General Notes                                                             |                 |                  |            |
|---------------------------------------------------------------------------|-----------------|------------------|------------|
| *Structural steel shall conform to ASTM-A992.                             |                 |                  |            |
| *Structural SQR/RND,tubing conform to ASTM A500 Grade C                   |                 |                  |            |
| *Pipe shall conform to ASTM A53, Grade B.                                 |                 |                  |            |
| *Channels, Angles and plates shall conform to A36.                        |                 |                  |            |
| *All bolts shall be 3/4" High strength in accordance with ASTM A325 (UNO) |                 |                  |            |
| *Welding Electrodes for Carbon steel :E70xx                               |                 |                  |            |
| 6                                                                         | 1               | Revised as noted | 11-11-2025 |
| 5                                                                         | 0               | For Fabrication  | 11-03-2025 |
| 4                                                                         | D               | For Re-Approval  | 10-24-2025 |
| 3                                                                         | C               | For Re-Approval  | 09-19-2025 |
| 2                                                                         | B               | Deleted          | 06-23-2025 |
| 1                                                                         | A               | For Approval     | 02-25-2025 |
| # of Copies                                                               | Revision/ Issue | Destination      | Date       |

IRON FABRICATION SERVICES, LLC.

3029 M. Street, NW, Suite 202  
Washington, DC 20007  
Tel: 202-800-5599  
Fax: 202-478-0303

Project Name and Address  
**MARYLAND AVENUE**  
Location: **1250 MARYLAND AVENUE SW  
WASHINGTON, DC 20024**

Contractor:  
**BALFOUR BEATTY**

Approved for Fabrication by: Signature

Contract # **224009** Drawing # **F-08.03**

Contract Item: **PLATE & ANGLE DETAIL**

Ref:  
**SOW - 08: E-08.00 - E-08.04**

Date  
**01/ 23/ 2025**  
Drawing Title:  
**MISCELLANEOUS DETAIL**  
Scale  
**VARIES**