


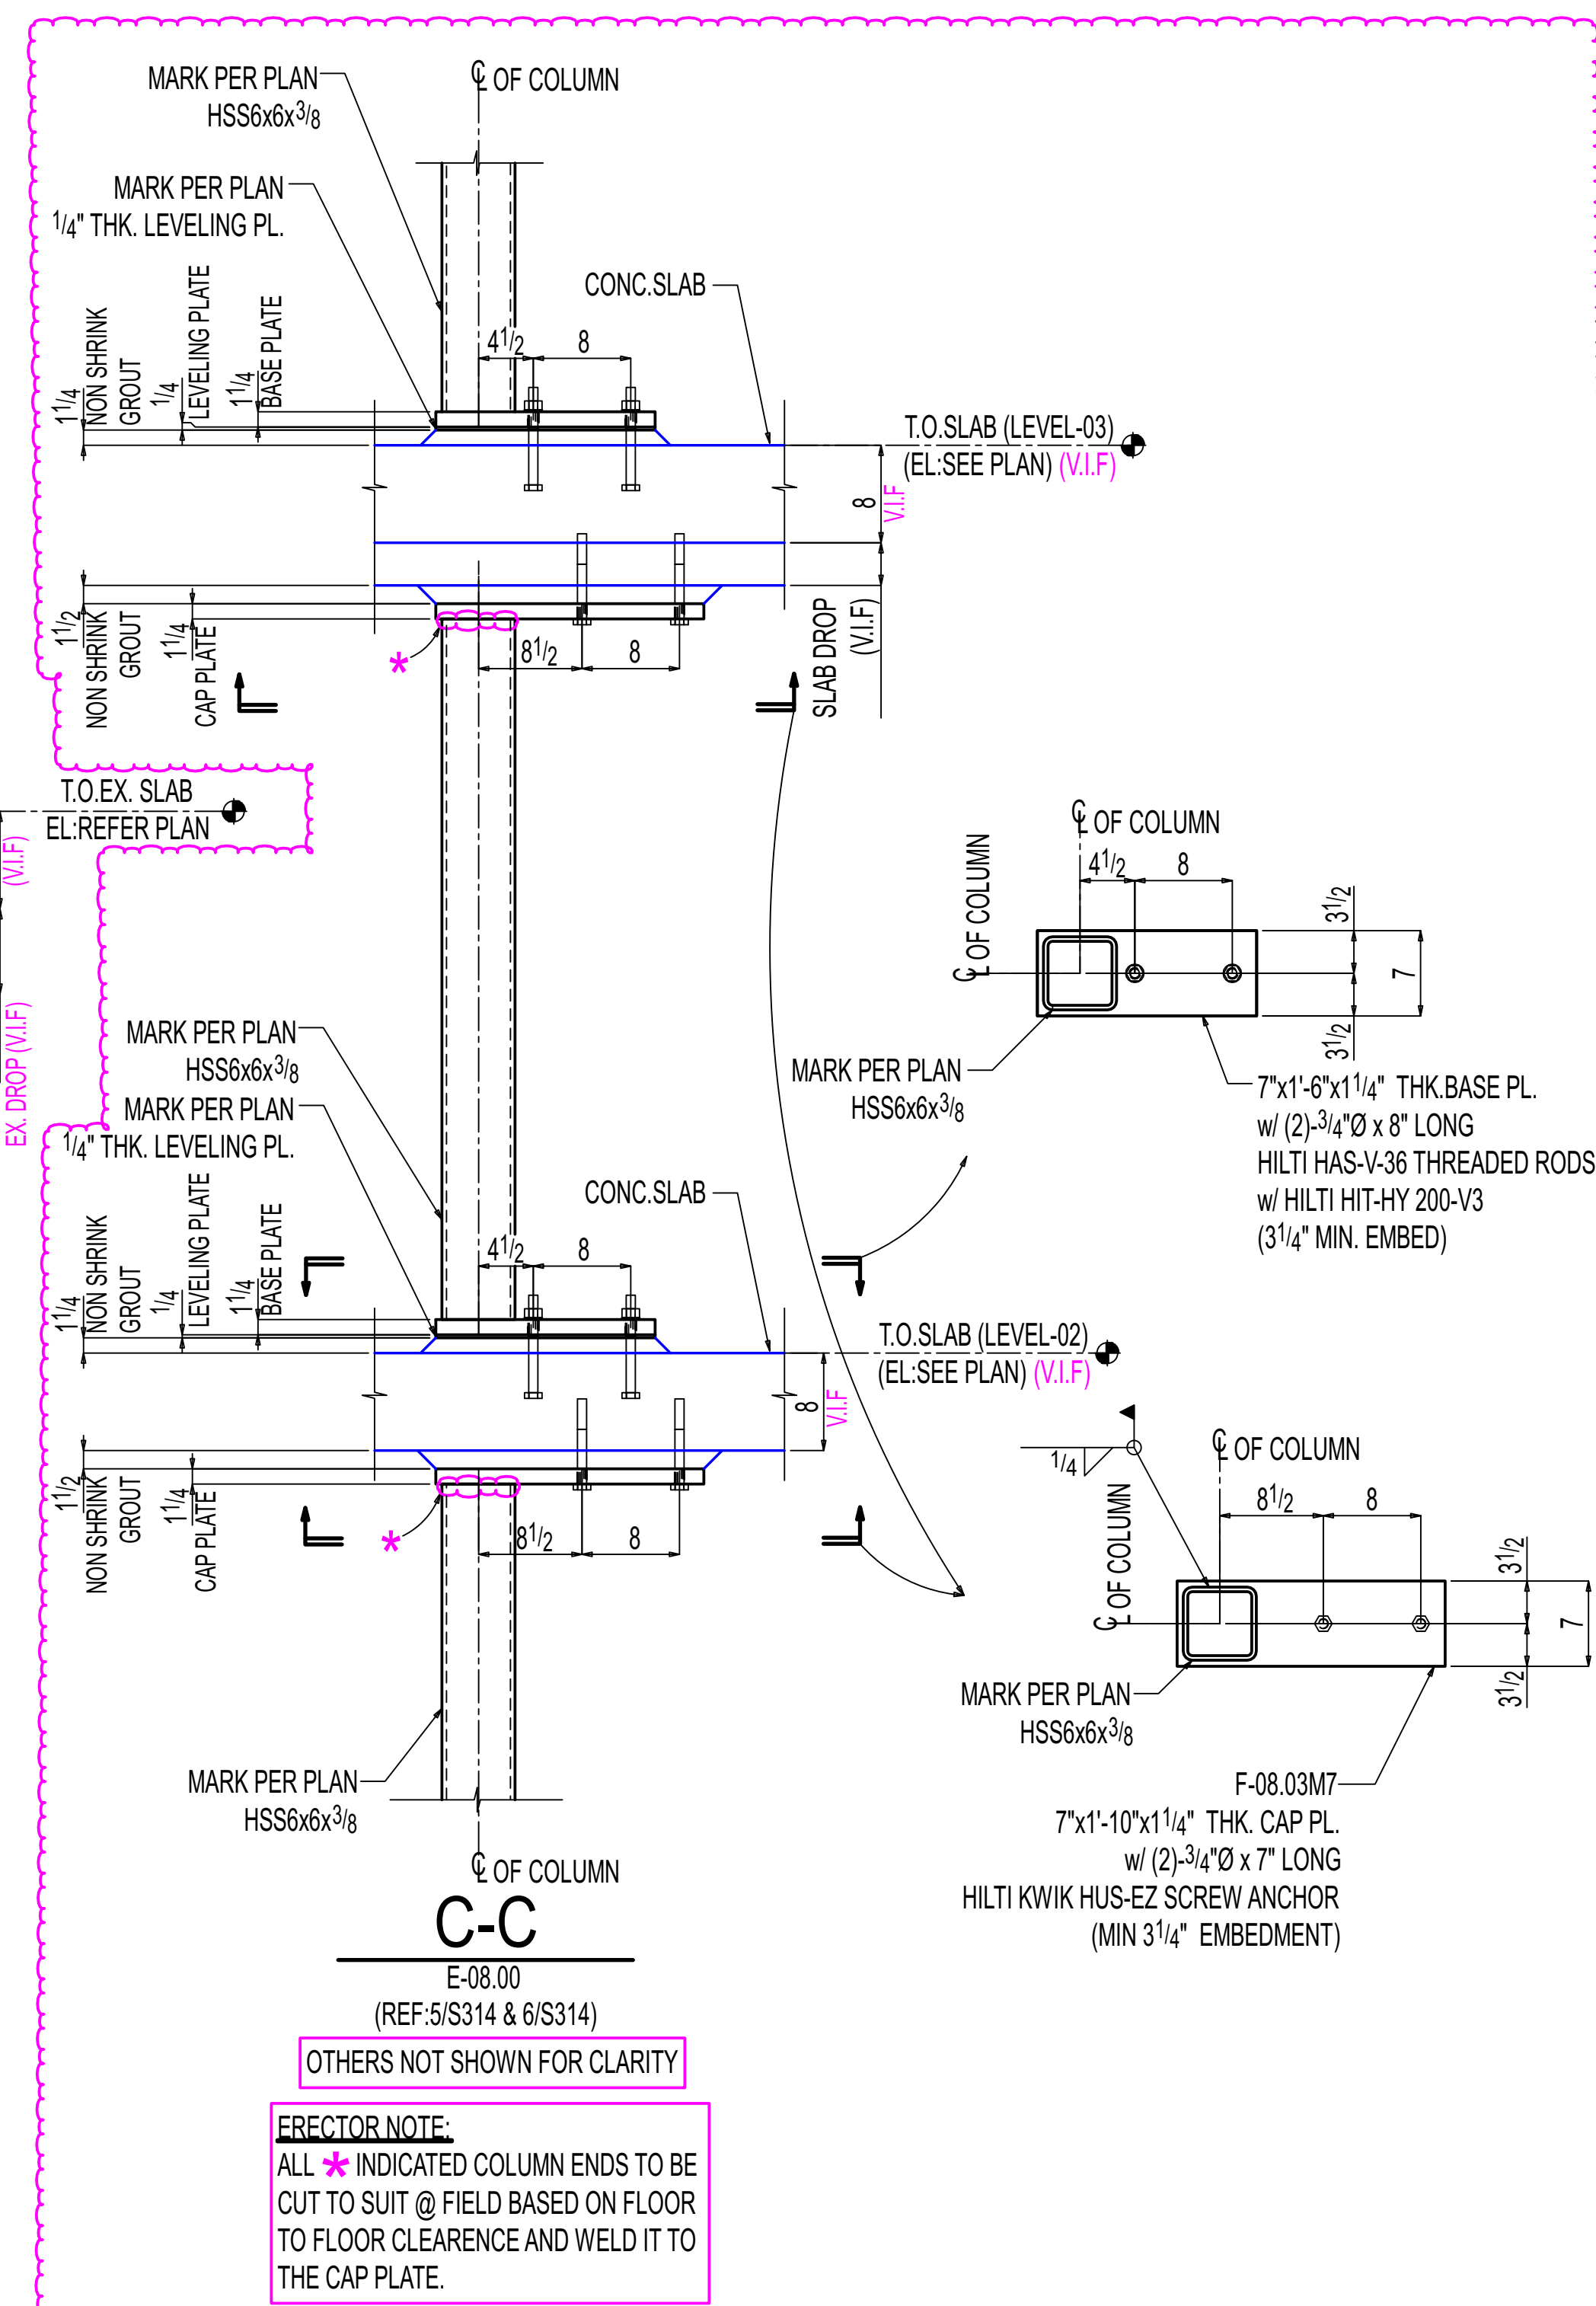

ERECTOR NOTE-1:
ADJUST HSS DEPTH IN FIELD BY CUT THE HSS TO MATCH
EXISTING SLAB DROP THICKNESS, AND WELD TO THE
TOP OF HSS FRAME AT SITE PRIOR TO ERECTING THE HSS FRAME.

Contract # 224009		Drawing # E-08.01
Contract Item: LEVEL-02 SLAB EXTENSION		
Ref: SOW-08:3,4,5&6 / S307		
Date 01/20/2025	Drawing Title: SOW #08 LEVEL-02 NEW SLAB EXTENSION SUPPORT SECTIONS	
Scale VARIABLE		