


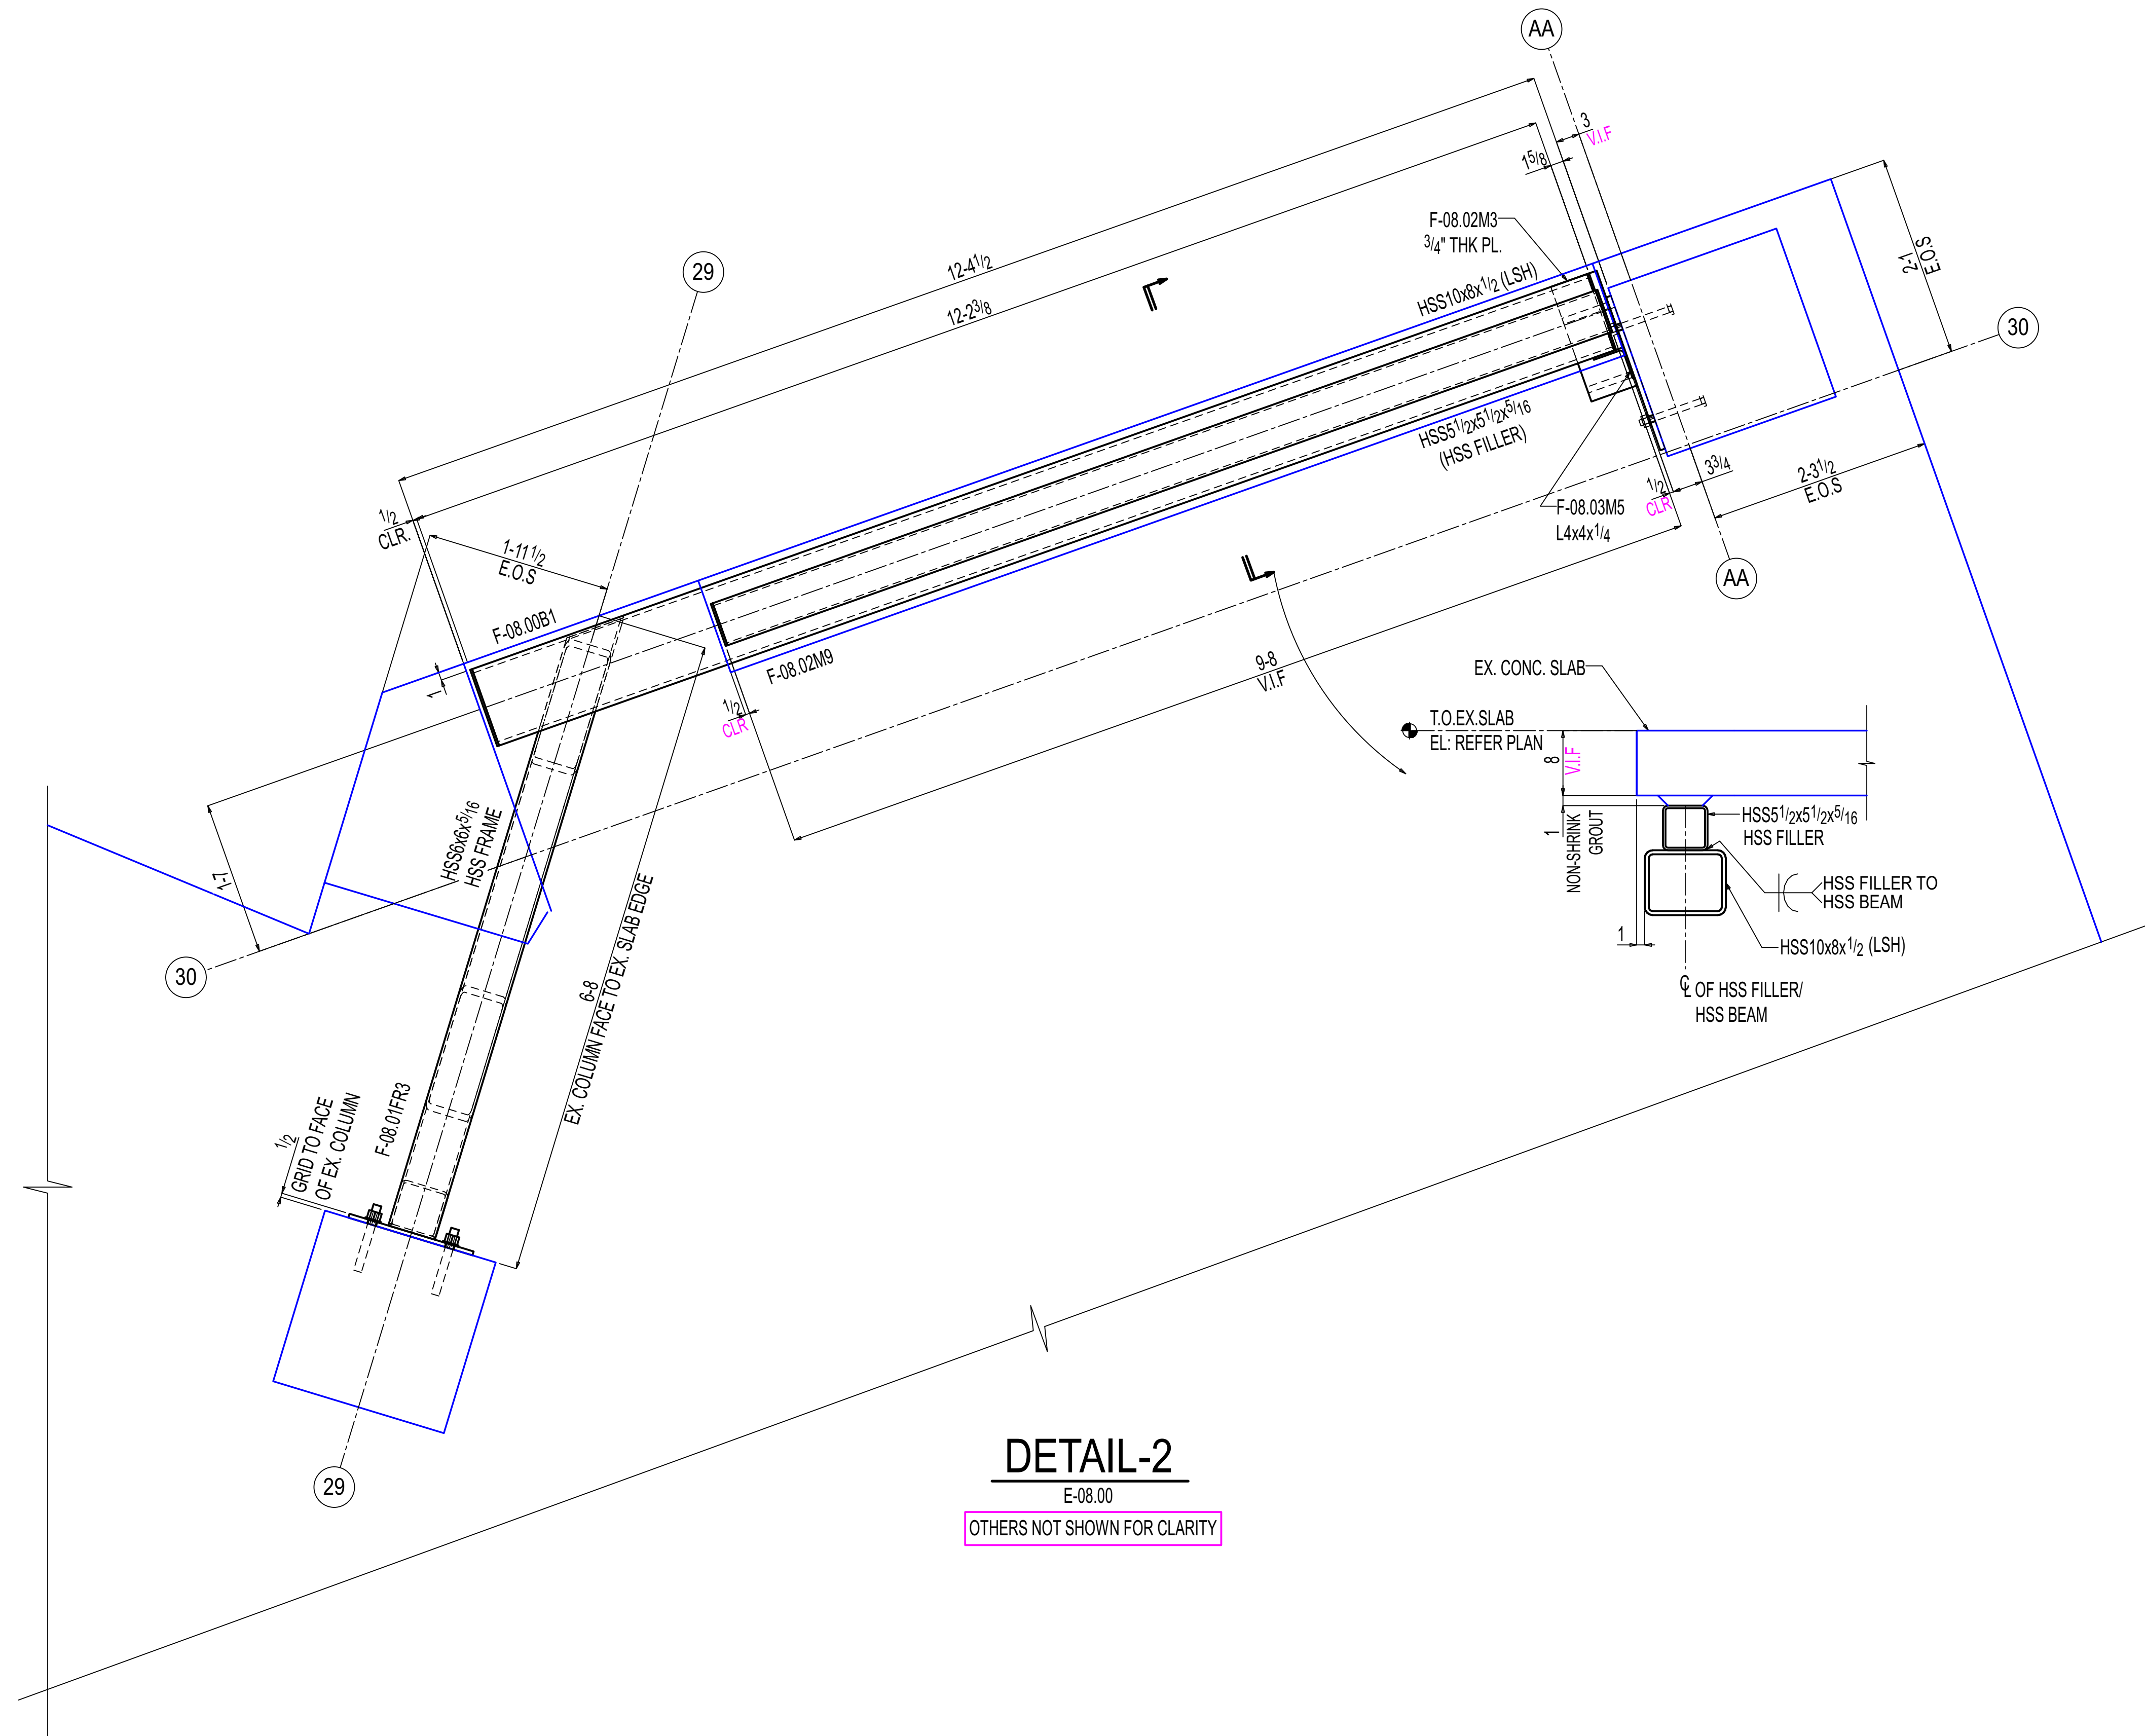

DETAIL-2

E-08.00

OTHERS NOT SHOWN FOR CLARITY

General Notes

- *Structural steel shall conform to ASTM-A992.
- *Structural SQR/RND.tubing conform to ASTM A500 Grade C
- *Pipe shall conform to ASTM A53, Grade B.
- *Channels, Angles and plates shall conform to A36.
- *All bolts shall be 3/4" High strength in accordance with ASTM A325 (UNO)
- *Welding Electrodes for Carbon steel :E70xx

# of Copies	Revision/ Issue	For Construction Destination	11-03-2025 Date
1	0	For Construction	11-03-2025

IRON FABRICATION SERVICES, LLC.

3029 M. Street, NW, Suite 202
Washington, DC 20007
Tel: 202-800-5599
Fax: 202-478-0303

Project Name and Address
MARYLAND AVENUE

Location: **1250 MARYLAND AVENUE SW
WASHINGTON, DC 20024**

Contractor:
BALFOUR BEATTY

Approved for Fabrication by:	Signature
------------------------------	-----------

Contract # 224009	Drawing # E-08.02A
Contract Item: LEVEL-02 SLAB EXTENSION	
Ref: SOW-08:3,4,5&6 / S307	
Date 01/ 20/ 2025	Drawing Title: SOW #08 LEVEL-02 DETAIL VIEW
Scale VARIES	