




NOTE:

1. ALL SLAB EXTENSION SUPPORT HSS FRAMES ARE FOR THE CENTER OF THE EXISTING CONCRETE COLUMN (U.N.O).
2. ALL SLAB EXTENSION SUPPORT FRAME SIZE IS HSS5x5x $\frac{3}{8}$ (U.N.O).



NOTE

* - HSS POST LOCATION SHOULD BE CO-ORDINATE WITH PRECAST MANUFACTURER FOR PRECAST BEARING LOCATION

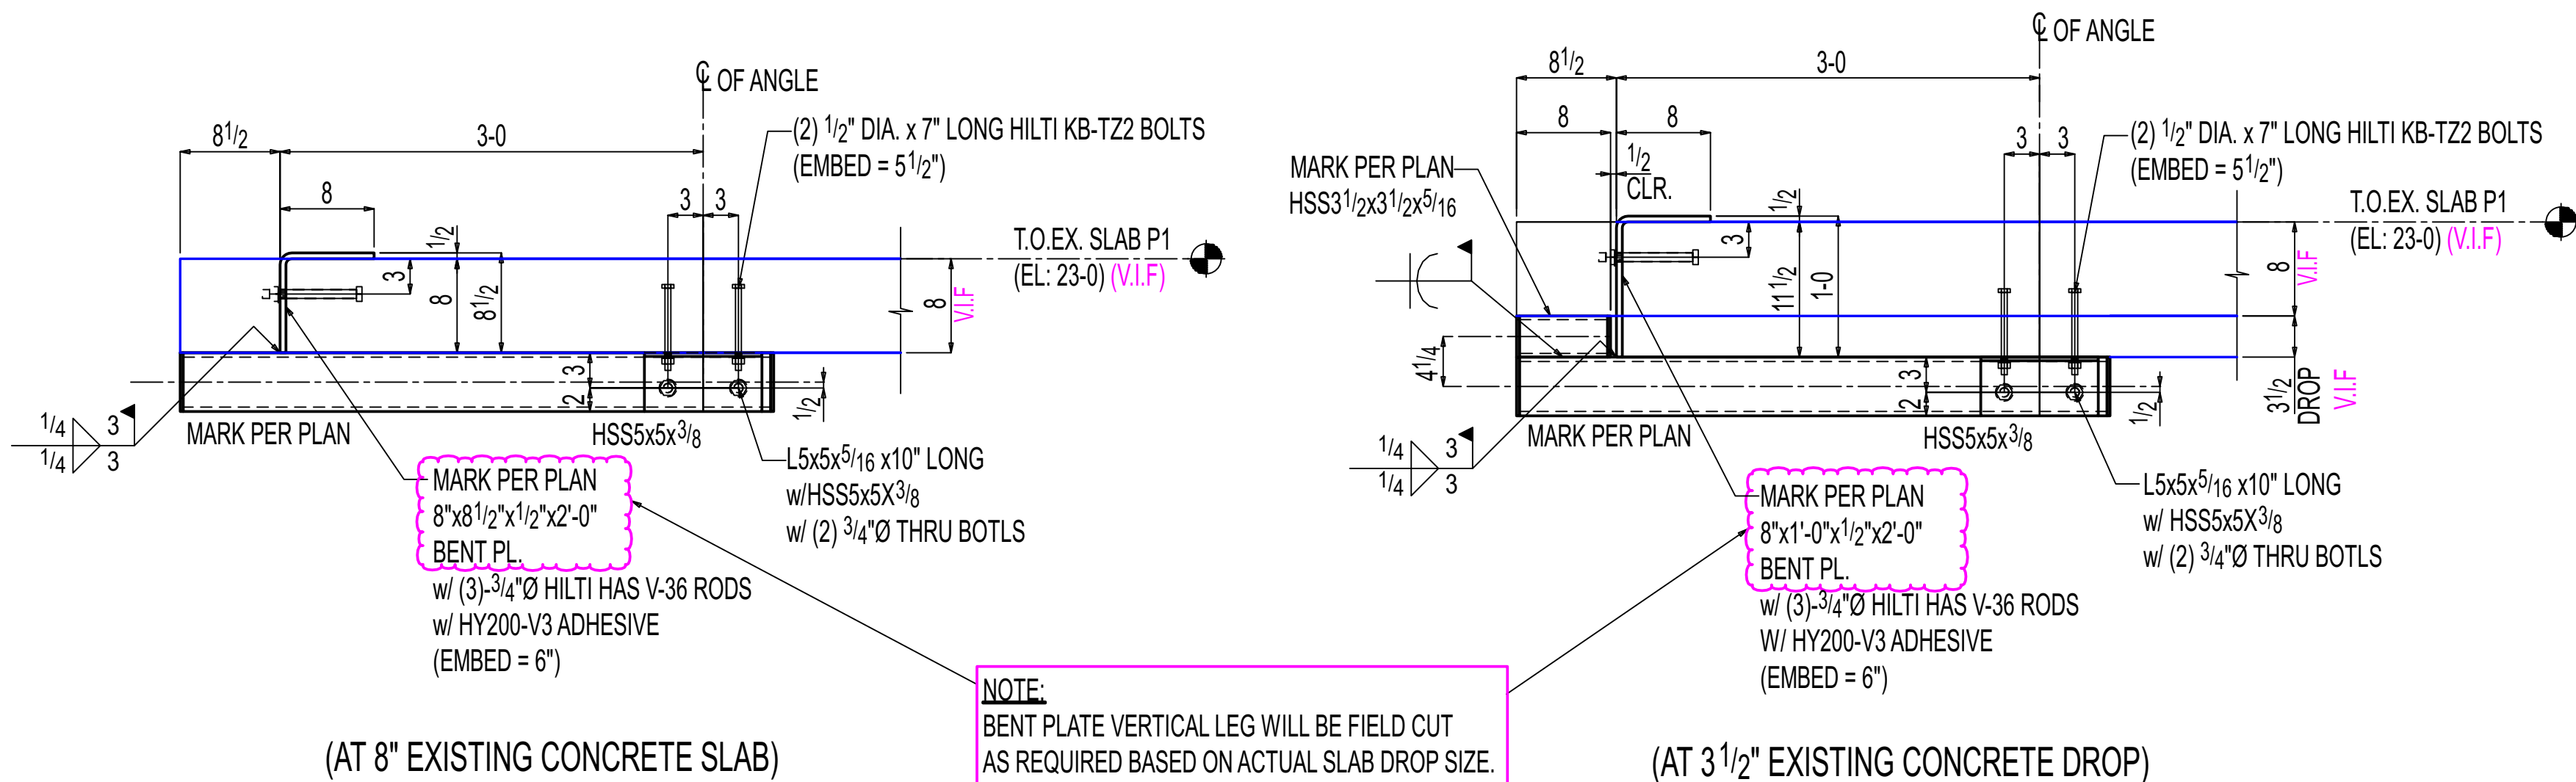

TYPICAL HSS OUTRIGGER SUPPORT PRECAST DETAIL

IRON FABRICATION SERVICES, LLC.

3029 M. Street, NW, Suite 202
Washington, DC 20007
Tel: 202-800-5599
Fax: 202-478-0303

Project Name and Address
MARYLAND AVENUE

Location: **1250 MARYLAND AVENUE SW**
WASHINGTON, DC 20024

Contractor:

BALFOUR BEATTY

Approved for Fabrication by:

Signature _____

Contract # **224009**Drawing # **E-08.05**

Contract Item:	LEVEL-P1 SLAB EXTENSION
----------------	------------------------------------

Ref: **SOW-08:S104,5/S315**

Date _____

01/20/2025

2	1
---	---

Drawing Title:

**SOW #08 LEVEL-P1 NEW
SLAB EXTENSION SUPPORT
PLAN & SECTIONS**