


| BILL OF MATERIAL |            |                        |      |             |                  |         |                |
|------------------|------------|------------------------|------|-------------|------------------|---------|----------------|
| LINE #           | QTY        | PC                     | MARK | DESCRIPTION | LENGTH           | REMARKS | ADVANCE MILL # |
| ONE              | F-09.00FR1 | FRAME                  |      |             |                  |         | 248            |
| 1                | F-09.00FR1 | HSS6x6x $\frac{9}{16}$ |      | 3           | 5 $\frac{3}{4}$  | A500C   | 81             |
| 1                | w2764      | W8x31                  |      | 1           | 4                | A992    | 41             |
| 1                | p346       | PL $\frac{1}{2}$ x16   |      | 4           | 6                | A36     | 123            |
| 1                | p688       | PL $\frac{1}{4}$ x6    |      | 0           | 6                | A36     | 3              |
| 5                | F-09.00FR3 | FRAME                  |      |             |                  |         | 1193           |
| 5                | F-09.00FR3 | HSS6x6x $\frac{9}{16}$ |      | 3           | 5 $\frac{3}{4}$  | A500C   | 406            |
| 5                | w2769      | W8x31                  |      | 1           | 0 $\frac{1}{2}$  | A992    | 161            |
| 5                | p346       | PL $\frac{1}{2}$ x16   |      | 4           | 6                | A36     | 613            |
| 5                | p688       | PL $\frac{1}{4}$ x6    |      | 0           | 6                | A36     | 13             |
| ONE              | F-09.00FR4 | FRAME                  |      |             |                  |         | 366            |
| 1                | F-09.00FR4 | HSS6x6x $\frac{9}{16}$ |      | 3           | 7 $\frac{3}{4}$  | A500C   | 85             |
| 1                | hss3770    | HSS6x6x $\frac{9}{16}$ |      | 3           | 6 $\frac{3}{4}$  | A500C   | 83             |
| 1                | hss1544    | HSS6x6x $\frac{9}{16}$ |      | 3           | 0 $\frac{1}{4}$  | A500C   | 70             |
| 1                | p346       | PL $\frac{1}{2}$ x16   |      | 4           | 6                | A36     | 123            |
| 2                | p688       | PL $\frac{1}{4}$ x6    |      | 0           | 6                | A36     | 5              |
| ONE              | F-09.00FR5 | FRAME                  |      |             |                  |         | 372            |
| 1                | F-09.00FR5 | HSS6x6x $\frac{9}{16}$ |      | 3           | 7 $\frac{3}{4}$  | A500C   | 85             |
| 1                | hss325     | HSS6x6x $\frac{9}{16}$ |      | 3           | 8 $\frac{9}{16}$ | A500C   | 87             |
| 1                | hss234     | HSS6x6x $\frac{9}{16}$ |      | 3           | 1 $\frac{1}{2}$  | A500C   | 73             |
| 1                | p346       | PL $\frac{1}{2}$ x16   |      | 4           | 6                | A36     | 123            |
| 2                | p688       | PL $\frac{1}{4}$ x6    |      | 0           | 6                | A36     | 5              |
| 2                | F-09.00FR6 | FRAME                  |      |             |                  |         | 500            |
| 2                | F-09.00FR6 | HSS6x6x $\frac{9}{16}$ |      | 3           | 5 $\frac{3}{4}$  | A500C   | 162            |
| 2                | w125       | W8x31                  |      | 1           | 5                | A992    | 88             |
| 2                | p346       | PL $\frac{1}{2}$ x16   |      | 4           | 6                | A36     | 245            |
| 2                | p688       | PL $\frac{1}{4}$ x6    |      | 0           | 6                | A36     | 5              |


Total weight : 2679

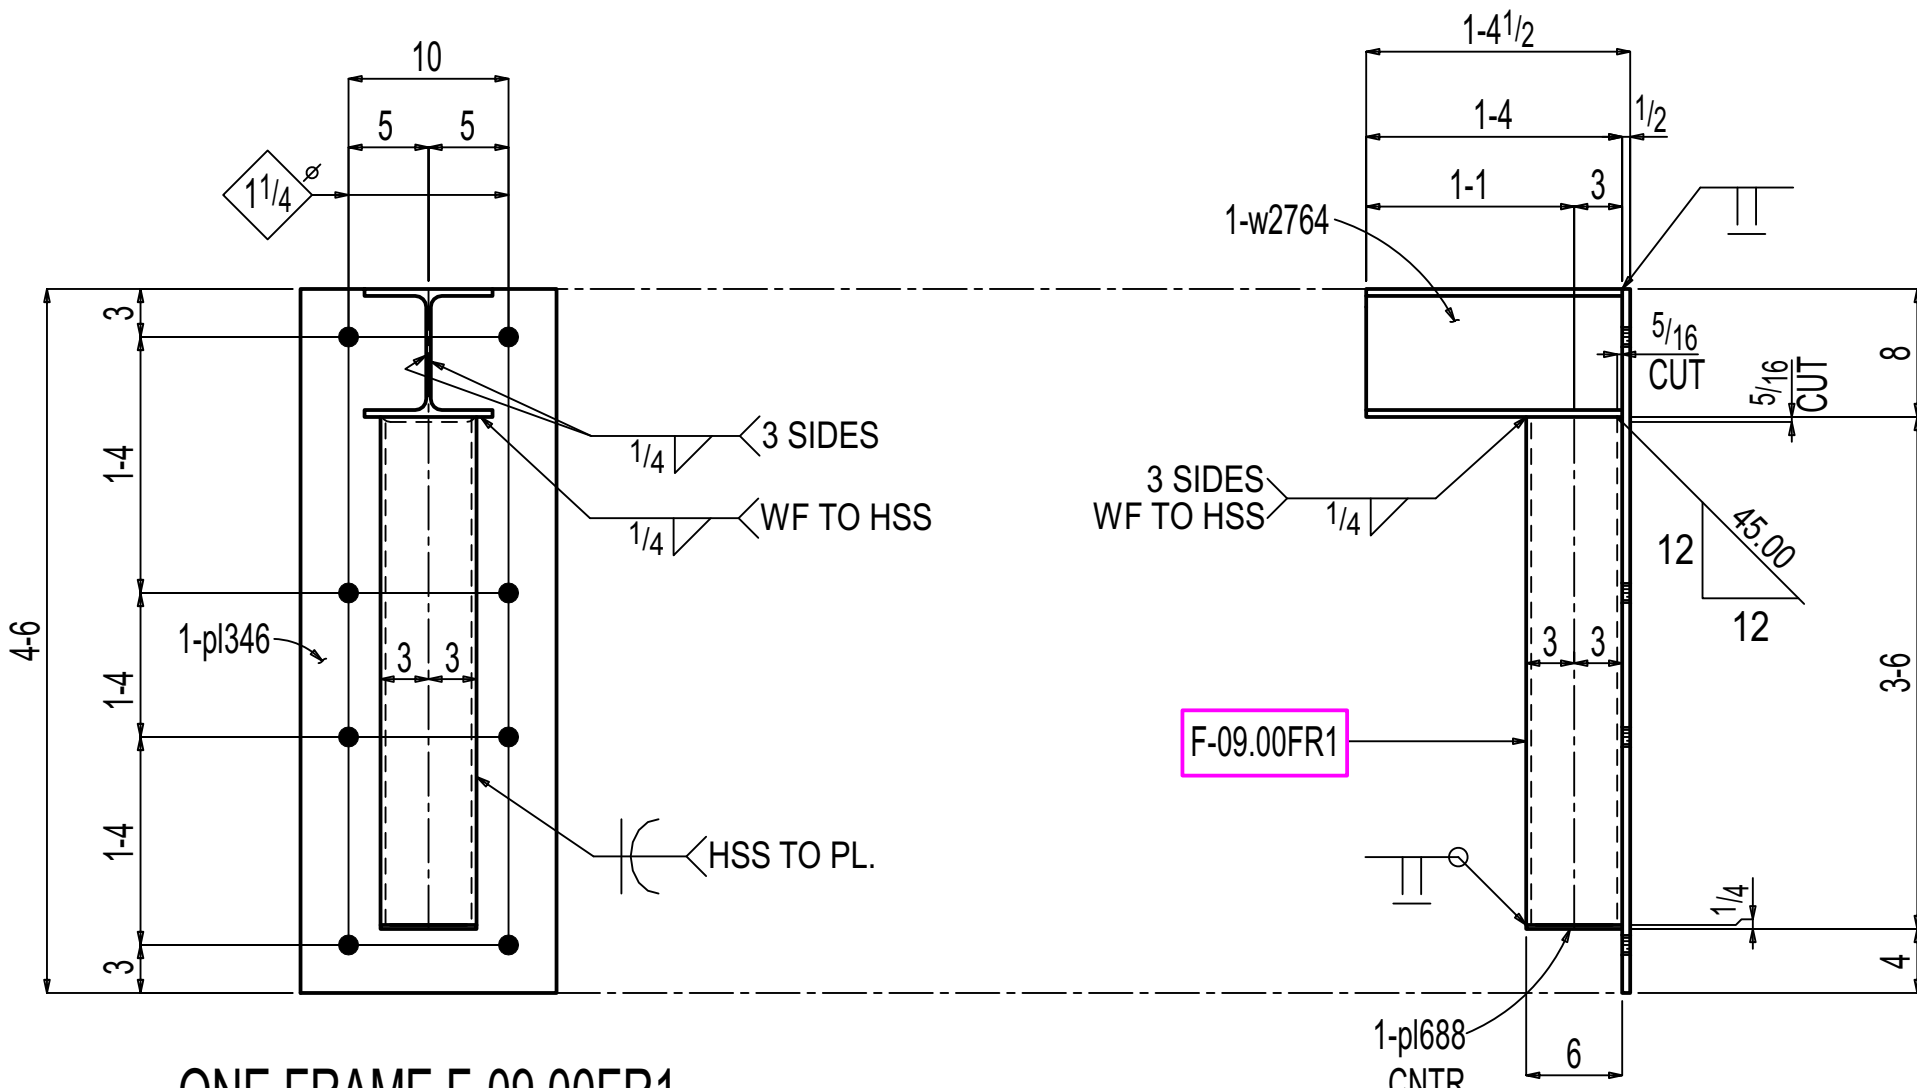


ONE FRAME F-09.00FR1

THIS PIECEMARK COMBINED  
WITH F-09.00FR3


ONE FRAME F-09.00FR2

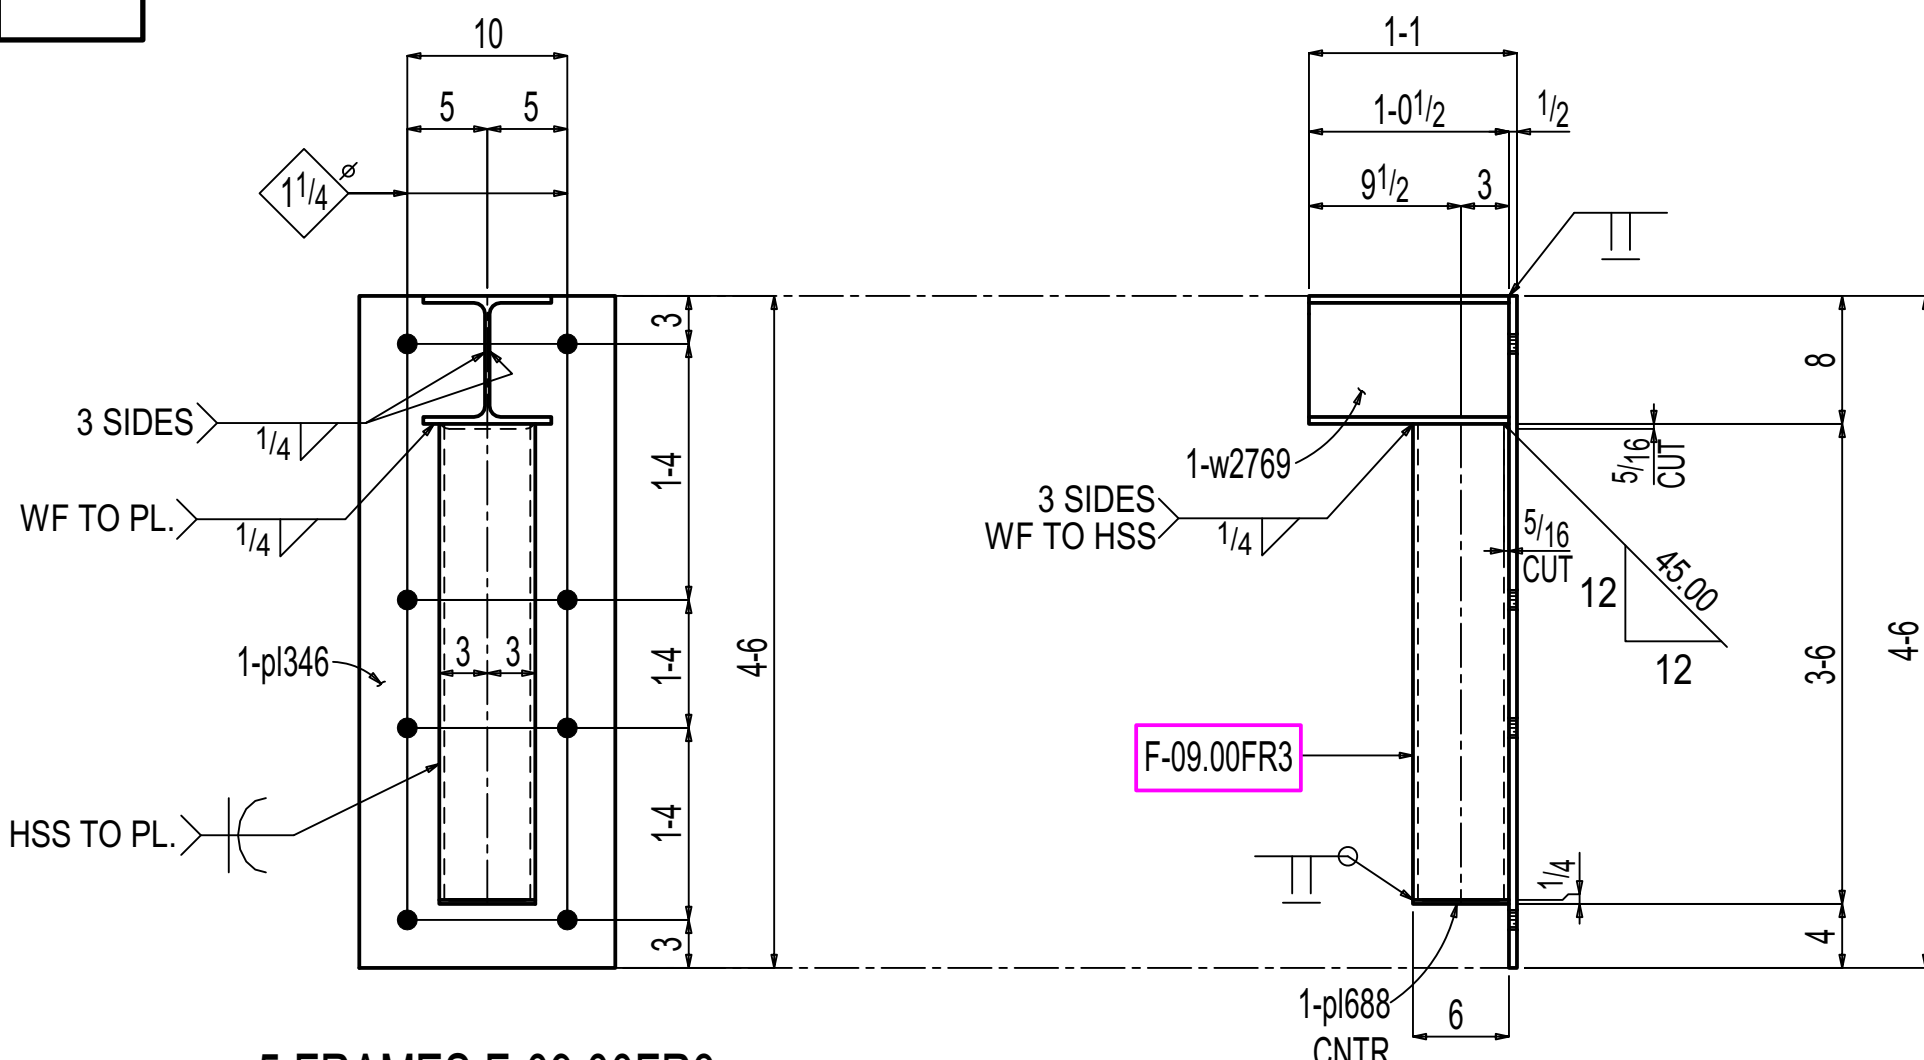


5 FRAMES F-09.00FR3

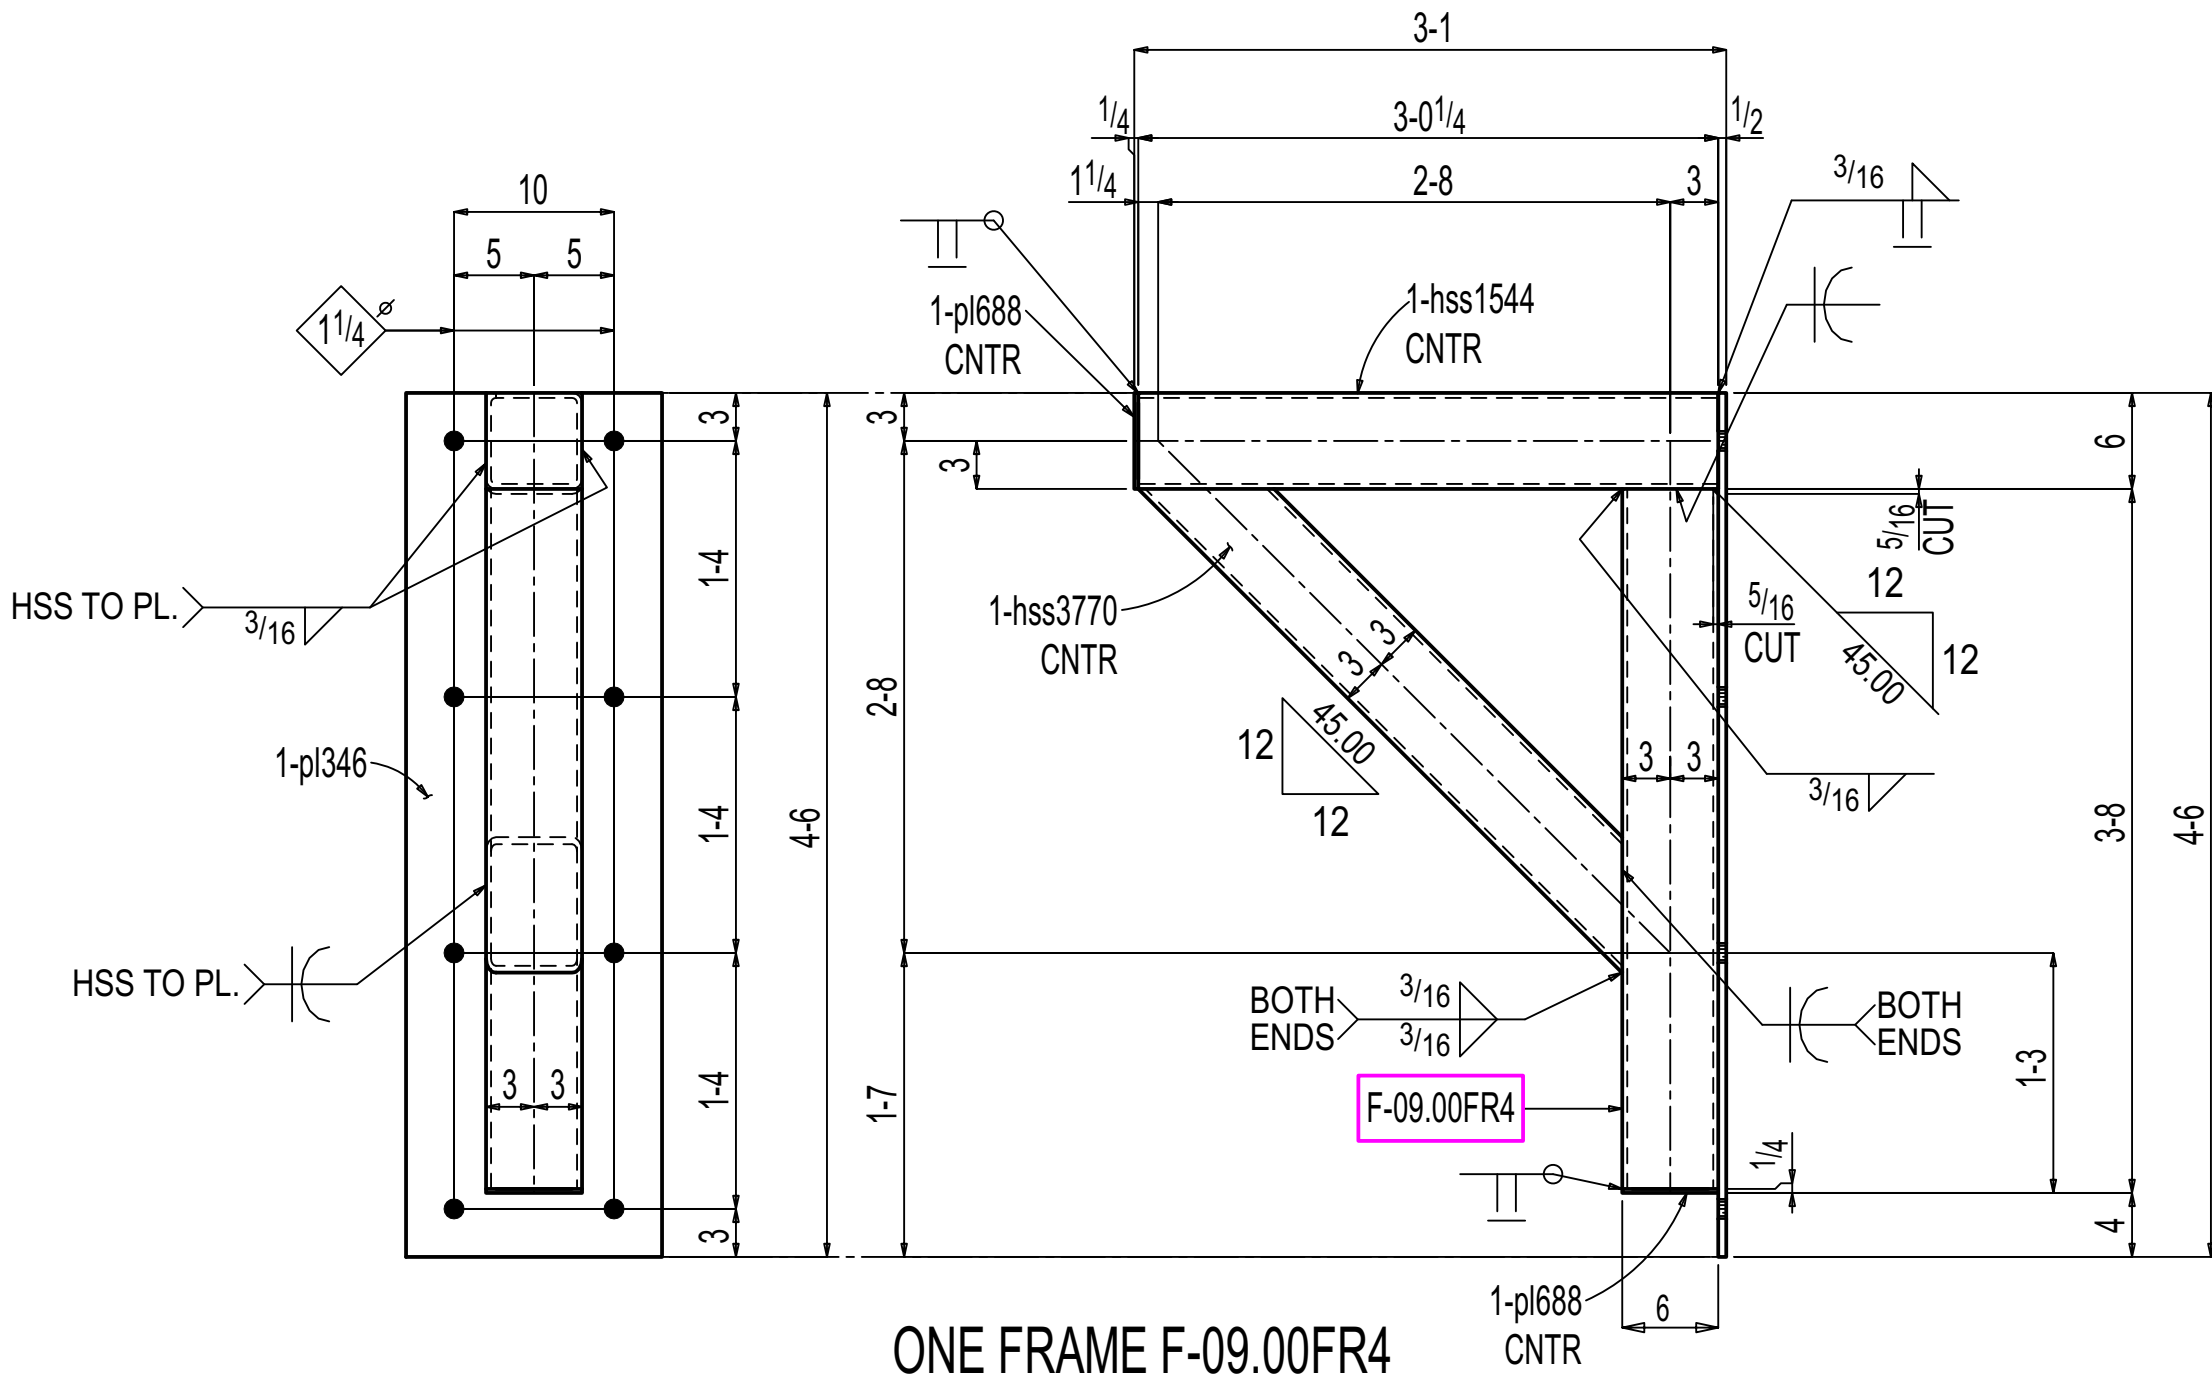

ONE FRAME F-09.00FR4

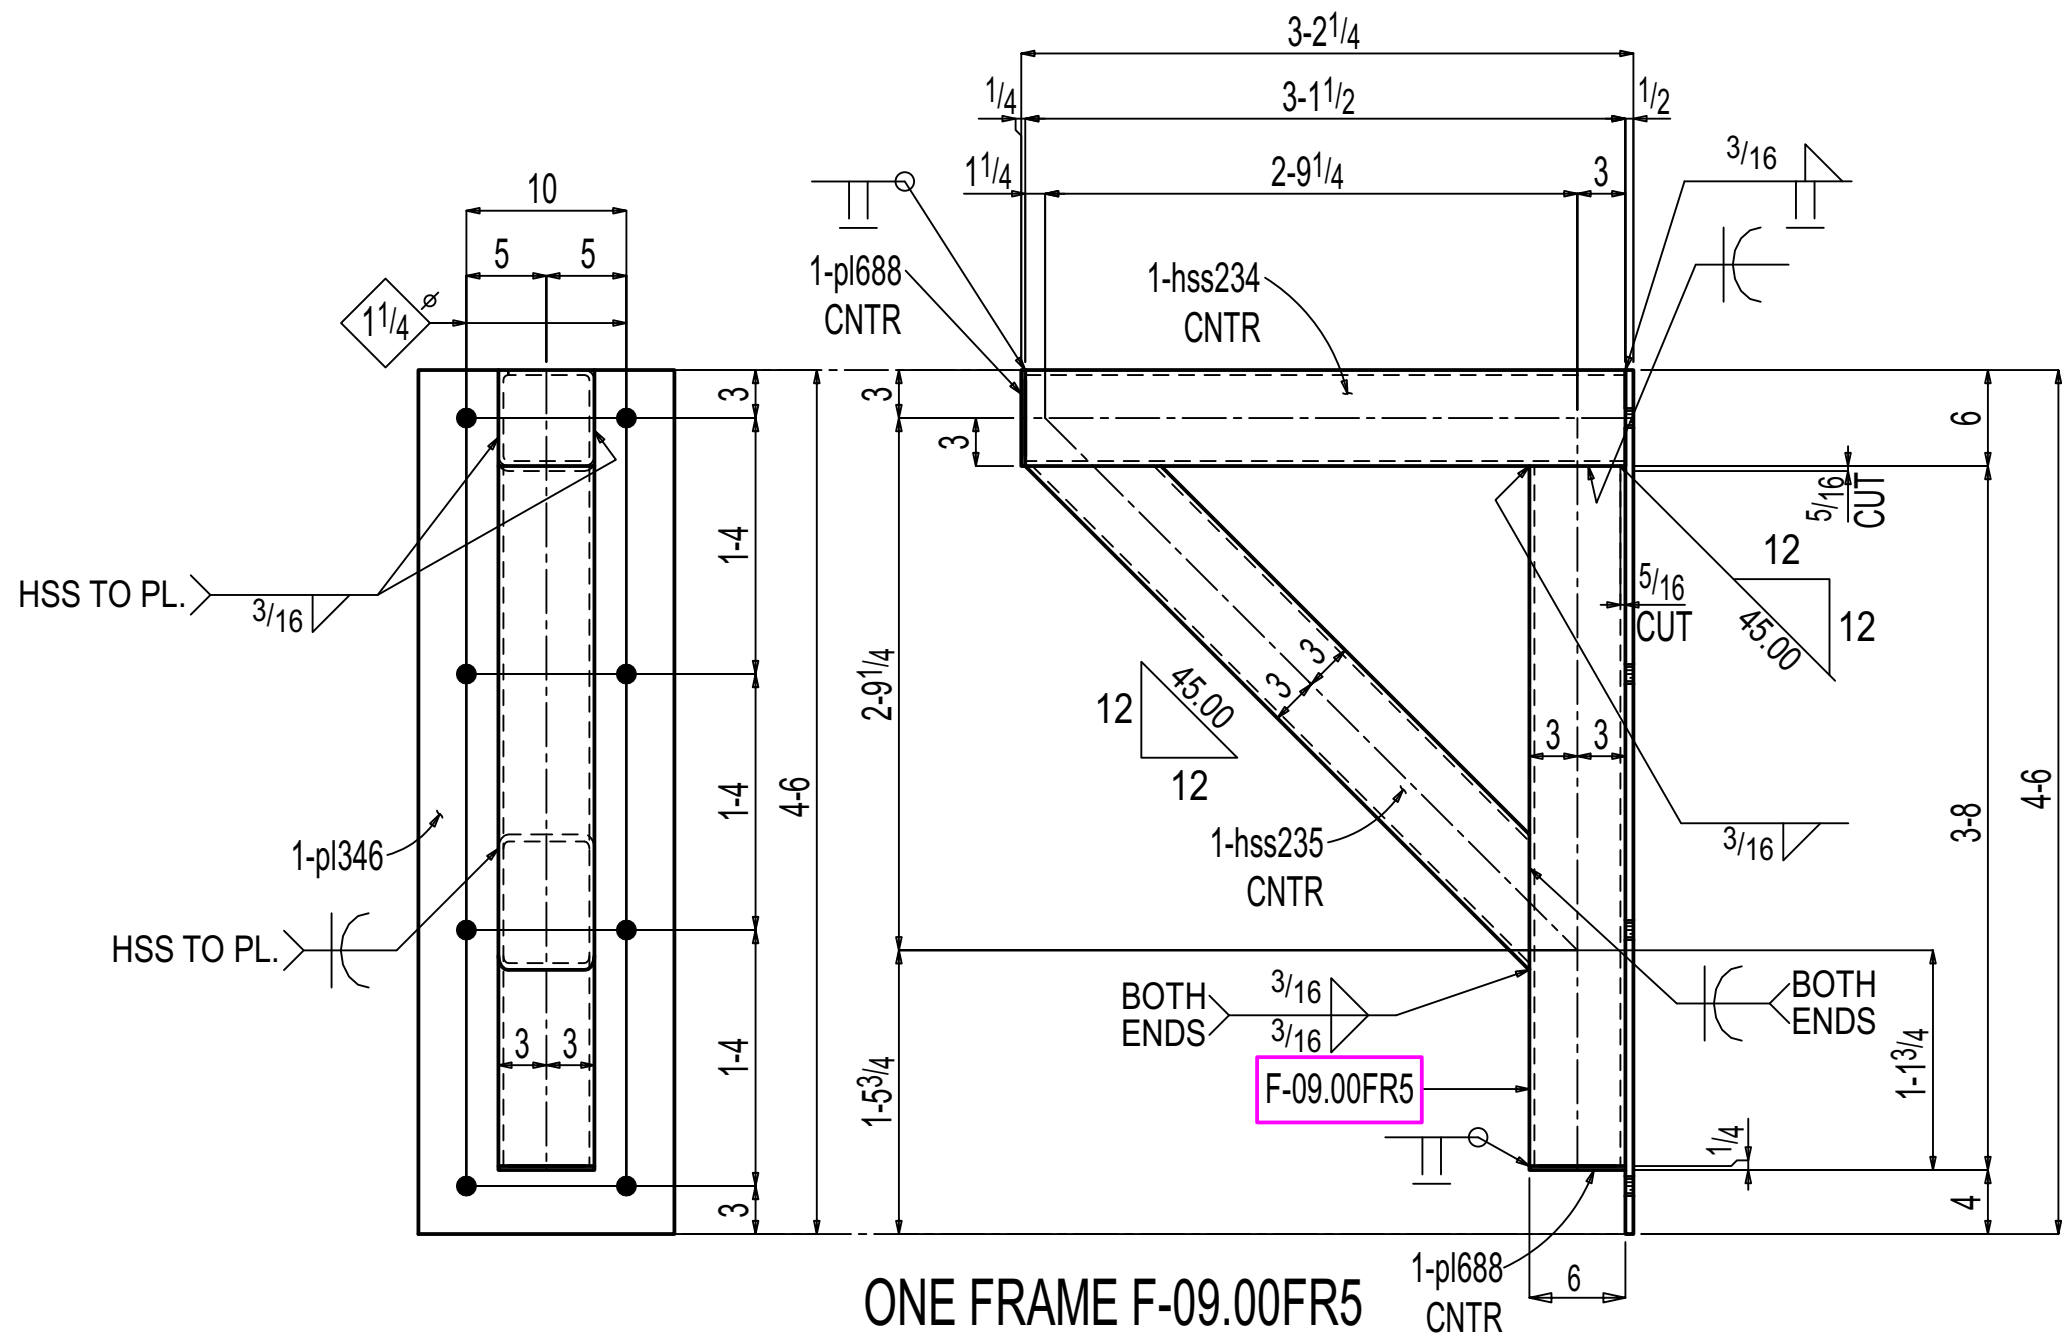

ONE FRAME F-09.00FR5

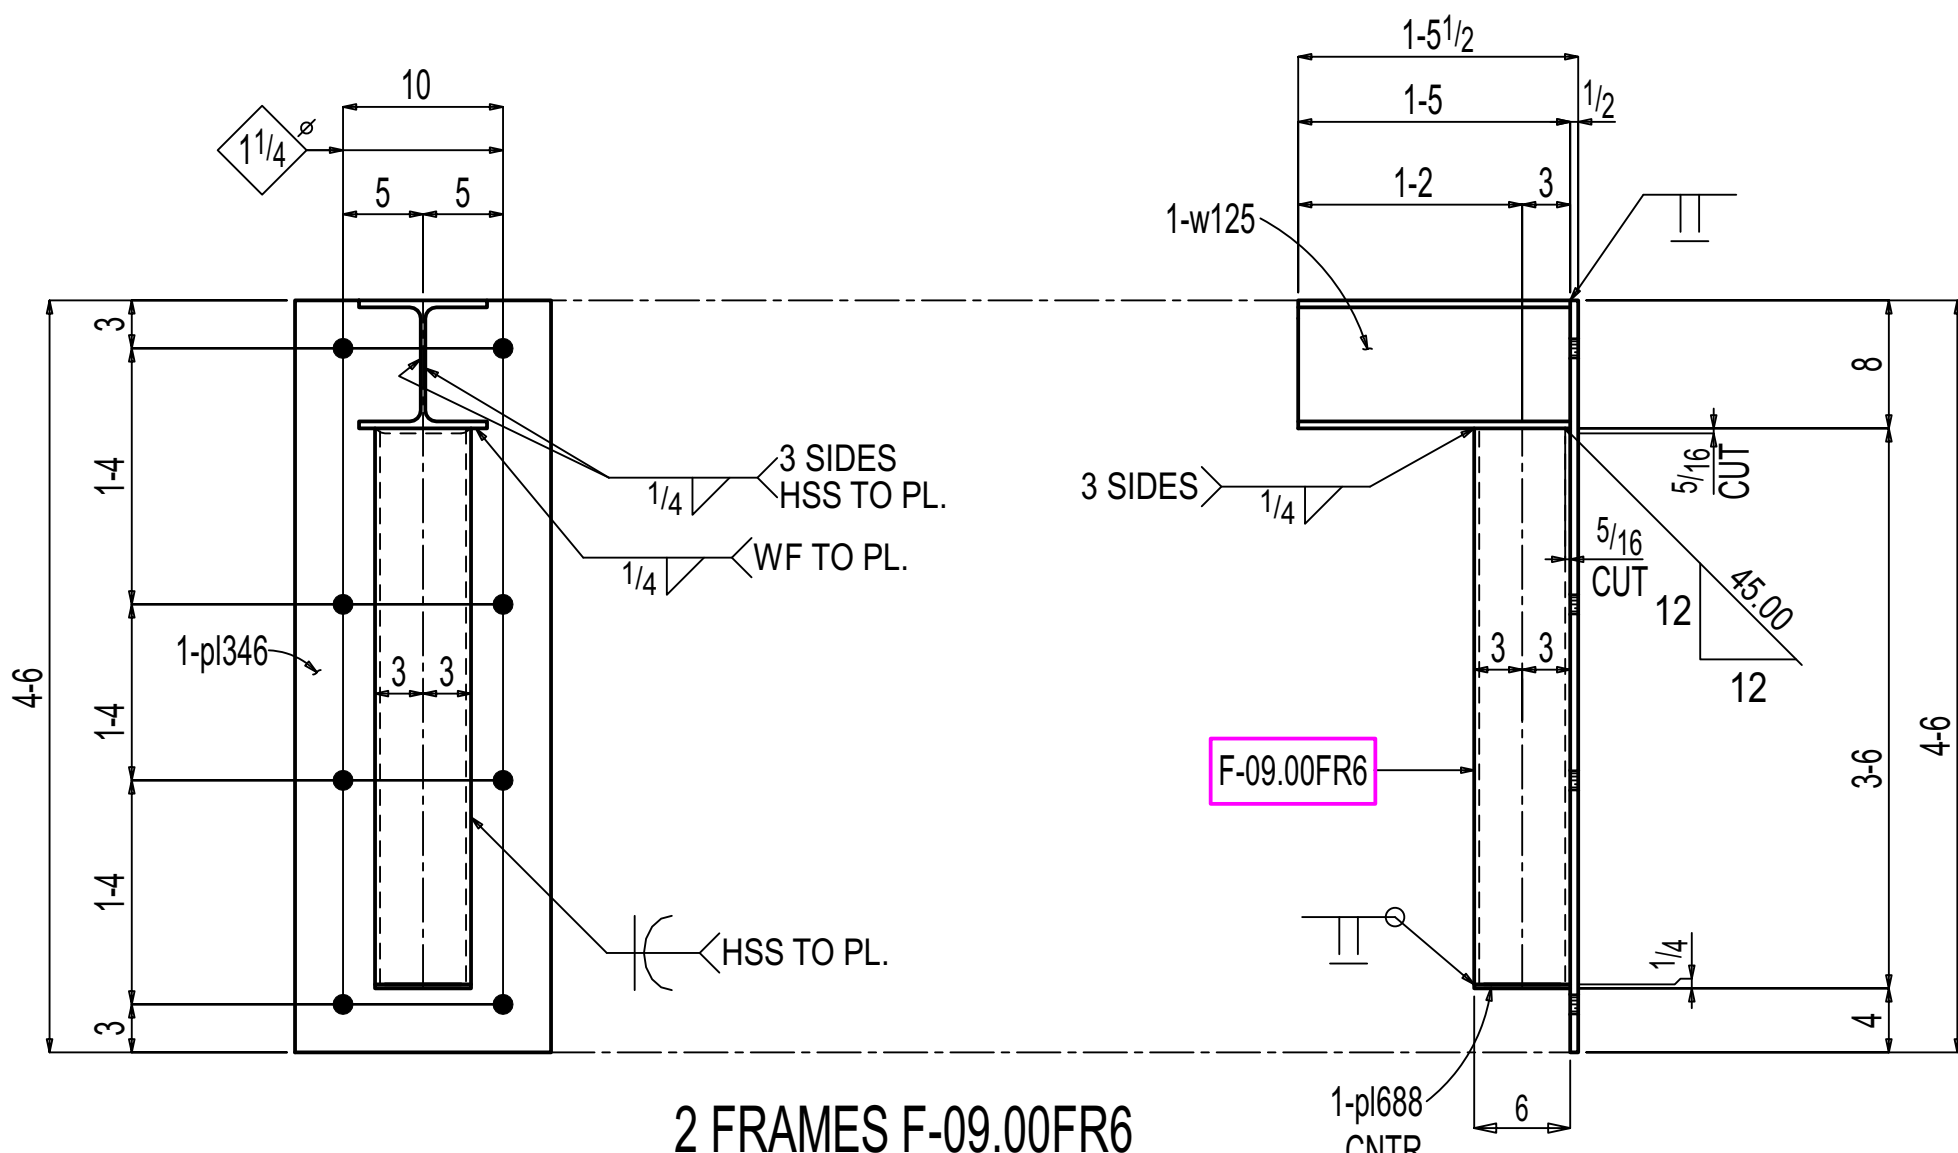

2 FRAMES F-09.00FR6

PAINT :NO PAINT  
PREPARATION :SSPC-SP3

| General Notes                                                                        |                 |                 |            |
|--------------------------------------------------------------------------------------|-----------------|-----------------|------------|
| *Structural steel shall conform to ASTM-A992.                                        |                 |                 |            |
| *Structural SQR/RND,tubing conform to ASTM A500 Grade C                              |                 |                 |            |
| *Pipe shall conform to ASTM A53, Grade B.                                            |                 |                 |            |
| *Channels, Angles and plates shall conform to A36.                                   |                 |                 |            |
| *All bolts shall be $\frac{3}{4}$ " High strength in accordance with ASTM A325 (UNO) |                 |                 |            |
| *Welding Electrodes for Carbon steel :E70xx                                          |                 |                 |            |
| 5                                                                                    | 0               | For Fabrication | 11-14-2025 |
| 4                                                                                    | D               | For Re-Approval | 10-24-2025 |
| 3                                                                                    | C               | For Re-Approval | 09-19-2025 |
| 2                                                                                    | B               | For Re-Approval | 06-23-2025 |
| 1                                                                                    | A               | For Approval    | 02-25-2025 |
| # of Copies                                                                          | Revision/ Issue | Destination     | Date       |

IRON FABRICATION SERVICES, LLC.

3029 M. Street, NW, Suite 202  
Washington, DC 20007  
Tel: 202-800-5599  
Fax: 202-478-0303

Project Name and Address  
**MARYLAND AVENUE**  
Location: **1250 MARYLAND AVENUE SW  
WASHINGTON, DC 20024**

Contractor:  
**BALFOUR BEATTY**

Approved for Fabrication by: Signature

Contract # **224009** Drawing # **F-09.00**

Contract Item: **FRAME**

Ref:  
**SOW - 09: E-09.00 - E-09.02**





Date  
01/ 23/ 2025  
Scale  
VARIES

Drawing Title:  
**FRAME DETAIL**



| BILL OF MATERIAL |            |             |      |             |         |        |         |
|------------------|------------|-------------|------|-------------|---------|--------|---------|
| LINE #           | QTY        | PC          | MARK | DESCRIPTION | LENGTH  | WEIGHT | ADVANCE |
|                  | TOTAL      |             |      |             | TOTAL   |        | MILL #  |
| ONE              | F-09.01FR1 | FRAME       |      |             |         | 155    |         |
| 1                | F-09.01FR1 | HSS6x2x5/16 |      | 4           | 89 1/16 | A500C  | 70      |
| 1                | p347       | PL1/2x9     |      | 5           | 6       | A36    | 84      |
| 1                | p3034      | PL1/4x2     |      | 0           | 6       | A36    | 1       |
|                  |            |             |      |             |         |        |         |
| ONE              | F-09.01FR2 | FRAME       |      |             |         | 212    |         |
| 1                | F-09.01FR2 | HSS6x6x5/16 |      | 3           | 81 1/16 | A500C  | 87      |
| 1                | p346       | PL1/2x16    |      | 4           | 6       | A36    | 123     |
| 1                | p688       | PL1/4x6     |      | 0           | 6       | A36    | 3       |
|                  |            |             |      |             |         |        |         |
| ONE              | F-09.01FR3 | FRAME       |      |             |         | 344    |         |
| 1                | F-09.01FR3 | HSS6x6x5/16 |      | 3           | 73/4    | A500C  | 85      |
| 1                | hss319     | HSS6x6x5/16 |      | 2           | 103/4   | A500C  | 68      |
| 1                | hss320     | HSS6x6x5/16 |      | 2           | 83/4    | A500C  | 64      |
| 1                | p346       | PL1/2x16    |      | 4           | 6       | A36    | 123     |
| 2                | p688       | PL1/4x6     |      | 0           | 6       | A36    | 5       |
|                  |            |             |      |             |         |        |         |
| ONE              | F-09.01FR4 | FRAME       |      |             |         | 212    |         |
| 1                | F-09.01FR4 | HSS6x6x5/16 |      | 3           | 83/4    | A500C  | 87      |
| 1                | p346       | PL1/2x16    |      | 4           | 6       | A36    | 123     |
| 1                | p688       | PL1/4x6     |      | 0           | 6       | A36    | 3       |

Total weight : 923

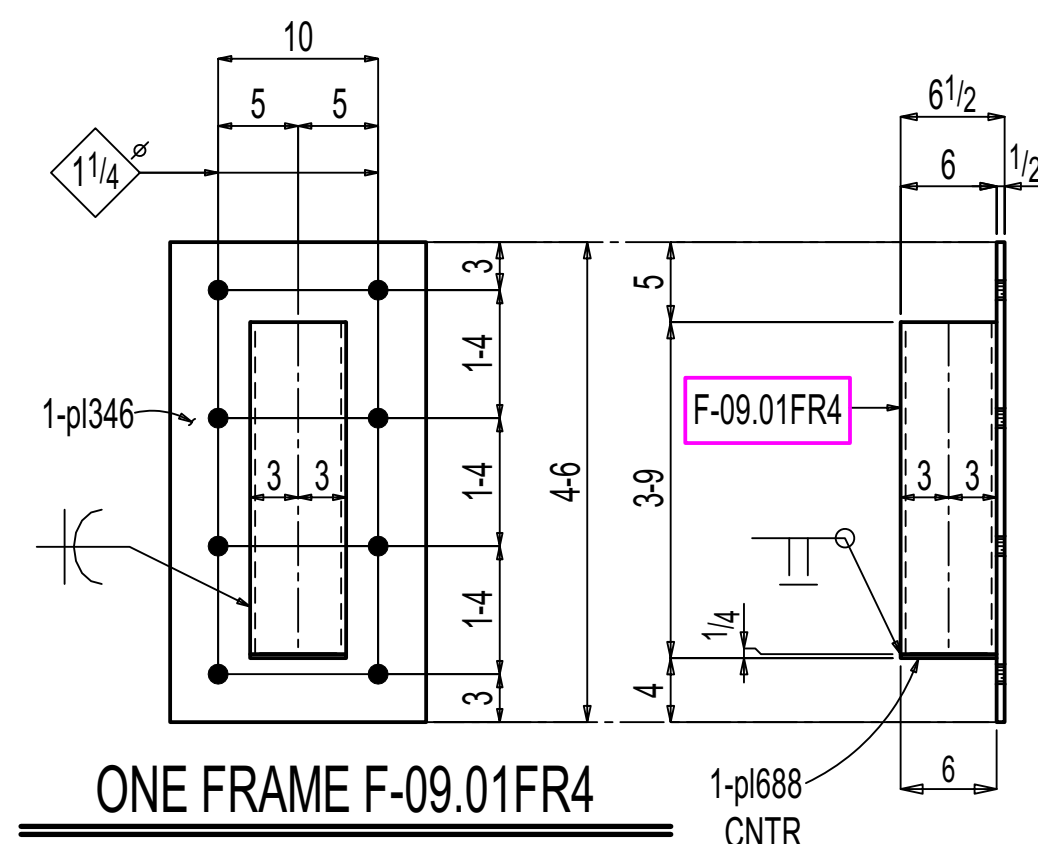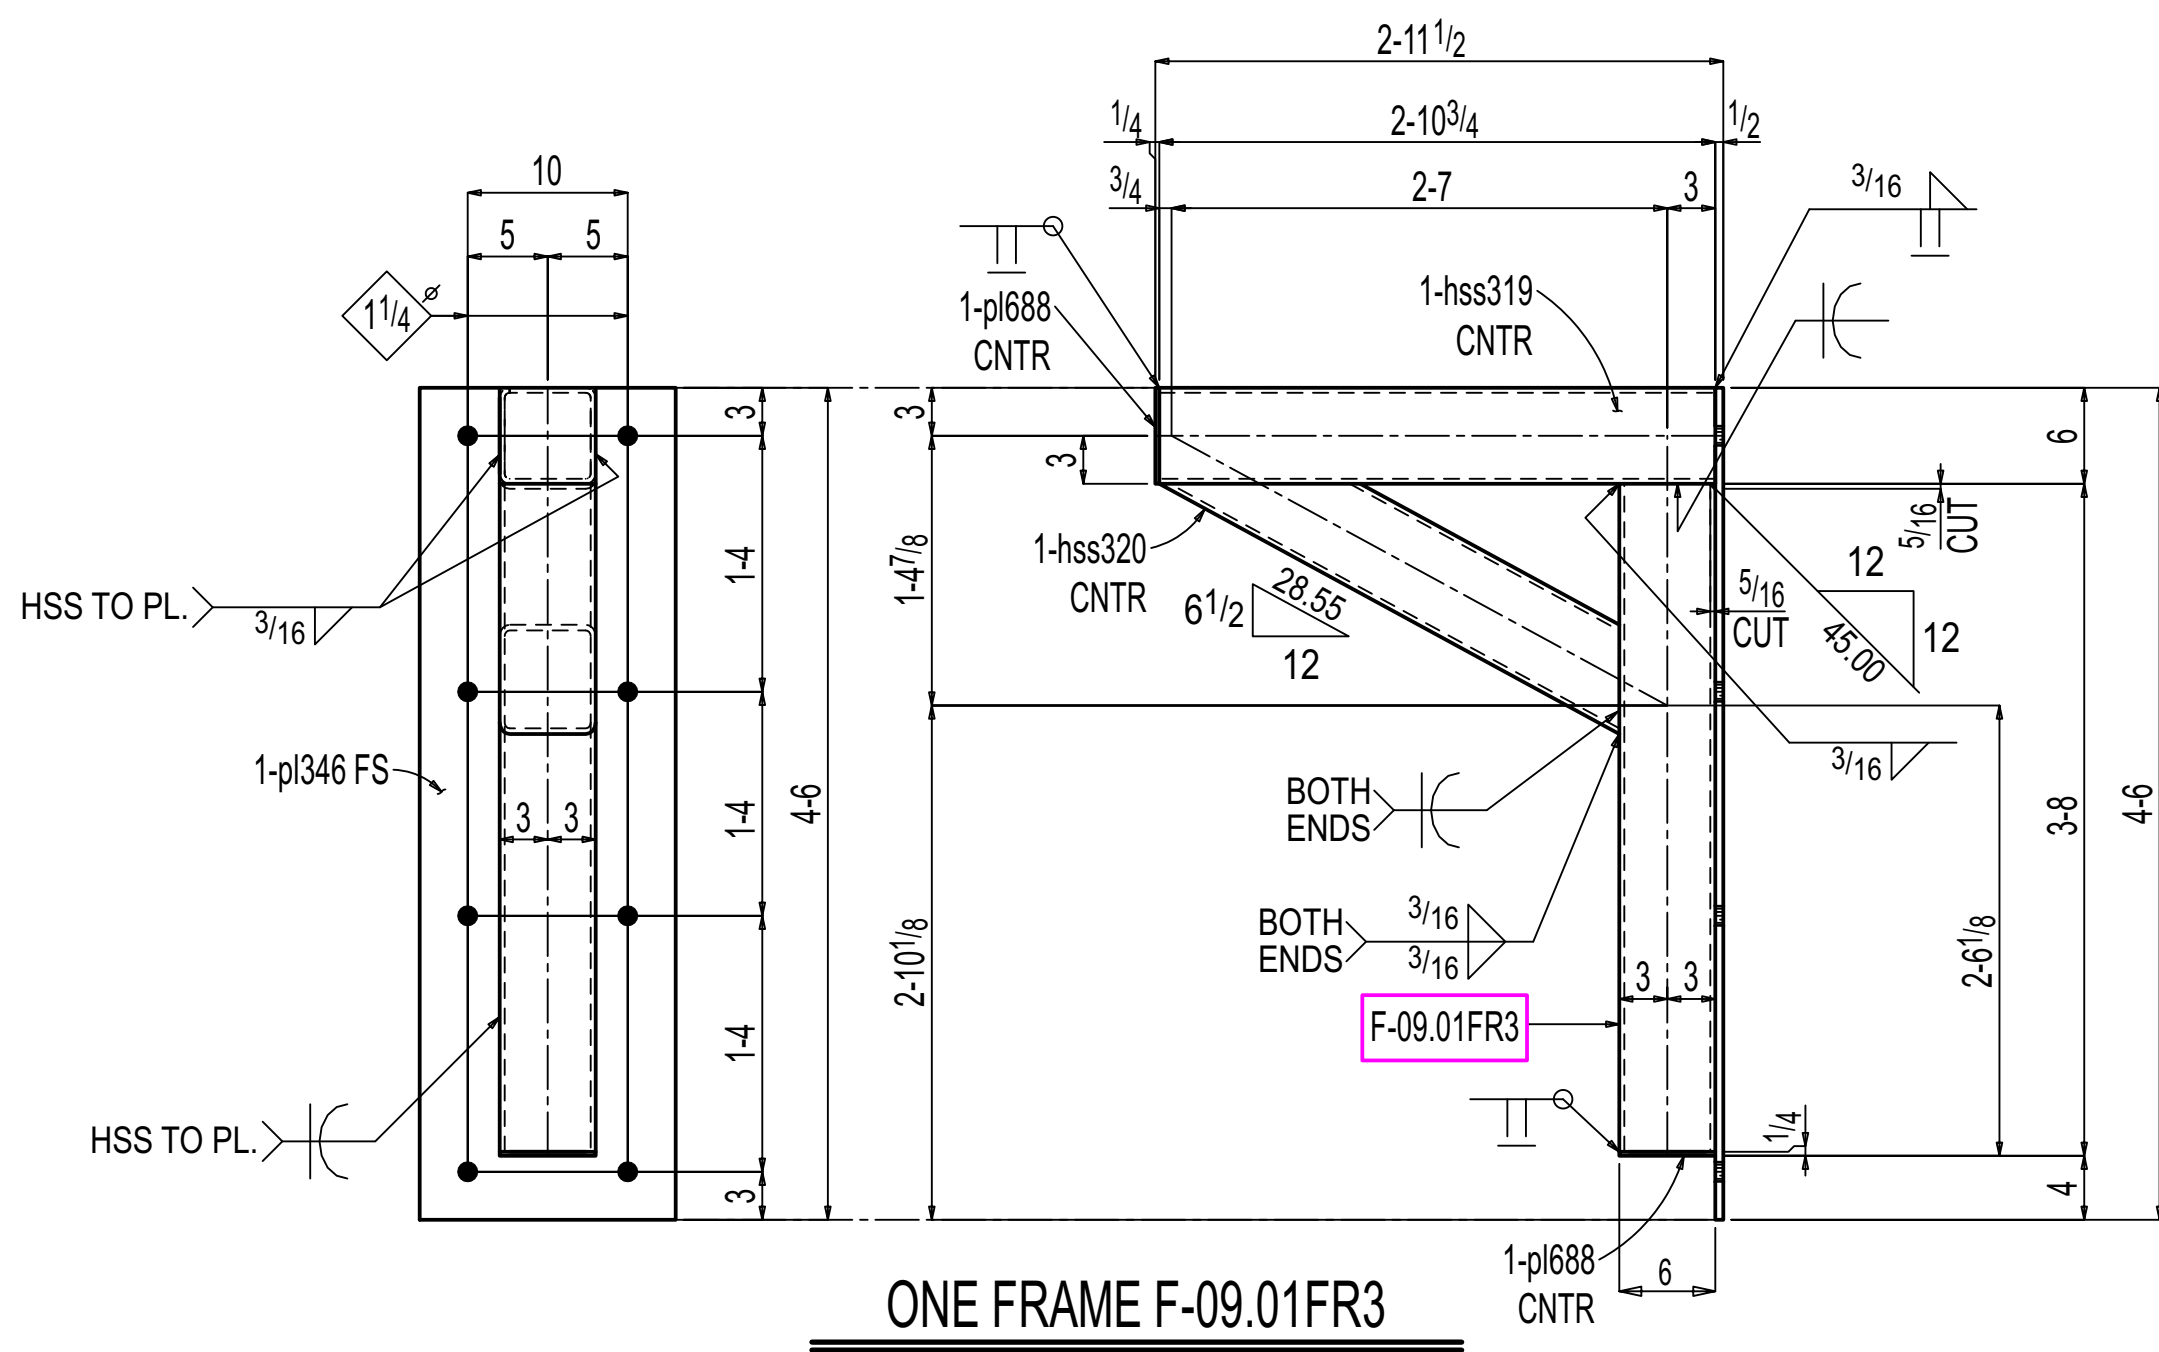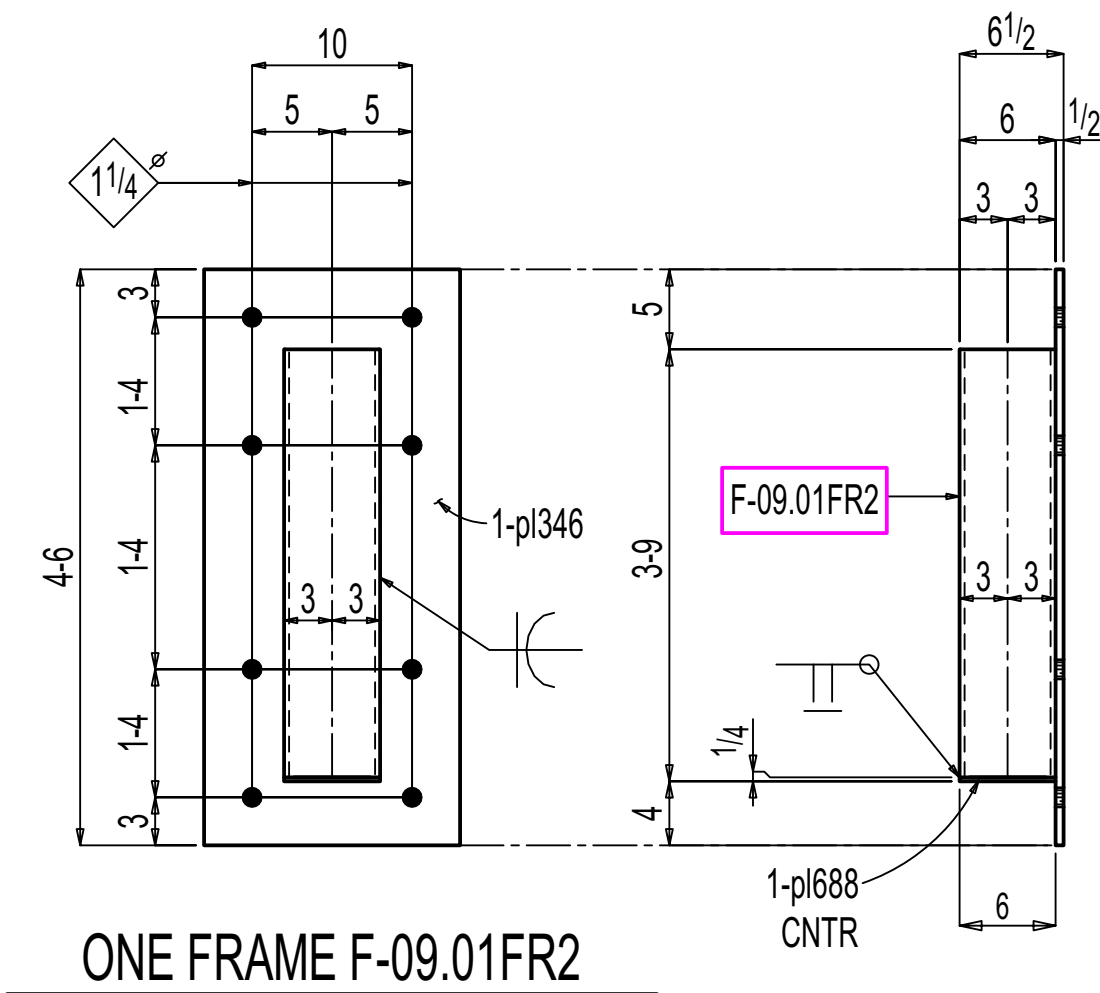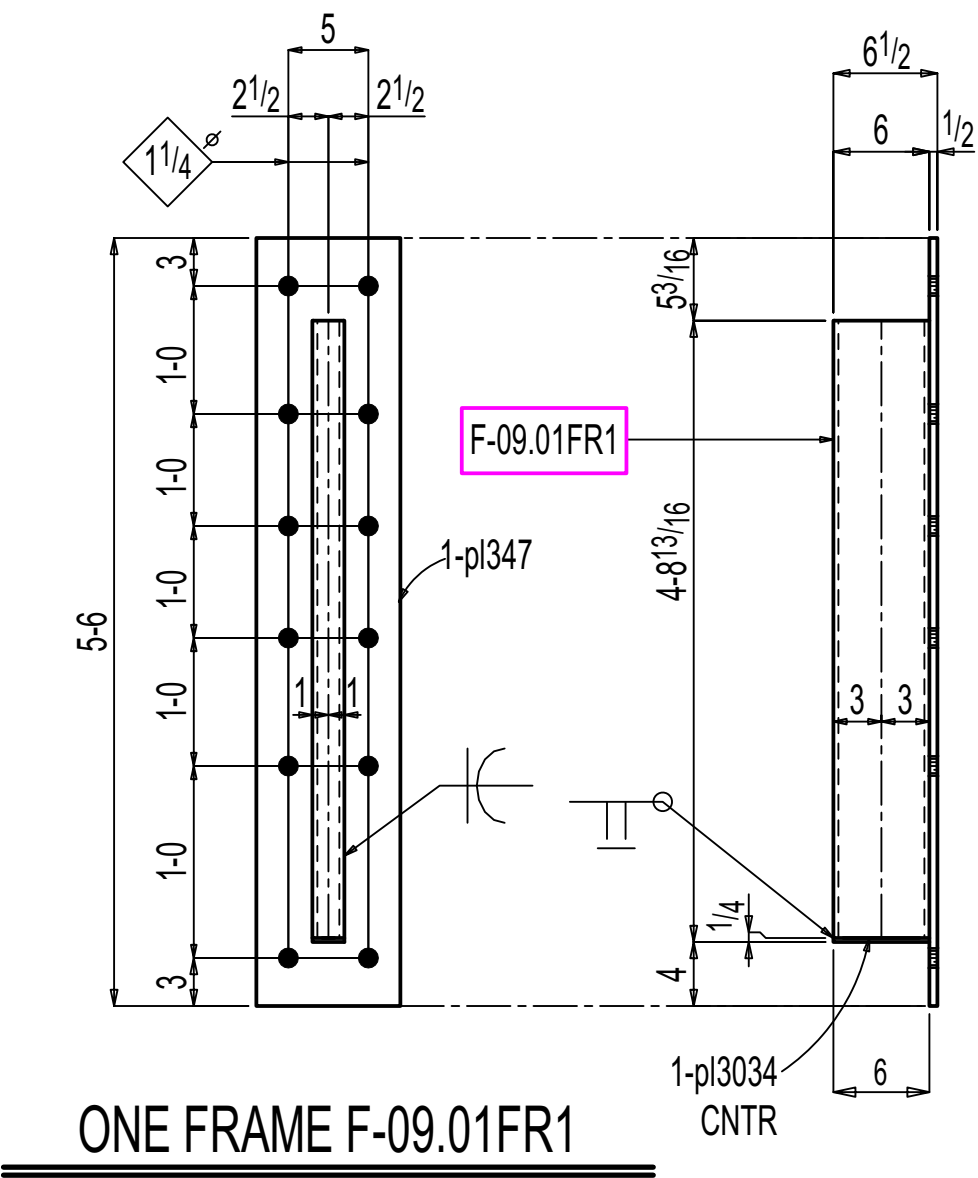

PAINT :NO PAINT  
PREPARATION :SSPC-SP3

| General Notes                                                             |                 |                 |            |
|---------------------------------------------------------------------------|-----------------|-----------------|------------|
| *Structural steel shall conform to ASTM-A992.                             |                 |                 |            |
| *Structural SQR/RND,tubing conform to ASTM A500 Grade C                   |                 |                 |            |
| *Pipe shall conform to ASTM A53, Grade B.                                 |                 |                 |            |
| *Channels, Angles and plates shall conform to A36.                        |                 |                 |            |
| *All bolts shall be 3/4" High strength in accordance with ASTM A325 (UNO) |                 |                 |            |
| *Welding Electrodes for Carbon steel :E70xx                               |                 |                 |            |
| 5                                                                         | 0               | For Fabrication | 11-14-2025 |
| 4                                                                         | D               | For Re-Approval | 10-24-2025 |
| 3                                                                         | C               | For Re-Approval | 09-19-2025 |
| 2                                                                         | B               | For Re-Approval | 06-23-2025 |
| 1                                                                         | A               | For Approval    | 02-25-2025 |
| # of Copies                                                               | Revision/ Issue | Destination     | Date       |

IRON FABRICATION SERVICES, LLC.

3029 M. Street, NW, Suite 202  
Washington, DC 20007  
Tel: 202-800-5599  
Fax: 202-478-0303

Project Name and Address  
**MARYLAND AVENUE**  
Location: **1250 MARYLAND AVENUE SW  
WASHINGTON, DC 20024**

Contractor:  
**BALFOUR BEATTY**


Approved for Fabrication by: Signature

|                |                                    |                |                     |
|----------------|------------------------------------|----------------|---------------------|
| Contract #     | <b>224009</b>                      | Drawing #      | <b>F-09.01</b>      |
| Contract Item: | <b>FRAME</b>                       |                |                     |
| Ref:           | <b>SOW - 09: E-09.00 - E-09.02</b> |                |                     |
| Date           | <b>01/ 23/ 2025</b>                | Drawing Title: | <b>FRAME DETAIL</b> |
| Scale          | <b>VARIES</b>                      |                |                     |




| BILL OF MATERIAL       |            |                        |             |          |                    |              |                |
|------------------------|------------|------------------------|-------------|----------|--------------------|--------------|----------------|
| LINE #                 | QTY        | PC MARK                | DESCRIPTION | LENGTH   | REMARKS            | WEIGHT TOTAL | ADVANCE MILL # |
| ONE F-09.02FR1 FRAME   |            |                        |             |          |                    | 212          |                |
| 1                      | F-09.02FR1 | HSS6x6x3/16            |             | 3 8 1/2  | A500C              | 87           |                |
| 1                      | p246       | PL1/2x16               |             | 4 6      | A36                | 123          |                |
| 1                      | p688       | PL1/4x6                |             | 0 6      | A36                | 3            |                |
| ONE F-09.02FR2 FRAME   |            |                        |             |          |                    | 394          |                |
| 1                      | F-09.02FR2 | HSS6x6x3/16            |             | 3 7 3/4  | A500C              | 85           |                |
| 1                      | hss379     | HSS6x6x3/16            |             | 4 1 1/16 | A500C              | 95           |                |
| 1                      | hss375     | HSS6x6x3/16            |             | 3 8 1/4  | A500C              | 86           |                |
| 1                      | p246       | PL1/2x16               |             | 4 6      | A36                | 123          |                |
| 2                      | p688       | PL1/4x6                |             | 0 6      | A36                | 5            |                |
| ONE F-09.02M1 PLATE    |            |                        |             |          |                    | 189          |                |
| 1                      | F-09.02M1  | PL1x18                 |             | 2 1      | A36                | 128          |                |
| 1                      | p248       | PL1x8                  |             | 1 6      | A36                | 41           |                |
| 3                      | p287       | PL1/2x7                |             | 0 7      | A36                | 21           |                |
| ONE F-09.02M2 HSS      |            |                        |             |          |                    | 153          |                |
| 1                      | F-09.02M2  | HSS6x6x3/8             |             | 5 5      | A500C              | 149          |                |
| 1                      | p2494      | PL1/4x6                |             | 0 10     | A36                | 4            |                |
| ONE F-09.02M3 HSS      |            |                        |             |          |                    | 201          |                |
| 1                      | F-09.02M3  | HSS6x6x3/8             |             | 6 1      | A500C              | 167          |                |
| 1                      | a156       | L5x5x3/16              |             | 0 10     | A36                | 9            |                |
| 1                      | p245       | PL1/2x6                |             | 1 8      | A36                | 17           |                |
| 2                      | p688       | PL1/4x6                |             | 0 6      | A36                | 5            |                |
| 2                      |            | 3/4 Dia A325N          |             | 0 7 1/2  | +1HD WASH          | 3            |                |
| FIELD BOLTS            |            |                        |             |          |                    |              |                |
| 2                      |            | 1/2 Dia HILTI K8-TZ2   |             | 0 7      |                    |              |                |
| EXPANSION ANCHOR       |            |                        |             |          | (5 1/2" EMBEDMENT) |              |                |
| ONE F-09.02M4 PLATE    |            |                        |             |          |                    | 54           |                |
| 1                      | F-09.02M4  | PL3/4x6                |             | 2 4 1/2  | A36                | 36           |                |
| 2                      | p2380      | PL3/4x6                |             | 0 7      | A36                | 18           |                |
| ONE F-09.02M5 PLATE    |            |                        |             |          |                    | 117          |                |
| 1                      | F-09.02M5  | PL5/8x22               |             | 2 6      | A36                | 117          |                |
| FIELD BOLTS            |            |                        |             |          |                    |              |                |
| 6                      |            | 3/4 Dia HILTI HAS V-36 |             | 0 8      |                    |              |                |
| w/ HILTI HIT HY-200 V3 |            |                        |             |          | (5" EMBEDMENT)     |              |                |
| ADHESIVE               |            |                        |             |          |                    |              |                |
| ONE F-09.02M6 PLATE    |            |                        |             |          |                    | 30           |                |
| 1                      | F-09.02M6  | PL1/2x9                |             | 1 4      | A36                | 20           |                |
| 1                      | a3197      | L6x6x3/8               |             | 0 8      | A36                | 10           |                |
| FIELD BOLTS            |            |                        |             |          |                    |              |                |
| 2                      |            | 3/4 Dia HILTI HAS V-36 |             | 0 10     |                    |              |                |
| w/ HILTI HIT HY-200 V3 |            |                        |             |          | (8" EMBEDMENT)     |              |                |
| ADHESIVE               |            |                        |             |          |                    |              |                |


Total weight : 1350

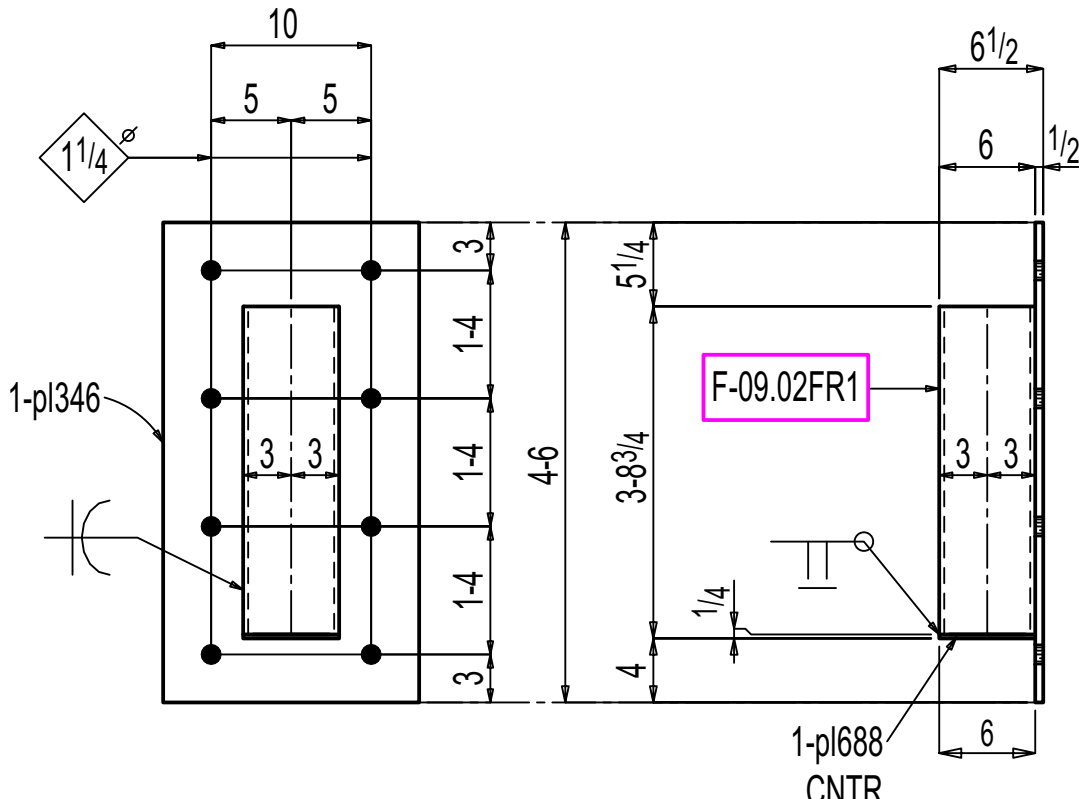


ONE FRAME F-09.02FR1

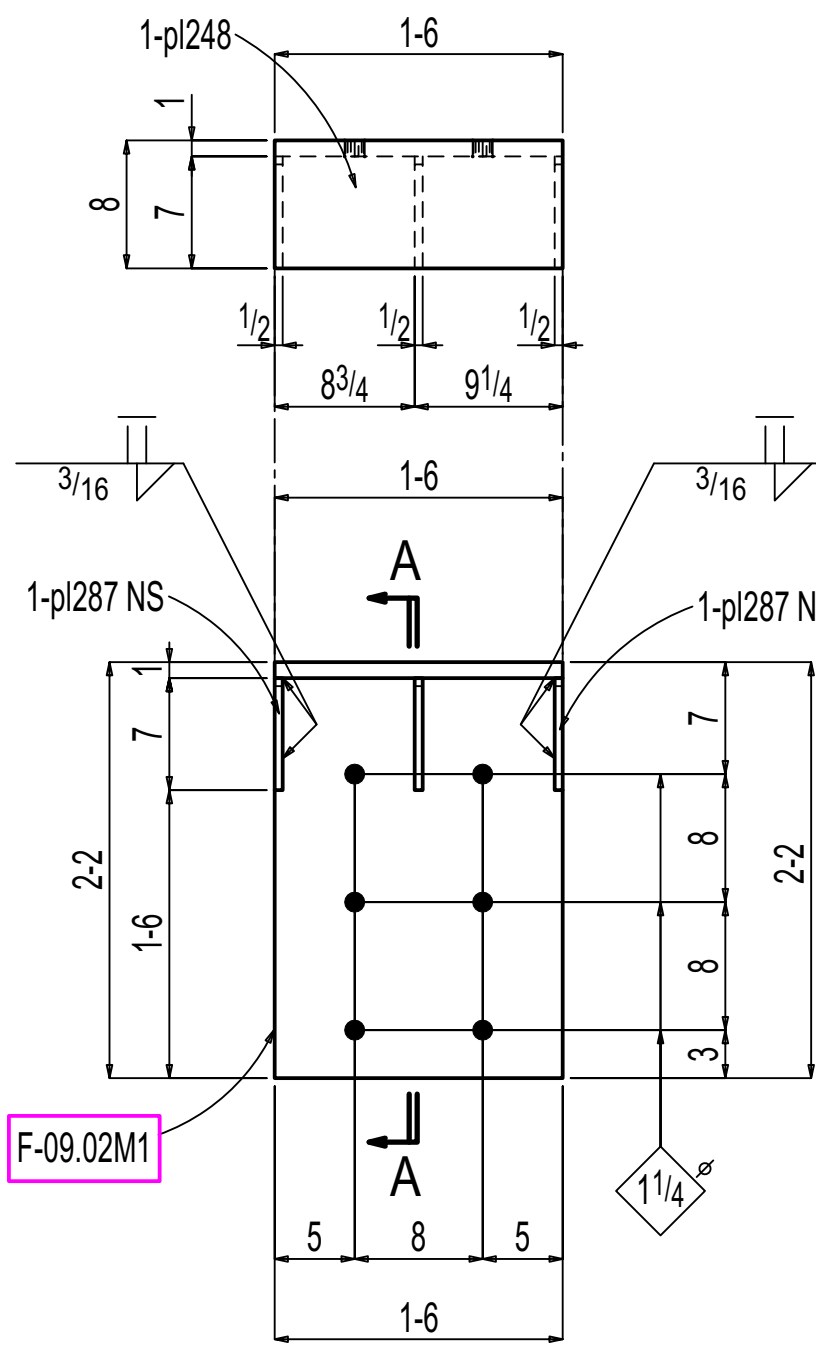


ONE PLATE F-09.02M1

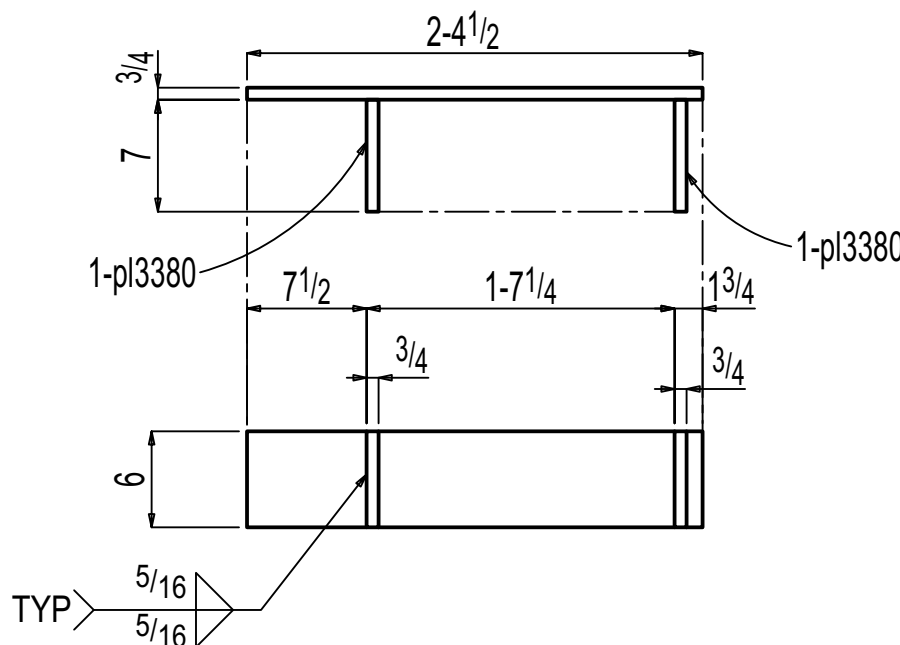


ONE PLATE F-09.02M4

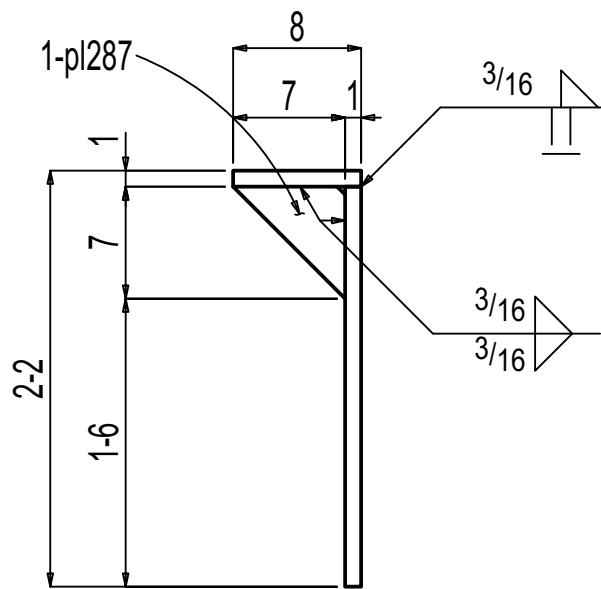


Section A-A  
F-09.02M1

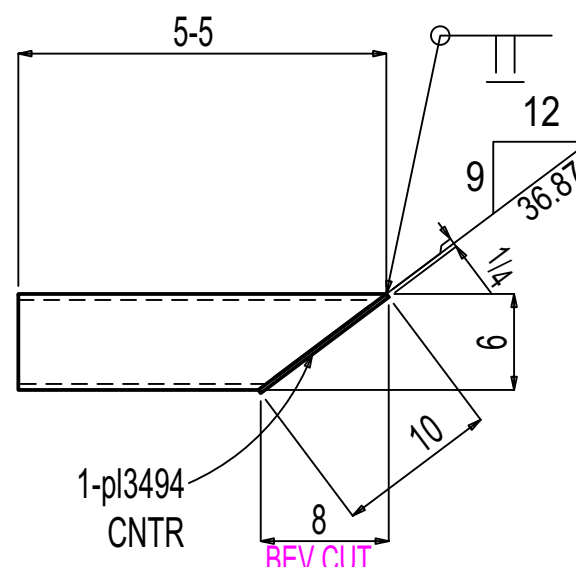

ONE HSS F-09.02M2

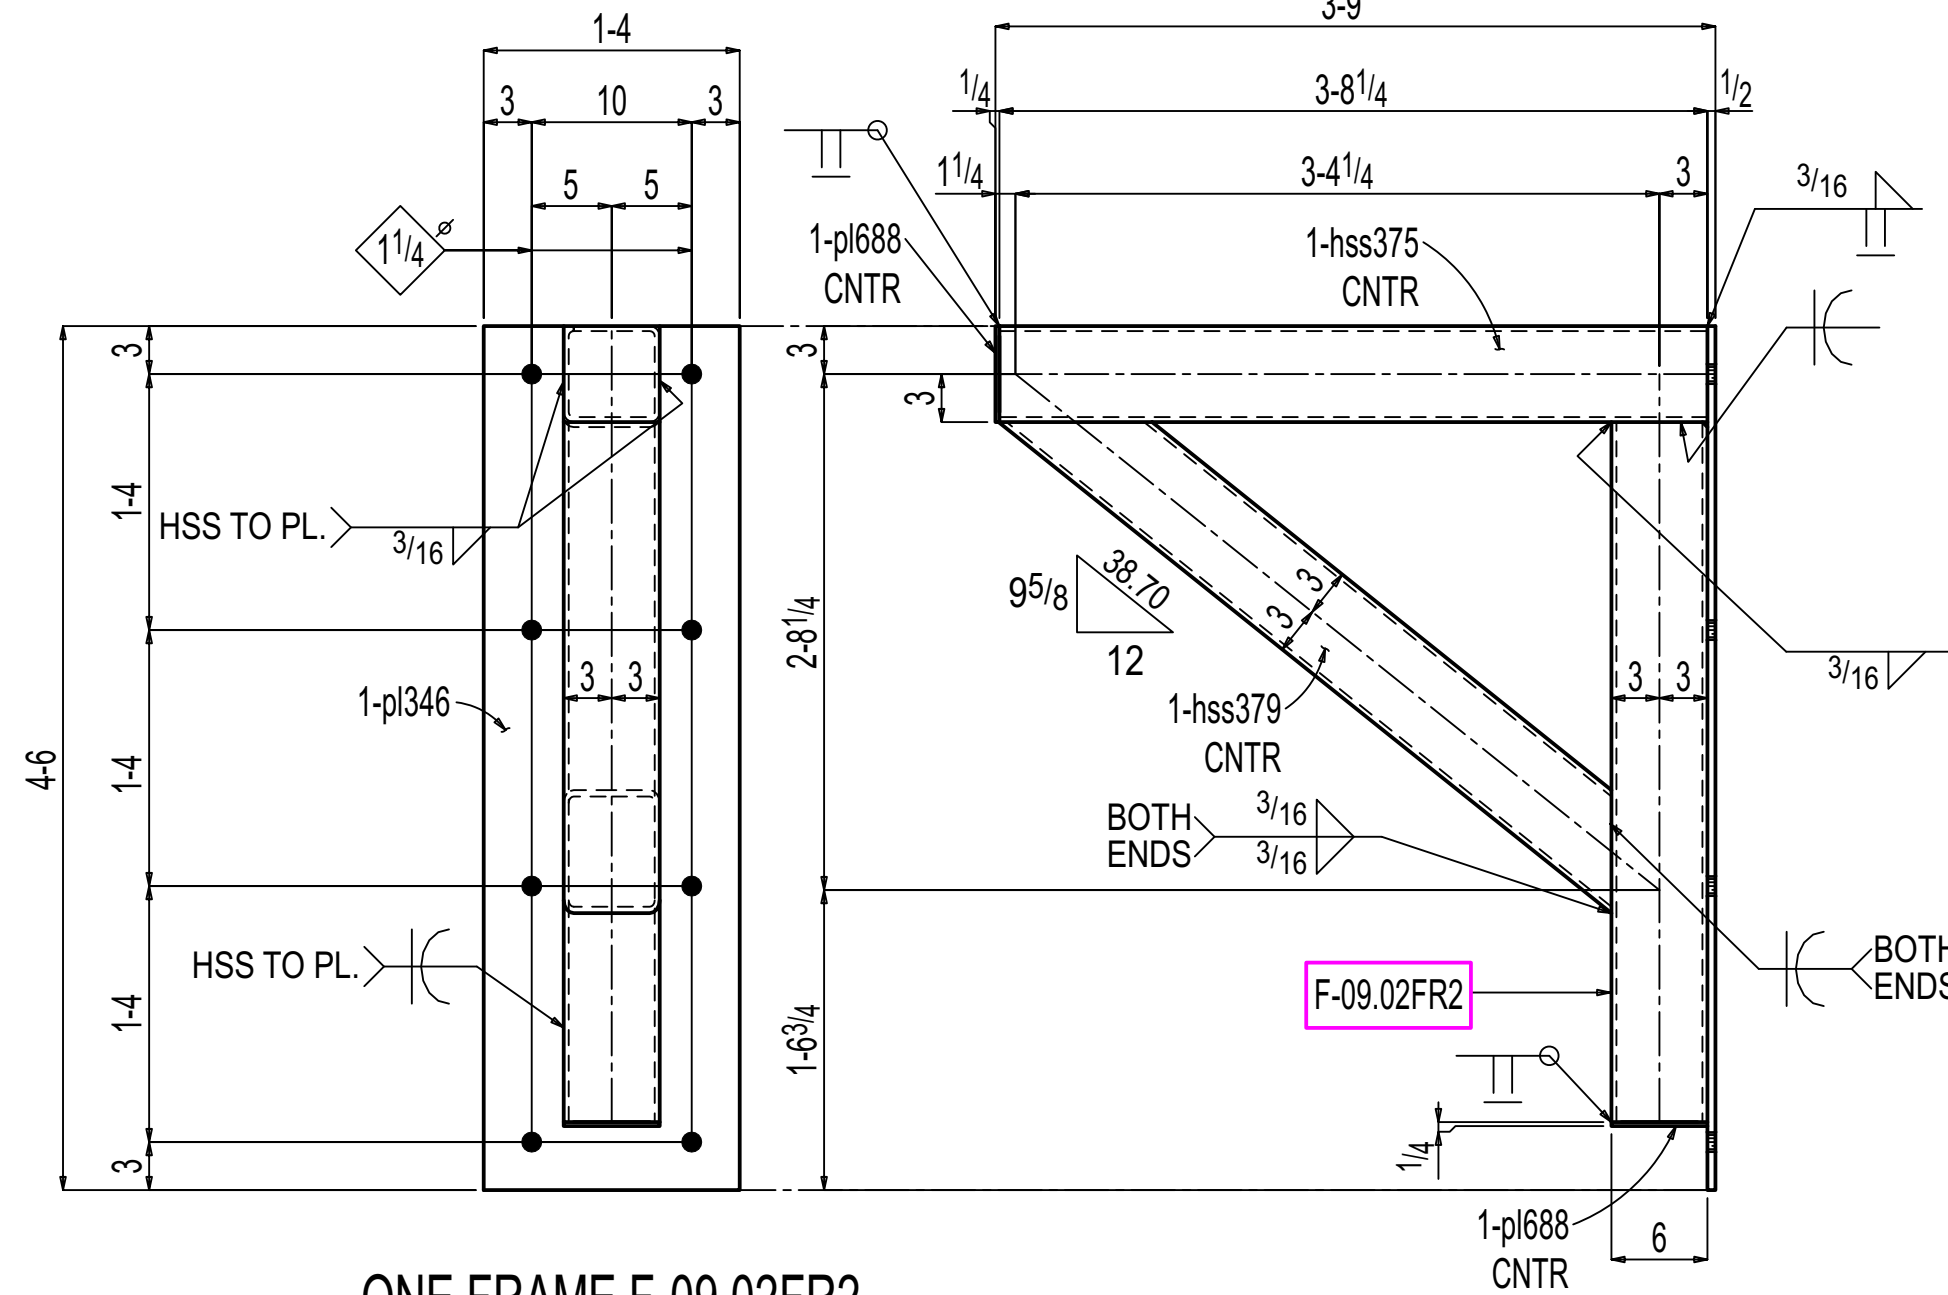


ONE FRAME F-09.02FR2

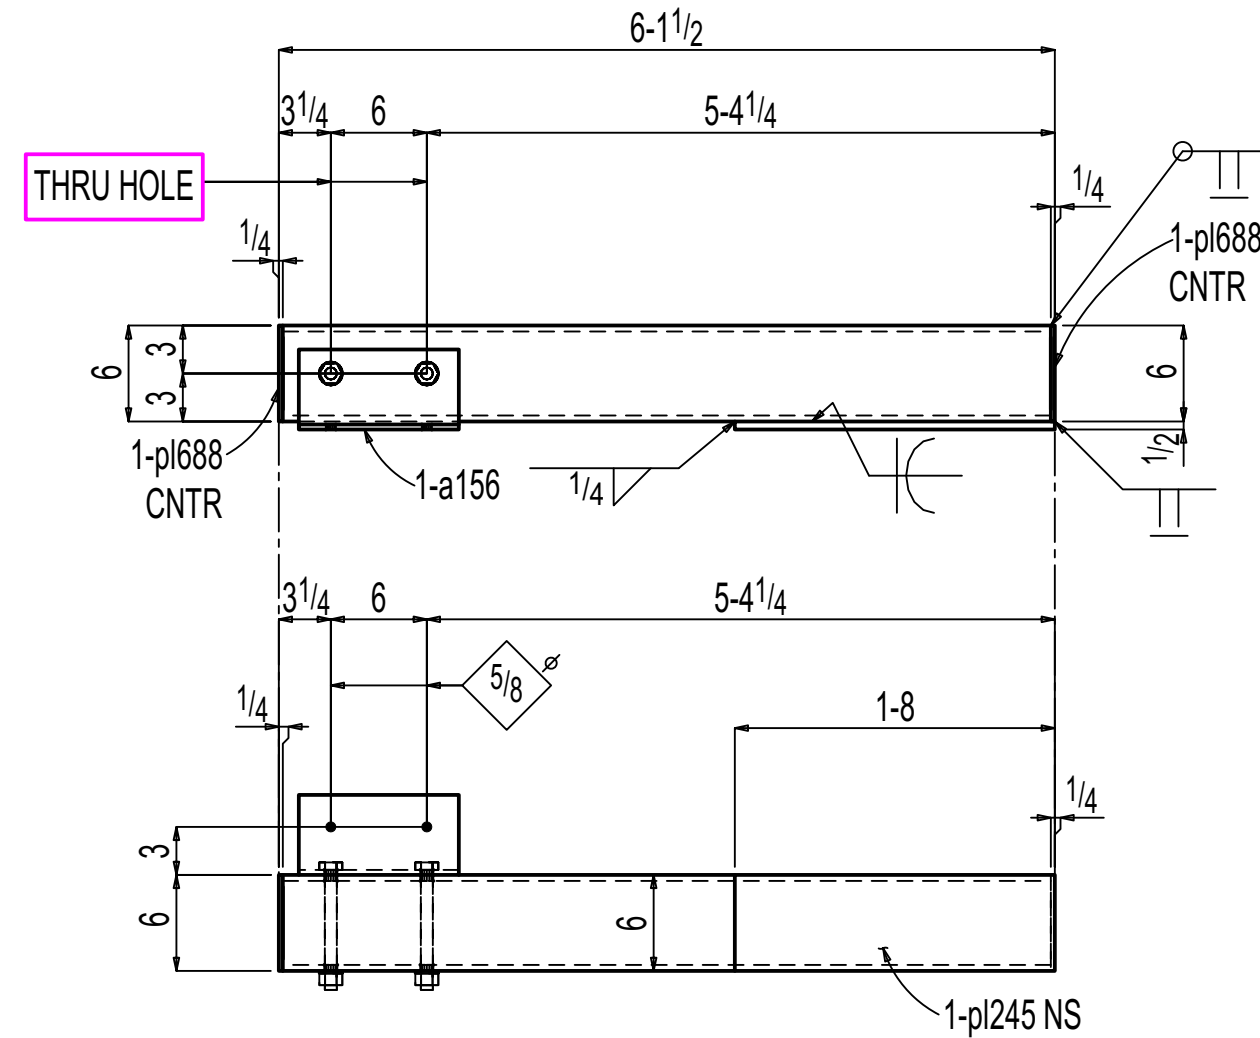

ONE HSS F-09.02M3

SHOP BOLTS:  
2-3/4Diax7 1/2 A325N

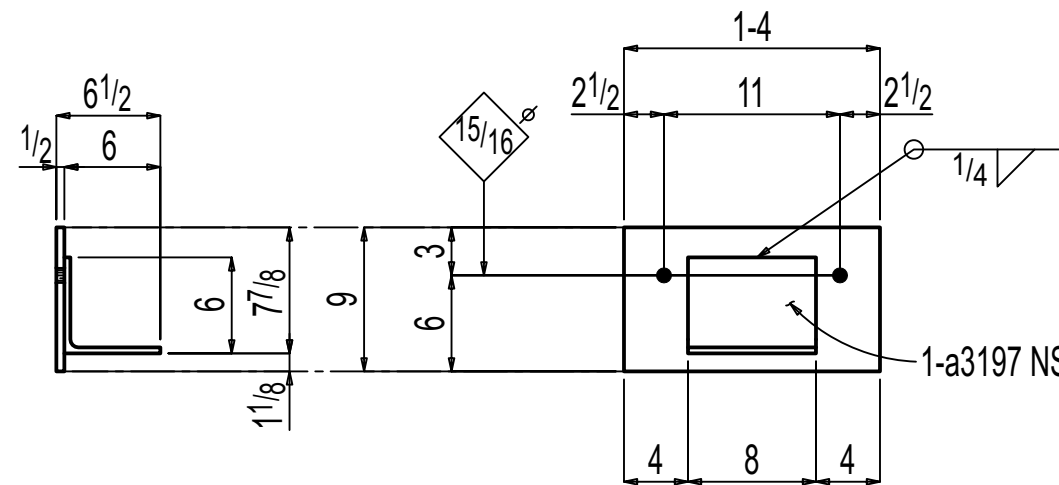

ONE PLATE F-09.02M6

PAINT PREPARATION :NO PAINT  
PREPARATION :SSPC-SP3

| General Notes                                                             |                 |                 |            |
|---------------------------------------------------------------------------|-----------------|-----------------|------------|
| *Structural steel shall conform to ASTM-A992.                             |                 |                 |            |
| *Structural SQR/RND,tubing conform to ASTM A500 Grade C                   |                 |                 |            |
| *Pipe shall conform to ASTM A53, Grade B.                                 |                 |                 |            |
| *Channels, Angles and plates shall conform to A36.                        |                 |                 |            |
| *All bolts shall be 3/4" High strength in accordance with ASTM A325 (UNO) |                 |                 |            |
| *Welding Electrodes for Carbon steel :E70xx                               |                 |                 |            |
| 5                                                                         | 0               | For Fabrication | 11-14-2025 |
| 4                                                                         | D               | For Re-Approval | 10-24-2025 |
| 3                                                                         | C               | For Re-Approval | 09-19-2025 |
| 2                                                                         | B               | For Re-Approval | 06-23-2025 |
| 1                                                                         | A               | For Approval    | 02-25-2025 |
| # of Copies                                                               | Revision/ Issue | Destination     | Date       |

IRON FABRICATION SERVICES, LLC.

3029 M. Street, NW, Suite 202  
Washington, DC 20007  
Tel: 202-800-5599  
Fax: 202-478-0303

Project Name and Address  
**MARYLAND AVENUE**  
Location: **1250 MARYLAND AVENUE SW**  
**WASHINGTON, DC 20024**

Contractor:  
**BALFOUR BEATTY**


Approved for Fabrication by: Signature

|                |                                    |                |                                         |
|----------------|------------------------------------|----------------|-----------------------------------------|
| Contract #     | <b>224009</b>                      | Drawing #      | <b>F-09.02</b>                          |
| Contract Item: | <b>FRAME</b>                       |                |                                         |
| Ref:           | <b>SOW - 09: E-09.00 - E-09.02</b> |                |                                         |
| Date           | <b>01/ 23/ 2025</b>                | Drawing Title: | <b>FRAME &amp; MISCELLANEOUS DETAIL</b> |
| Scale          | <b>VARIES</b>                      |                |                                         |




| BILL OF MATERIAL |     |           |                                                                |                                                   |                                  |                                            |                             |
|------------------|-----|-----------|----------------------------------------------------------------|---------------------------------------------------|----------------------------------|--------------------------------------------|-----------------------------|
| LINE #           | QTY | PC        | MARK                                                           | DESCRIPTION                                       | LENGTH                           | REMARKS                                    | WEIGHT TOTAL ADVANCE MILL # |
|                  | ONE | F-09.03C1 |                                                                | COLUMN                                            |                                  |                                            | 329                         |
|                  | 1   | F-09.03C1 | HSS6x6x <sup>3</sup> / <sub>8</sub>                            |                                                   | 10 4                             | A500C                                      | 284                         |
|                  | 1   | p11965    | PL1 <sup>1</sup> / <sub>2</sub> x7                             |                                                   | 1 6                              | A36                                        | 45                          |
|                  |     |           |                                                                | FIELD BOLTS                                       |                                  |                                            |                             |
|                  | 2   |           |                                                                | <sup>3</sup> / <sub>4</sub> Dia HILTI HAS V-36    | 0 8                              | ( <sup>3</sup> / <sub>4</sub> " EMBEDMENT) |                             |
|                  |     |           |                                                                | w/ HILTI HIT HY-200 EPOXY                         |                                  |                                            |                             |
|                  | ONE | F-09.03C2 |                                                                | COLUMN                                            |                                  |                                            | 313                         |
|                  | 1   | F-09.03C2 | HSS6x6x <sup>3</sup> / <sub>8</sub>                            |                                                   | 9 10 <sup>3</sup> / <sub>4</sub> | A500C                                      | 272                         |
|                  | 2   | p13368    | PL <sup>3</sup> / <sub>8</sub> x6 <sup>1</sup> / <sub>2</sub>  |                                                   | 1 6                              | A36                                        | 41                          |
|                  |     |           |                                                                | FIELD BOLTS                                       |                                  |                                            |                             |
|                  | 2   |           |                                                                | <sup>3</sup> / <sub>4</sub> Dia HILTI Kwik HUS-EZ | 0 4 <sup>1</sup> / <sub>2</sub>  | ( <sup>2</sup> / <sub>3</sub> " EMBEDMENT) |                             |
|                  |     |           |                                                                | SCREW ANCHOR                                      |                                  |                                            |                             |
|                  | ONE | F-09.03B1 |                                                                | BEAM                                              |                                  |                                            | 716                         |
|                  | 1   | F-09.03B1 | HSS10x8x <sup>1</sup> / <sub>4</sub>                           |                                                   | 18 9 <sup>1</sup> / <sub>8</sub> | A500C                                      | 548                         |
|                  | 1   | bp1122    | PL <sup>1</sup> / <sub>4</sub> x9 <sup>1</sup> / <sub>2</sub>  |                                                   | 10 0                             | BENT A36                                   | 81                          |
|                  | 1   | bp1123    | PL <sup>1</sup> / <sub>4</sub> x9 <sup>1</sup> / <sub>2</sub>  |                                                   | 8 10 <sup>3</sup> / <sub>4</sub> | BENT A36                                   | 72                          |
|                  | 2   | p13418    | PL <sup>1</sup> / <sub>4</sub> x8                              |                                                   | 0 10                             | A36                                        | 11                          |
|                  | 1   | p13489    | PL <sup>1</sup> / <sub>4</sub> x4                              |                                                   | 1 1                              | A36                                        | 4                           |
|                  | ONE | F-09.03B2 |                                                                | BEAM                                              |                                  |                                            | 863                         |
|                  | 1   | F-09.03B2 | HSS10x8x <sup>3</sup> / <sub>16</sub>                          |                                                   | 19 4 <sup>7</sup> / <sub>8</sub> | A500C                                      | 701                         |
|                  | 2   | p13526    | PL <sup>1</sup> / <sub>4</sub> x8                              |                                                   | 0 10                             | A36                                        | 11                          |
|                  | 1   | fb25      | FL <sup>1</sup> / <sub>4</sub> x9 <sup>3</sup> / <sub>16</sub> |                                                   | 7 11 <sup>3</sup> / <sub>4</sub> | A36                                        | 35                          |
|                  | 1   | fb37      | FL <sup>1</sup> / <sub>4</sub> x9 <sup>3</sup> / <sub>16</sub> |                                                   | 3 4 <sup>1</sup> / <sub>4</sub>  | A36                                        | 17                          |
|                  | 1   | fb26      | FL <sup>1</sup> / <sub>4</sub> x9 <sup>3</sup> / <sub>16</sub> |                                                   | 8 0                              | A36                                        | 28                          |
|                  | 1   | p13532    | PL <sup>1</sup> / <sub>4</sub> x4                              |                                                   | 1 4 <sup>1</sup> / <sub>8</sub>  | A36                                        | 5                           |
|                  | 1   | p1443     | PL <sup>1</sup> / <sub>4</sub> x4                              |                                                   | 1 3 <sup>3</sup> / <sub>4</sub>  | A36                                        | 4                           |
|                  | 1   | fb143     | FL <sup>1</sup> / <sub>4</sub> x9 <sup>3</sup> / <sub>16</sub> |                                                   | 8 0                              | A36                                        | 26                          |
|                  | 1   | fb154     | FL <sup>1</sup> / <sub>4</sub> x9 <sup>3</sup> / <sub>16</sub> |                                                   | 7 11 <sup>3</sup> / <sub>8</sub> | A36                                        | 25                          |
|                  | 1   | fb15      | FL <sup>1</sup> / <sub>4</sub> x9 <sup>3</sup> / <sub>16</sub> |                                                   | 3 3 <sup>5</sup> / <sub>16</sub> | A36                                        | 11                          |

Total weight : 2221

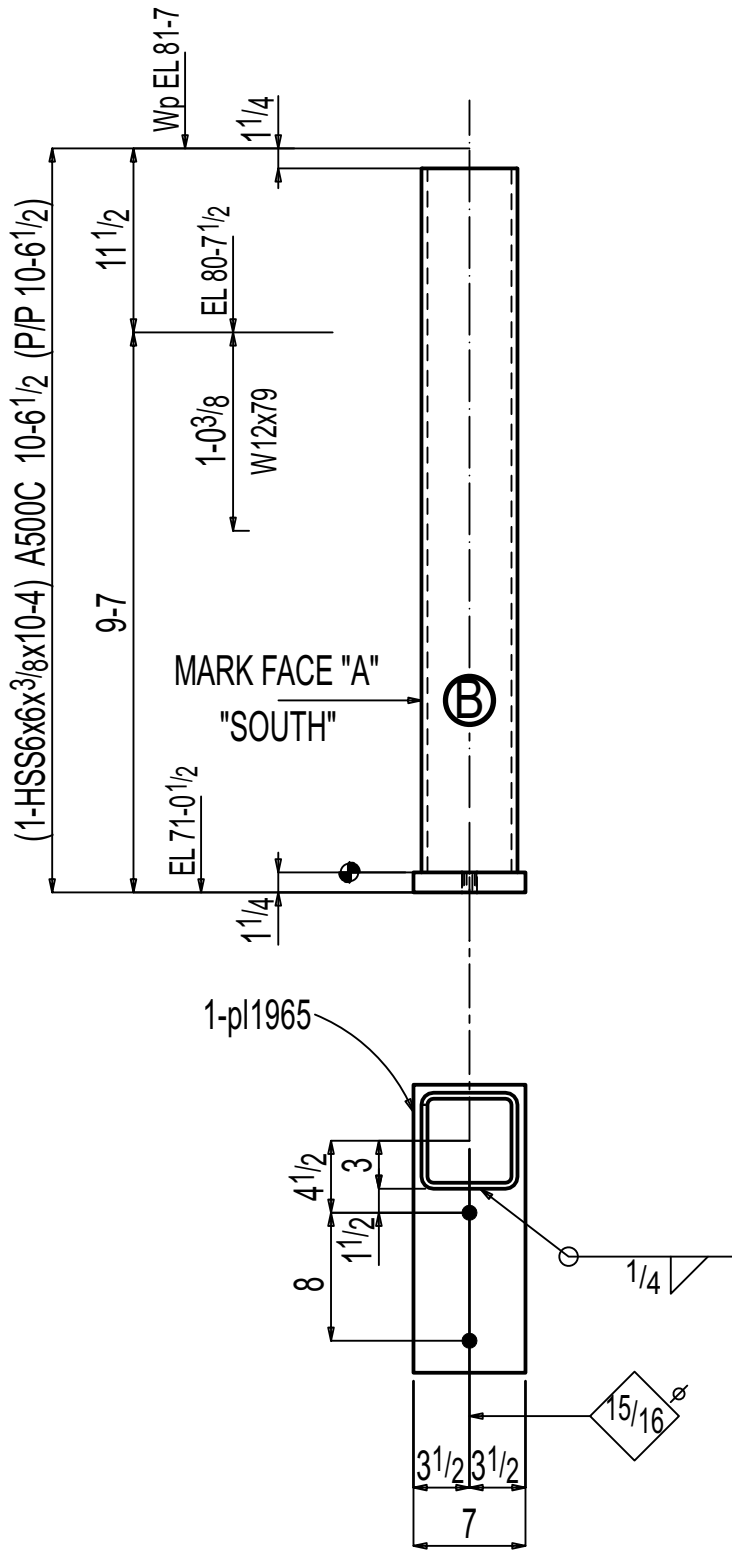


ONE COLUMN F-09.03C1

AT GRID:  
EE & A

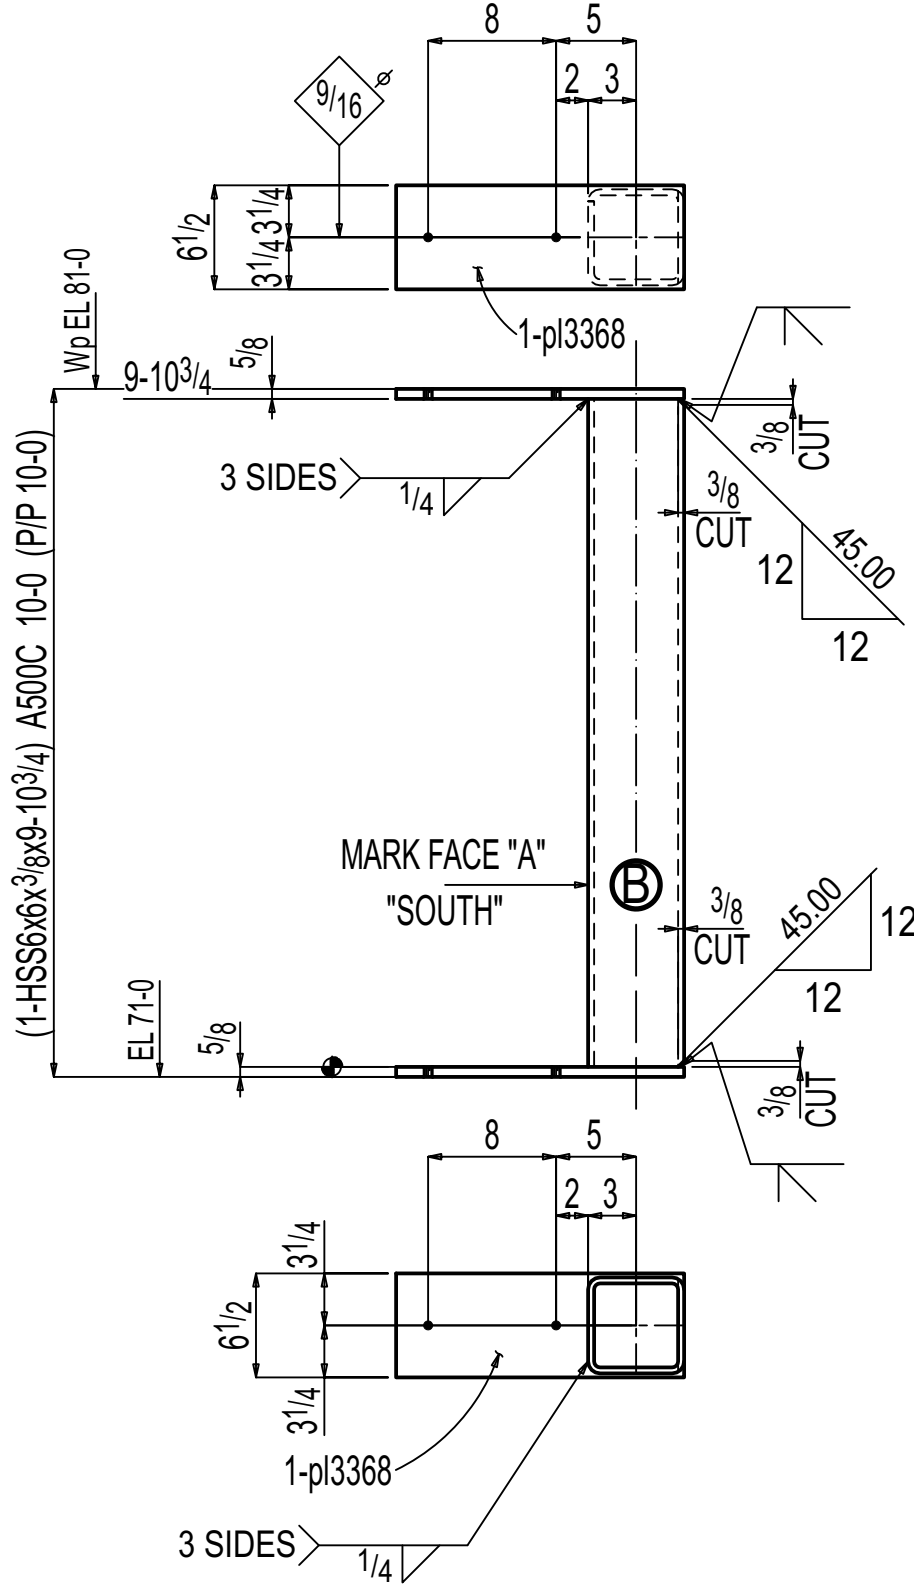


ONE COLUMN F-09.03C2


AT GRID:  
AA & K

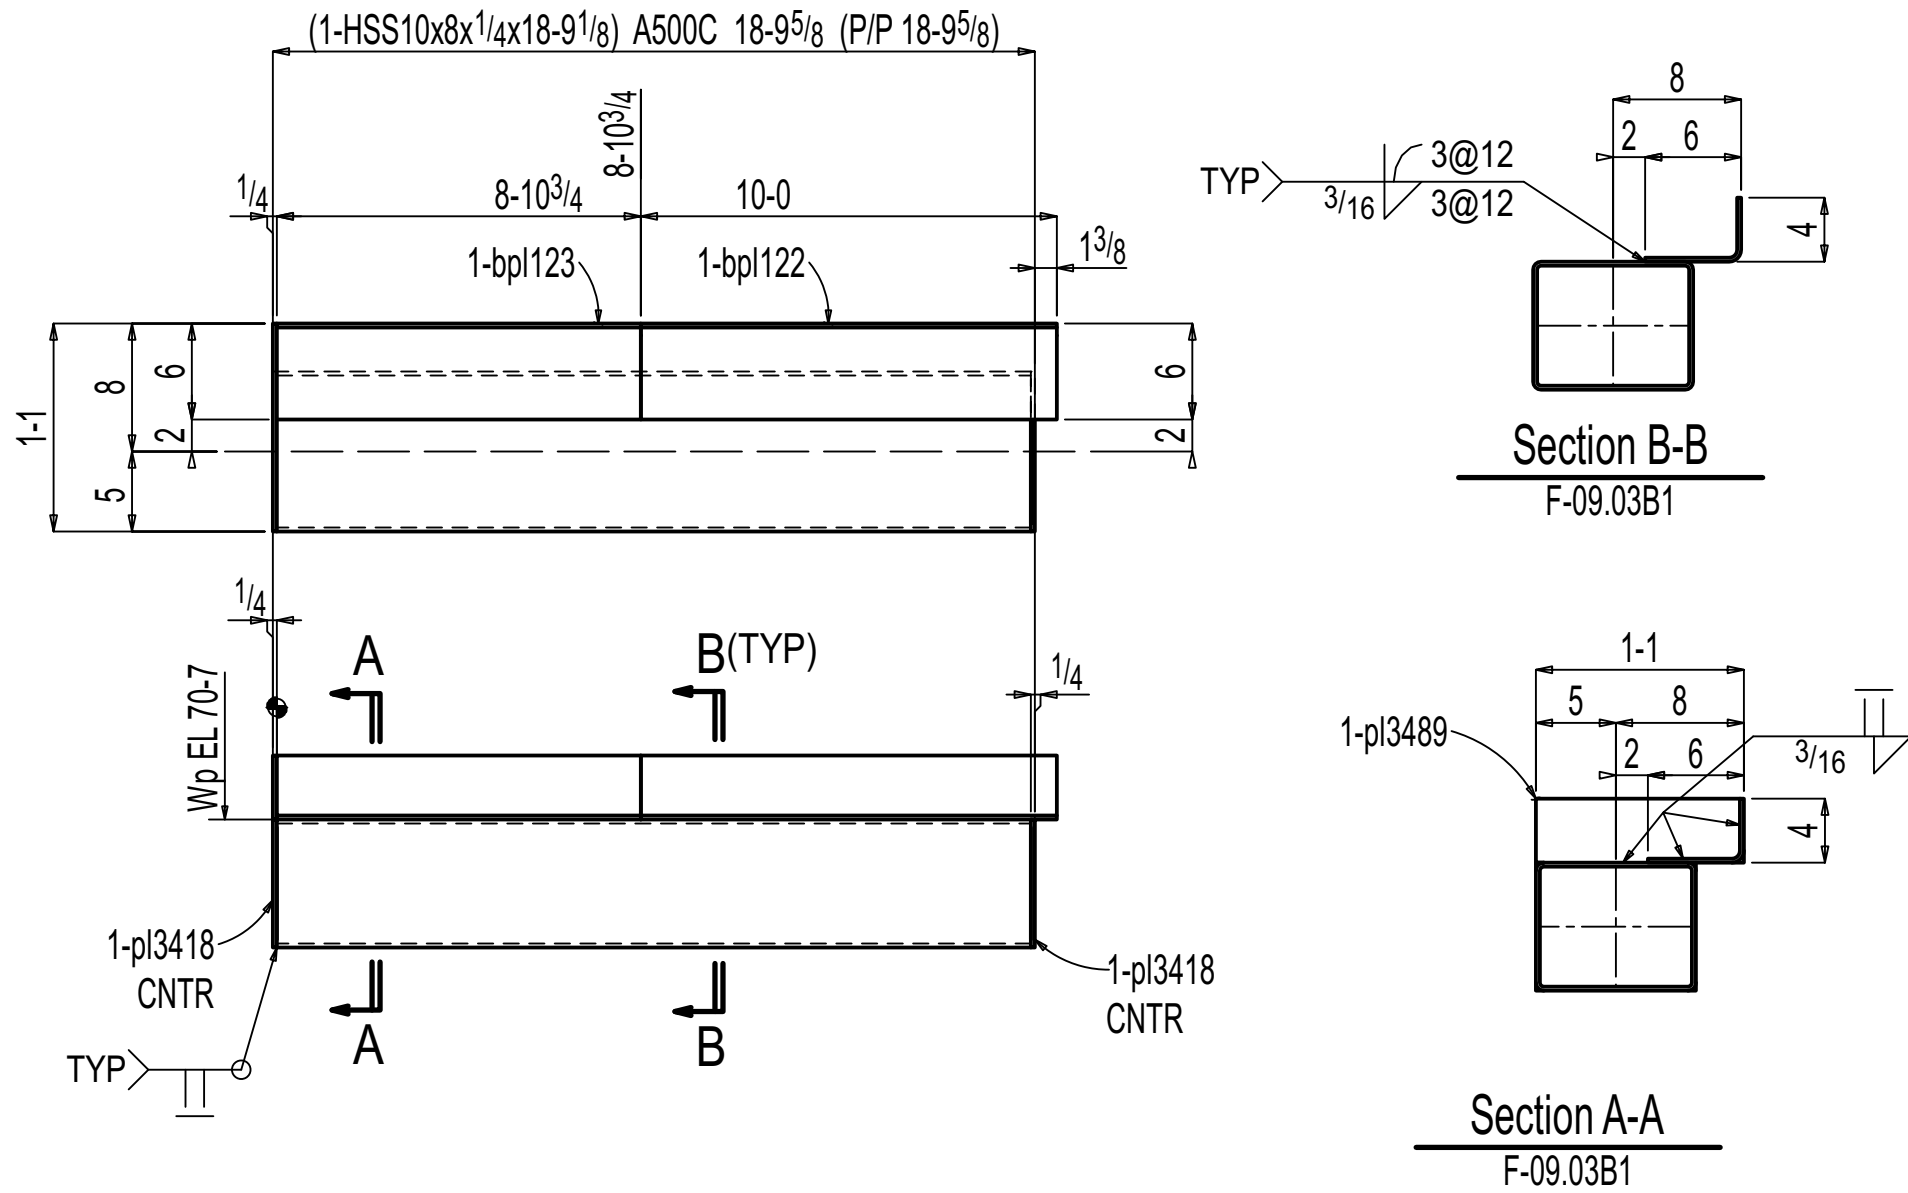

ONE BEAM F-09.03B1

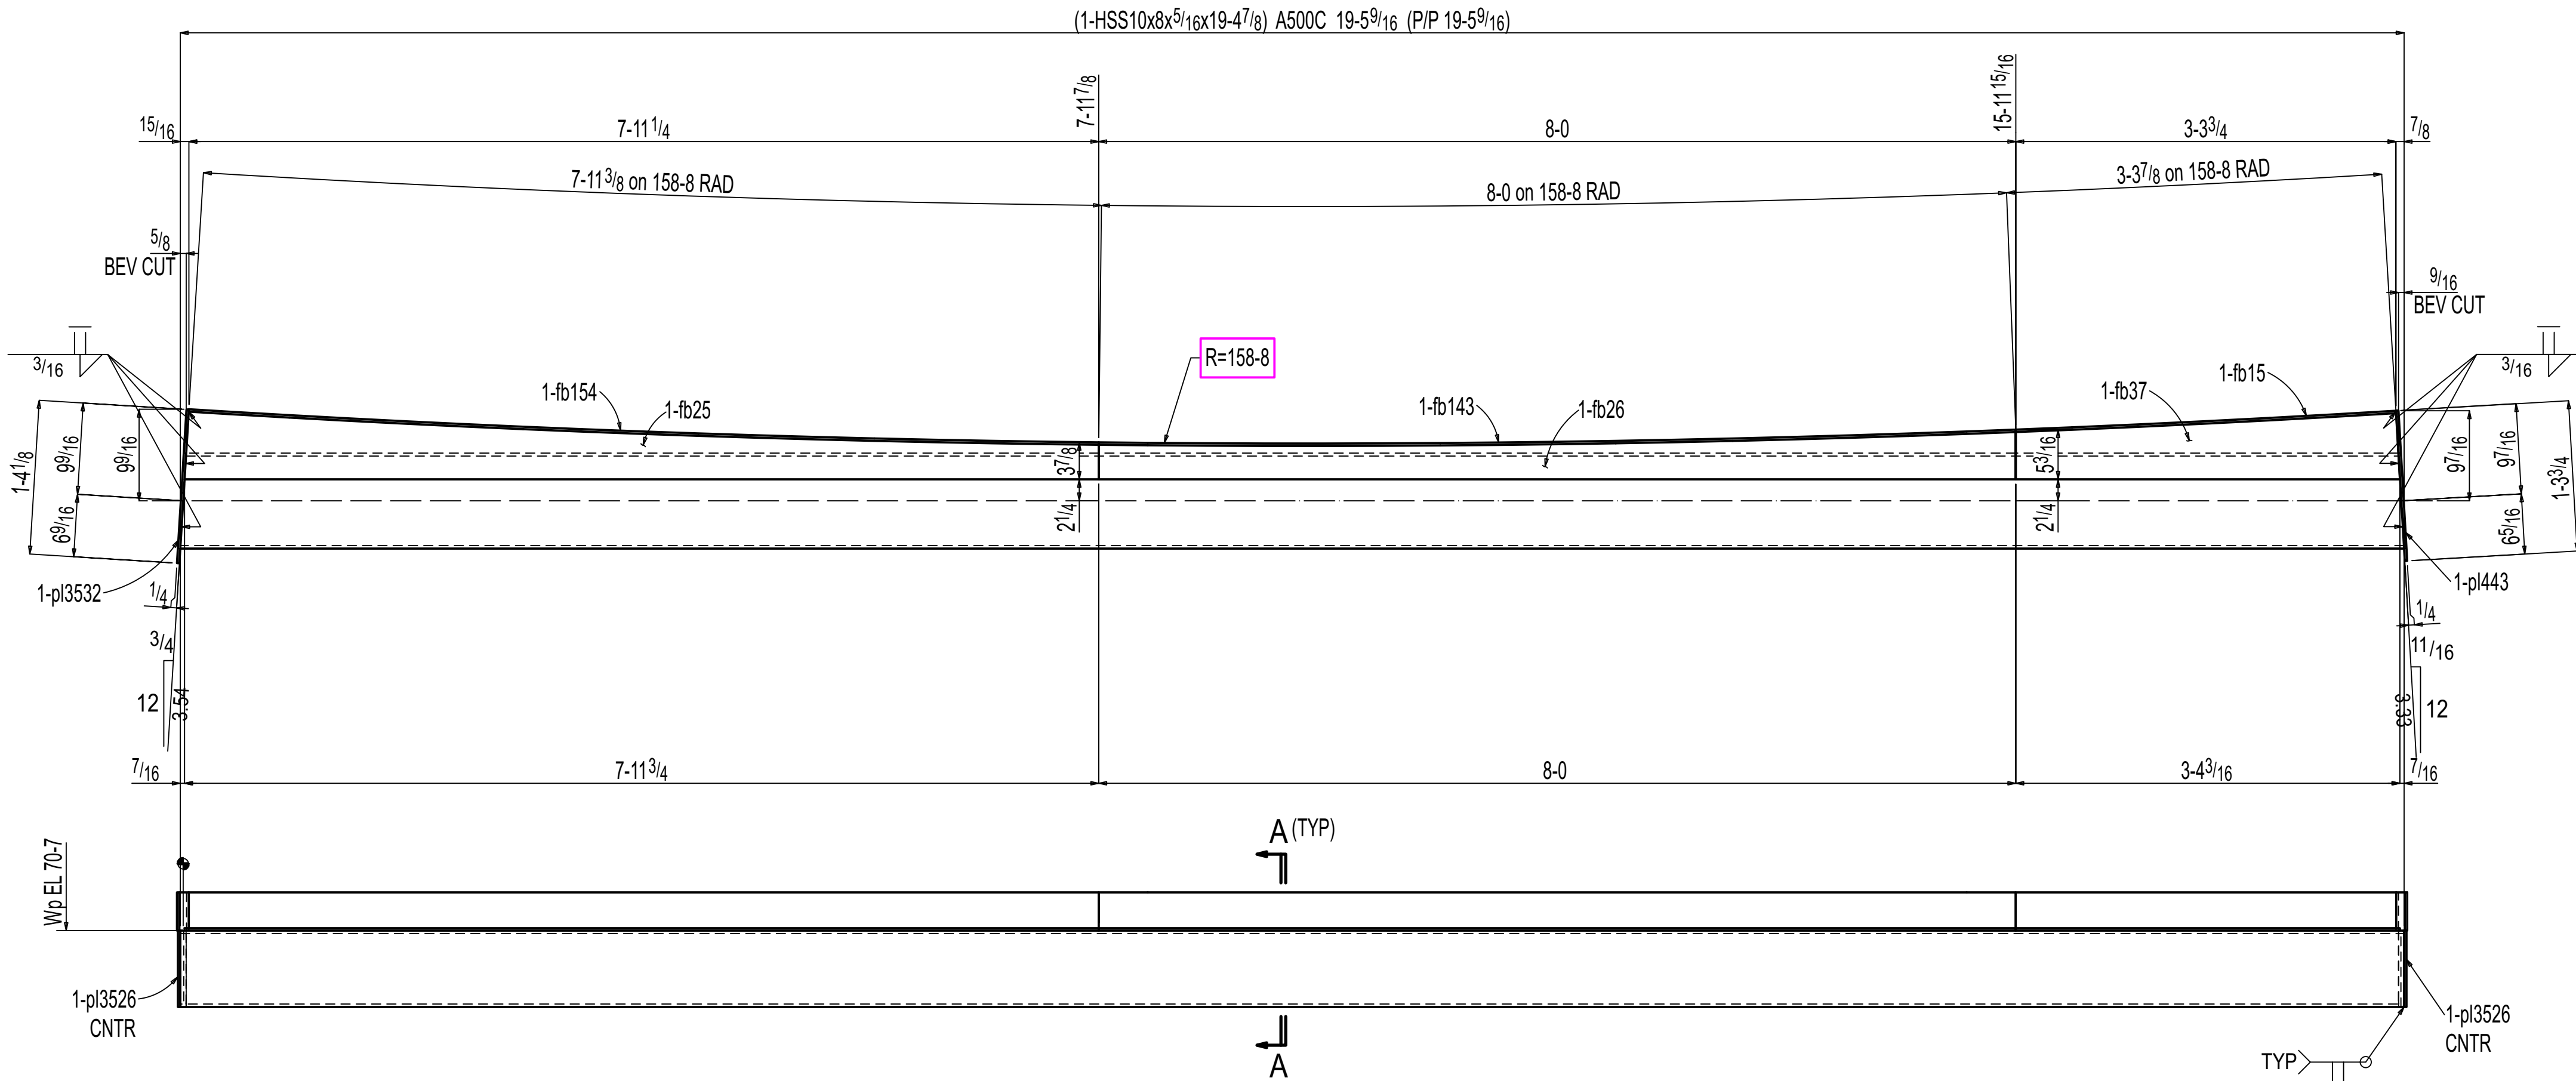

ONE BEAM F-09.03B2

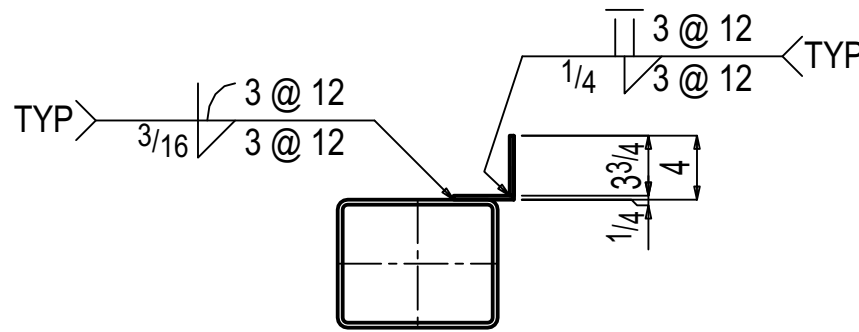

Section A-A  
F-09.03B2

PAINT :NO PAINT  
PREPARATION :SSPC-SP3

| General Notes                                                                                      |                 |                 |            |
|---|-----------------|-----------------|------------|
| *Structural steel shall conform to ASTM-A992.                                                      |                 |                 |            |
| *Structural SQR/RND,tubing conform to ASTM A500 Grade C                                            |                 |                 |            |
| *Pipe shall conform to ASTM A53, Grade B.                                                          |                 |                 |            |
| *Channels, Angles and plates shall conform to A36.                                                 |                 |                 |            |
| *All bolts shall be <sup>3</sup> / <sub>4</sub> " High strength in accordance with ASTM A325 (UNO) |                 |                 |            |
| *Welding Electrodes for Carbon steel :E70xx                                                        |                 |                 |            |
| 5                                                                                                  | 0               | For Fabrication | 11-14-2025 |
| 4                                                                                                  | D               | For Re-Approval | 10-24-2025 |
| 3                                                                                                  | C               | For Re-Approval | 09-19-2025 |
| 2                                                                                                  | B               | For Re-Approval | 06-23-2025 |
| 1                                                                                                  | A               | For Approval    | 02-25-2025 |
| # of Copies                                                                                        | Revision/ Issue | Destination     | Date       |

IRON FABRICATION SERVICES, LLC.

3029 M. Street, NW, Suite 202  
Washington, DC 20007  
Tel: 202-800-5599  
Fax: 202-478-0303

Project Name and Address  
**MARYLAND AVENUE**

Location: **1250 MARYLAND AVENUE SW  
WASHINGTON, DC 20024**

Contractor:  
**BALFOUR BEATTY**

Approved for Fabrication by: Signature

Contract # **224009** Drawing # **F-09.03**

Contract Item: **BEAM**










Ref:  
**SOW - 09: E-09.00 - E-09.02**

Date **01/ 23/ 2025** Drawing Title: **BEAM & COLUMN DETAIL**  
Scale **VARIES**



| BILL OF MATERIAL |           |                        |      |             |                    |          |         |
|------------------|-----------|------------------------|------|-------------|--------------------|----------|---------|
| LINE #           | QTY       | PC                     | MARK | DESCRIPTION | LENGTH             | REMARKS  | ADVANCE |
|                  | TOTAL     |                        |      |             |                    |          | MILL #  |
| ONE              | F-09.04B1 | BEAM                   |      |             |                    |          | 969     |
| 1                | F-09.04B1 | HSS8x6x1/2             |      |             | 22 10 1/2          | A500C    | 962     |
| 2                | pl1459    | PL 1/4x6               |      |             | 0 8                | A36      | 7       |
| ONE              | F-09.04B2 | BEAM                   |      |             |                    |          | 521     |
| 1                | F-09.04B2 | HSS6x6x1/2             |      |             | 14 7 3/4           | A500C    | 516     |
| 2                | pl688     | PL 1/4x6               |      |             | 0 6                | A36      | 5       |
| ONE              | F-09.04B3 | BEAM                   |      |             |                    |          | 899     |
| 1                | F-09.04B3 | HSS8x8x1/4             |      |             | 28 13 1/8          | A500C    | 726     |
| 2                | pl3696    | PL 1/4x8               |      |             | 0 8                | A36      | 9       |
| 3                | bp1982    | PL 1/4x6 9/16          |      |             | 8 0                | BENT A36 | 134     |
| 1                | bp1121    | PL 1/4x6 9/16          |      |             | 4 13/8             | BENT A36 | 23      |
| 2                | pl3489    | PL 1/4x4               |      |             | 1 1                | A36      | 7       |
| ONE              | F-09.04A1 | ANGLE                  |      |             |                    |          | 126     |
| 1                | F-09.04A1 | L4x4x3/16              |      |             | 15 5               | A36      | 126     |
| 16               |           | FIELD BOLTS            |      |             |                    |          |         |
|                  |           | 1/2 Dia HILTI HAS V-36 |      |             | 0 4 1/2            |          |         |
|                  |           | w/ HILTI HIT HY-200 V3 |      |             | (2 3/4" EMBEDMENT) |          |         |
|                  |           | ADHESIVE               |      |             |                    |          |         |
| ONE              | F-09.04A2 | ANGLE                  |      |             |                    |          | 30      |
| 1                | F-09.04A2 | L4x4x3/16              |      |             | 3 6                | A36      | 29      |
| 1                | pl3484    | PL 1/4x3 11/16         |      |             | 0 3 11/16          | A36      | 1       |
| 4                |           | FIELD BOLTS            |      |             |                    |          |         |
|                  |           | 1/2 Dia HILTI HAS V-36 |      |             | 0 4 1/2            |          |         |
|                  |           | w/ HILTI HIT HY-200 V3 |      |             | (2 3/4" EMBEDMENT) |          |         |
|                  |           | ADHESIVE               |      |             |                    |          |         |
| ONE              | F-09.04A3 | ANGLE                  |      |             |                    |          | 160     |
| 1                | F-09.04A3 | L4x4x3/16              |      |             | 19 6 1/4           | A36      | 160     |
| 29               |           | FIELD BOLTS            |      |             |                    |          |         |
|                  |           | 1/2 Dia HILTI HAS V-36 |      |             | 0 4 1/2            |          |         |
|                  |           | w/ HILTI HIT HY-200 V3 |      |             | (2 3/4" EMBEDMENT) |          |         |
|                  |           | ADHESIVE               |      |             |                    |          |         |
| ONE              | F-09.04A5 | ANGLE                  |      |             |                    |          | 110     |
| 1                | F-09.04A5 | L4x4x3/16              |      |             | 13 2 7/8           | A36      | 109     |
| 1                | pl485     | PL 1/4x3 11/16         |      |             | 0 3 11/16          | A36      | 1       |
| 14               |           | FIELD BOLTS            |      |             |                    |          |         |
|                  |           | 1/2 Dia HILTI HAS V-36 |      |             | 0 4 1/2            |          |         |
|                  |           | w/ HILTI HIT HY-200 V3 |      |             | (2 3/4" EMBEDMENT) |          |         |
|                  |           | ADHESIVE               |      |             |                    |          |         |
| ONE              | F-09.04A6 | ANGLE                  |      |             |                    |          | 123     |
| 1                | F-09.04A6 | L4x4x3/16              |      |             | 14 11              | A36      | 122     |
| 1                | pl485     | PL 1/4x3 11/16         |      |             | 0 3 11/16          | A36      | 1       |
| 15               |           | FIELD BOLTS            |      |             |                    |          |         |
|                  |           | 1/2 Dia HILTI HAS V-36 |      |             | 0 4 1/2            |          |         |
|                  |           | w/ HILTI HIT HY-200 V3 |      |             | (2 3/4" EMBEDMENT) |          |         |
|                  |           | ADHESIVE               |      |             |                    |          |         |

Total weight : 2938

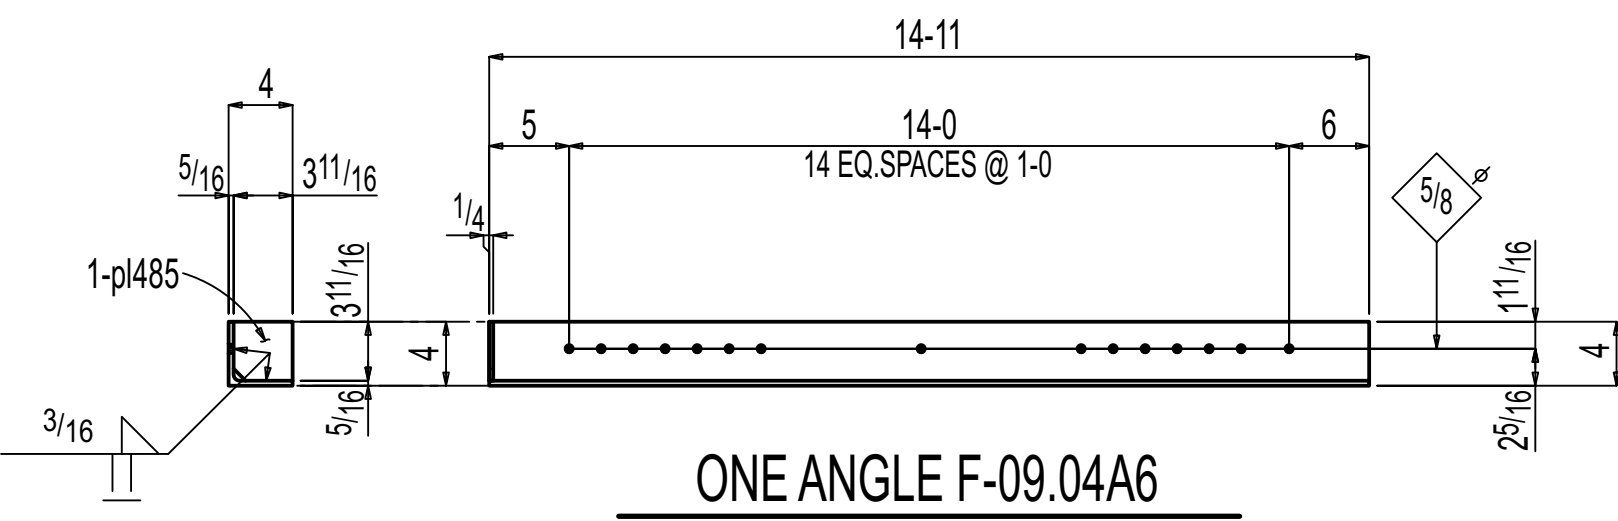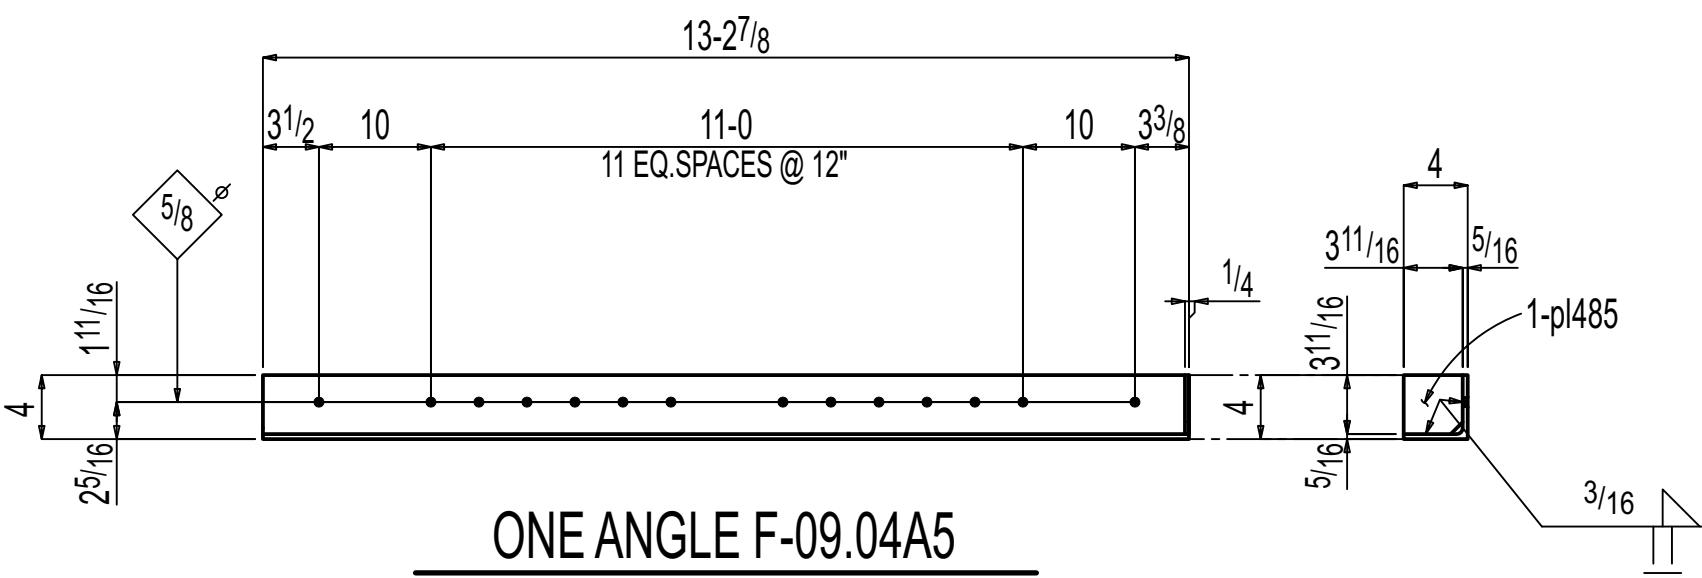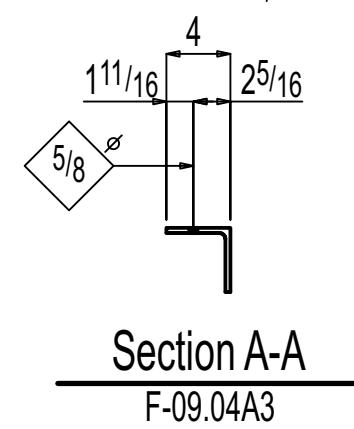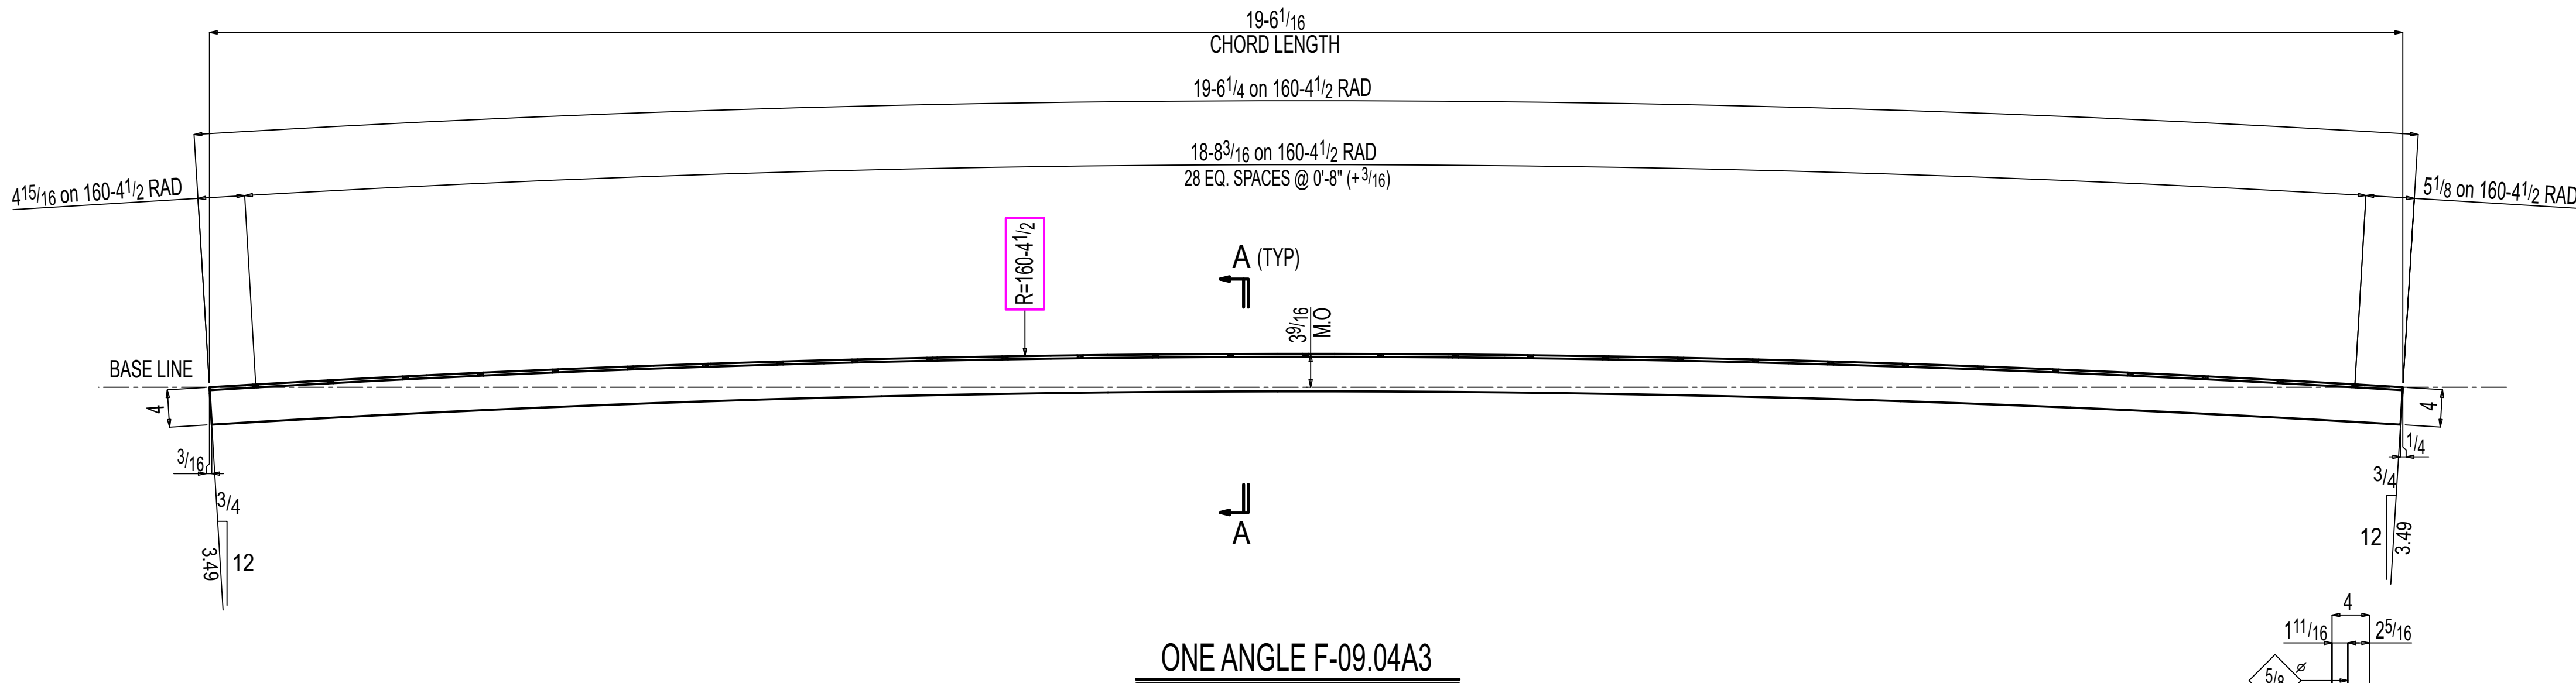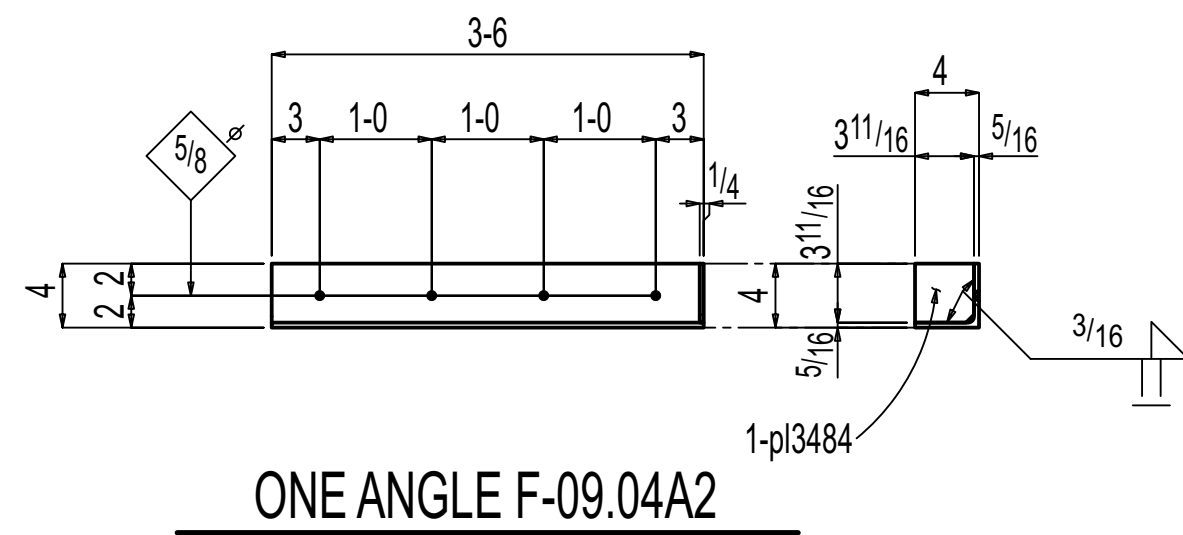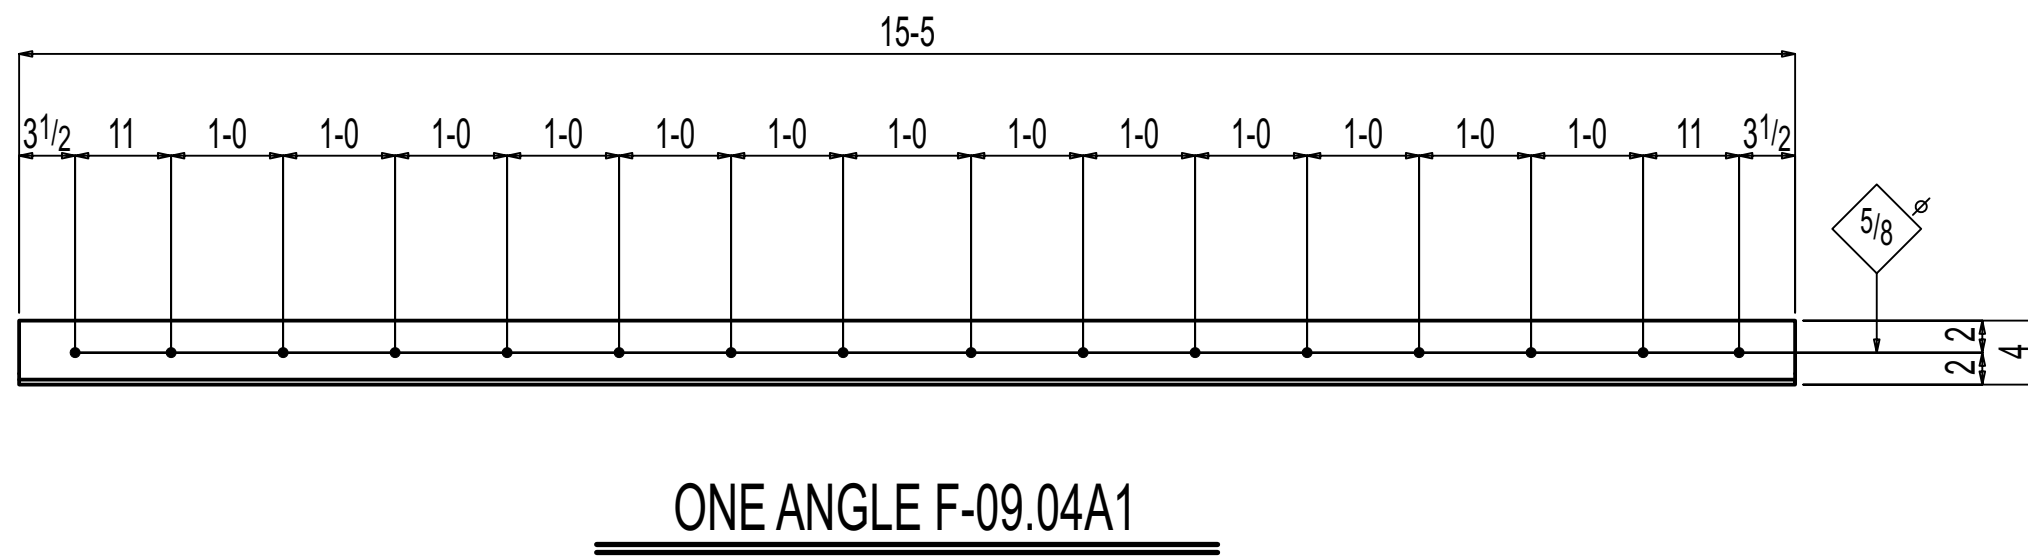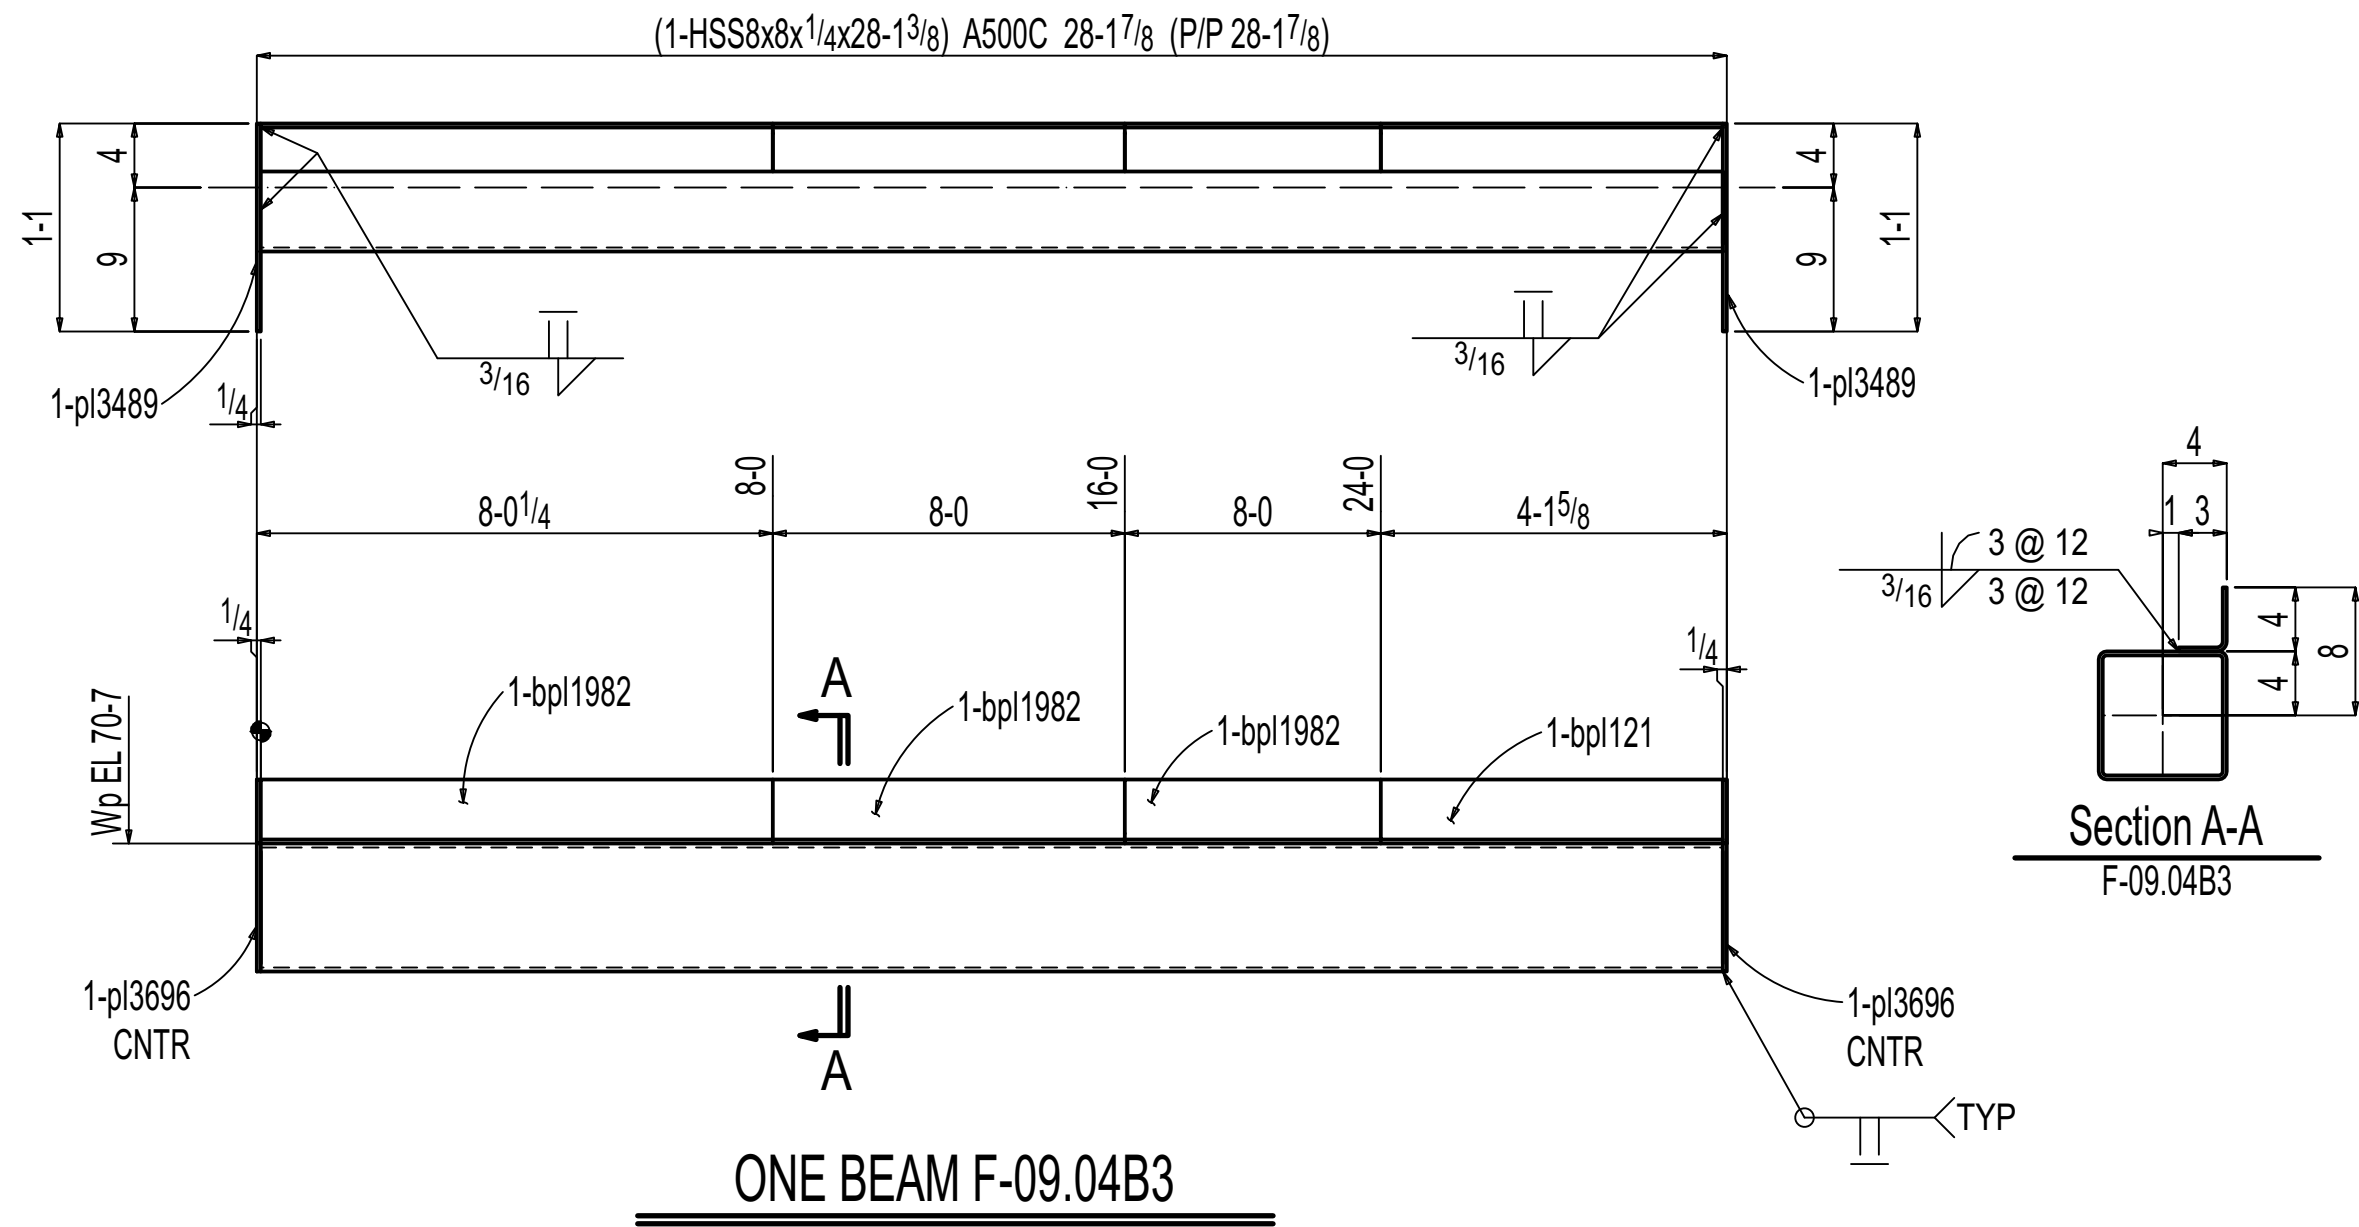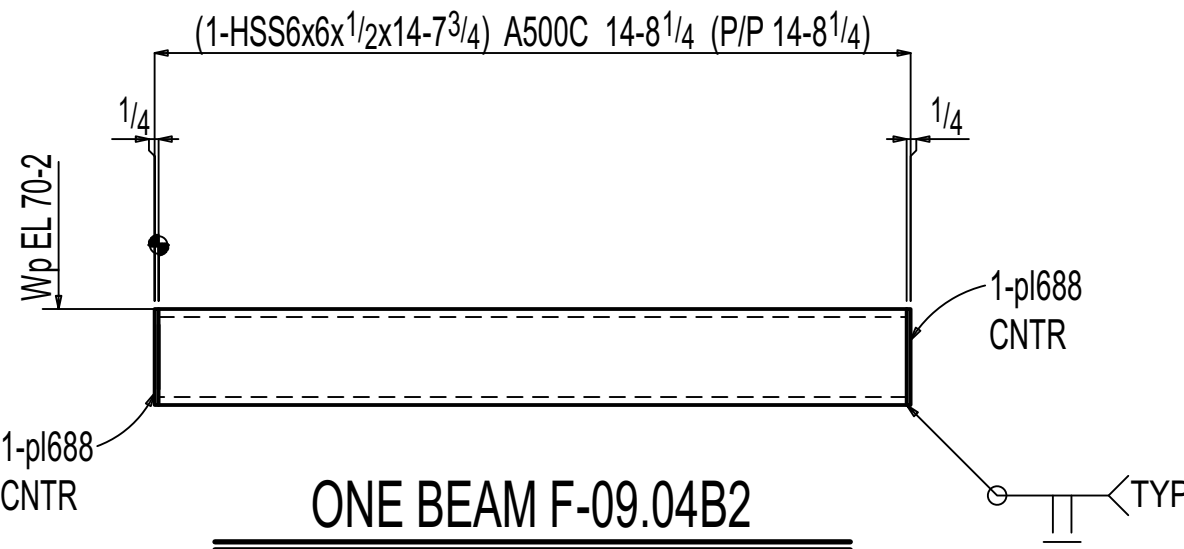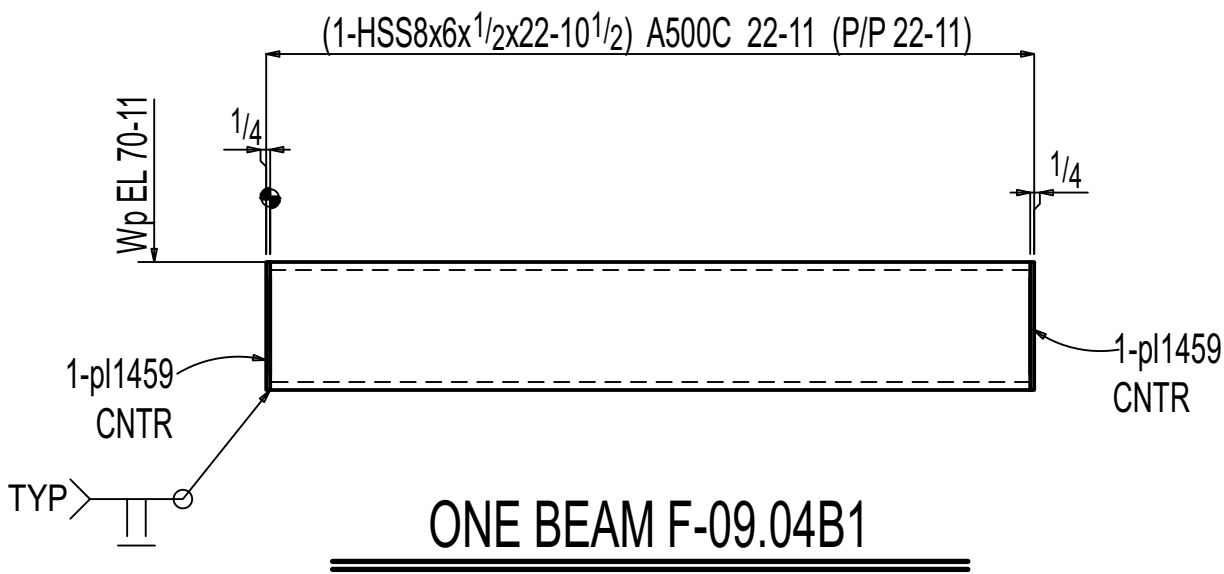

PAINT :NO PAINT  
PREPARATION :SSPC-SP3

| General Notes                                                             |                 |                 |            |
|---------------------------------------------------------------------------|-----------------|-----------------|------------|
| *Structural steel shall conform to ASTM-A992.                             |                 |                 |            |
| *Structural SQR/RND,tubing conform to ASTM A500 Grade C                   |                 |                 |            |
| *Pipe shall conform to ASTM A53, Grade B.                                 |                 |                 |            |
| *Channels, Angles and plates shall conform to A36.                        |                 |                 |            |
| *All bolts shall be 3/4" High strength in accordance with ASTM A325 (UNO) |                 |                 |            |
| *Welding Electrodes for Carbon steel :E70xx                               |                 |                 |            |
| 5                                                                         | 0               | For Fabrication | 11-14-2025 |
| 4                                                                         | D               | For Re-Approval | 10-24-2025 |
| 3                                                                         | C               | For Re-Approval | 09-19-2025 |
| 2                                                                         | B               | Deleted         | 06-23-2025 |
| 1                                                                         | A               | For Approval    | 02-25-2025 |
| # of Copies                                                               | Revision/ Issue | Destination     | Date       |

IRON FABRICATION SERVICES, LLC.

3029 M. Street, NW, Suite 202  
Washington, DC 20007  
Tel: 202-800-5599  
Fax: 202-478-0303

Project Name and Address  
**MARYLAND AVENUE**  
Location: **1250 MARYLAND AVENUE SW  
WASHINGTON, DC 20024**

Contractor:  
**BALFOUR BEATTY**

Approved for Fabrication by: Signature

Contract # **224009** Drawing # **F-09.04**

Contract Item: **BEAM**


Ref:  
**SOW - 09: E-09.00 - E-09.01**

Date **01/23/2025** Drawing Title: **BEAMS & ANGLE DETAIL**  
Scale **VARIES**




| BILL OF MATERIAL |            |                        |      |             |                    |         |         |
|------------------|------------|------------------------|------|-------------|--------------------|---------|---------|
| LINE #           | QTY        | PC                     | MARK | DESCRIPTION | LENGTH             | REMARKS | ADVANCE |
|                  | TOTAL      |                        |      |             | TOTAL              |         | MILL #  |
| ONE              | F-09.05BP1 | BENT PLATE             |      |             |                    |         | 72      |
| 1                | F-09.05BP1 | PL 1/2x2 3/16          |      | 2 0         | BENT A36           |         | 72      |
|                  |            | FIELD BOLTS            |      |             |                    |         |         |
| 3                |            | 3/4 Dia HILTI HAS V-36 |      | 0 8         | (6" EMBEDMENT)     |         |         |
|                  |            | w/ HILTI HIT HY-200    |      |             |                    |         |         |
|                  |            | ADHESIVE               |      |             |                    |         |         |
| ONE              | F-09.05BP2 | BENT PLATE             |      |             |                    |         | 53      |
| 1                | F-09.05BP2 | PL 1/2x1 5/16          |      | 2 0         | BENT A36           |         | 53      |
|                  |            | FIELD BOLTS            |      |             |                    |         |         |
| 3                |            | 3/4 Dia HILTI HAS V-36 |      | 0 8         | (6" EMBEDMENT)     |         |         |
|                  |            | w/ HILTI HIT HY-200    |      |             |                    |         |         |
|                  |            | ADHESIVE               |      |             |                    |         |         |
| 2                | F-09.05M2  | HSS                    |      |             |                    |         | 43      |
| 2                | F-09.05M2  | HSS 3/16x3 1/2x5/16    |      | 1 6 1/2     | A500C              |         | 39      |
| 4                | p218       | PL 1/4x3 1/2           |      | 0 3 1/2     | A36                |         | 3       |
| ONE              | F-09.05M3  | HSS                    |      |             |                    |         | 41      |
| 1                | F-09.05M3  | HSS 6x6x5/16           |      | 1 6 5/8     | A500C              |         | 36      |
| 2                | p688       | PL 1/4x6               |      | 0 6         | A36                |         | 5       |
| 2                | F-09.05M4  | HSS                    |      |             |                    |         | 39      |
| 2                | F-09.05M4  | HSS 5/16x5 1/2x5/16    |      | 0 8 1/2     | A500C              |         | 30      |
| 4                | p690       | PL 1/4x5 1/2           |      | 0 5 1/2     | A36                |         | 9       |
| 3                | F-09.05M5  | PLATE                  |      |             |                    |         | 36      |
| 3                | F-09.05M5  | PL 1/2x8               |      | 0 10 1/2    | A36                |         | 36      |
| 6                | F-09.05M6  | PLATE                  |      |             |                    |         | 41      |
| 6                | F-09.05M6  | PL 1/2x6               |      | 0 8         | A36                |         | 41      |
| 6                | F-09.05M7  | PLATE WASHER           |      |             |                    |         | 8       |
| 6                | F-09.05M7  | PL 1/2x3               |      | 0 3         | A36                |         | 8       |
| 6                | F-09.05M8  | THREADED ROD           |      |             |                    |         | 15      |
| 6                | F-09.05M8  | 1" Ø THREADED ROD      |      | 0 11 1/2    | F1554 GR. 55       |         | 15      |
|                  |            | w/ HILTI HIT HY-200 V3 |      |             | (8" EMBEDMENT)     |         |         |
|                  |            | ADHESIVE               |      |             |                    |         |         |
|                  |            | FIELD BOLTS            |      |             |                    |         |         |
| 6                |            | 1 NUT                  |      |             | HHNT A563          |         |         |
| 120              | F-09.05M9  | THREADED ROD           |      |             |                    |         | 227     |
| 120              | F-09.05M9  | 1" Ø THREADED ROD      |      | 0 8 1/2     | F1554 GR. 55       |         | 227     |
|                  |            | w/ HILTI HIT HY-200 V3 |      |             | (6" EMBEDMENT)     |         |         |
|                  |            | ADHESIVE               |      |             |                    |         |         |
| 120              |            | 1 NUT                  |      |             | HHNT A563          |         |         |
| 120              |            | 1 WASHER               |      |             | HD F436            |         |         |
| 12               | F-09.05M10 | THREADED ROD           |      |             |                    |         | 29      |
| 12               | F-09.05M10 | 1" Ø THREADED ROD      |      | 0 11        | F1554 GR. 55       |         | 29      |
|                  |            | w/ HILTI HIT HY-200 V3 |      |             | (8" EMBEDMENT)     |         |         |
|                  |            | ADHESIVE               |      |             |                    |         |         |
| 12               |            | 1 NUT                  |      |             | HHNT A563          |         |         |
| 12               |            | 1 WASHER               |      |             | HD F436            |         |         |
| 5                | F-09.05M11 | HSS                    |      |             |                    |         | 67      |
| 5                | F-09.05M11 | HSS 3/16x3 1/2x5/16    |      | 0 11        | A500C              |         | 58      |
| 10               | p218       | PL 1/4x3 1/2           |      | 0 3 1/2     | A36                |         | 9       |
| 2                | F-09.05M12 | THREADED ROD           |      |             |                    |         | 1       |
| 2                | F-09.05M12 | 1/2" Ø THREADED ROD    |      | 0 6         | F1554 GR. 55       |         | 1       |
|                  |            | w/HILTI HIT HY-200 V3  |      |             |                    |         |         |
|                  |            | ADHESIVE               |      |             |                    |         |         |
| 2                |            | 1/2 NUT                |      |             | HHNT A563          |         |         |
| 2                |            | 1/2 WASHER             |      |             | HD F436            |         |         |
| ONE              | F-09.05LP1 | LEVELING PLATE         |      |             |                    |         | 8       |
| 1                | F-09.05LP1 | PL 1/4x6 1/2           |      | 1 6         | A36                |         | 8       |
| ONE              | F-10.03LP2 | LEVELING PLATE         |      |             |                    |         | 9       |
| 1                | F-10.03LP2 | PL 1/4x7               |      | 1 6         | A36                |         | 9       |
| ONE              | F-09.05P1  | PLATE                  |      |             |                    |         | 55      |
| 1                | F-09.05P1  | PL 1 1/4x7             |      | 1 10        | A36                |         | 55      |
|                  |            | FIELD BOLTS            |      |             |                    |         |         |
| 2                |            | 3/4 Dia HILTI HUS-EZ   |      | 0 7         | (3 1/4" EMBEDMENT) |         |         |
|                  |            | SCREW ANCHOR           |      |             |                    |         |         |


Total weight : 744

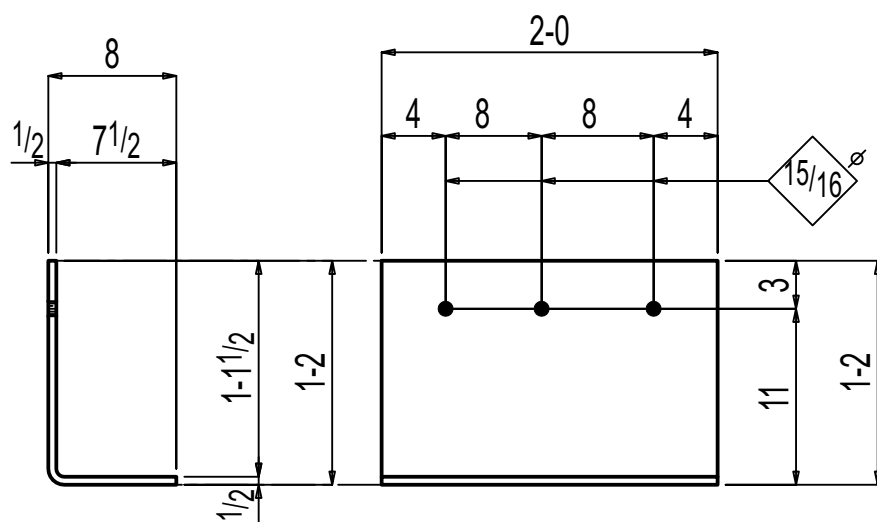


ONE BENT PLATE F-09.05BP1

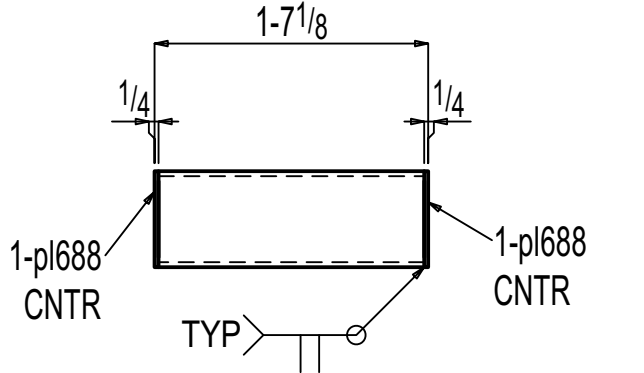


ONE HSS F-09.05M3

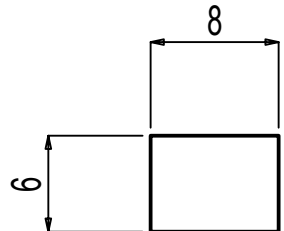


6 PLATES F-09.05M6

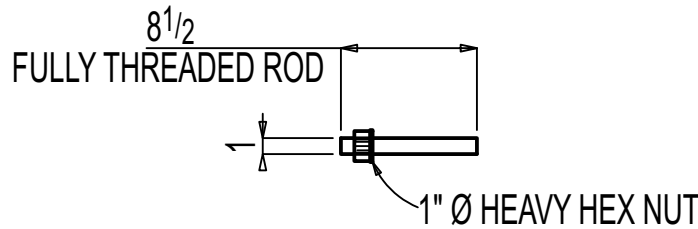


120 THREADED RODS F-09.05M9

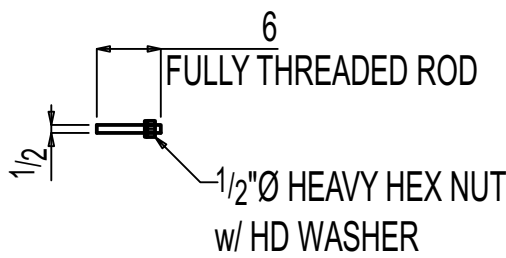


2 THREADED RODS F-09.05M12

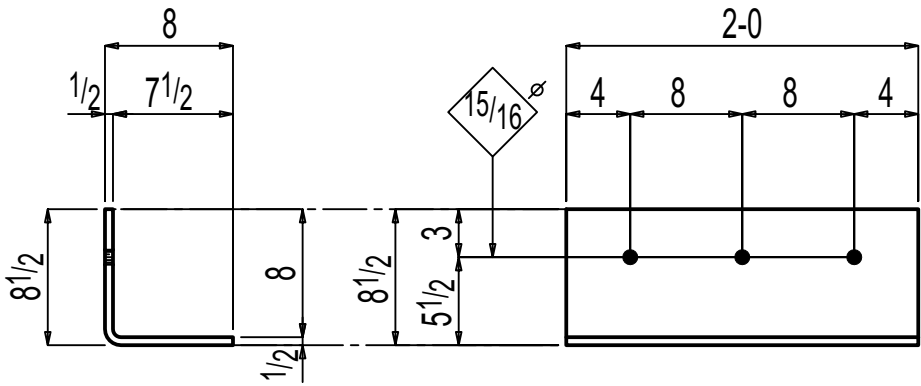


ONE BENT PLATE F-09.05BP2

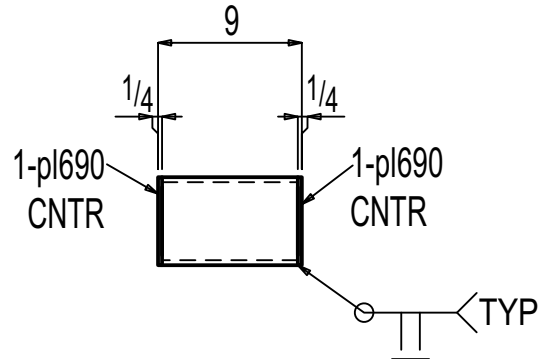


2 HSES F-09.05M4

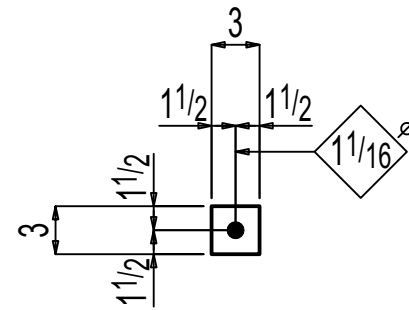


6 PLATE WASHERS F-09.05M7

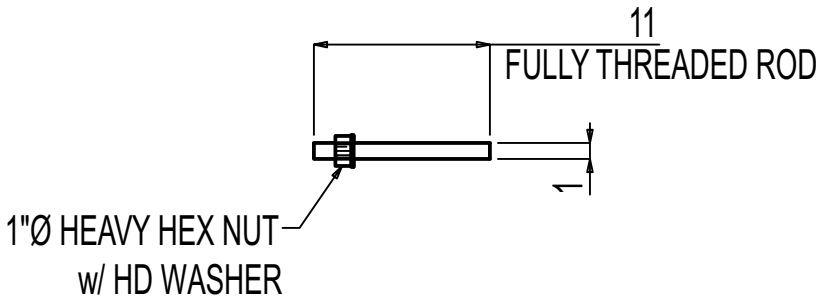

12 THREADED RODS F-09.05M10

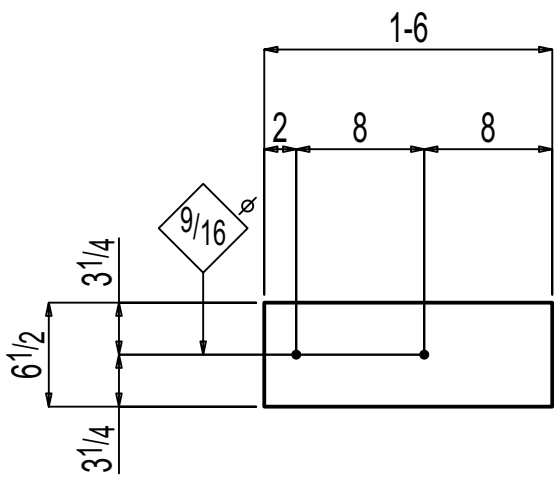


ONE LEVELING PLATE F-09.05LP1

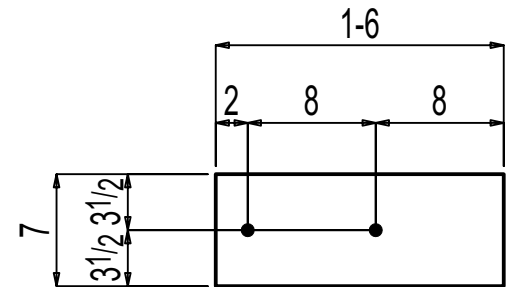


ONE LEVELING PLATE F-10.03LP2

NOT IN USE


ONE HSS F-09.05M1

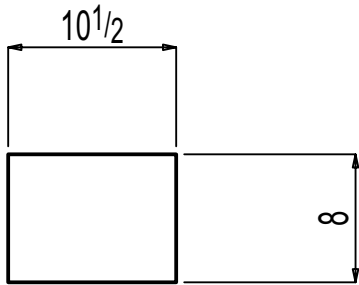


3 PLATES F-09.05M5

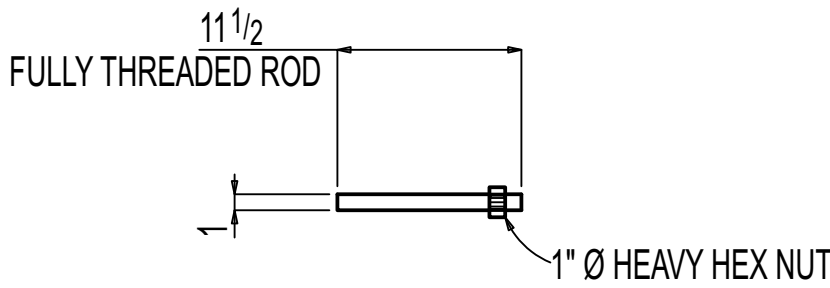

6 THREADED RODS F-09.05M8

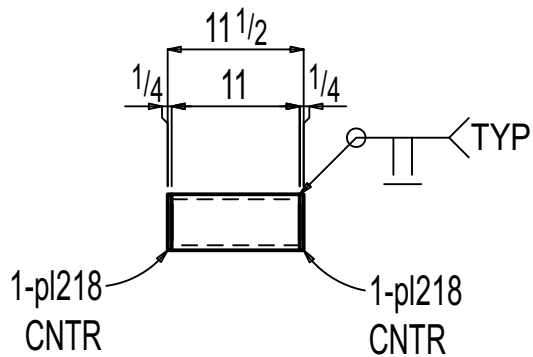


5 HSES F-09.05M11

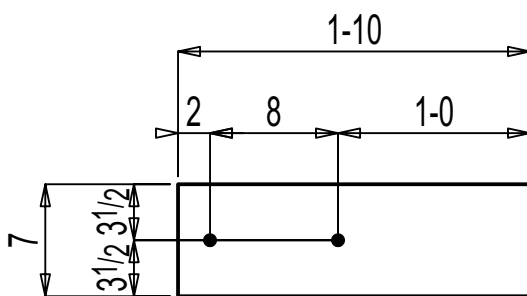

ONE PLATE F-09.05P1

PAINT PREPARATION :NO PAINT :SSPC-SP3

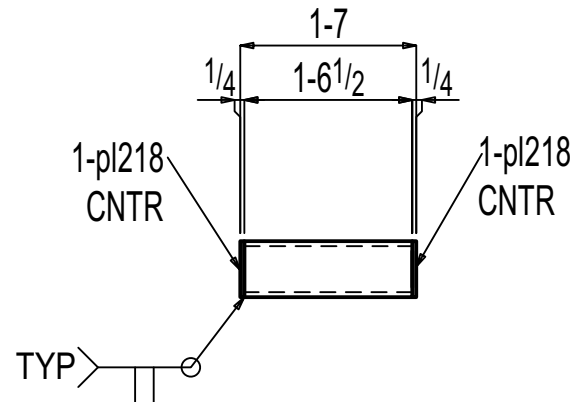

2 HSES F-09.05M2

| General Notes                                                             |                 |                 |            |
|---------------------------------------------------------------------------|-----------------|-----------------|------------|
| *Structural steel shall conform to ASTM-A992.                             |                 |                 |            |
| *Structural SQR/RND,tubing conform to ASTM A500 Grade C                   |                 |                 |            |
| *Pipe shall conform to ASTM A53, Grade B.                                 |                 |                 |            |
| *Channels, Angles and plates shall conform to A36.                        |                 |                 |            |
| *All bolts shall be 3/4" High strength in accordance with ASTM A325 (UNO) |                 |                 |            |
| *Welding Electrodes for Carbon steel :E70xx                               |                 |                 |            |
| 5                                                                         | 0               | For Fabrication | 11-14-2025 |
| 4                                                                         | D               | For Re-Approval | 10-24-2025 |
| 3                                                                         | C               | For Re-Approval | 09-19-2025 |
| 2                                                                         | B               | For Re-Approval | 06-23-2025 |
| 1                                                                         | A               | For Approval    | 02-25-2025 |
| # of Copies                                                               | Revision/ Issue | Destination     | Date       |

IRON FABRICATION SERVICES, LLC.

3029 M. Street, NW, Suite 202  
Washington, DC 20007  
Tel: 202-800-5599  
Fax: 202-478-0303

Project Name and Address

MARYLAND AVENUE

Location: 1250 MARYLAND AVENUE SW  
WASHINGTON, DC 20024

Contractor:

BALFOUR BEATTY


|                              |           |
|------------------------------|-----------|
| Approved for Fabrication by: | Signature |
|------------------------------|-----------|

|                |                             |                |                      |
|----------------|-----------------------------|----------------|----------------------|
| Contract #     | 224009                      | Drawing #      | F-09.05              |
| Contract Item: | BEAM                        |                |                      |
| Ref:           | SOW - 09: E-09.00 - E-09.02 |                |                      |
| Date           | 01/ 23/ 2025                | Drawing Title: | MISCELLANEOUS DETAIL |
| Scale          | VARIABLES                   |                |                      |




| BILL OF MATERIAL |     |            |                                      |                                    |         |              |                |
|------------------|-----|------------|--------------------------------------|------------------------------------|---------|--------------|----------------|
| LINE #           | QTY | PC MARK    | DESCRIPTION                          | LENGTH                             | REMARKS | WEIGHT TOTAL | ADVANCE MILL # |
|                  | ONE | F-09.06M1  | HSS                                  |                                    |         | 124          |                |
|                  | 1   | F-09.06M1  | HSS6x6x <sup>5</sup> / <sub>16</sub> | 5' 2 <sup>5</sup> / <sub>8</sub>   | A500C   | 122          |                |
|                  | 1   | pl688      | PL <sup>1</sup> / <sub>4</sub> x6    | 0' 6                               | A36     | 3            |                |
|                  | ONE | F-09.06M2  | HSS                                  |                                    |         | 123          |                |
|                  | 1   | F-09.06M2  | HSS6x6x <sup>3</sup> / <sub>16</sub> | 5' 3 <sup>1</sup> / <sub>16</sub>  | A500C   | 123          |                |
|                  | ONE | F-09.06M3  | HSS                                  |                                    |         | 78           |                |
|                  | 1   | F-09.06M3  | HSS6x6x <sup>3</sup> / <sub>16</sub> | 3' 3                               | A500C   | 76           |                |
|                  | 1   | pl688      | PL <sup>1</sup> / <sub>4</sub> x6    | 0' 6                               | A36     | 3            |                |
|                  | ONE | F-09.06M4  | HSS                                  |                                    |         | 77           |                |
|                  | 1   | F-09.06M4  | HSS6x6x <sup>3</sup> / <sub>16</sub> | 3' 3 <sup>1</sup> / <sub>2</sub>   | A500C   | 77           |                |
|                  | 4   | F-09.06M6  | SHIM PL                              |                                    |         | 10           |                |
|                  | 4   | F-09.06M6  | PL <sup>1</sup> / <sub>8</sub> x8    | 0' 9                               | A36     | 10           |                |
|                  | ONE | F-09.06M7  | HSS                                  |                                    |         | 84           |                |
|                  | 1   | F-09.06M7  | HSS6x6x <sup>3</sup> / <sub>16</sub> | 3' 7 <sup>1</sup> / <sub>4</sub>   | A500C   | 84           |                |
|                  | ONE | F-09.06M8  | HSS                                  |                                    |         | 81           |                |
|                  | 1   | F-09.06M8  | HSS6x6x <sup>3</sup> / <sub>16</sub> | 3' 4 <sup>3</sup> / <sub>16</sub>  | A500C   | 78           |                |
|                  | 1   | pl688      | PL <sup>1</sup> / <sub>4</sub> x6    | 0' 6                               | A36     | 3            |                |
|                  | ONE | F-09.06M9  | HSS                                  |                                    |         | 53           |                |
|                  | 1   | F-09.06M9  | HSS6x2x <sup>5</sup> / <sub>16</sub> | 3' 6 <sup>5</sup> / <sub>8</sub>   | A500C   | 53           |                |
|                  | 1   | pl3034     | PL <sup>1</sup> / <sub>4</sub> x2    | 0' 6                               | A36     | 1            |                |
|                  | ONE | F-09.06M10 | HSS                                  |                                    |         | 58           |                |
|                  | 1   | F-09.06M10 | HSS6x2x <sup>3</sup> / <sub>16</sub> | 3' 11 <sup>3</sup> / <sub>16</sub> | A500C   | 58           |                |
|                  | ONE | F-09.06A1  | ANGLE                                |                                    |         | 7            |                |
|                  | 1   | F-09.06A1  | L4x4x <sup>1</sup> / <sub>4</sub>    | 1' 0                               | A36     | 7            |                |


Total weight : 696

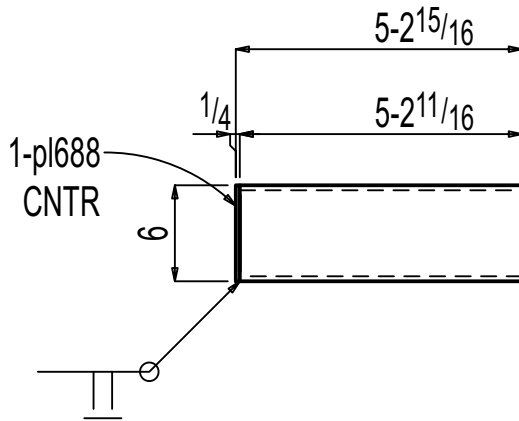


ONE HSS F-09.06M1

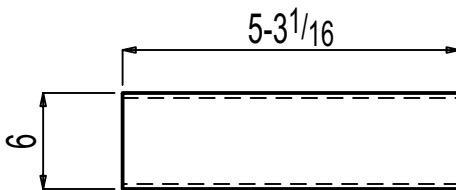

ONE HSS F-09.06M2

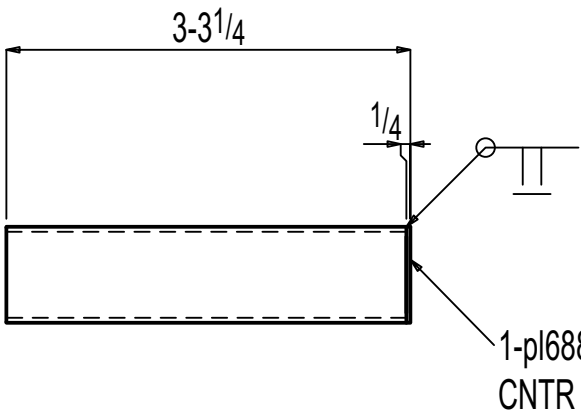


ONE HSS F-09.06M3

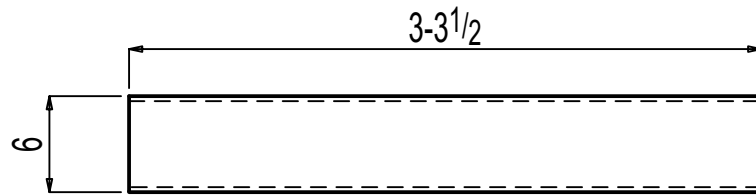


ONE HSS F-09.06M4


NOT IN USE

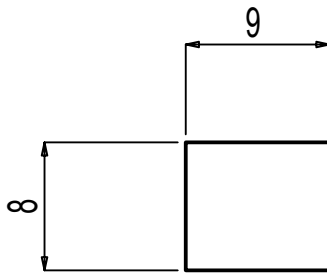


4 SHIM PL.S F-09.06M6

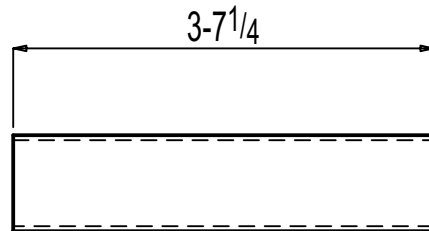


ONE HSS F-09.06M7

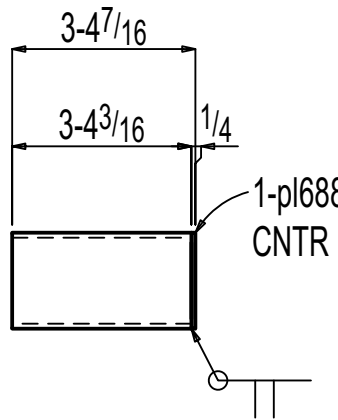


ONE HSS F-09.06M8

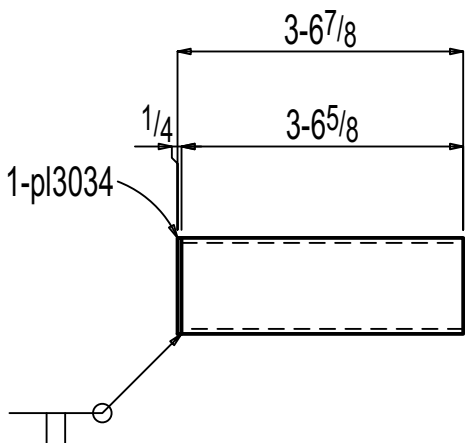

ONE HSS F-09.06M9

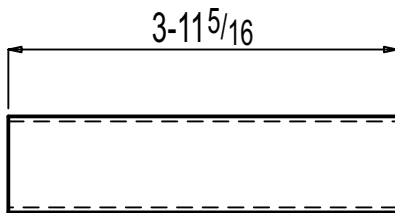

ONE HSS F-09.06M10

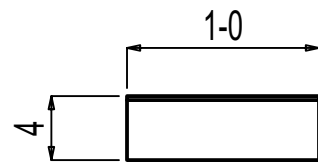

ONE ANGLE F-09.06A1

PAINT :NO PAINT  
PREPARATION :SSPC-SP3

| General Notes                                                             |                 |                 |            |
|---------------------------------------------------------------------------|-----------------|-----------------|------------|
| *Structural steel shall conform to ASTM-A992.                             |                 |                 |            |
| *Structural SQR/RND,tubing conform to ASTM A500 Grade C                   |                 |                 |            |
| *Pipe shall conform to ASTM A53, Grade B.                                 |                 |                 |            |
| *Channels, Angles and plates shall conform to A36.                        |                 |                 |            |
| *All bolts shall be 3/4" High strength in accordance with ASTM A325 (UNO) |                 |                 |            |
| *Welding Electrodes for Carbon steel :E70xx                               |                 |                 |            |
|                                                                           |                 |                 |            |
|                                                                           |                 |                 |            |
|                                                                           |                 |                 |            |
| 3                                                                         | 0               | For Fabrication | 11-14-2025 |
| 2                                                                         | B               | Deleted         | 09-19-2025 |
| 1                                                                         | A               | For Approval    | 06-23-2025 |
| # of Copies                                                               | Revision/ Issue | Destination     | Date       |

IRON FABRICATION SERVICES, LLC.

3029 M. Street, NW, Suite 202  
Washington, DC 20007  
Tel: 202-800-5599  
Fax: 202-478-0303

Project Name and Address  
**MARYLAND AVENUE**

Location: **1250 MARYLAND AVENUE SW  
WASHINGTON, DC 20024**

Contractor:  
**BALFOUR BEATTY**

|                              |           |
|------------------------------|-----------|
| Approved for Fabrication by: | Signature |
|                              |           |

|                                            |                                      |
|--------------------------------------------|--------------------------------------|
| Contract # <b>224009</b>                   | Drawing # <b>F-09.06</b>             |
| Contract Item: <b>BEAM</b>                 |                                      |
| Ref:<br><b>SOW - 09: E-09.00 - E-09.02</b> |                                      |
| Date<br><b>01/ 23/ 2025</b>                | Drawing Title:<br><b>MISC DETAIL</b> |
| Scale<br>VARIES                            |                                      |