
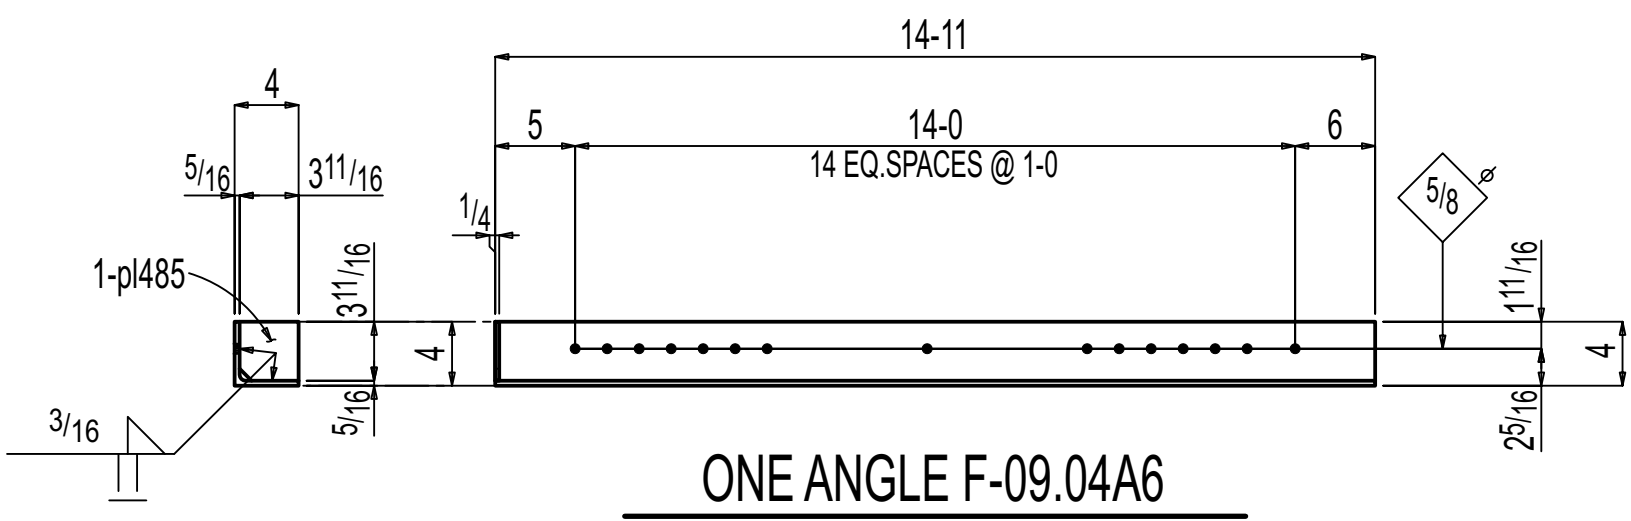
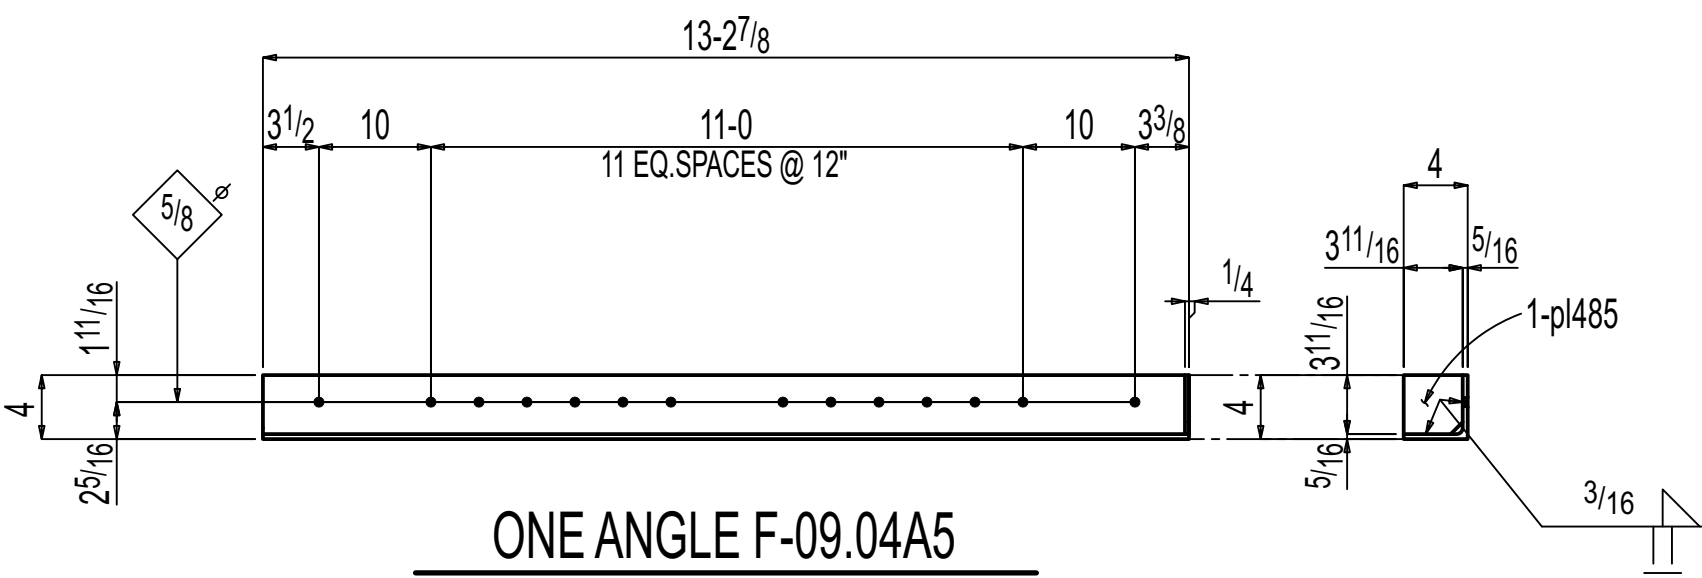
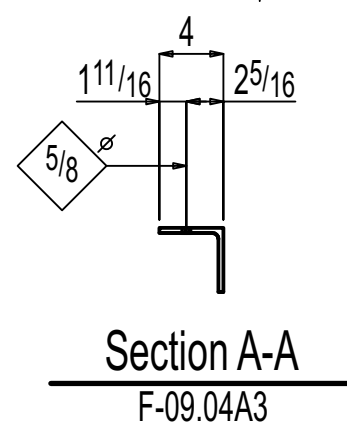
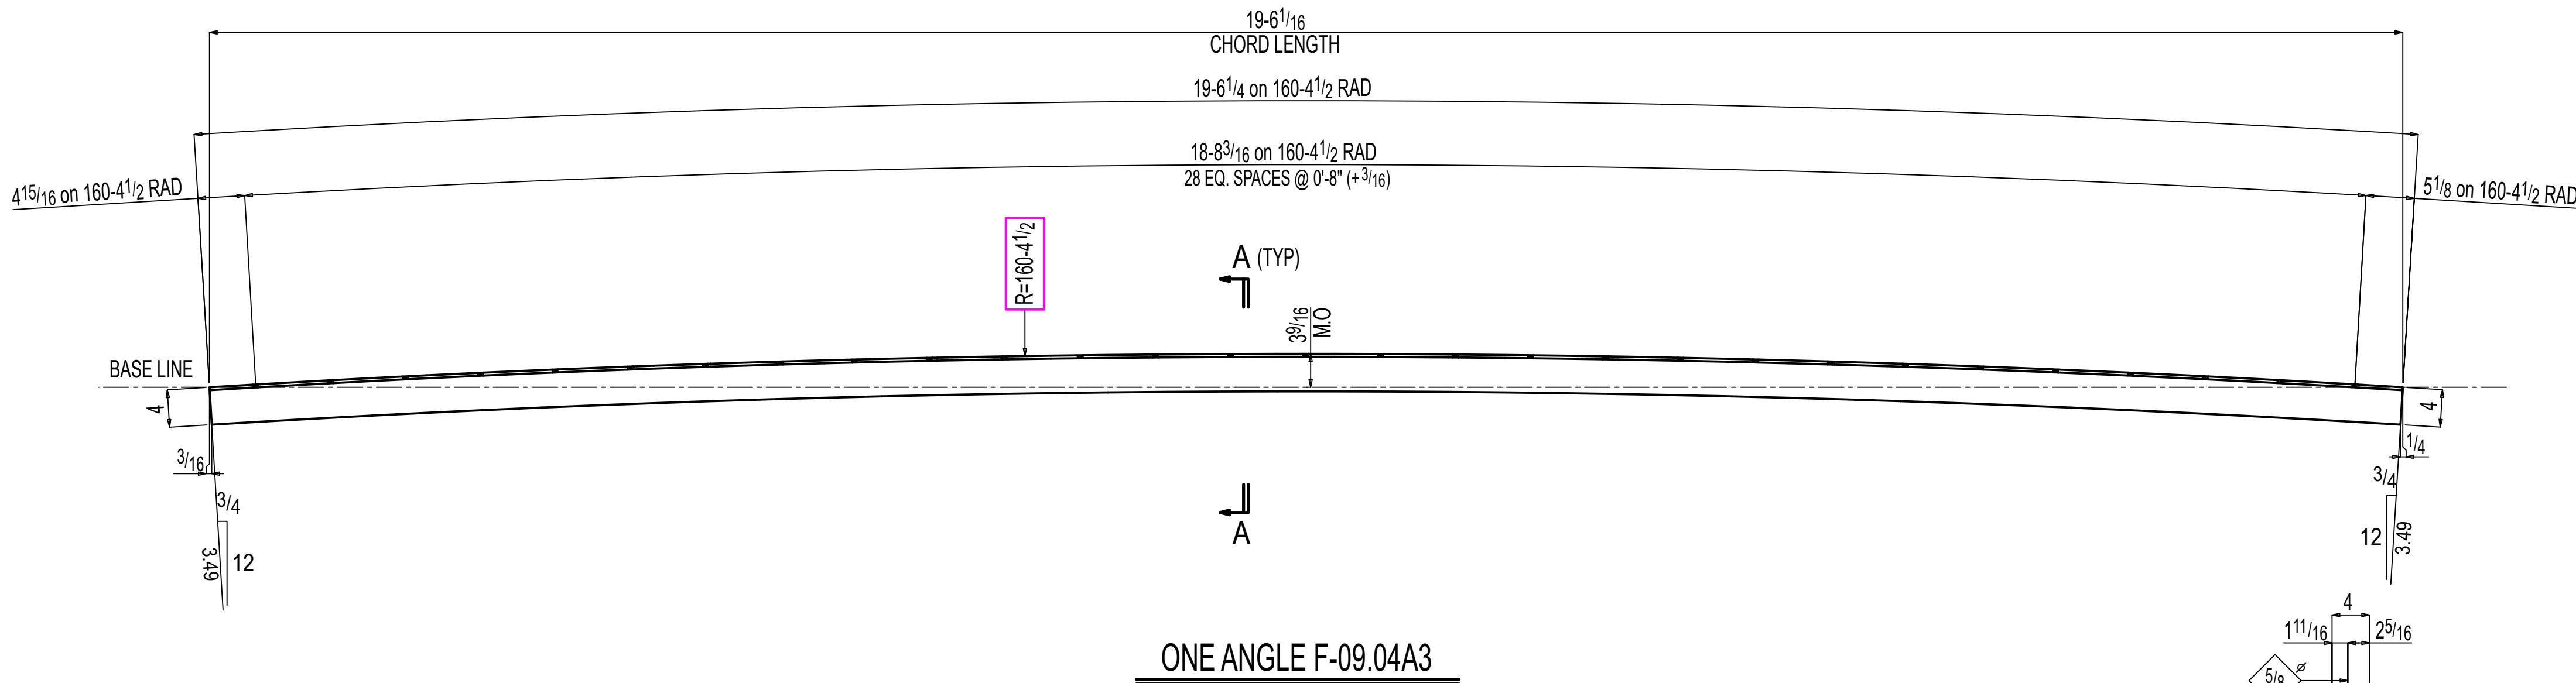
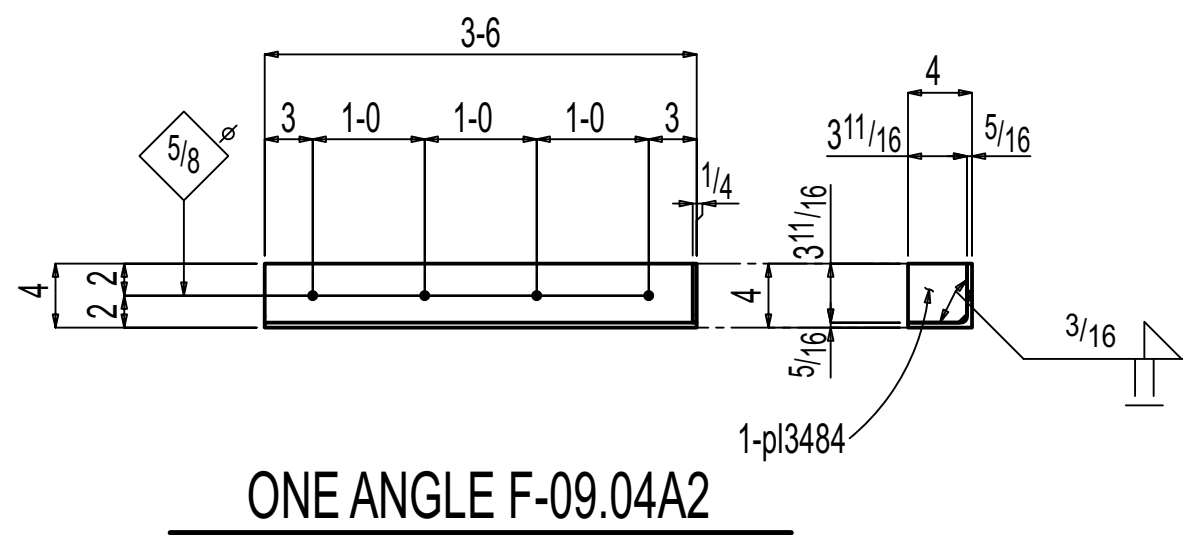
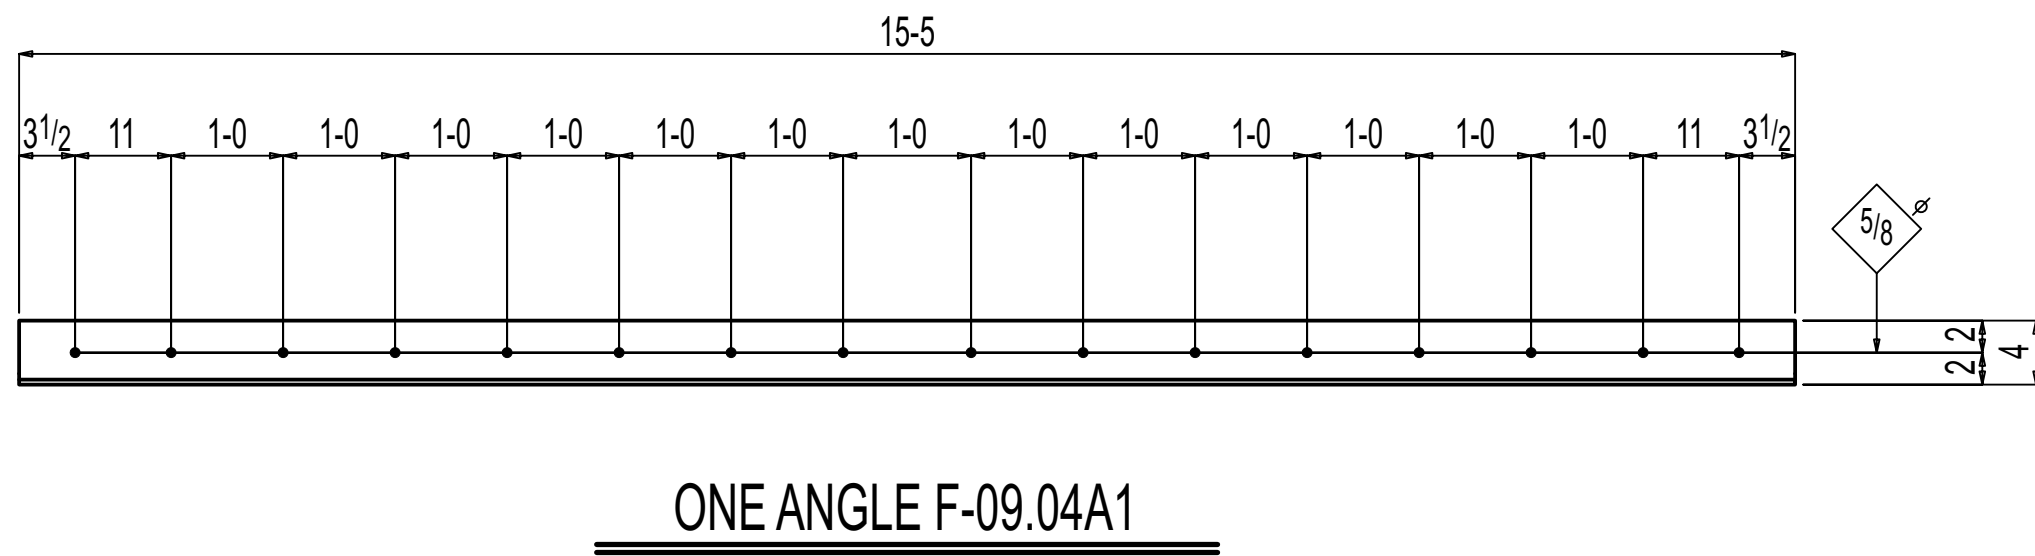
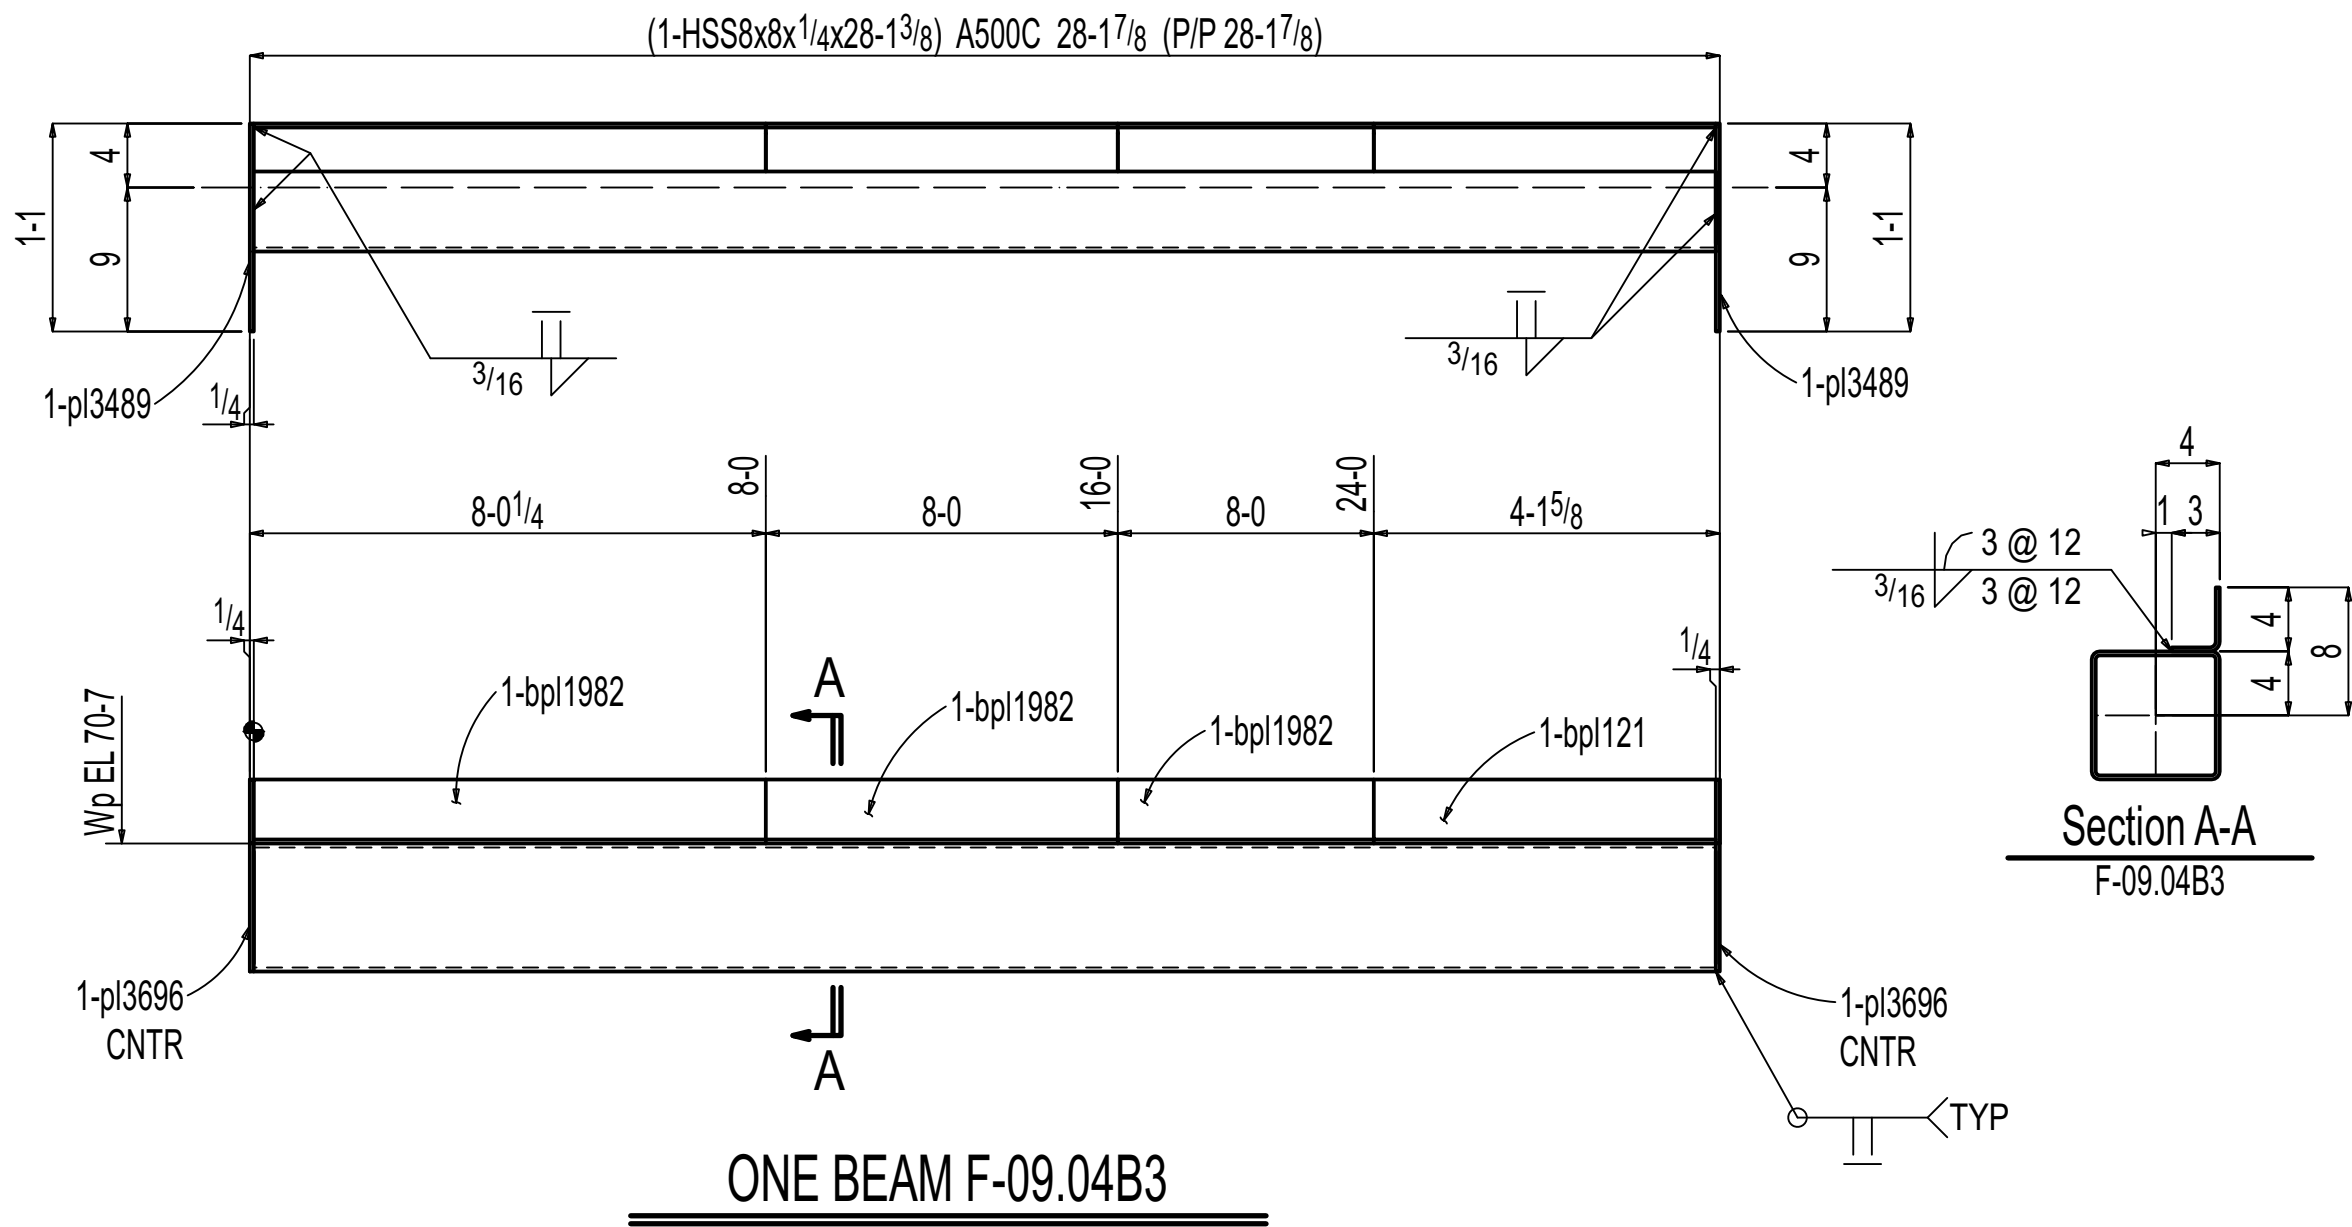
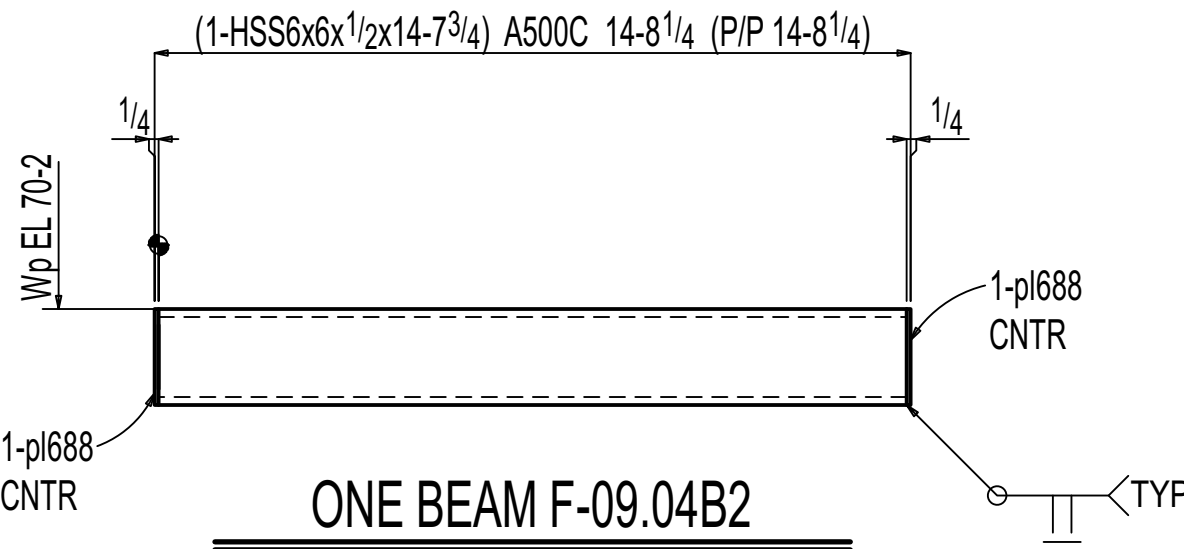


BILL OF MATERIAL							
LINE #	QTY	PC	MARK	DESCRIPTION	LENGTH	REMARKS	ADVANCE
	TOTAL						MILL #
ONE	F-09.04B1	BEAM					969
1	F-09.04B1	HSS8x6x1/2			22 10 1/2	A500C	962
2	pl1459	PL 1/4x6			0 8	A36	7
ONE	F-09.04B2	BEAM					521
1	F-09.04B2	HSS6x6x1/2			14 7 3/4	A500C	516
2	pl688	PL 1/4x6			0 6	A36	5
ONE	F-09.04B3	BEAM					899
1	F-09.04B3	HSS8x8x1/4			28 13 1/8	A500C	726
2	pl3696	PL 1/4x8			0 8	A36	9
3	bp1982	PL 1/4x6 9/16			8 0	BENT A36	134
1	bp1121	PL 1/4x6 9/16			4 13 1/8	BENT A36	23
2	pl3489	PL 1/4x4			1 1	A36	7
ONE	F-09.04A1	ANGLE					126
1	F-09.04A1	L4x4x3/16			15 5	A36	126
16		FIELD BOLTS					
		1/2 Dia HILTI HAS V-36			0 4 1/2		
		w/ HILTI HIT HY-200 V3			(2 3/4" EMBEDMENT)		
		ADHESIVE					
ONE	F-09.04A2	ANGLE					30
1	F-09.04A2	L4x4x3/16			3 6	A36	29
1	pl3484	PL 1/4x3 11/16			0 3 11/16	A36	1
4		FIELD BOLTS					
		1/2 Dia HILTI HAS V-36			0 4 1/2		
		w/ HILTI HIT HY-200 V3			(2 3/4" EMBEDMENT)		
		ADHESIVE					
ONE	F-09.04A3	ANGLE					160
1	F-09.04A3	L4x4x3/16			19 6 1/4	A36	160
29		FIELD BOLTS					
		1/2 Dia HILTI HAS V-36			0 4 1/2		
		w/ HILTI HIT HY-200 V3			(2 3/4" EMBEDMENT)		
		ADHESIVE					
ONE	F-09.04A5	ANGLE					110
1	F-09.04A5	L4x4x3/16			13 2 7/8	A36	109
1	pl485	PL 1/4x3 11/16			0 3 11/16	A36	1
14		FIELD BOLTS					
		1/2 Dia HILTI HAS V-36			0 4 1/2		
		w/ HILTI HIT HY-200 V3			(2 3/4" EMBEDMENT)		
		ADHESIVE					
ONE	F-09.04A6	ANGLE					123
1	F-09.04A6	L4x4x3/16			14 11	A36	122
1	pl485	PL 1/4x3 11/16			0 3 11/16	A36	1
15		FIELD BOLTS					
		1/2 Dia HILTI HAS V-36			0 4 1/2		
		w/ HILTI HIT HY-200 V3			(2 3/4" EMBEDMENT)		
		ADHESIVE					

Total weight : 2938

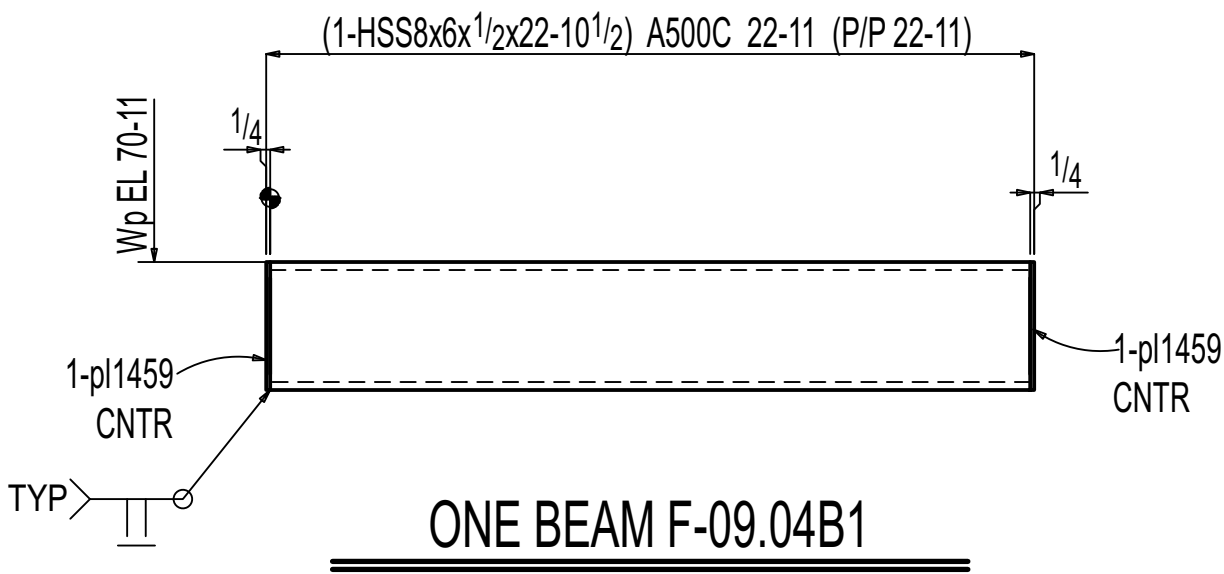

PAINT :NO PAINT
PREPARATION :SSPC-SP3

General Notes			
*Structural steel shall conform to ASTM-A992.			
*Structural SQR/RND,tubing conform to ASTM A500 Grade C			
*Pipe shall conform to ASTM A53, Grade B.			
*Channels, Angles and plates shall conform to A36.			
*All bolts shall be 3/4" High strength in accordance with ASTM A325 (UNO)			
*Welding Electrodes for Carbon steel :E70xx			
5	0	For Fabrication	11-14-2025
4	D	For Re-Approval	10-24-2025
3	C	For Re-Approval	09-19-2025
2	B	Deleted	06-23-2025
1	A	For Approval	02-25-2025
# of Copies	Revision/ Issue	Destination	Date

IRON FABRICATION SERVICES, LLC.

3029 M. Street, NW, Suite 202
Washington, DC 20007
Tel: 202-800-5599
Fax: 202-478-0303

Project Name and Address
MARYLAND AVENUE
Location: **1250 MARYLAND AVENUE SW
WASHINGTON, DC 20024**

Contractor:
BALFOUR BEATTY

Approved for Fabrication by: Signature

Contract # **224009** Drawing # **F-09.04**

Contract Item: **BEAM**

Ref:
SOW - 09: E-09.00 - E-09.01

Date **01/23/2025** Drawing Title: **BEAMS & ANGLE DETAIL**
Scale **VARIES**