
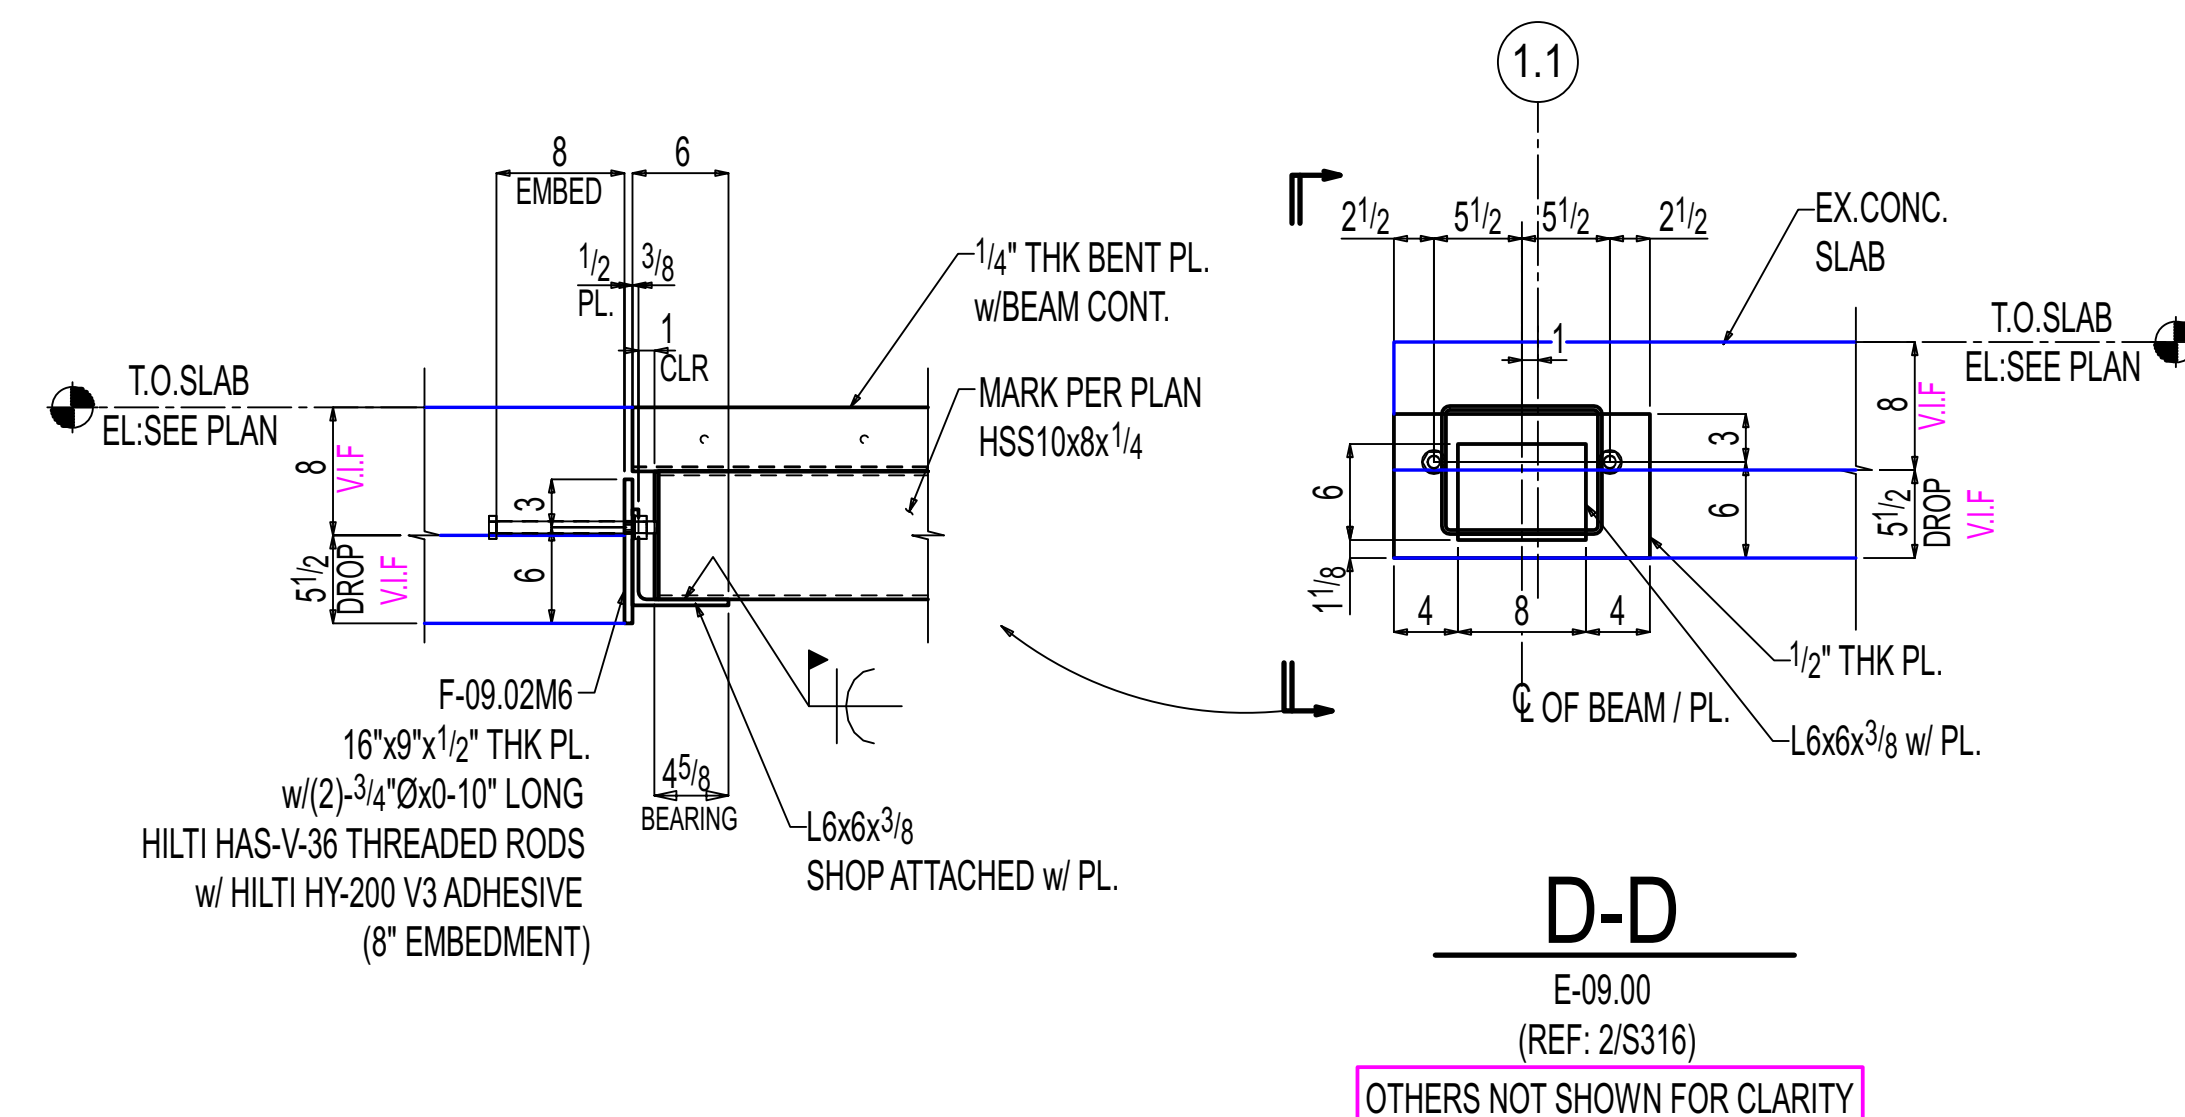
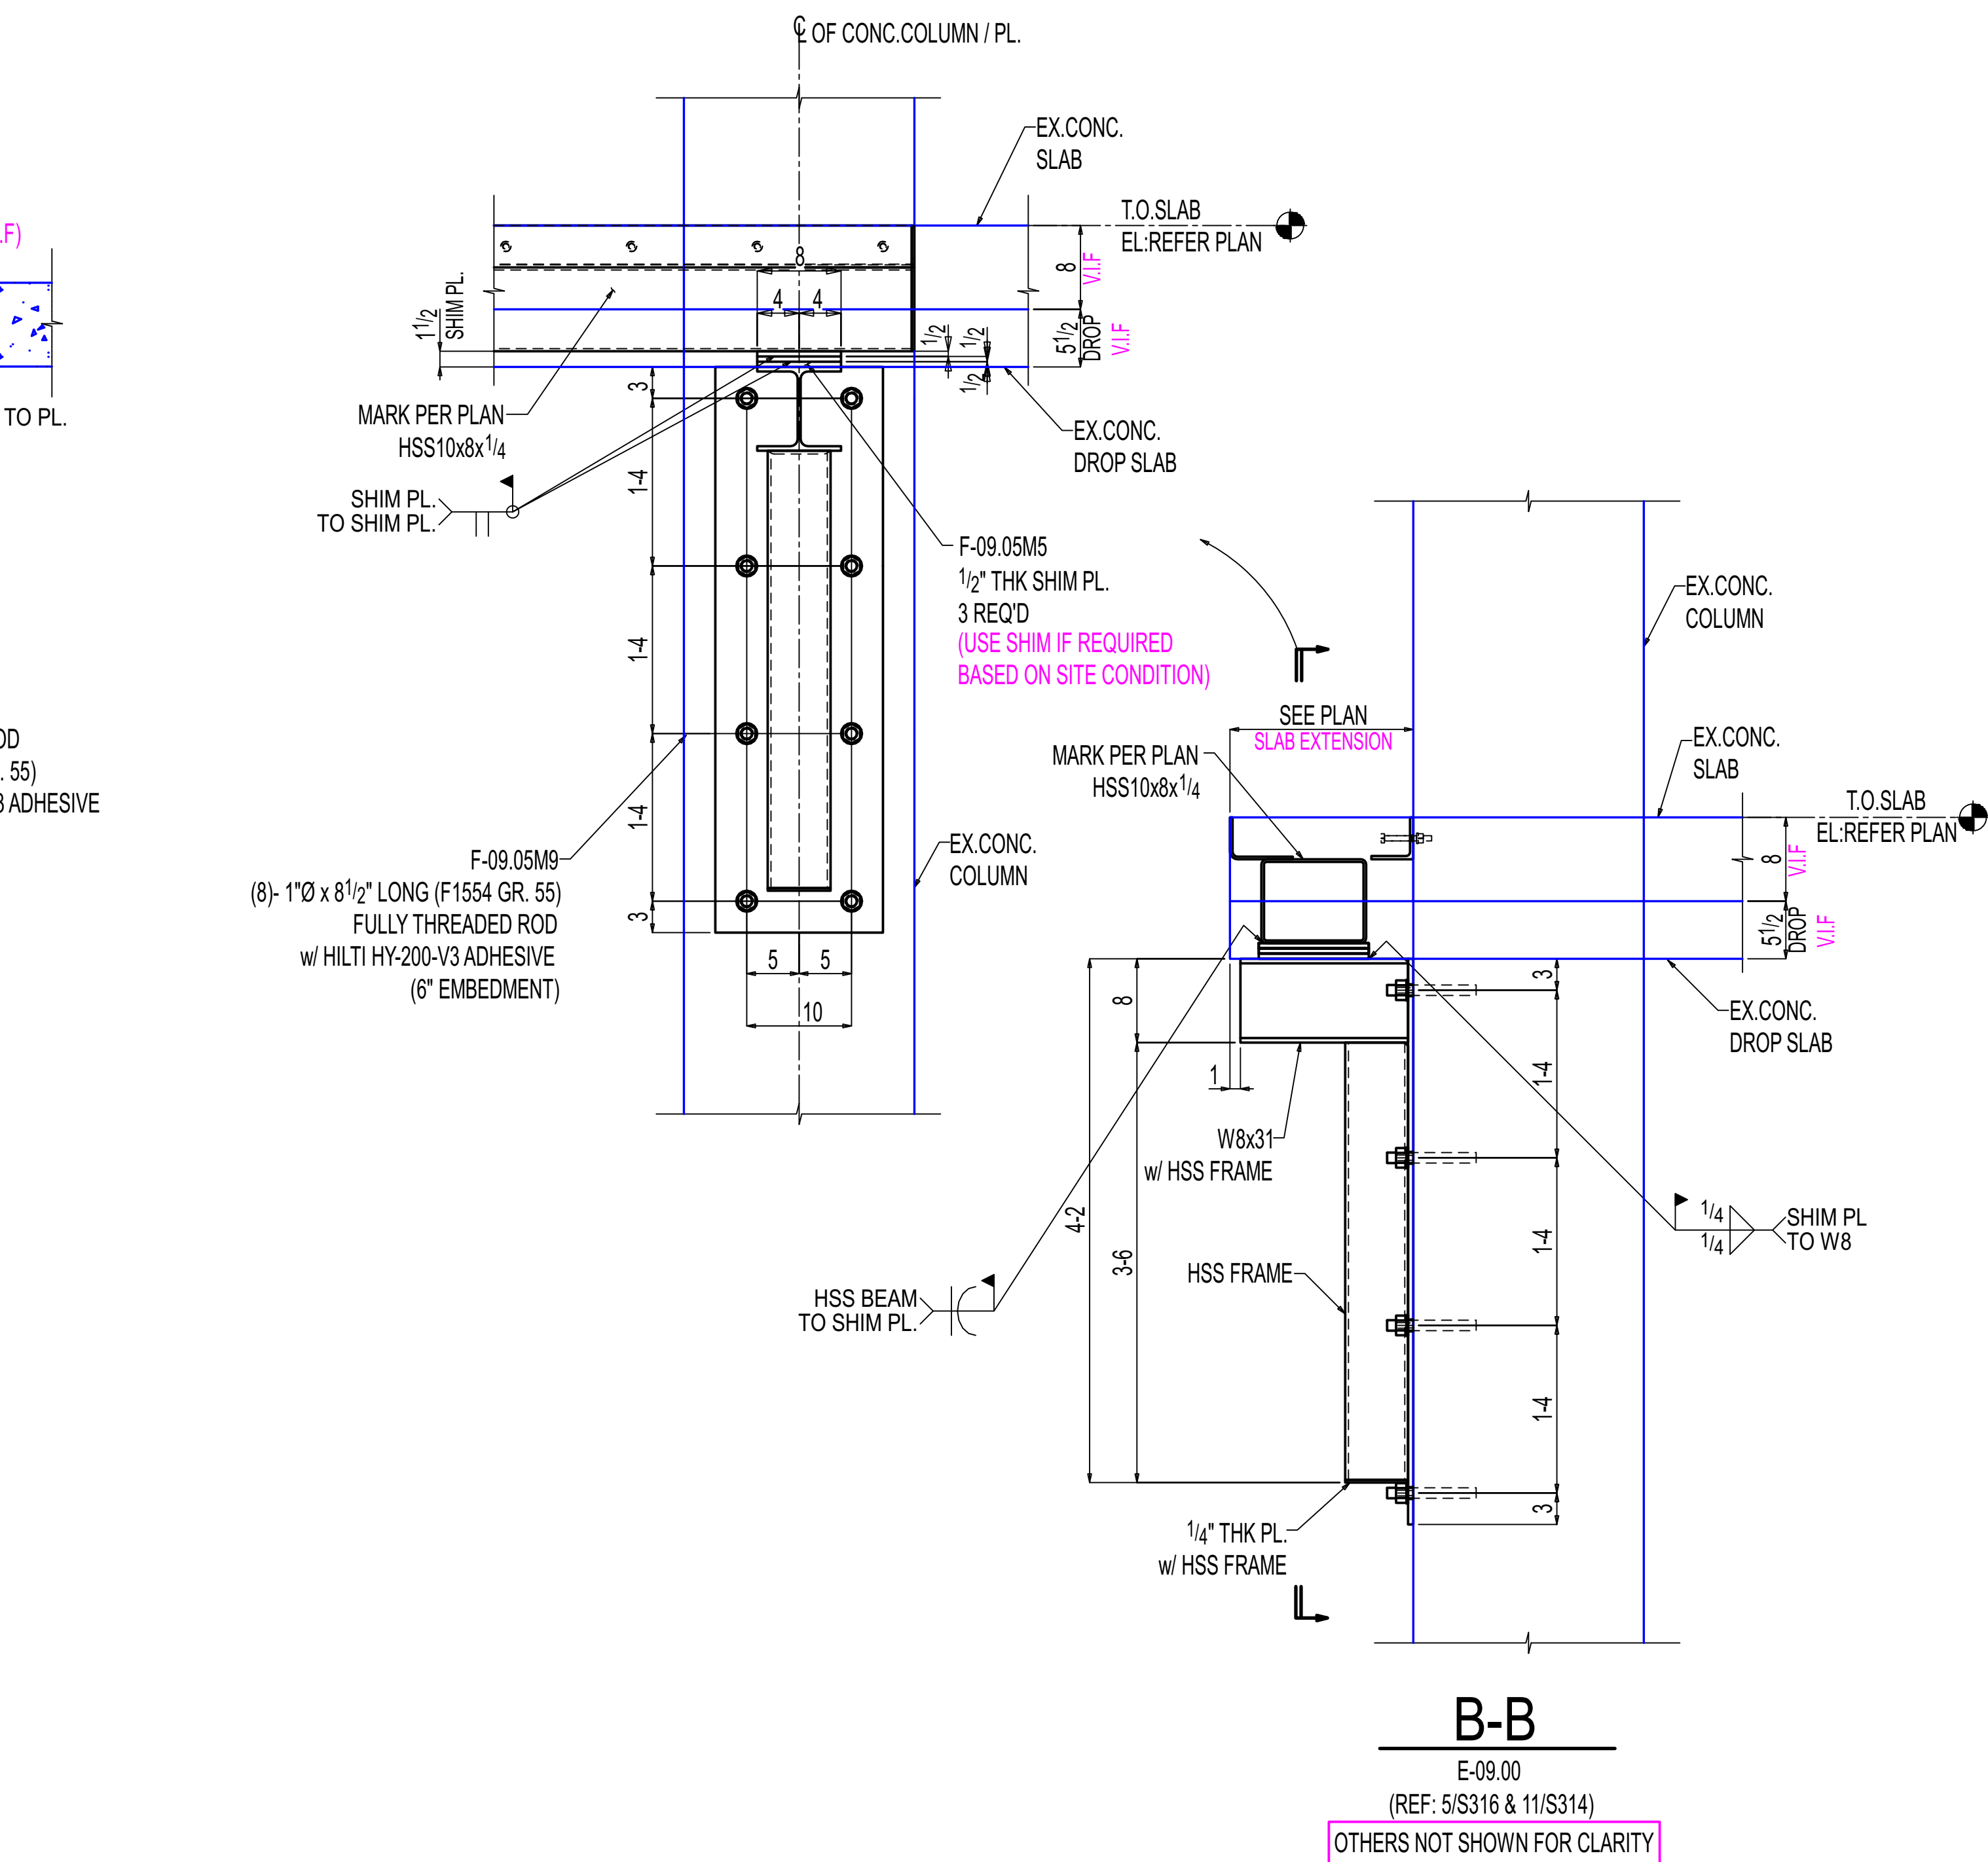


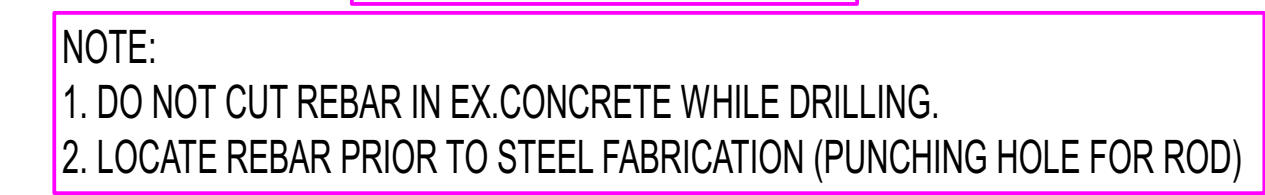

- *Structural steel shall conform to ASTM-A992.
- *Structural SQR/RND,tubing conform to ASTM A500 Grade C
- *Pipe shall conform to ASTM A53, Grade B.
- *Channels, Angles and plates shall conform to A36.
- *All bolts shall be 3/4" High strength in accordance with ASTM A325 (UNO)
- *Welding Electrodes for Carbon steel :E70xx

5	0	For Construction	11-14-2025
4	D	For Re-Approval	10-24-2025
3	C	For Re-Approval	09-19-2025
2	B	For Re-Approval	06-23-2025
1	A	For Approval	02-25-2025
# of Copies	Revision/ Issue	Destination	Date

3029 M. Street, NW, Suite 202
Washington, DC 20007
Tel: 202-800-5599
Fax: 202-478-0303

Location: **1250 MARYLAND AVENUE SW**
WASHINGTON, DC 20024

BALFOUR BEATTY

signature

Drawing # **E-09.01**

Drawing Title:

**SOW #09 LEVEL-03 NEW
SLAB EXTENSION SUPPORT
SECTIONS**