
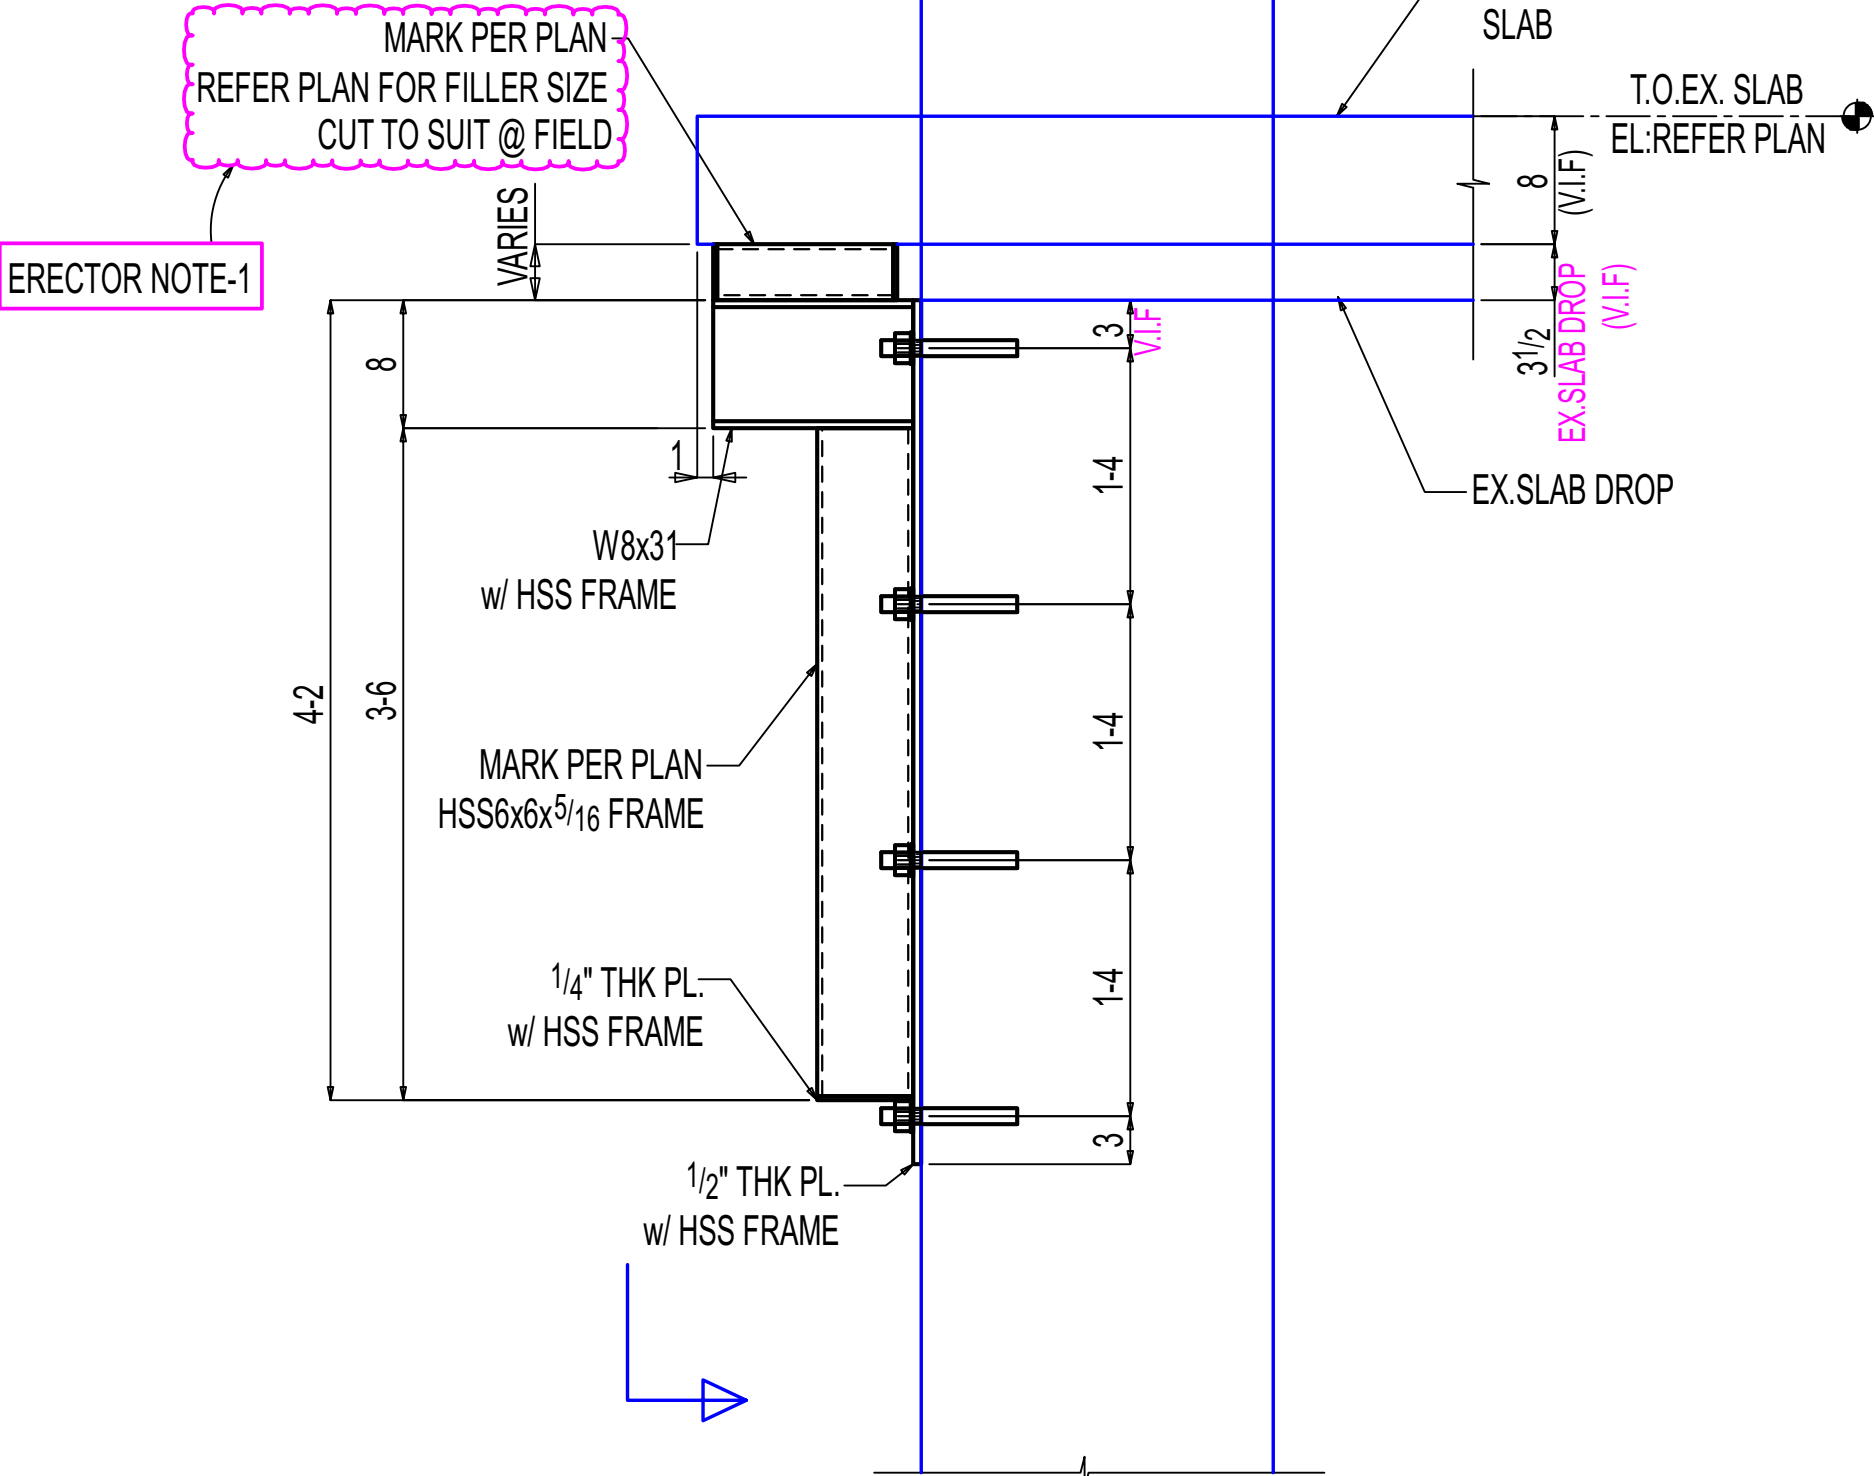


NOT IN USE

F-F
E-09.00

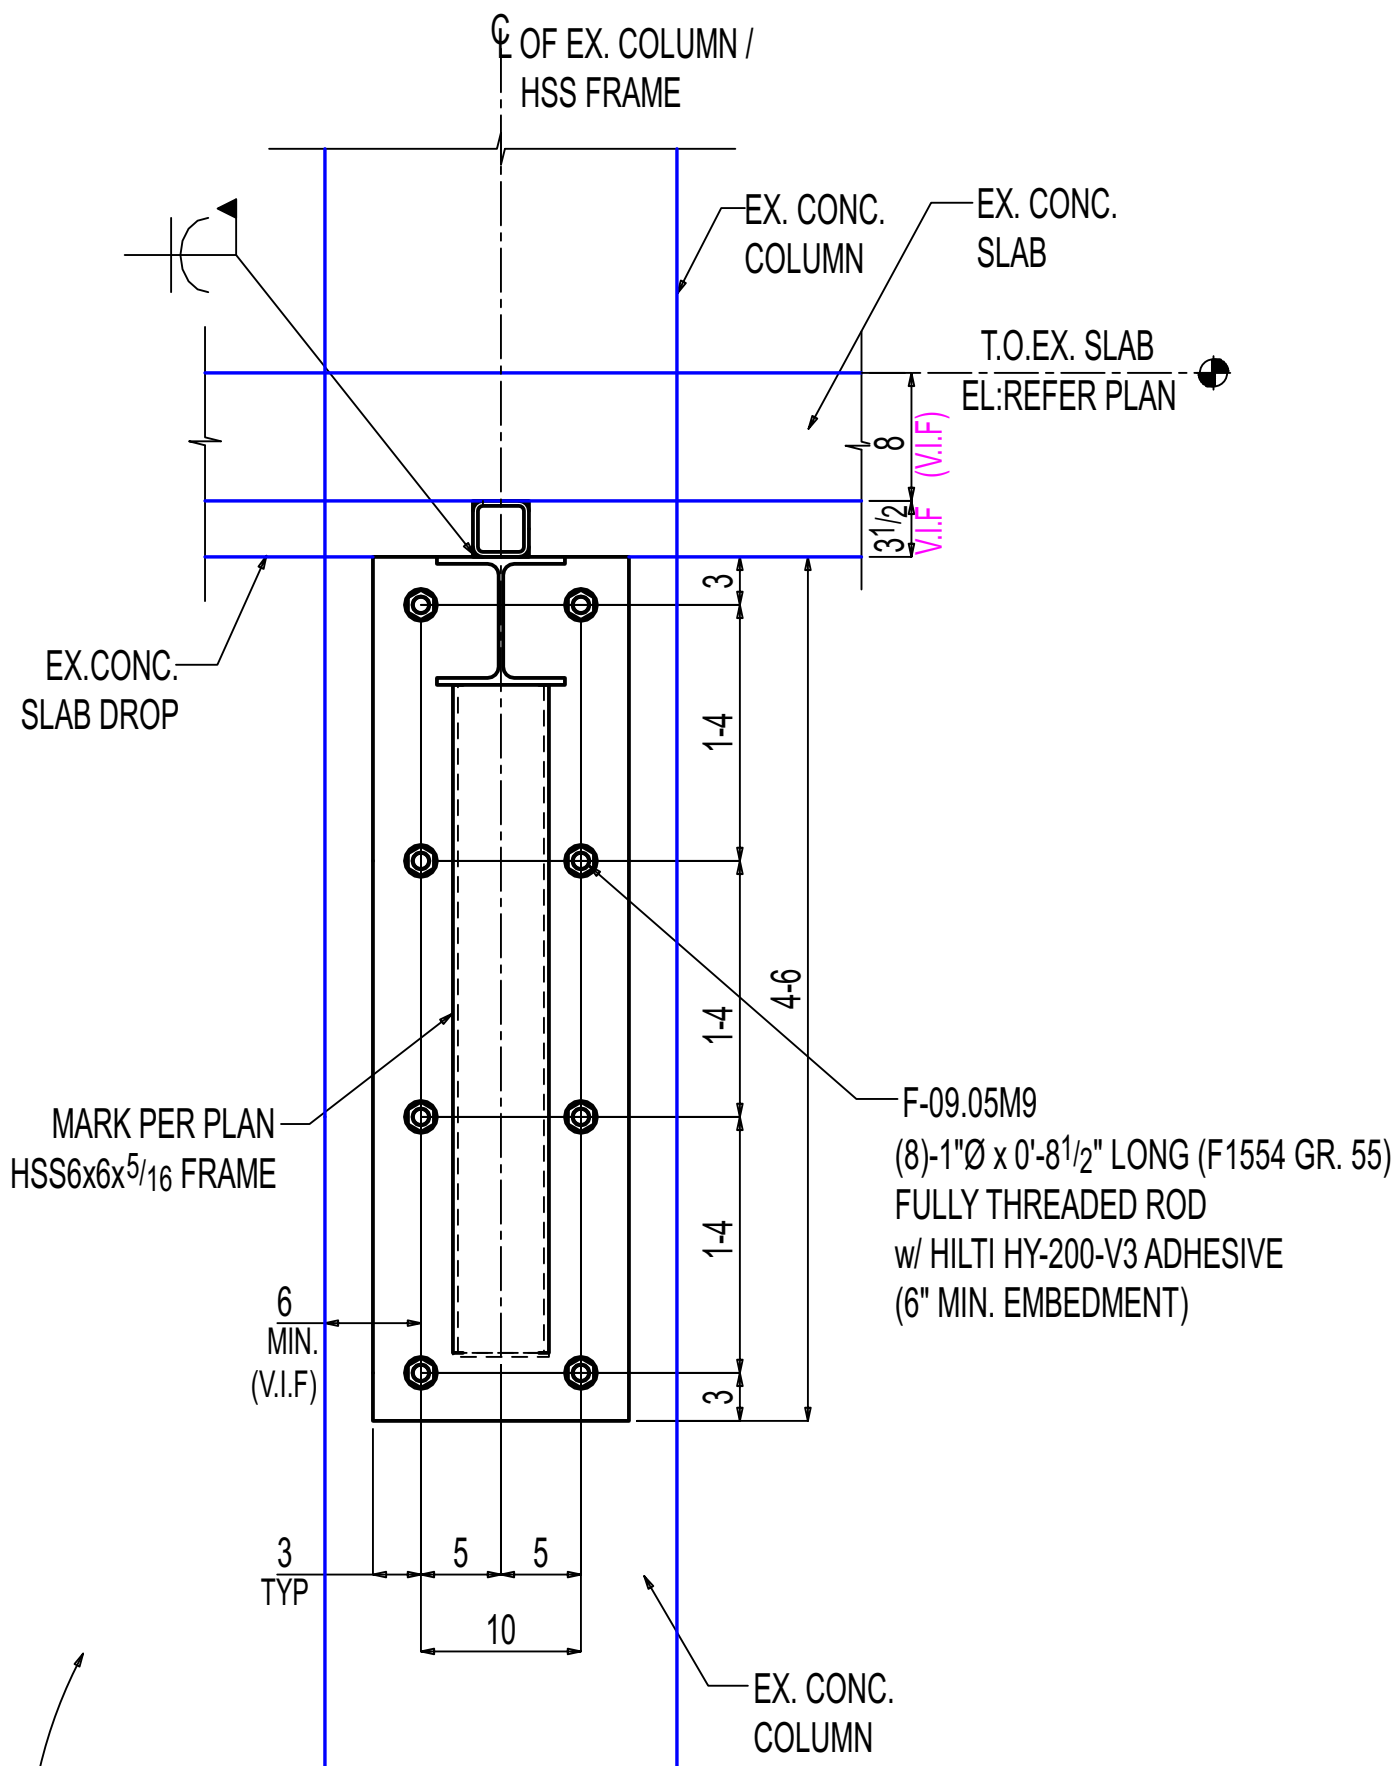

G-G
E-09.00
(REF: 11/S314)

OTHERS NOT SHOWN FOR CLARITY



SHOP / ERECTOR NOTE:
LOCATE EXISTING REBAR PRIOR TO FABRICATION OF PLATE.
DO NOT DRILL THROUGH REBAR.

ERECTOR NOTE-1:
ADJUST HSS DEPTH IN FIELD BY CUT THE HSS TO MATCH
EXISTING SLAB DROP THICKNESS, AND WELD TO THE
TOP OF HSS FRAME AT SITE PRIOR TO ERECTING THE HSS FRAME.

NOTE:
FILLER SIZE AND REQUIREMENT WILL BE
FINALIZED AFTER FIELD MEASUREMENT.

MARK PER PLAN
HSS3 1/2x3 1/2x5/16
CUT TO SUIT @ FIELD

ERECTOR NOTE-1

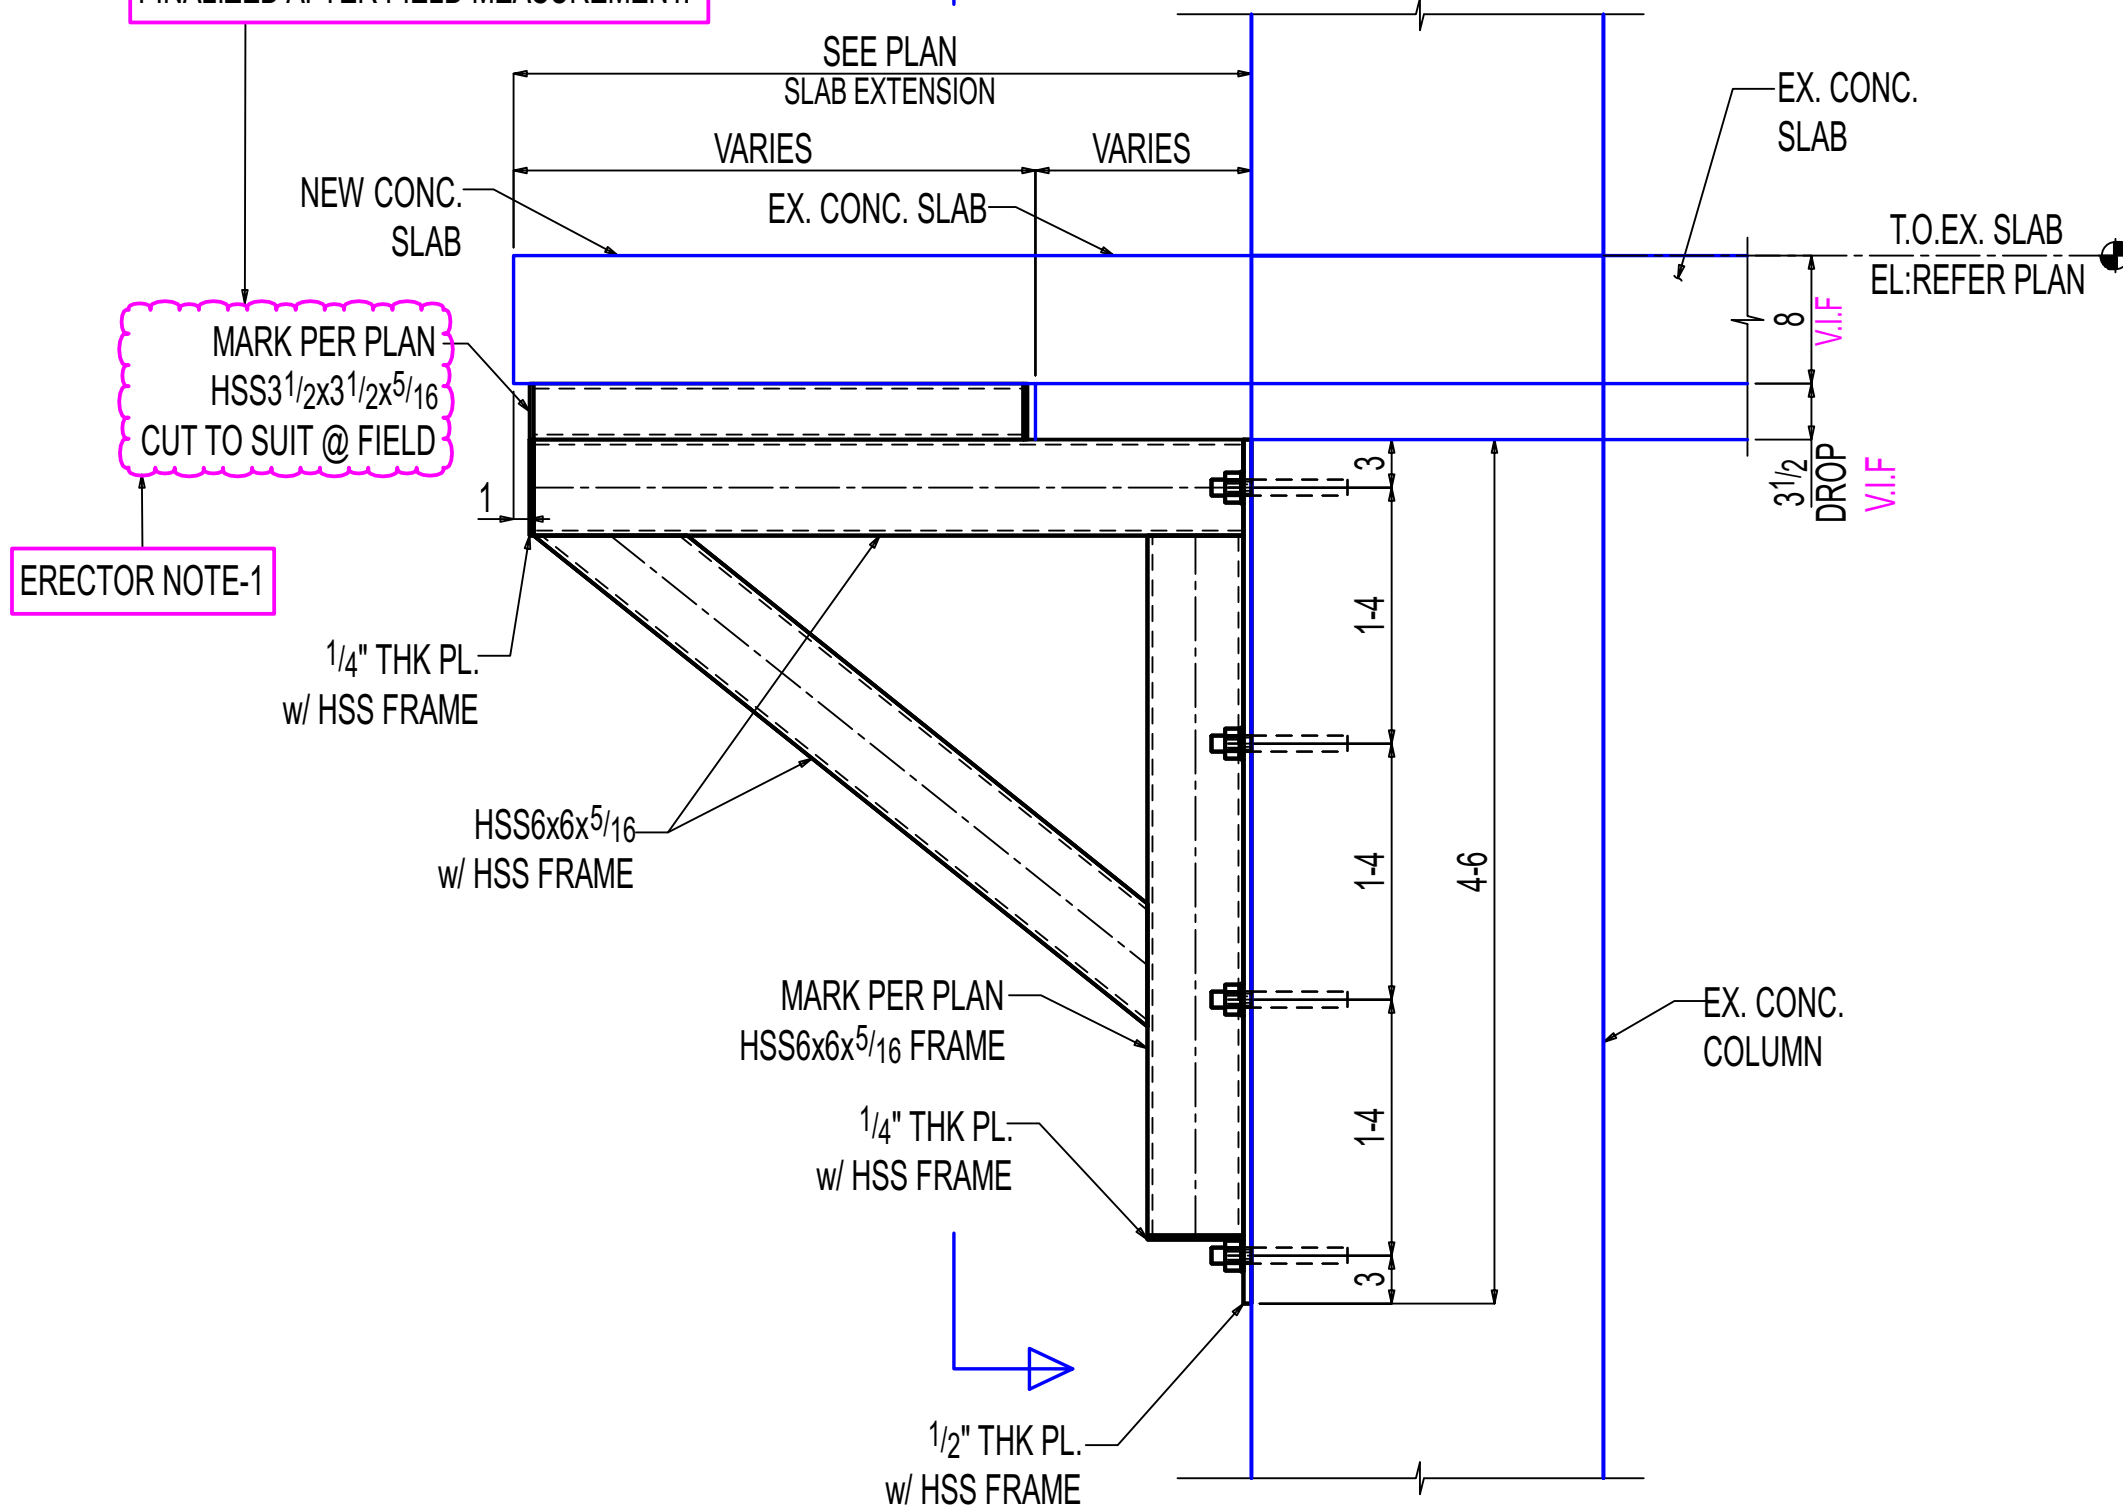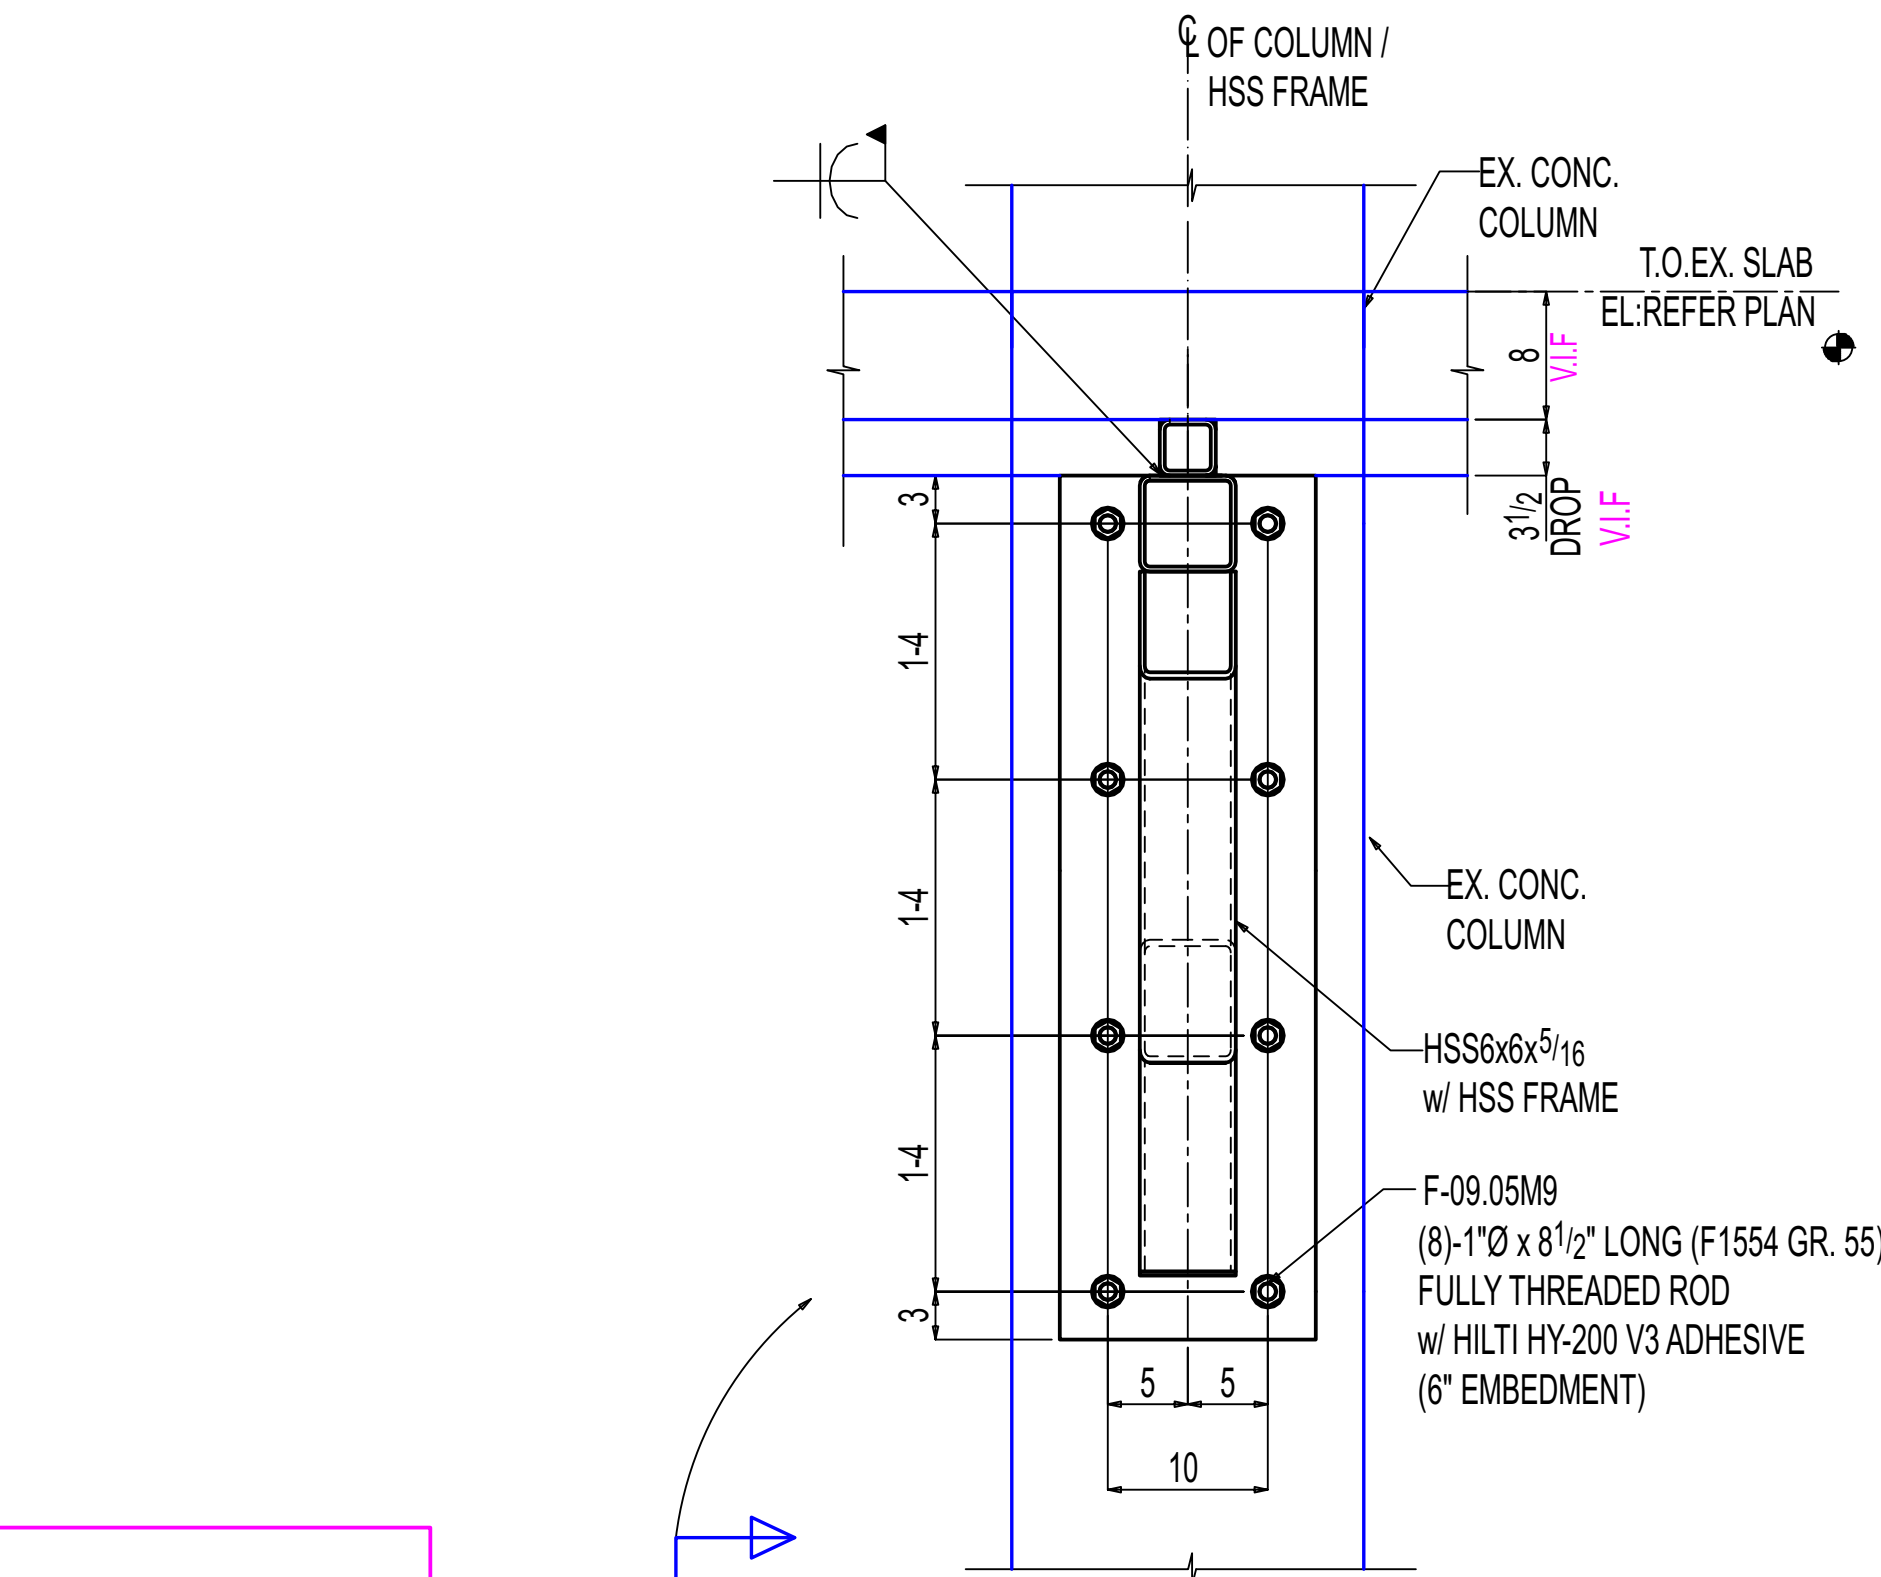

H-H
E-09.00A
(REF: 3/S307)

OTHERS NOT SHOWN FOR CLARITY

General Notes

- *Structural steel shall conform to ASTM-A992.
- *Structural SQR/RND.tubing conform to ASTM A500 Grade C
- *Pipe shall conform to ASTM A53, Grade B.
- *Channels, Angles and plates shall conform to A36.
- *All bolts shall be 3/4" High strength in accordance with ASTM A325 (UNO)
- *Welding Electrodes for Carbon steel :E70xx

# of Copies	Revision/ Issue	Destination	Date
5	0	For Construction	11-14-2025
4	D	For Re-Approval	10-24-2025
3	C	For Re-Approval	09-19-2025
2	B	For Re-Approval	06-23-2025
1	A	For Approval	02-25-2025

IRON FABRICATION SERVICES, LLC.

3029 M. Street, NW, Suite 202
Washington, DC 20007
Tel: 202-800-5599
Fax: 202-478-0303

Project Name and Address

MARYLAND AVENUE
Location: **1250 MARYLAND AVENUE SW**
WASHINGTON, DC 20024

Contractor:

BALFOUR BEATTY

Approved for Fabrication by:	Signature
------------------------------	-----------

Contract # **224009** Drawing # **E-09.02**

Contract Item: **LEVEL-03**
SLAB EXTENSION

Ref:
SOW-09: 3,4,5&6 / S307

Date 01/ 20/ 2025	Drawing Title: SOW #09 LEVEL-03 NEW SLAB EXTENSION SUPPORT SECTIONS
Scale VARIES	