


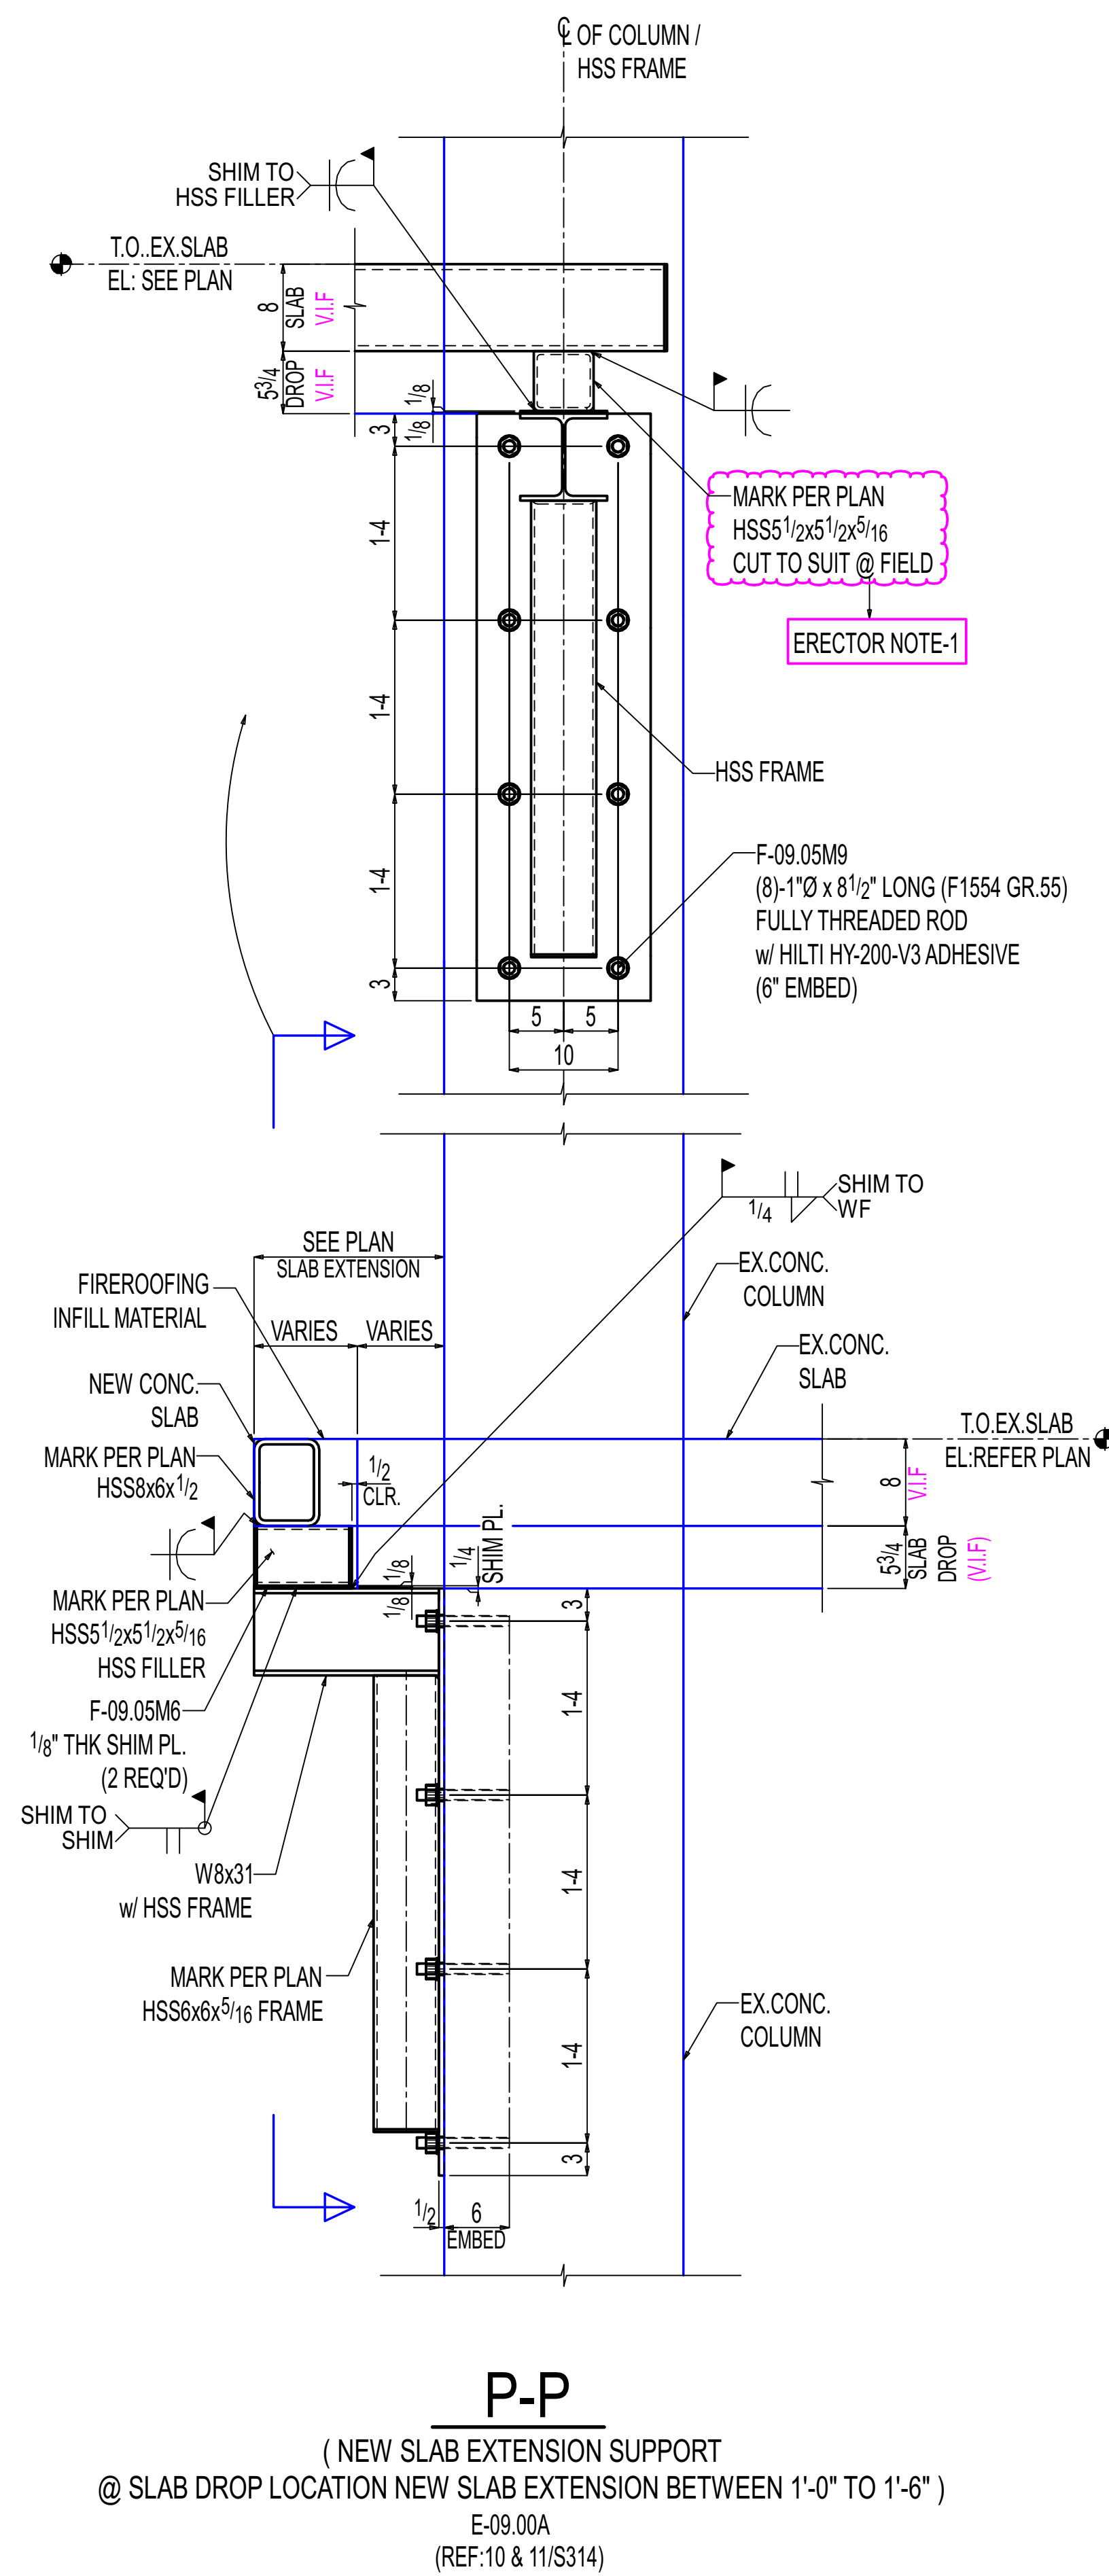


P-P
(NEW SLAB EXTENSION SUPPORT
@ SLAB DROP LOCATION NEW SLAB EXTENSION BETWEEN 1'-0" TO 1'-6")
E-09.00A
(REF: 10 & 11/S314)

OTHERS NOT SHOWN FOR CLARITY

ERECTOR NOTE-1:
ADJUST HSS DEPTH IN FIELD BY CUT THE HSS TO MATCH
EXISTING SLAB DROP THICKNESS, AND WELD TO THE
TOP OF HSS FRAME AT SITE PRIOR TO ERECTING THE HSS FRAME.


SHOP / ERECTOR NOTE:
LOCATE EXISTING REBAR PRIOR TO FABRICATION OF PLATE.
DO NOT DRILL THROUGH REBAR.

*** - ERECTOR NOTE:**
PROVIDE 1" NON-SHRINK GROUT x 12" LONG
CENTERED BENEATH AT PRECAST
ATTACHMENT POINTS.

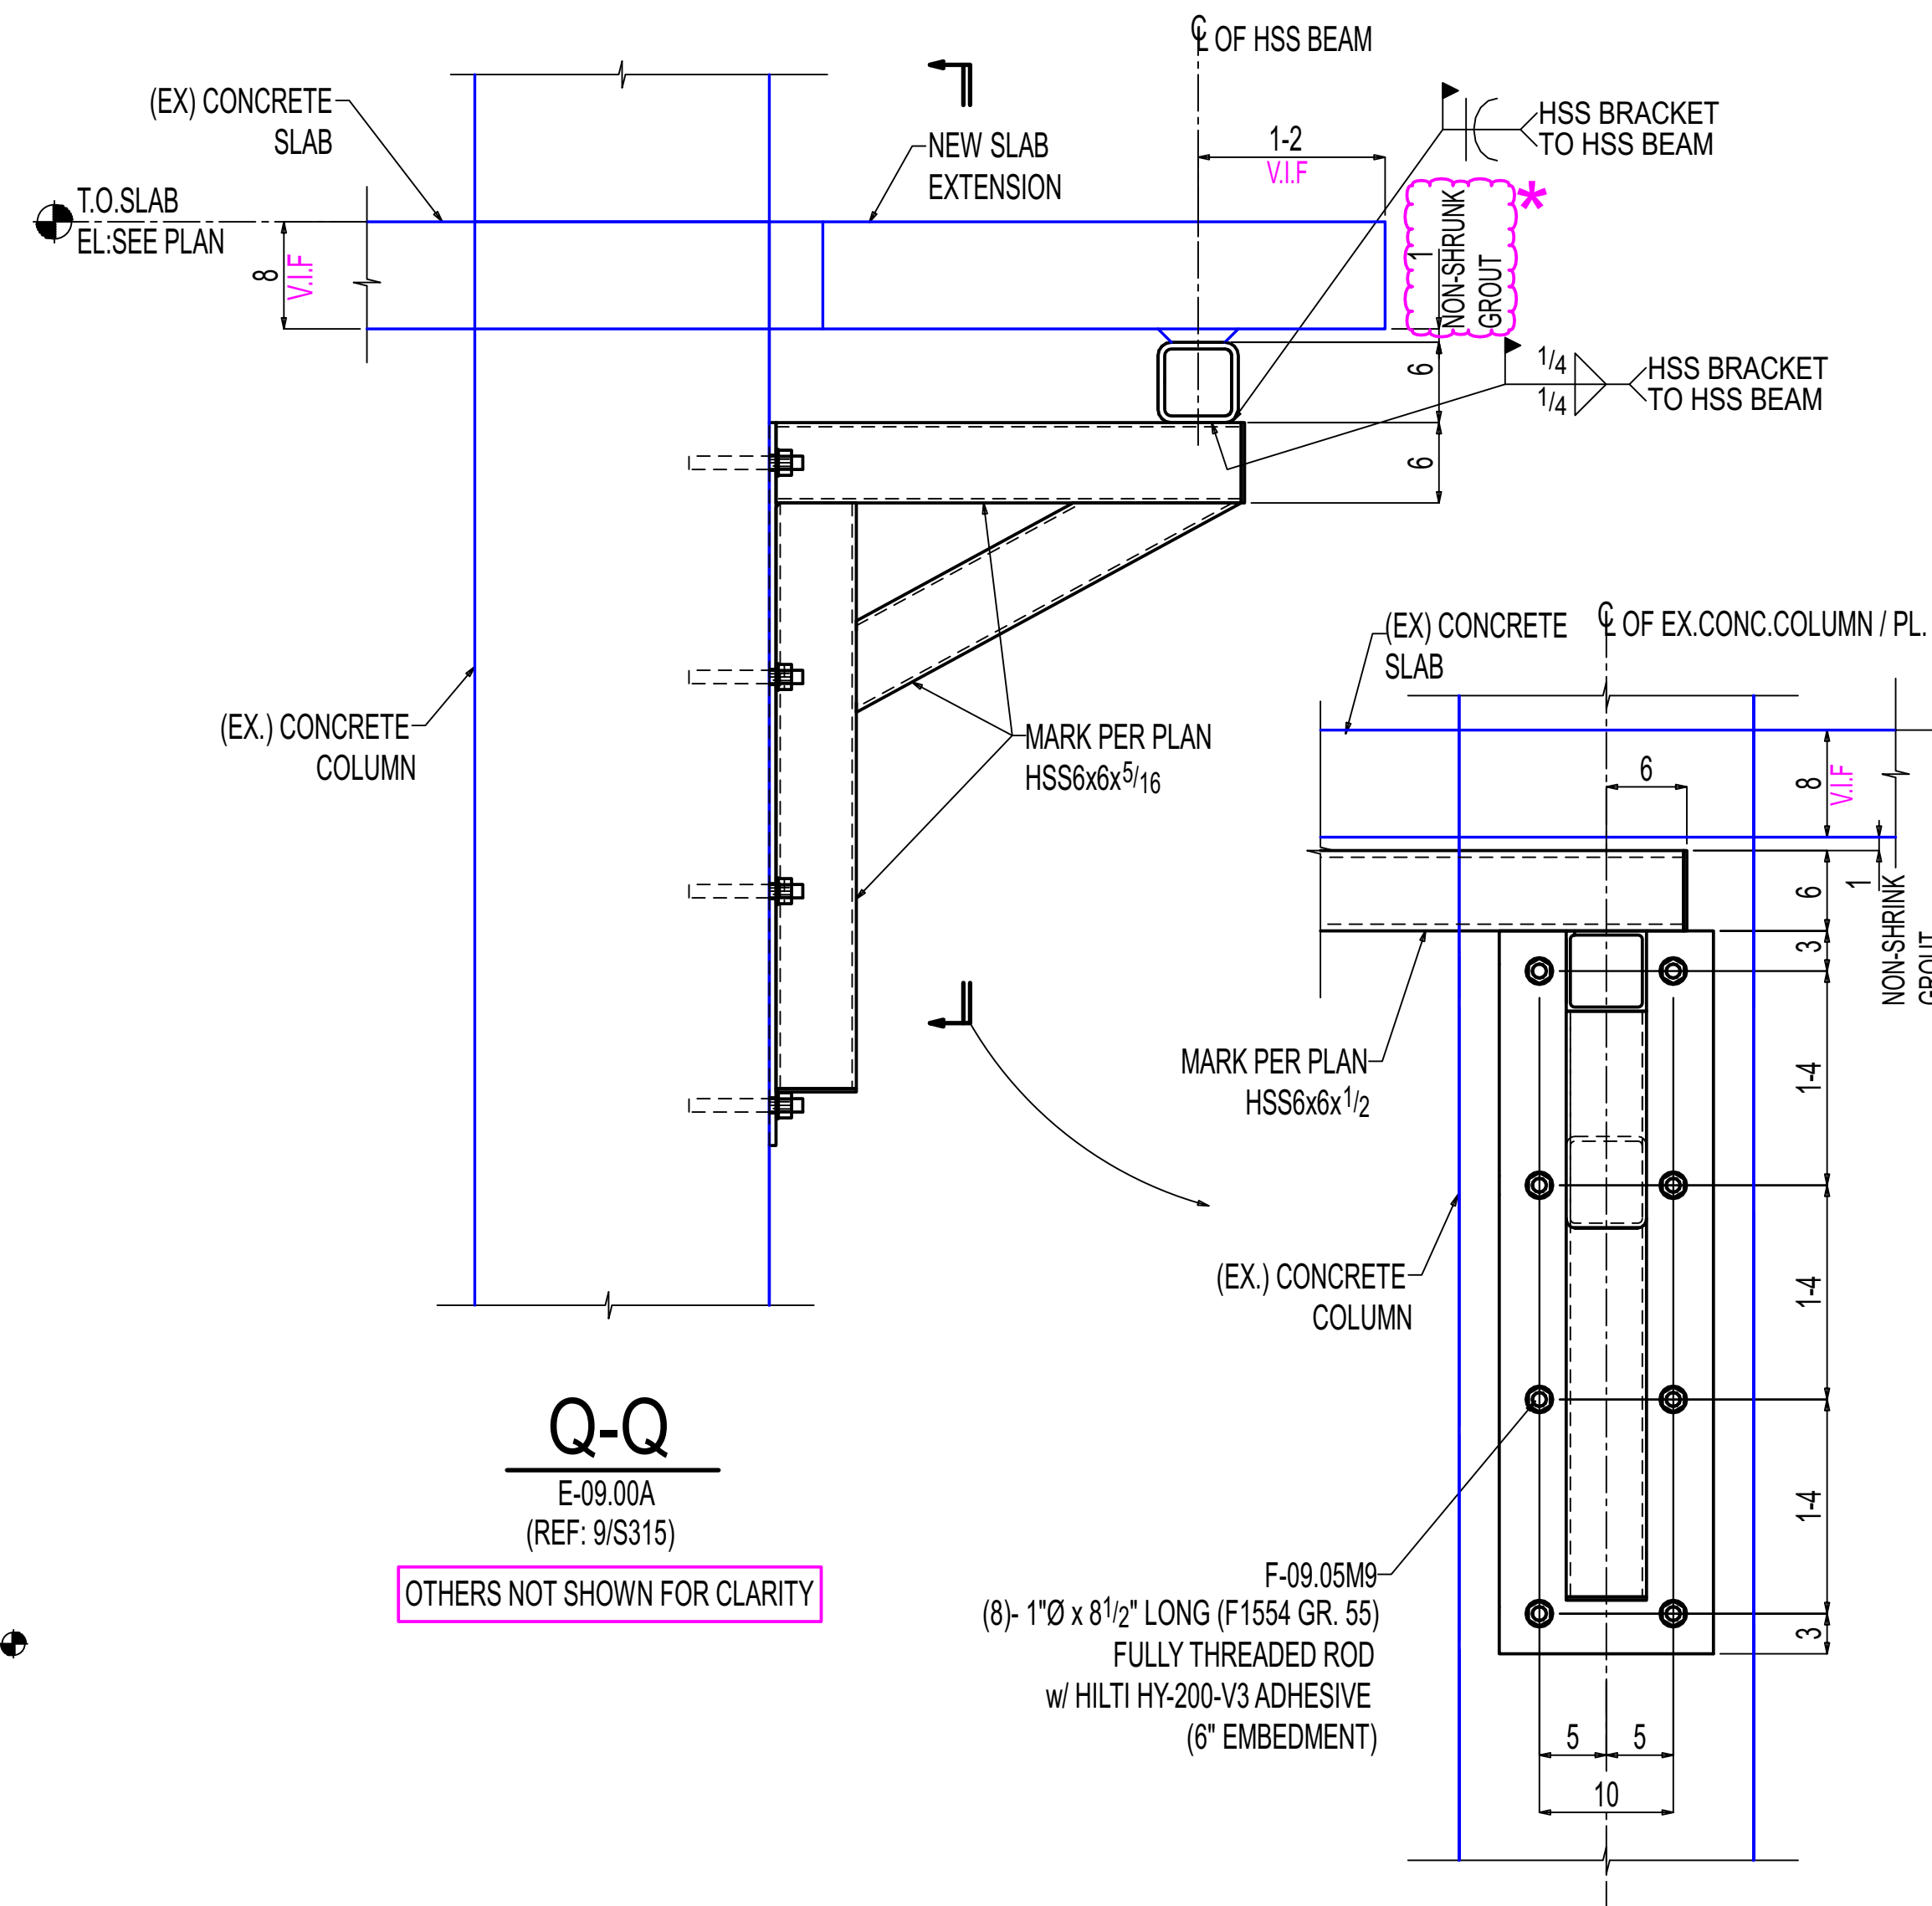


Q-Q
E-09.00A
(REF: 9/S315)

OTHERS NOT SHOWN FOR CLARITY

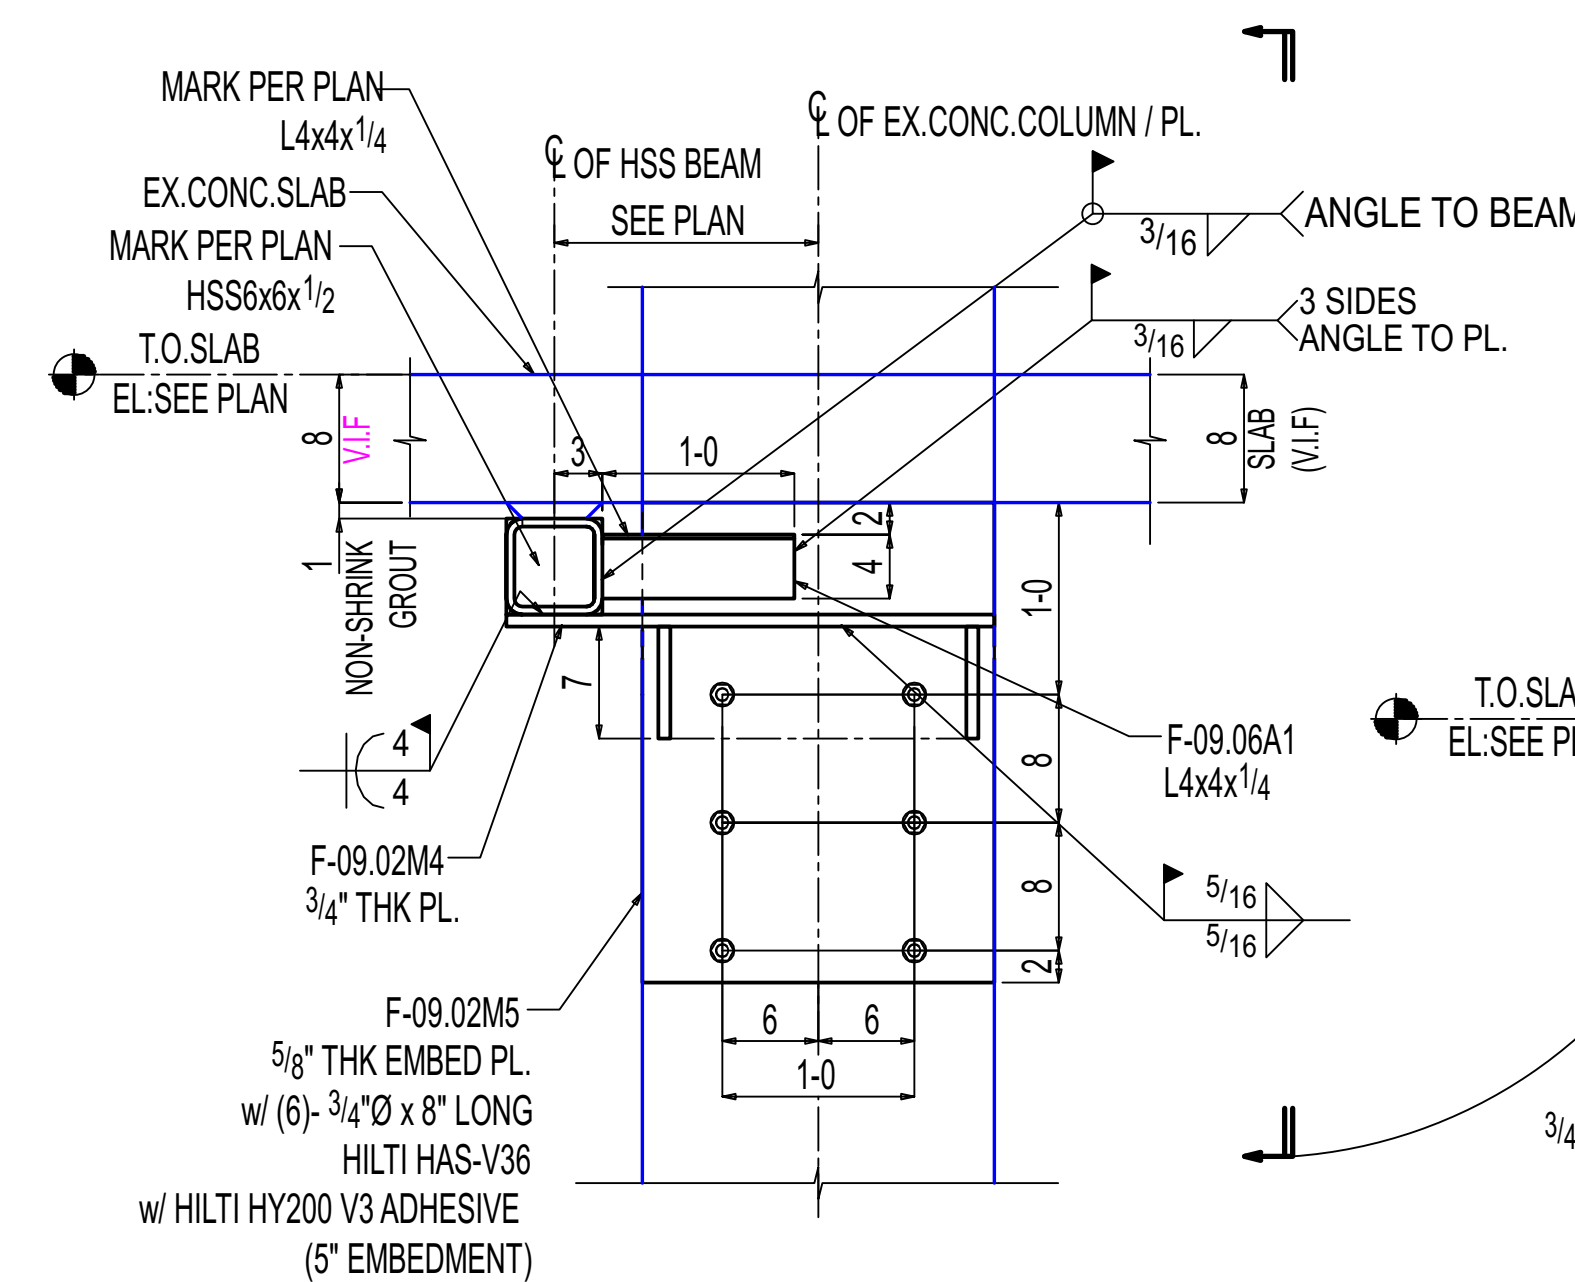

R-R
E-09.00A
(REF: 7/S316)

OTHERS NOT SHOWN FOR CLARITY

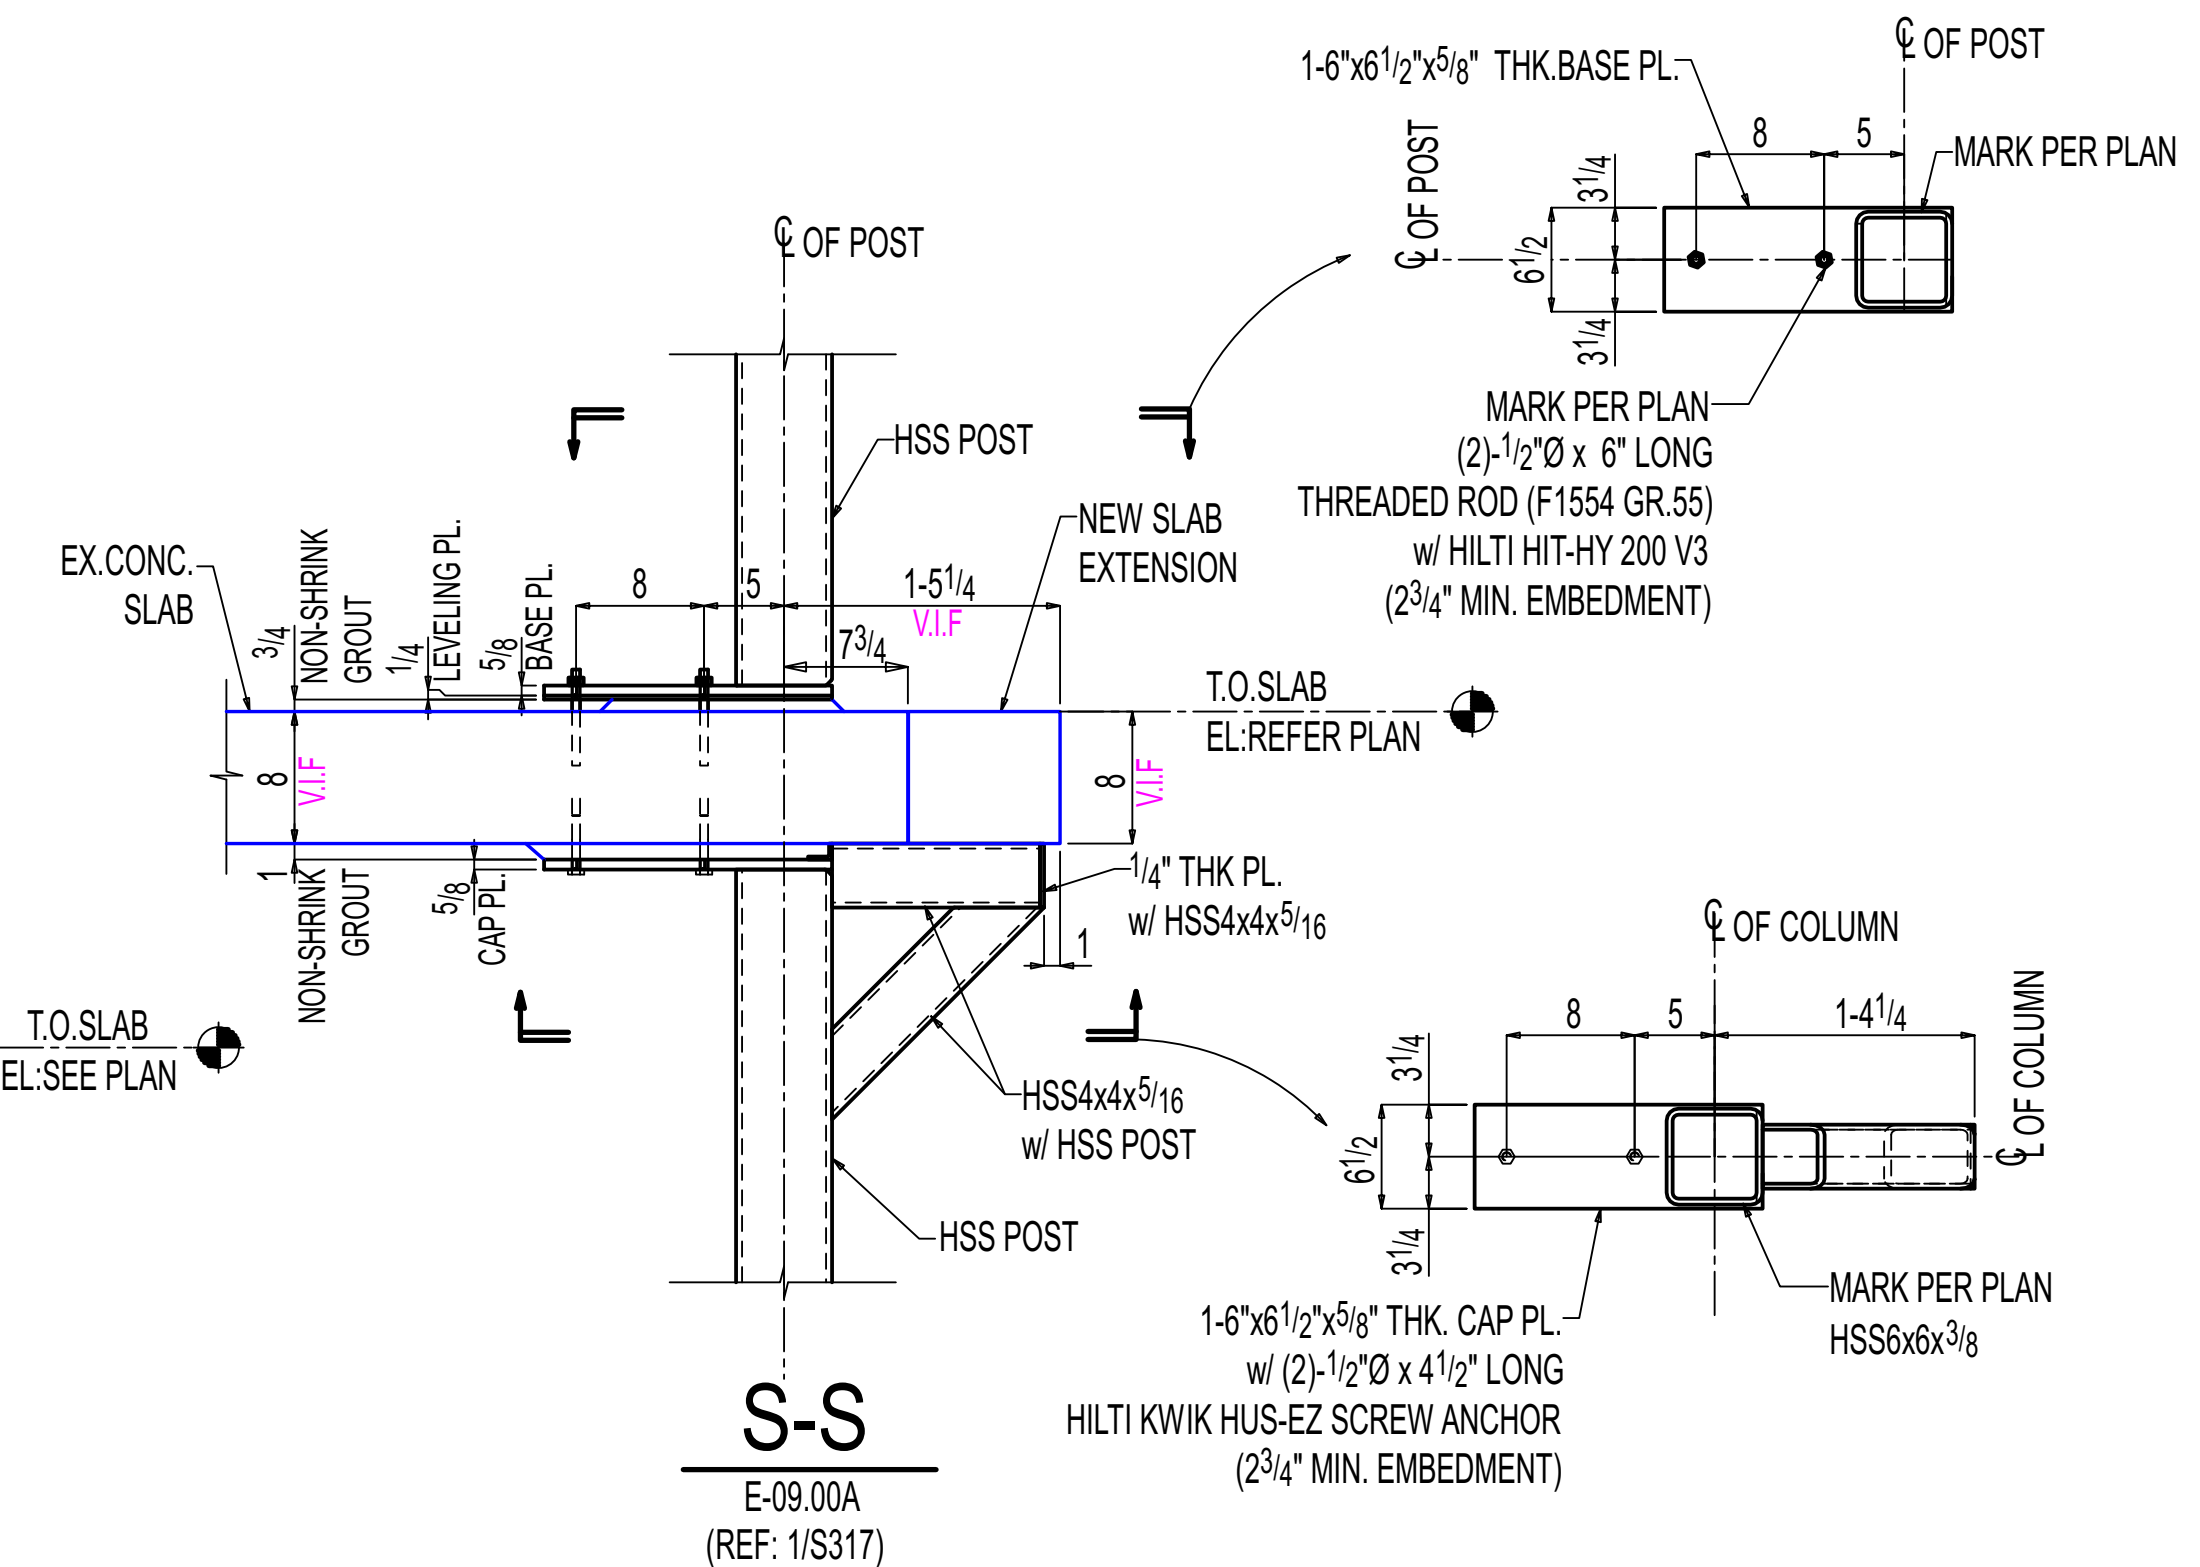

OTHERS NOT SHOWN FOR CLARITY

General Notes

- *Structural steel shall conform to ASTM-A992.
- *Structural SQR/RND tubing conform to ASTM A500 Grade C
- *Pipe shall conform to ASTM A53, Grade B.
- *Channels, Angles and plates shall conform to A36.
- *All bolts shall be 3/4" High strength in accordance with ASTM A325 (UNO)
- *Welding Electrodes for Carbon steel :E70xx

# of Copies	Revision/ Issue	Destination	Date
3	0	For Construction	11-14-2025
2	B	For Re-Approval	10-24-2025
1	A	For Approval	09-19-2025

IRON FABRICATION SERVICES, LLC.

3029 M. Street, NW, Suite 202
Washington, DC 20007
Tel: 202-800-5599
Fax: 202-478-0303

Project Name and Address
MARYLAND AVENUE

Location: **1250 MARYLAND AVENUE SW
WASHINGTON, DC 20024**

Contractor:
BALFOUR BEATTY

Approved for Fabrication by: Signature

Contract # **224009** Drawing # **E-09.04**

Contract Item: **LEVEL-03
SLAB EXTENSION**

Ref:
SOW-09: 3,4,5&6 / S307

Date
01/20/2025
Scale
VARIES
Drawing Title:
**SOW #09 LEVEL-03 NEW
SLAB EXTENSION SUPPORT
SECTIONS**