



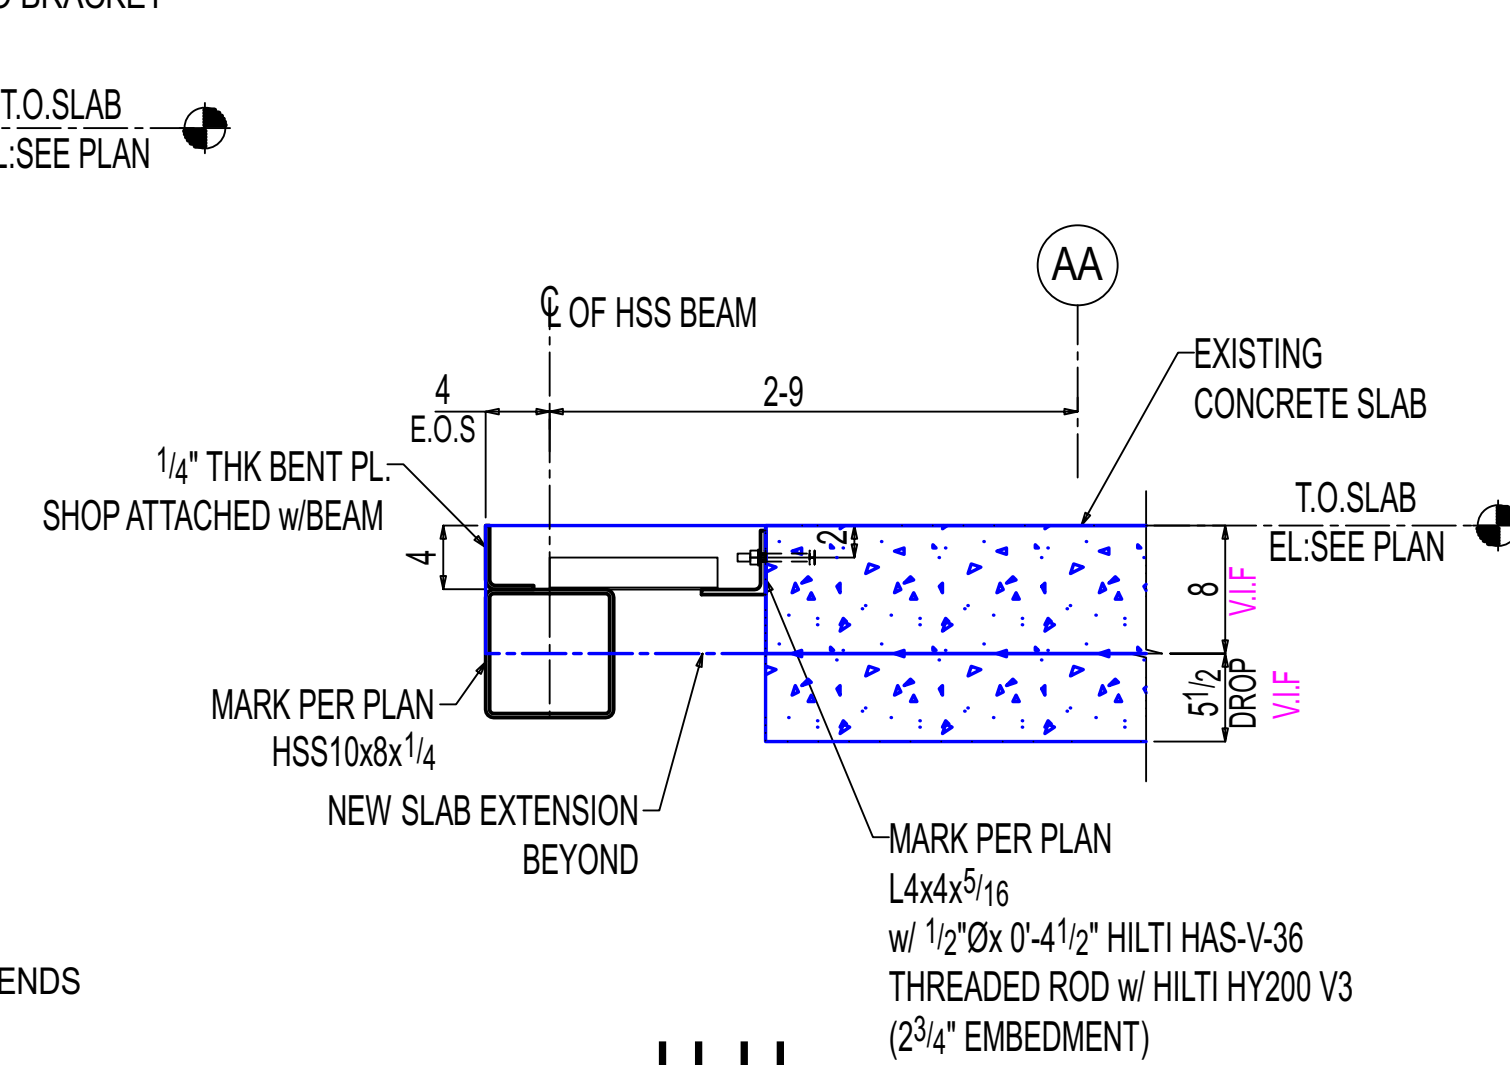

C. OF COLUMN /
 HSS FRAME
 EX. CONC.
 COLUMN
 T.O. EX. SLAB
 EL. REFER PLAN
 8
 V.I.F.
 5 1/2
 DROP
 V.I.F.
 3
 1.4
 1.4
 1.4
 3
 5
 5
 10
 EX. CONC.
 COLUMN
 HSS6x6x5/16
 w/ HSS FRAME
 F-09.05M9
 (8)-1"Ø x 8 1/2" LONG (F1554 GR. 55)
 FULLY THREADED ROD
 w/ HILTI HY-200 V3 ADHESIVE
 (6" EMBEDMENT)

OTHERS NOT SHOWN FOR CLARITY

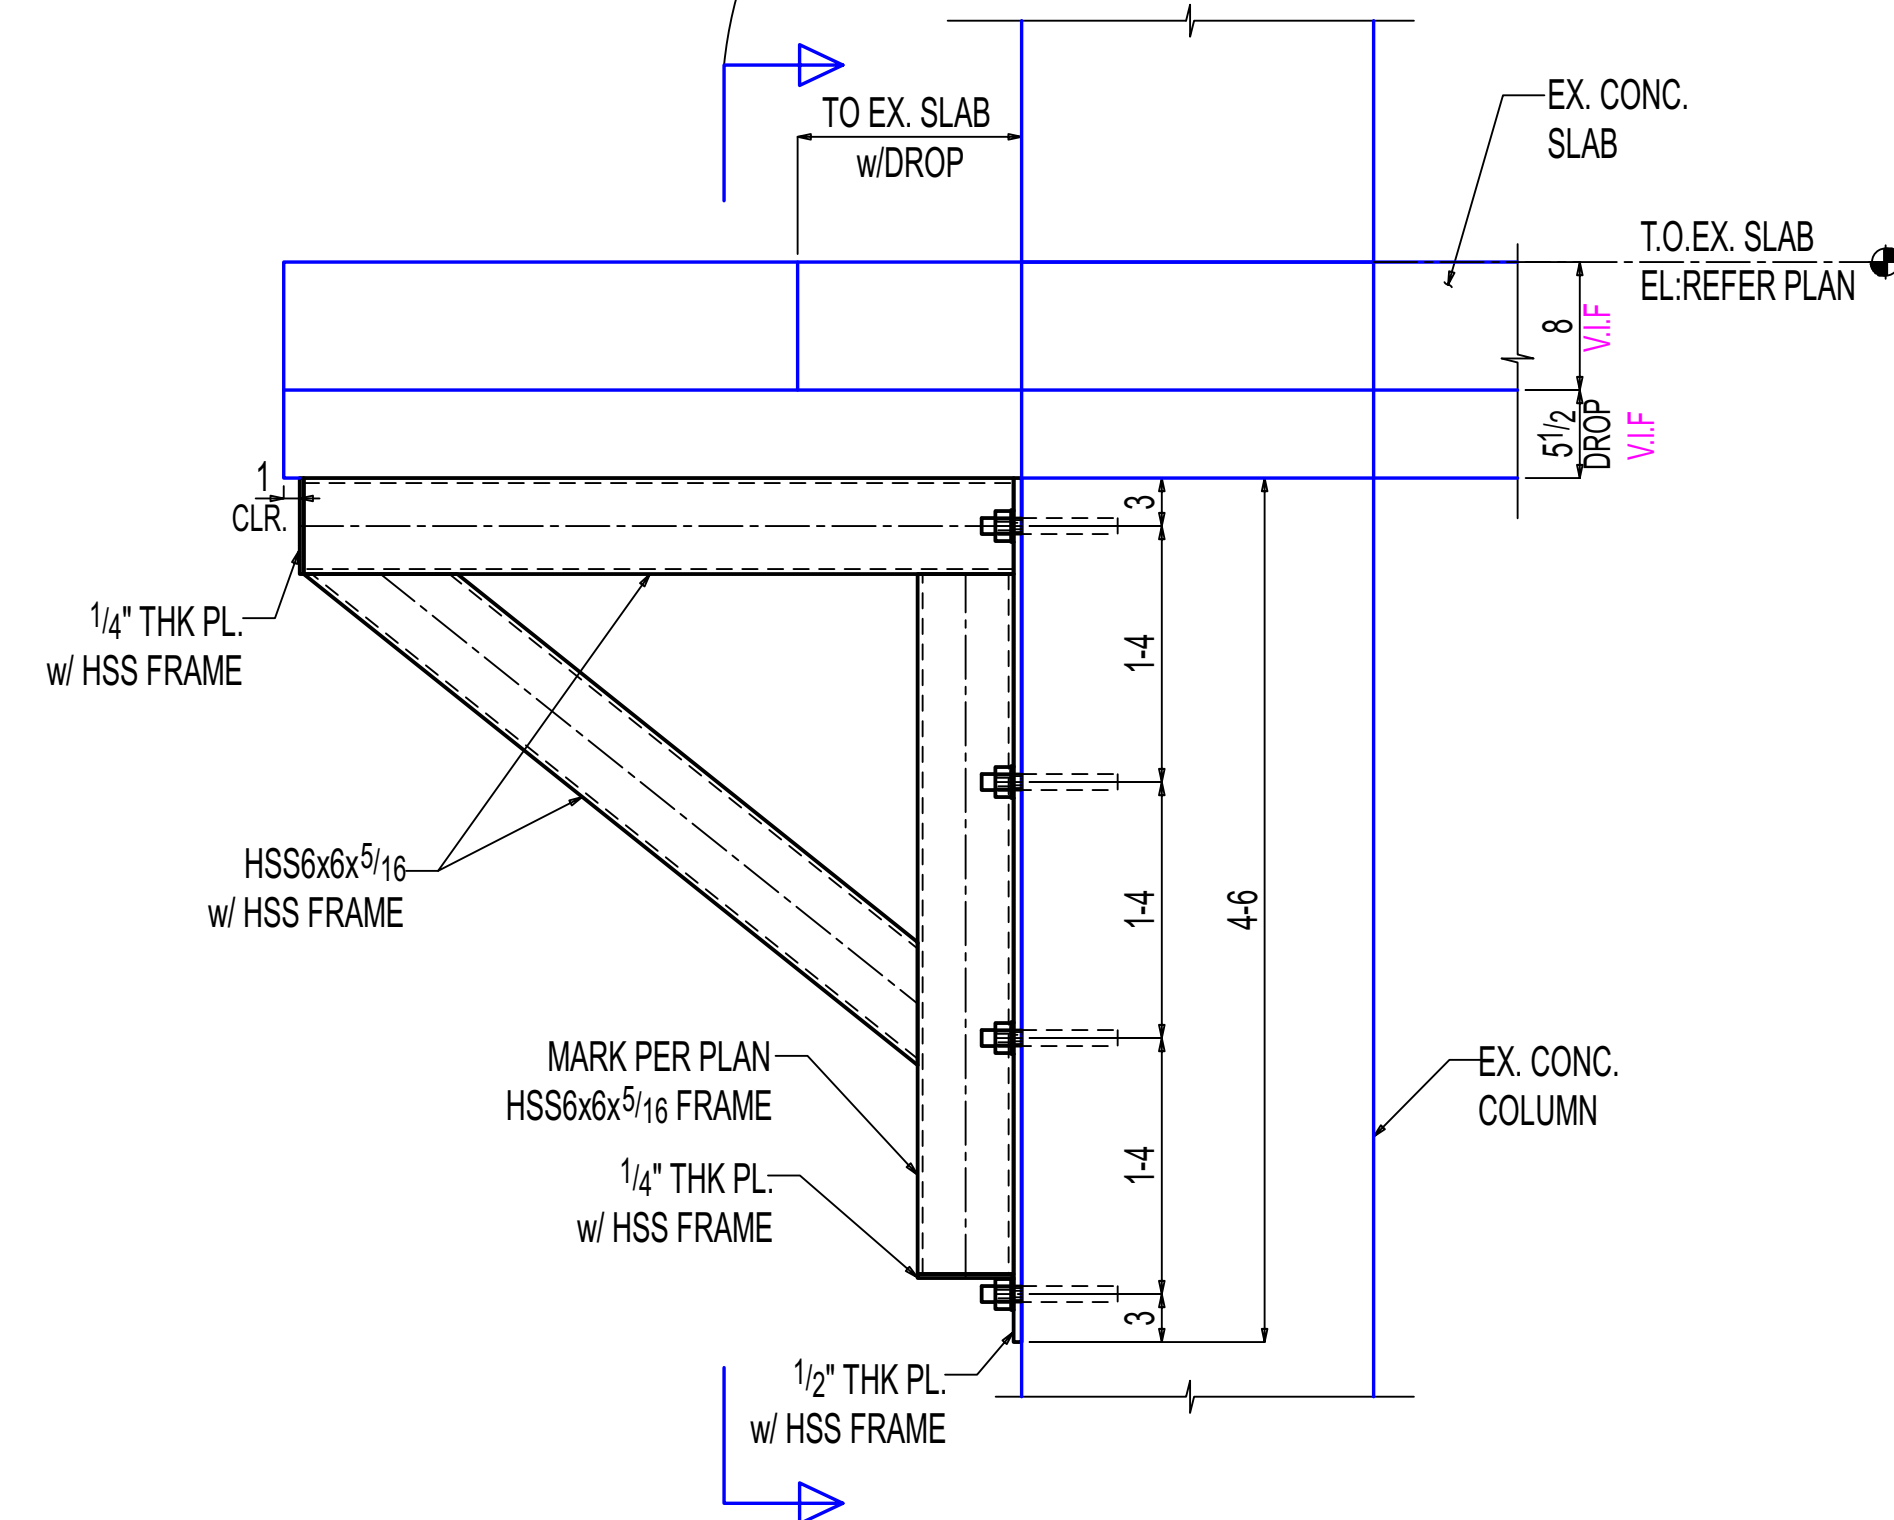

V-V
E-09.00A
(REF: 5/S316)

OTHERS NOT SHOWN FOR CLARITY

OTHERS NOT SHOWN FOR CLARITY

IRON FABRICATION SERVICES, LLC.

3029 M. Street, NW, Suite 202
Washington, DC 20007
Tel: 202-800-5599
Fax: 202-478-0303

Project Name and Address
MARYLAND AVENUE

Location: **1250 MARYLAND AVENUE SW**
WASHINGTON, DC 20024

Contractor: **BALFOUR BEATTY**

Approved for Fabrication by:	Signature

Contract # 224009		Drawing # E-09.05
Contract Item: LEVEL-03 SLAB EXTENSION		
Ref: SOW-09: 3,4,5&6 / S307		
Date 01/20/2025	Drawing Title: SOW #09 LEVEL-03 NEW SLAB EXTENSION SUPPORT SECTIONS	
Scale VARIES		