
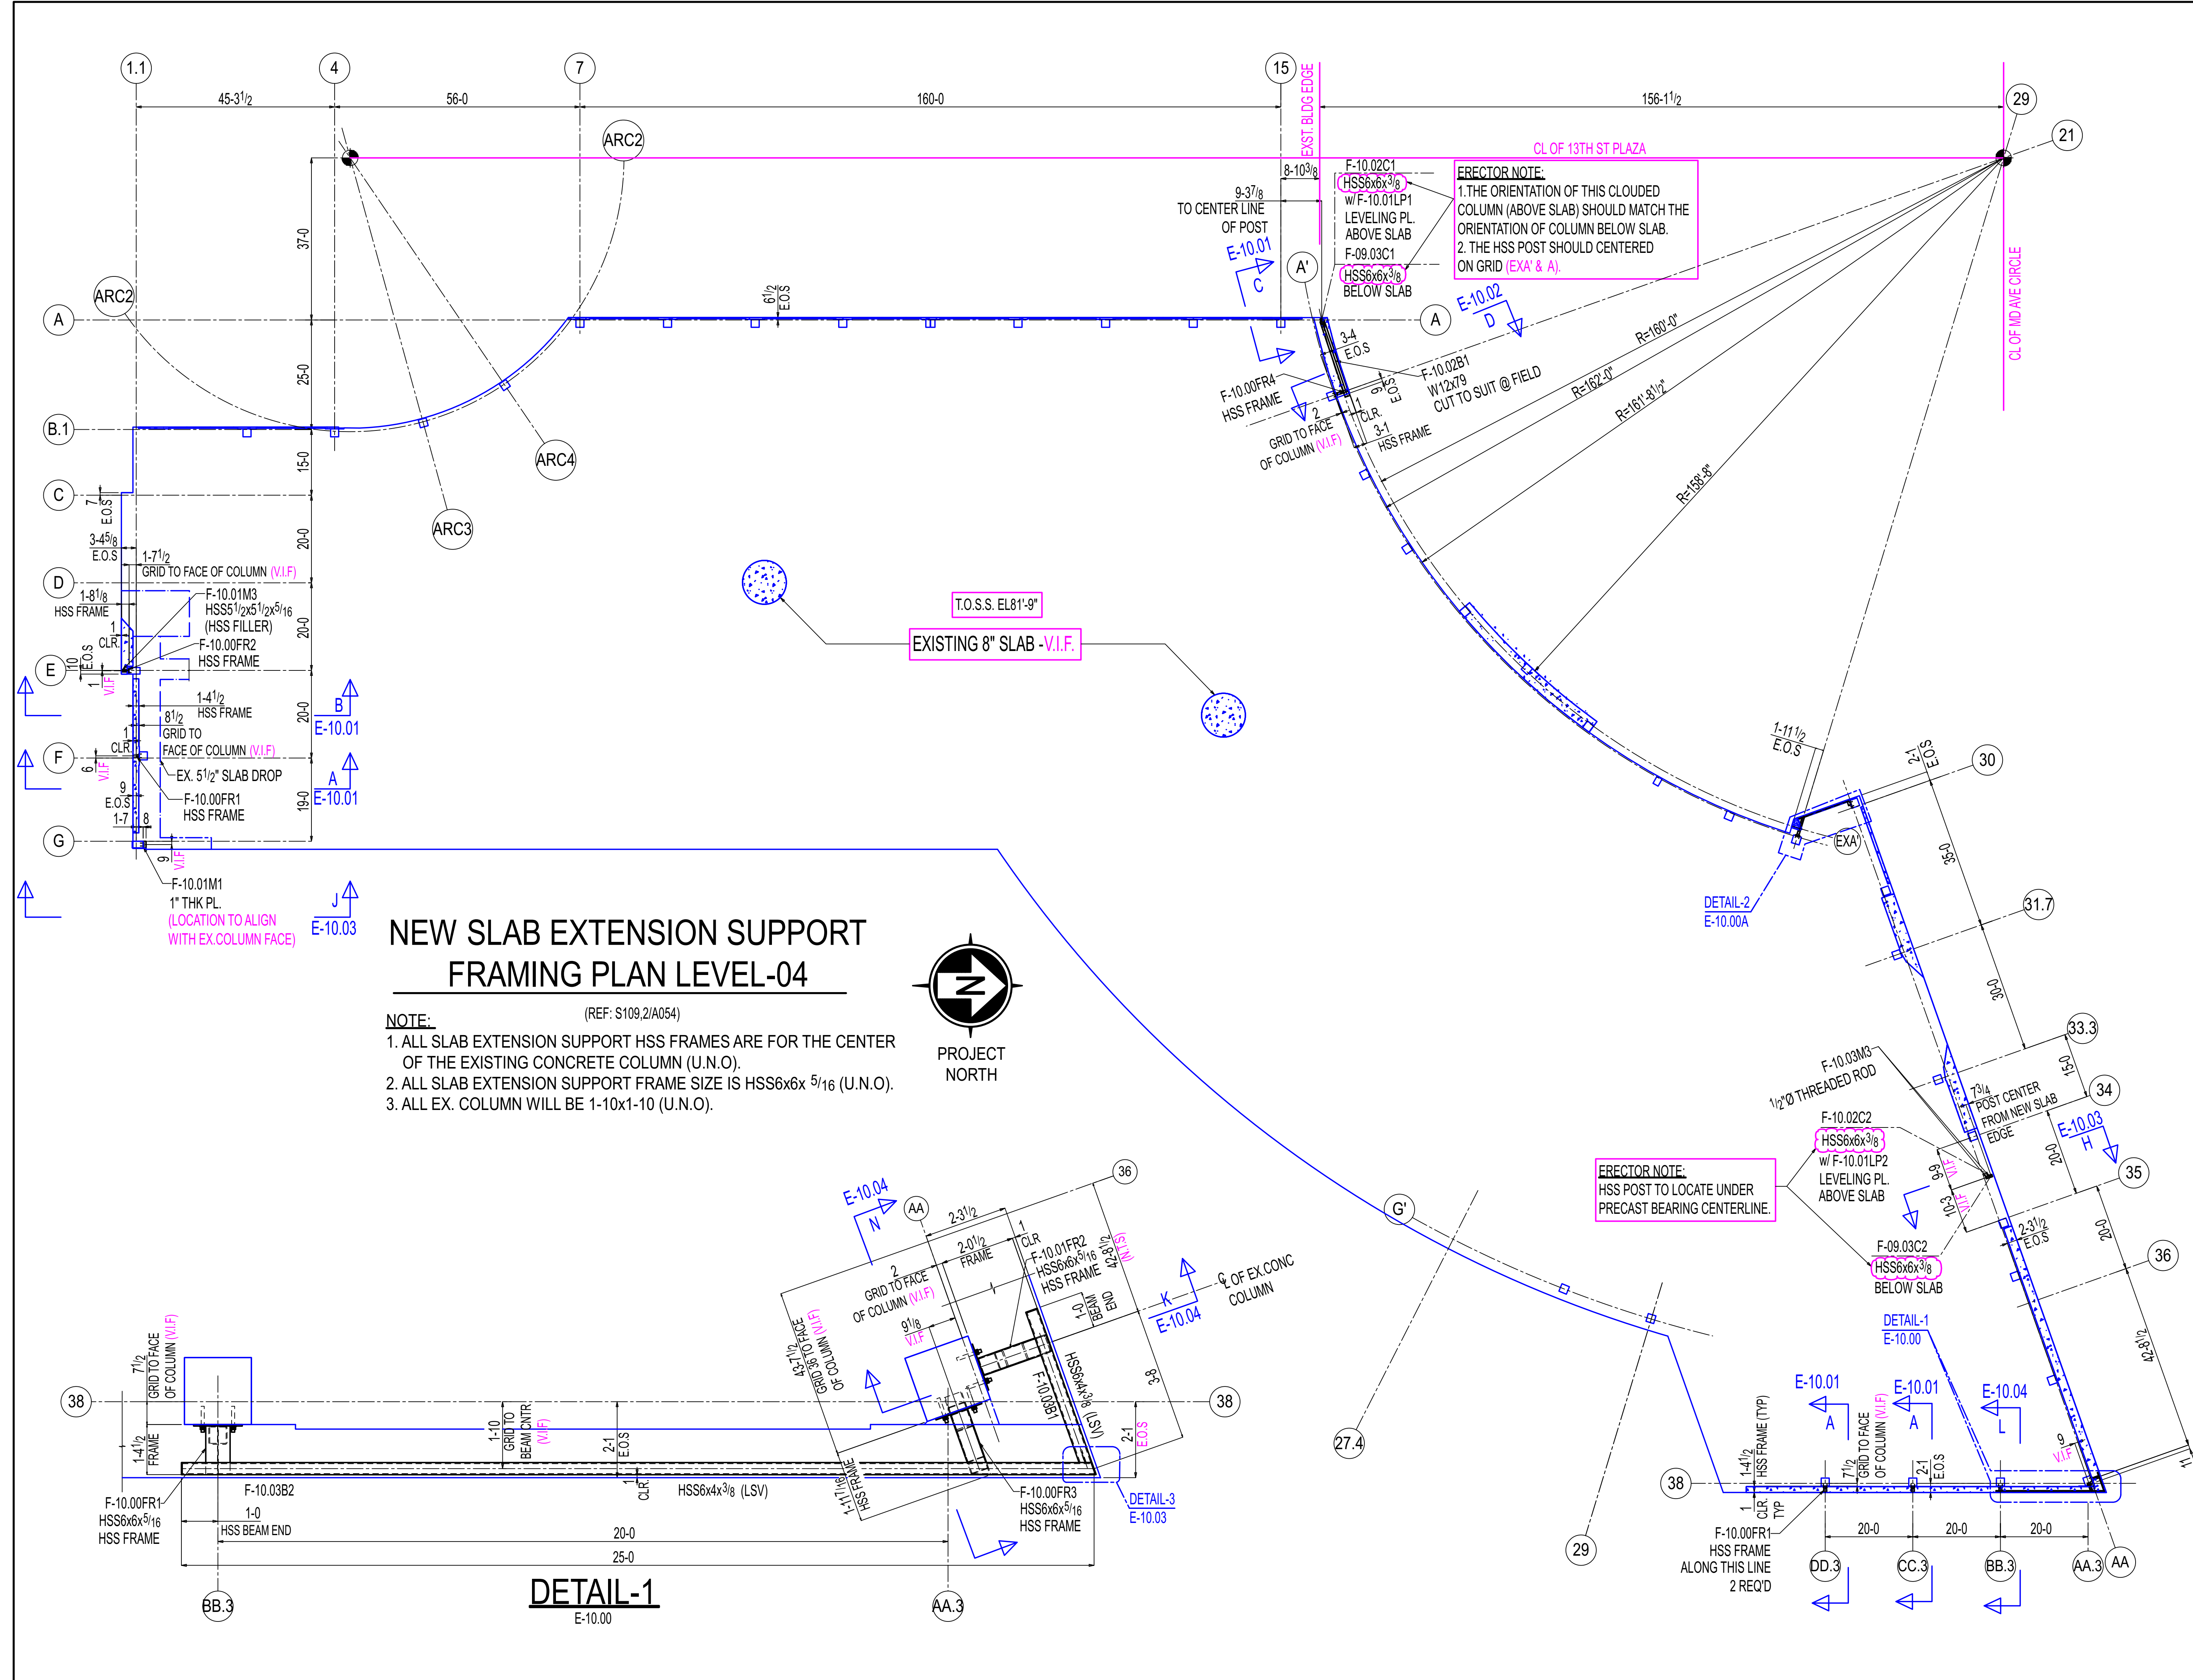


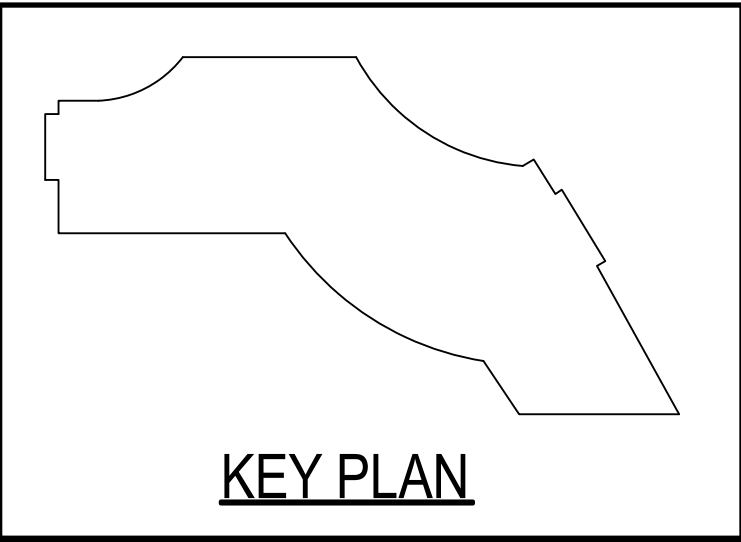

General Notes

- *Structural steel shall conform to ASTM-A992.
- *Structural SQR/RND tubing conform to ASTM A500 Grade C.
- *Pipe shall conform to ASTM A53, Grade B.
- *Channels, Angles and plates shall conform to A36.
- *All bolts shall be 3/4" High strength in accordance with ASTM A325 (UNO).
- *Welding Electrodes for Carbon steel :E70xx

# of Copies	Revision/ Issue	Destination	Date
5	0	For Construction	11-14-2025
4	D	For Re-Approval	10-24-2025
3	C	For Re-Approval	09-19-2025
2	B	For Re-Approval	06-23-2025
1	A	For Approval	02-25-2025

IRON FABRICATION SERVICES, LLC.

3029 M. Street, NW, Suite 202
Washington, DC 20007
Tel: 202-800-5599
Fax: 202-478-0303

Project Name and Address
MARYLAND AVENUE

Location: **1250 MARYLAND AVENUE SW
WASHINGTON, DC 20024**

Contractor:
BALFOUR BEATTY

Approved for Fabrication by: _____
Signature

Contract # **224009** Drawing # **E-10.00**

Contract Item: **LEVEL-04
SLAB EXTENSION**

Ref: **SOW-10: (S109,2/A054)**

Date
01/20/2025

Scale
VARIES

Drawing Title:
**SOW #10 LEVEL-04 NEW
SLAB EXTENSION SUPPORT
FRAMING PLAN**



E-10.00

OTHERS NOT SHOWN FOR CLARITY

General Notes

- *Structural steel shall conform to ASTM-A992.
- *Structural SQR/RND.tubing conform to ASTM A500 Grade C
- *Pipe shall conform to ASTM A53, Grade B.
- *Channels, Angles and plates shall conform to A36.
- *All bolts shall be $\frac{3}{4}$ " High strength in accordance with ASTM A325 (UNO)
- *Welding Electrodes for Carbon steel :E70xx

1	0	For Construction	11-14-2025
# of Copies	Revision/Issue	Destination	Date

IRON FABRICATION SERVICES, LLC.

3029 M. Street, NW, Suite 202
Washington, DC 20007
Tel: 202-800-5599
Fax: 202-478-0303

Project Name and Address
MARYLAND AVENUE

Location: **1250 MARYLAND AVENUE SW**
WASHINGTON, DC 20024

Contractor:

BALFOUR BEATTY

Approved for Fabrication by:

Signature

Contract # **224009**Drawing # **E-10.00A**

Contract Item:	LEVEL-04 SLAB EXTENSION
----------------	------------------------------------

Ref:


SOW-10: (S109,2/A054)

Date
01/20/2025

Drawing Title:


Scale
VARIES

**SOW #10 LEVEL-04
DETAIL VIEW**

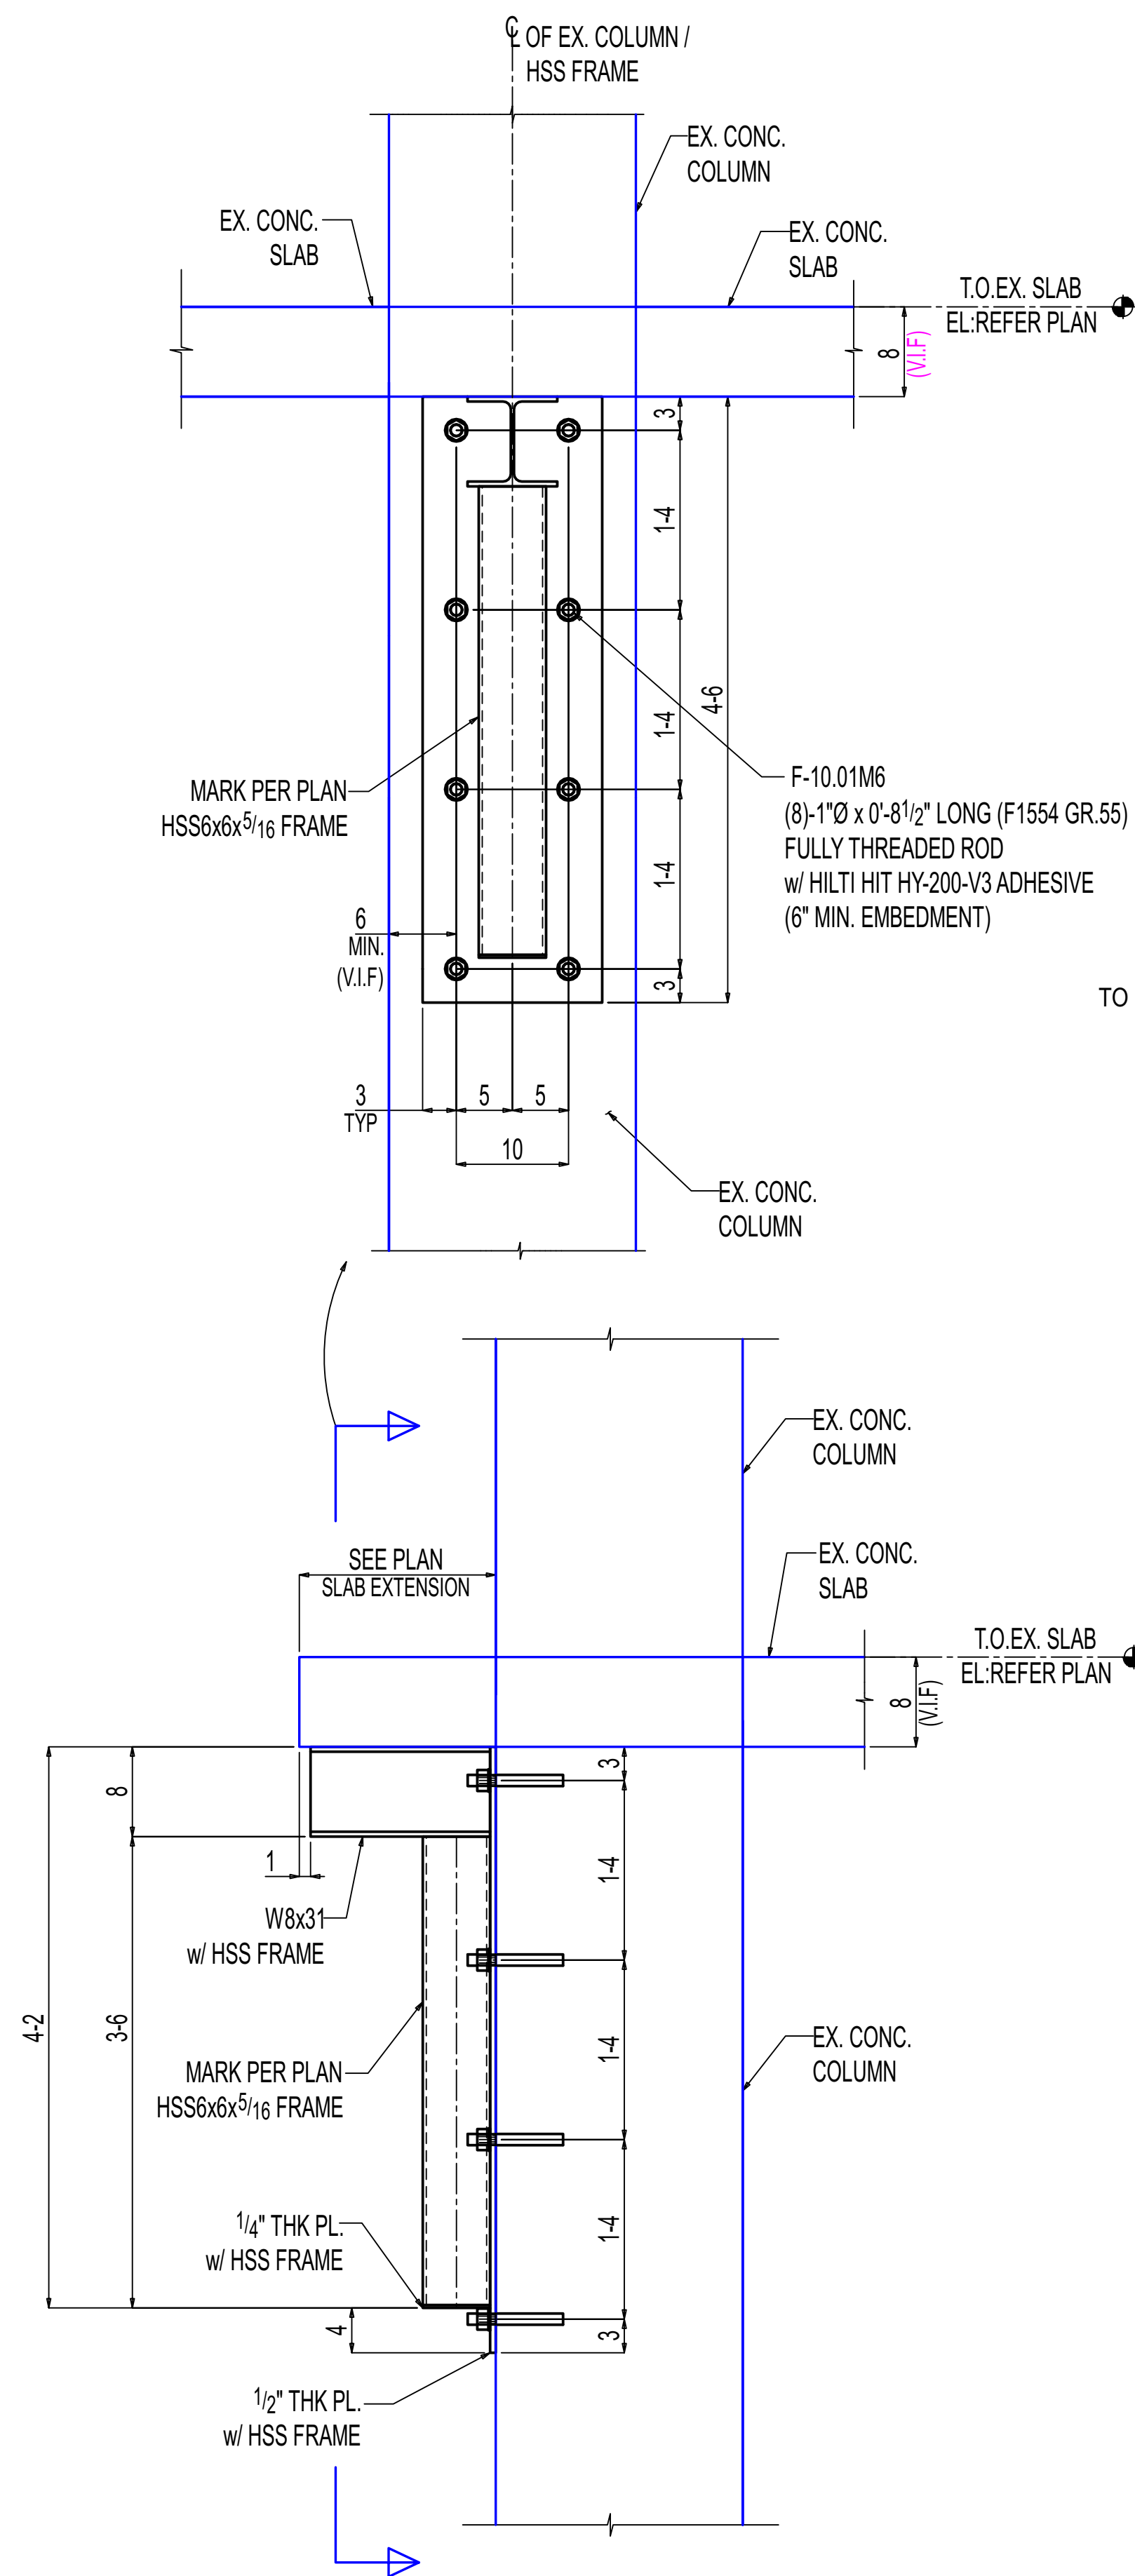


A-A
(NEW SLAB EXTENSION SUPPORT 1'-6" TO 3'-1")
E-10.00
(REF:11/S314)
OTHERS NOT SHOWN FOR CLARITY

SHOP / ERECTOR NOTE:
LOCATE EXISTING REBAR PRIOR TO FABRICATION OF PLATE.
DO NOT DRILL THROUGH REBAR.

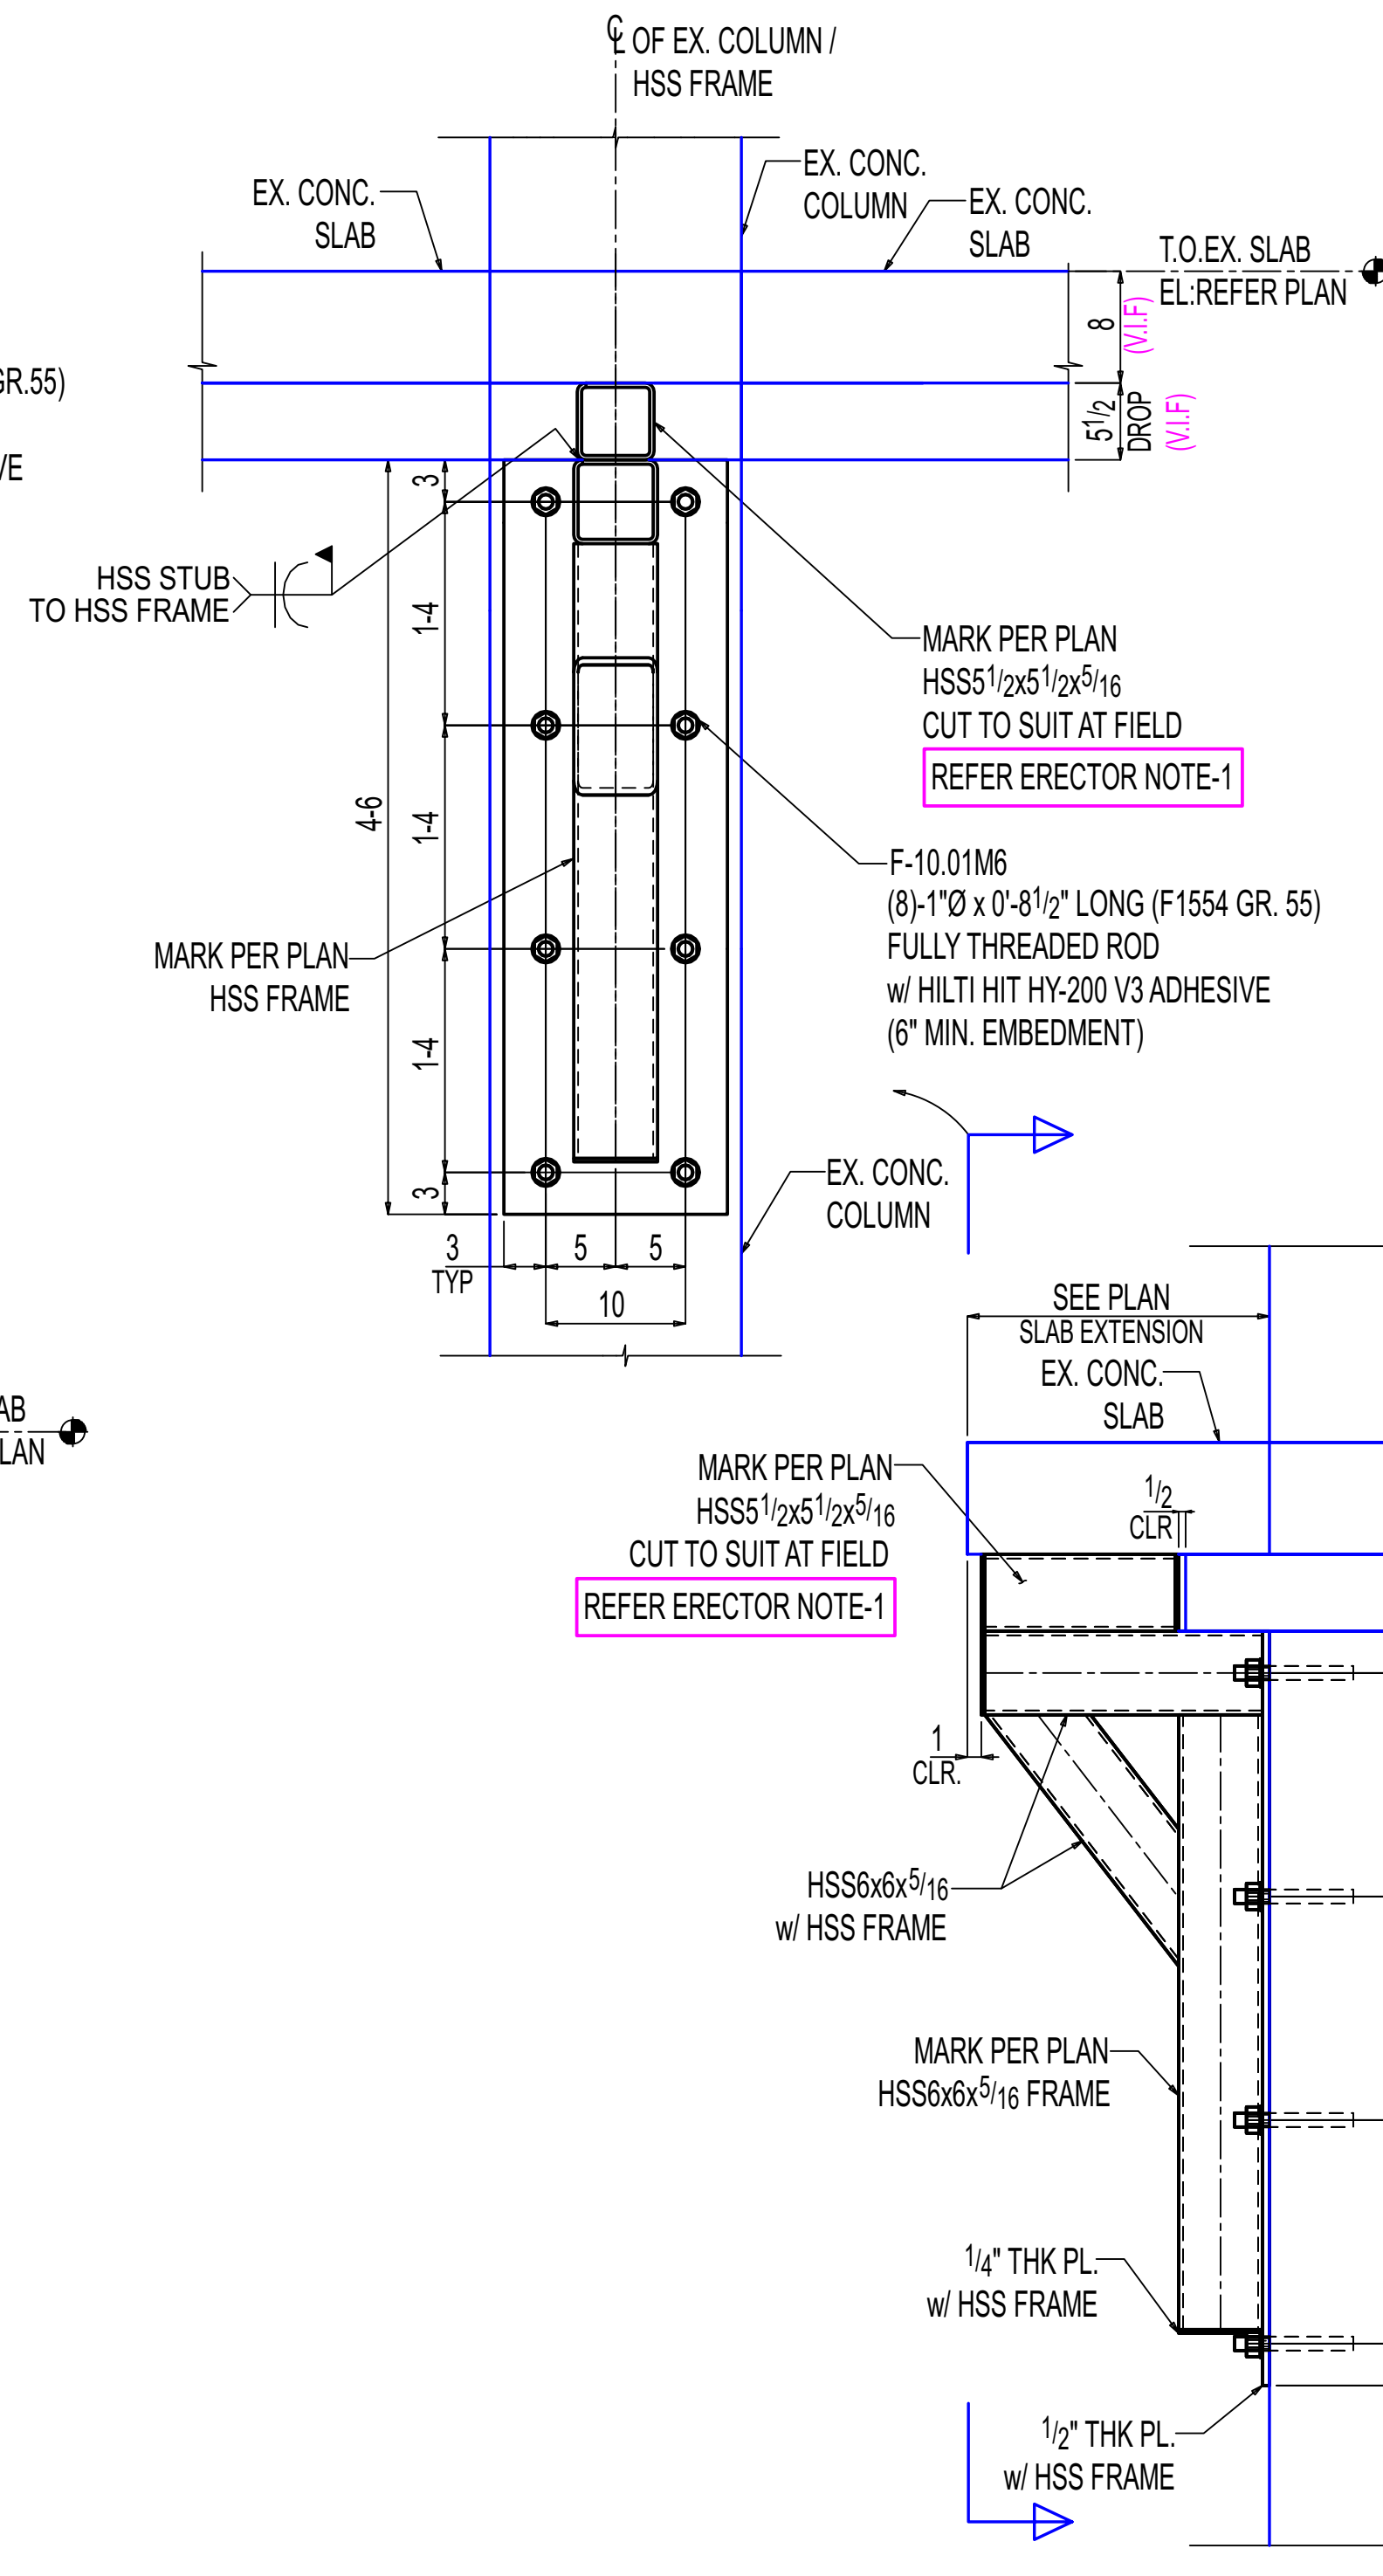

B-B
(NEW SLAB EXTENSION SUPPORT 1'-6" TO 3'-1")
E-10.00
(REF:3 & 4/S307)
OTHERS NOT SHOWN FOR CLARITY

ERECTOR NOTE-1:
ADJUST HSS DEPTH BY FIELD CUTTING TO MATCH
EXISTING SLAB DROP THICKNESS, AND WELD TO THE
TOP OF HSS FRAME AT SITE PRIOR TO ERECTING THE HSS FRAME.

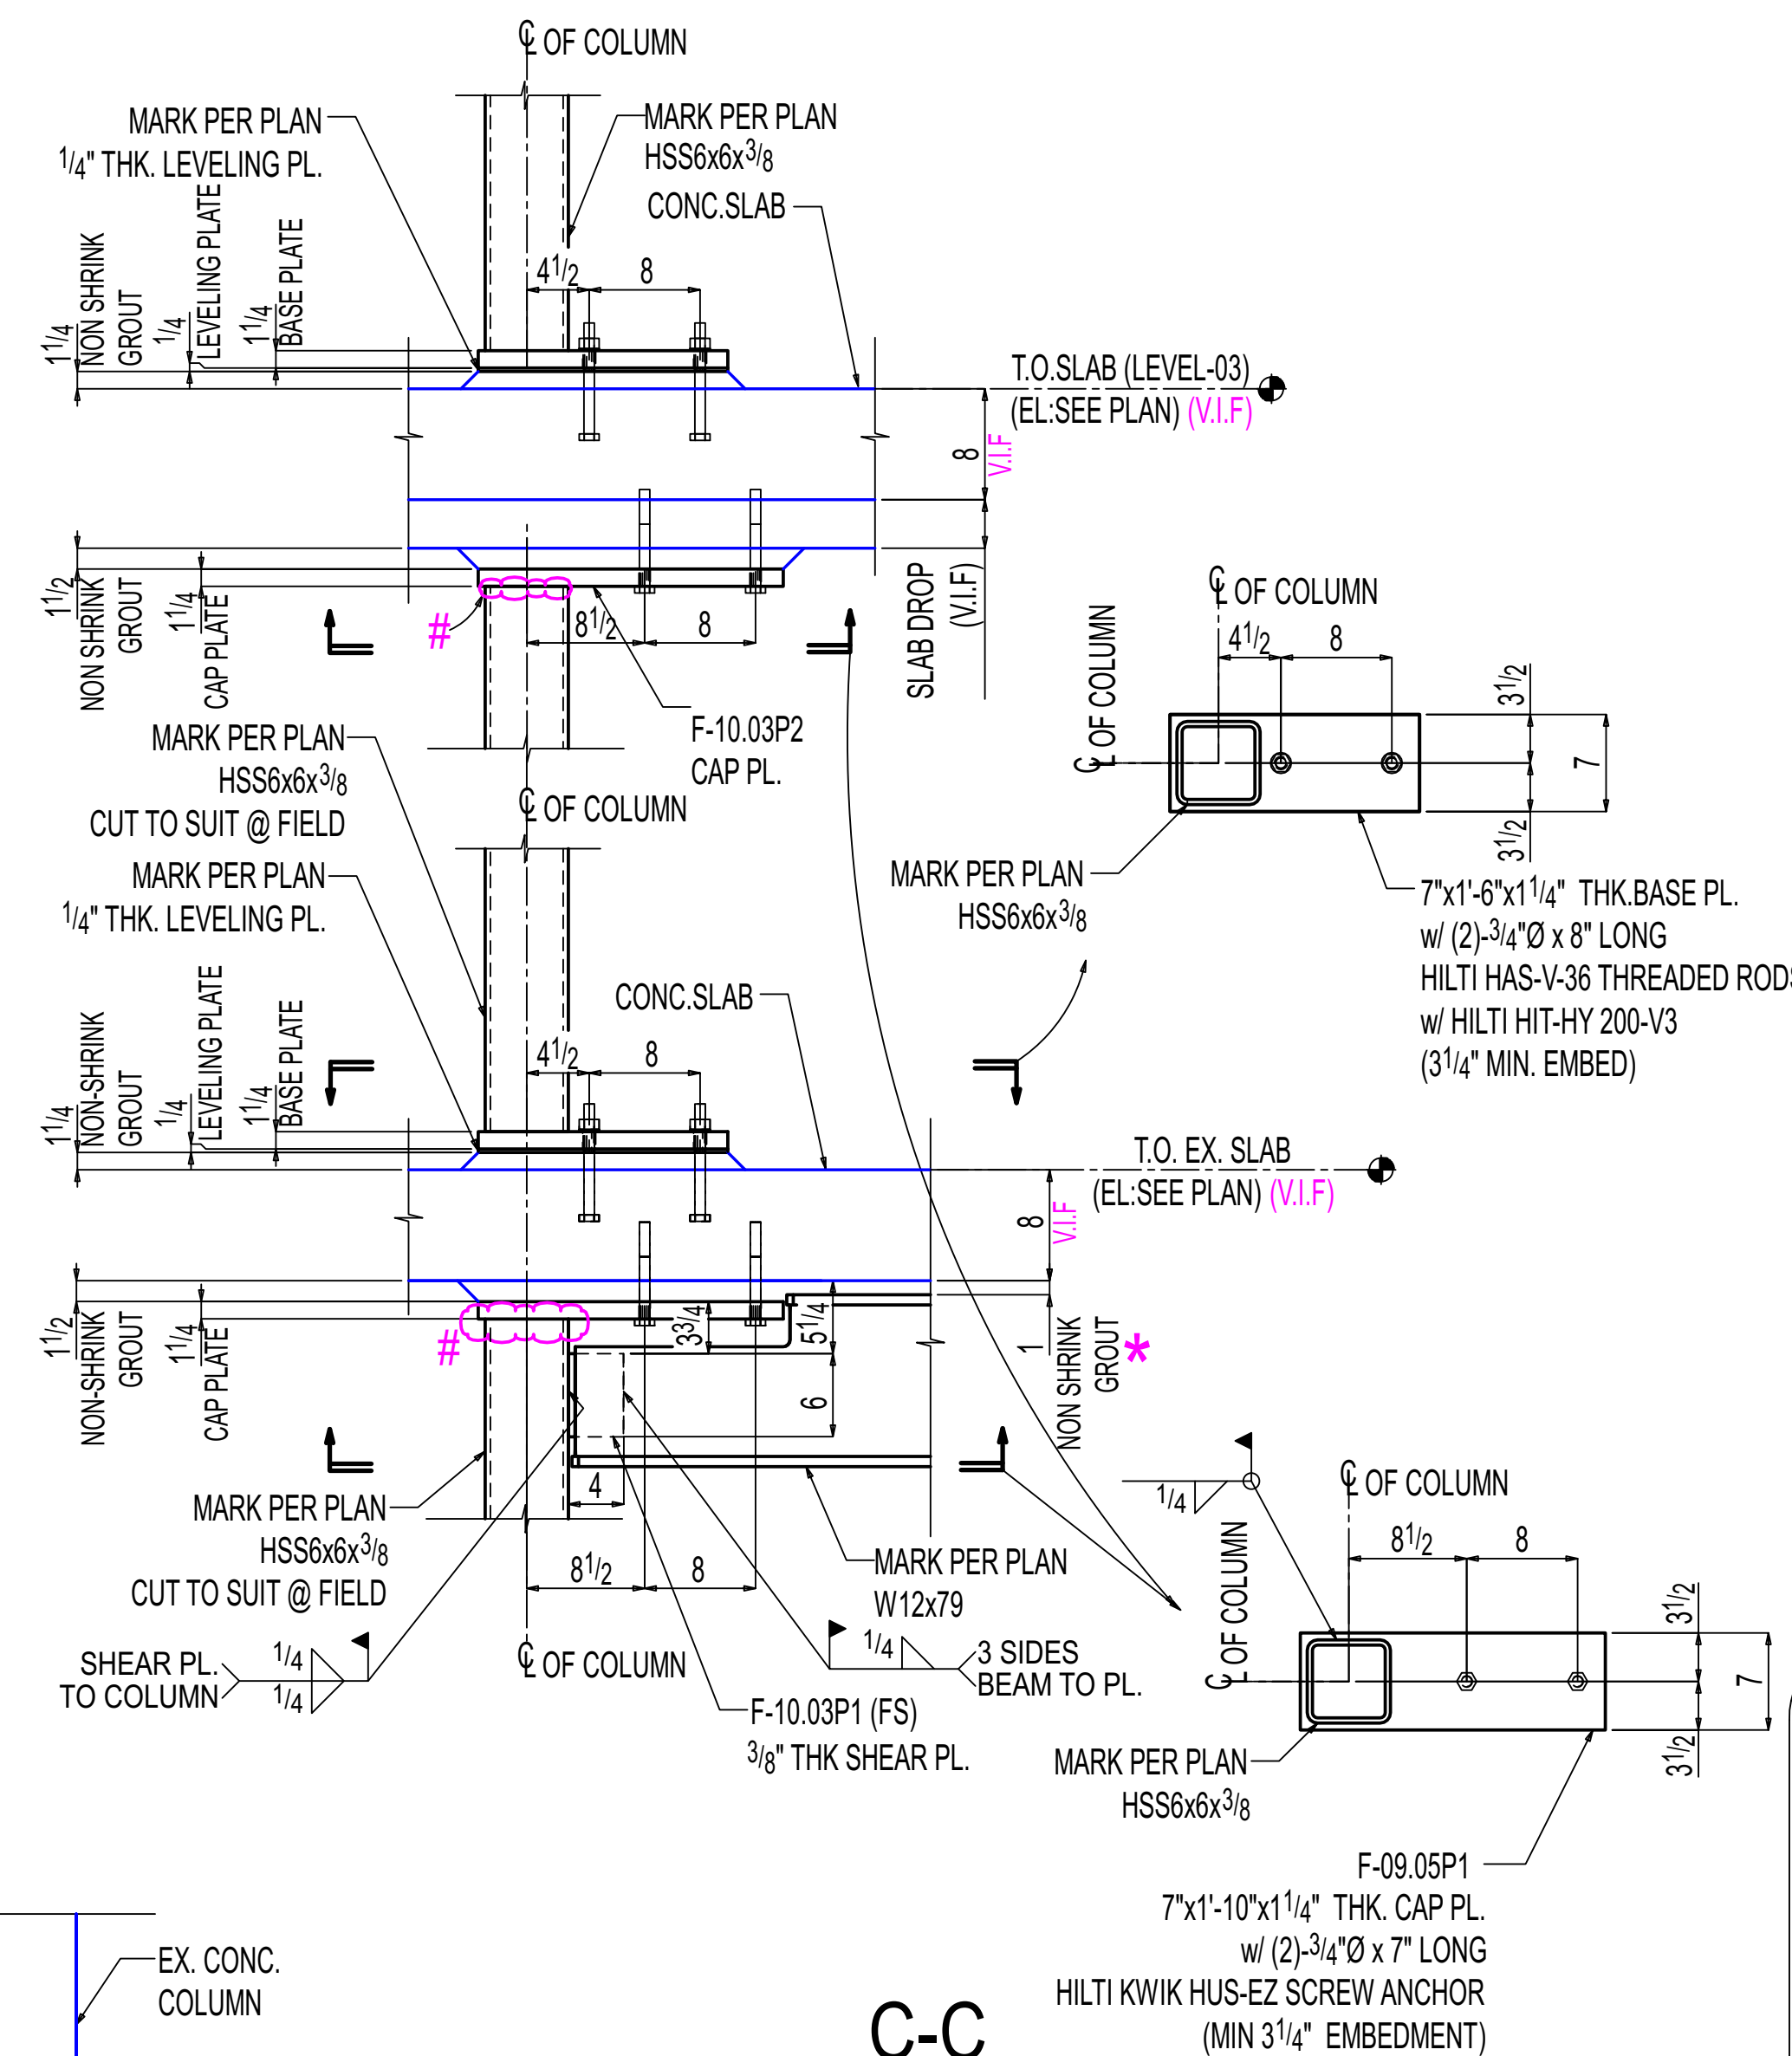

C-C
(NEW SLAB EXTENSION SUPPORT 1'-6" TO 3'-1")
E-10.00
(REF:7/S314)
OTHERS NOT SHOWN FOR CLARITY

ERECTOR NOTE:
ALL # INDICATED COLUMN ENDS TO BE CUT TO SUIT @ FIELD
BASED ON FLOOR TO FLOOR CLEARANCE AND WELD IT TO THE CAP PLATE.

*** - ERECTOR NOTE:**
PROVIDE 1" NON-SHRINK GROUT x 12" LONG
CENTERED BENEATH AT PRECAST
ATTACHMENT POINTS.

General Notes

- *Structural steel shall conform to ASTM-A992.
- *Structural SQR/RND tubing conform to ASTM A500 Grade C
- *Pipe shall conform to ASTM A53, Grade B.
- *Channels, Angles and plates shall conform to A36.
- *All bolts shall be 3/4" High strength in accordance with ASTM A325 (UNO)
- *Welding Electrodes for Carbon steel :E70xx

# of Copies	Revision/ Issue	Destination	Date
5	0	For Construction	11-14-2025
4	D	For Re-Approval	10-24-2025
3	C	For Re-Approval	09-19-2025
2	B	For Re-Approval	06-23-2025
1	A	For Approval	02-25-2025

IRON FABRICATION SERVICES, LLC.

3029 M. Street, NW, Suite 202
Washington, DC 20007
Tel: 202-800-5599
Fax: 202-478-0303

Project Name and Address
MARYLAND AVENUE

Location: **1250 MARYLAND AVENUE SW
WASHINGTON, DC 20024**

Contractor:
BALFOUR BEATTY

Approved for Fabrication by: _____
Signature

Contract # **224009** Drawing # **E-10.01**



Contract Item: **LEVEL-04
SLAB EXTENSION**

Ref: **SOW-10: 3,4,5&6 / S307**

Date **01/20/2025** Drawing Title:
**SOW #10 LEVEL-04 NEW
SLAB EXTENSION SUPPORT
SECTIONS**
Scale
VARIES

* - ERECTOR NOTE:
PROVIDE 1" NON-SHRINK GROUT x 12" LONG
CENTERED BENEATH AT PRECAST
ATTACHMENT POINTS.

ERECTOR NOTE:
FIELD TRIM AS REQUIRED AT CLOUDED BEAM END.

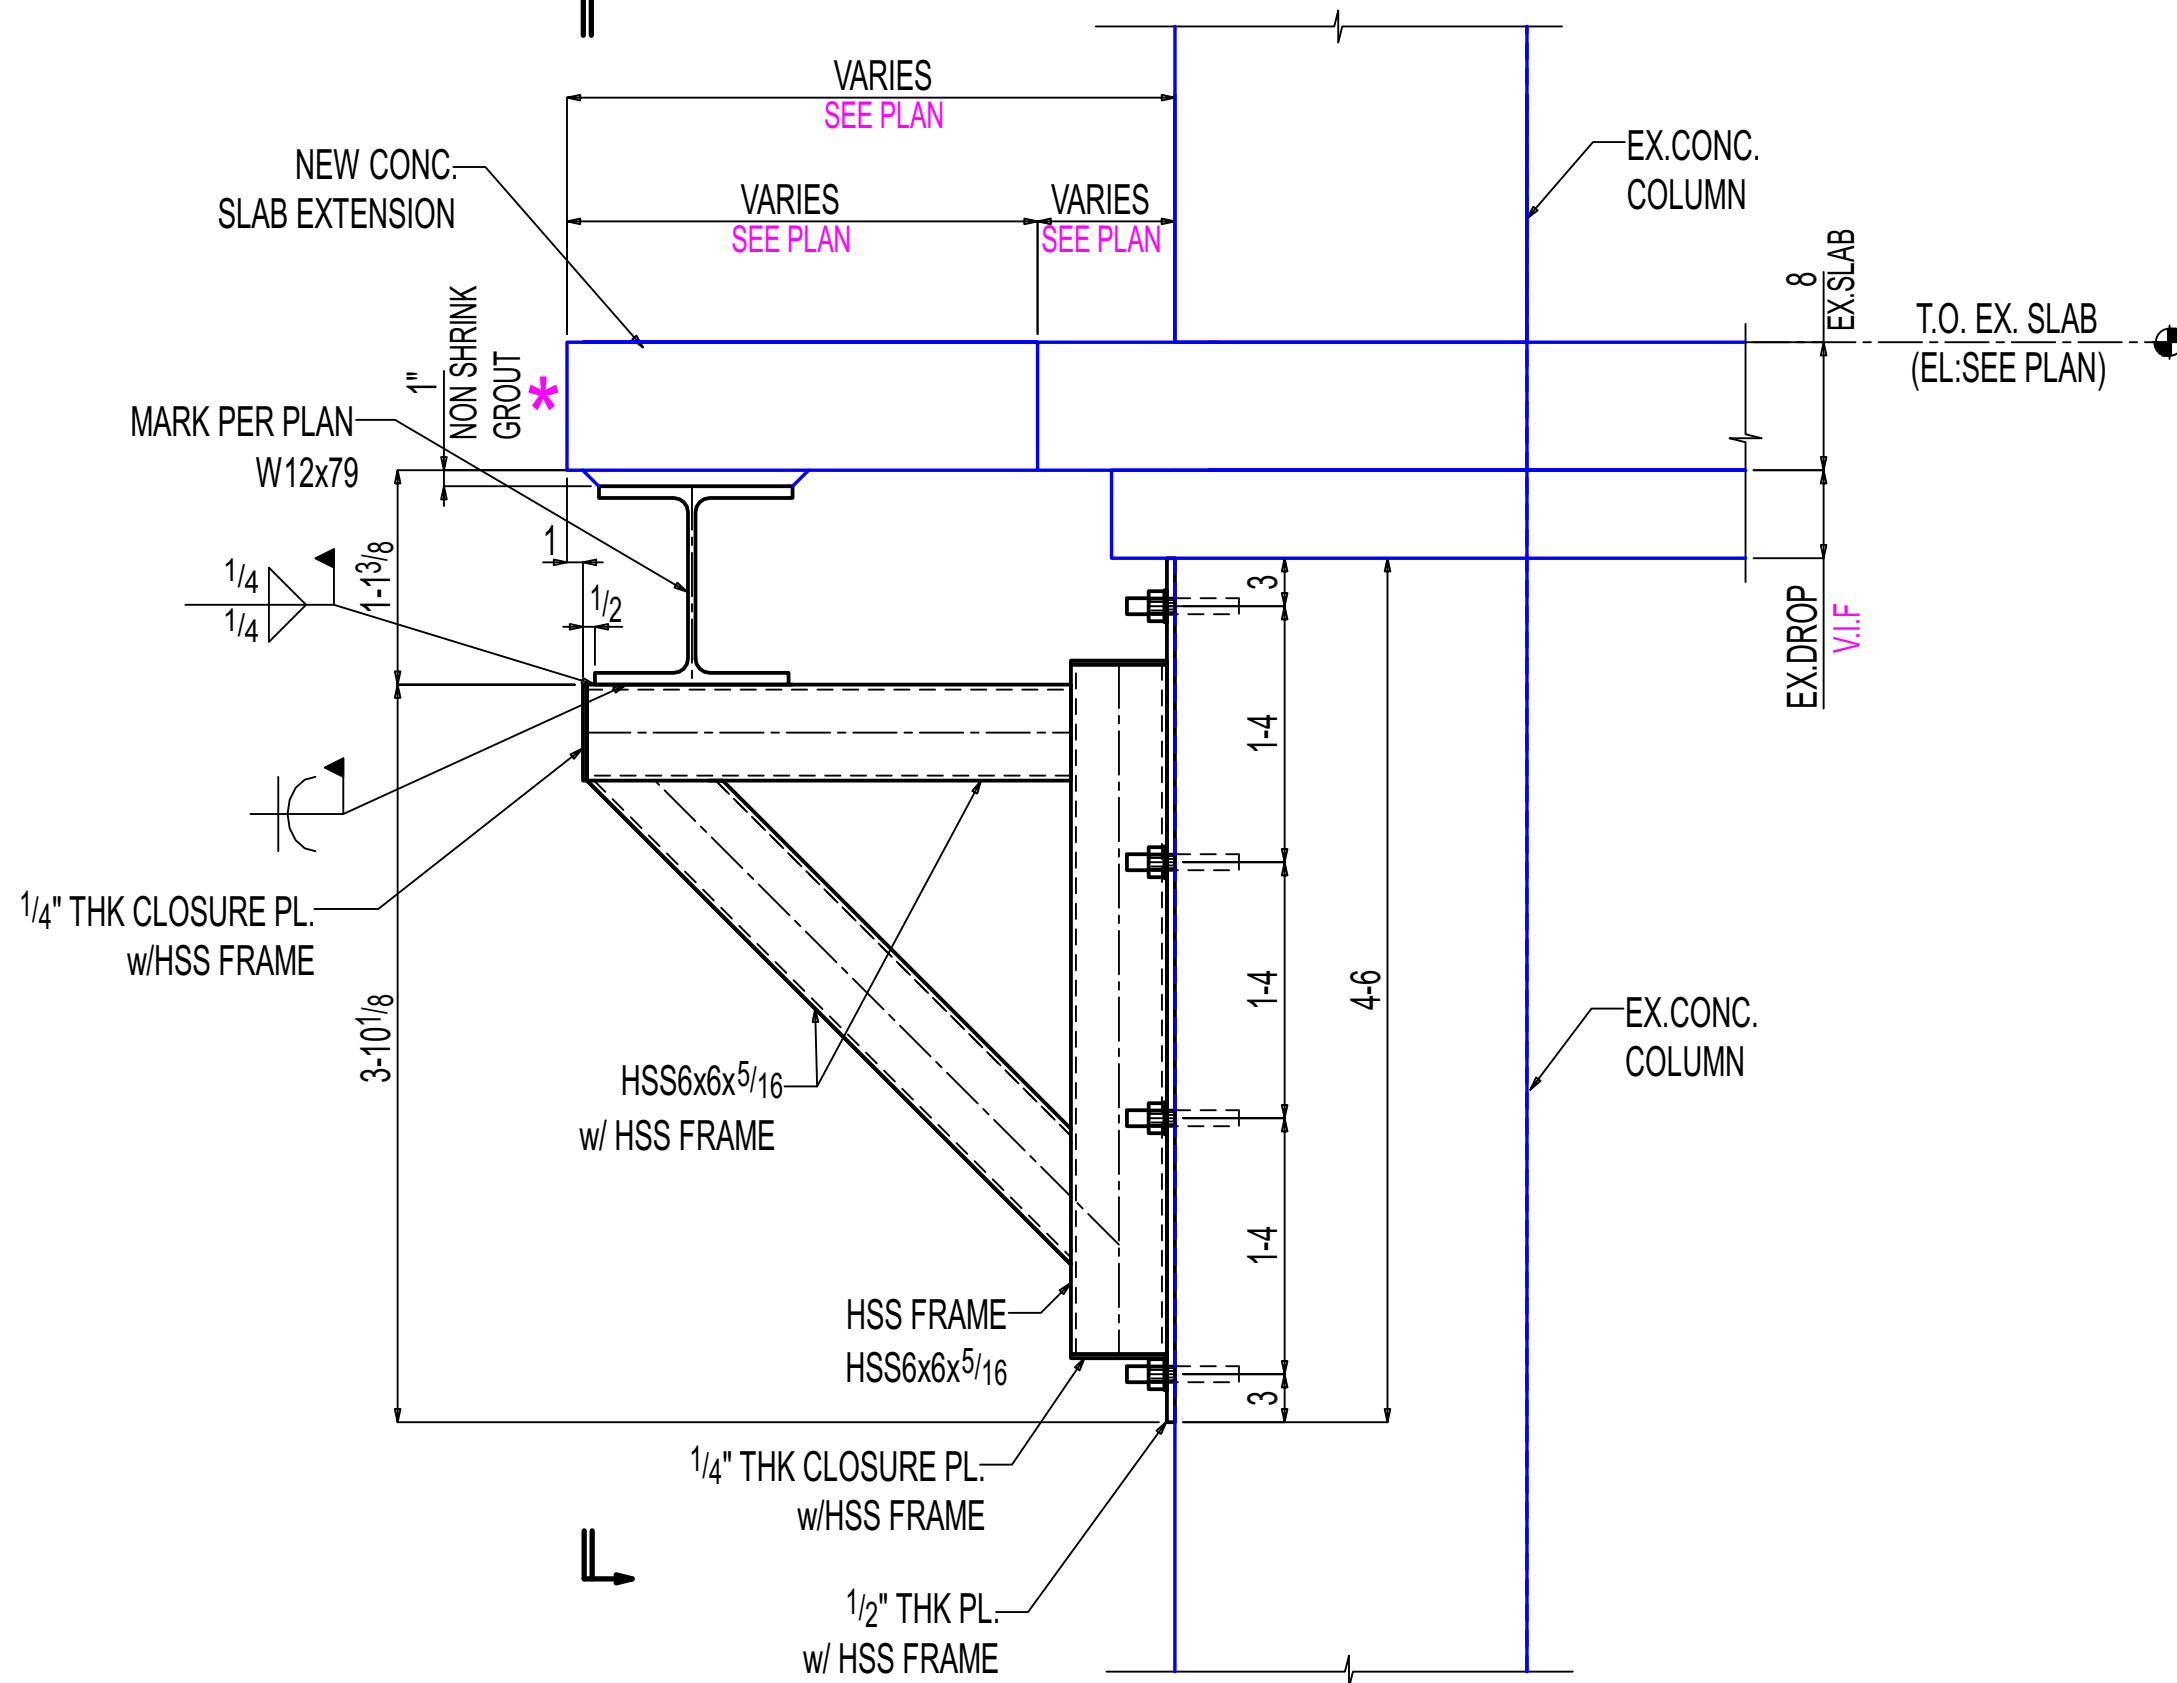
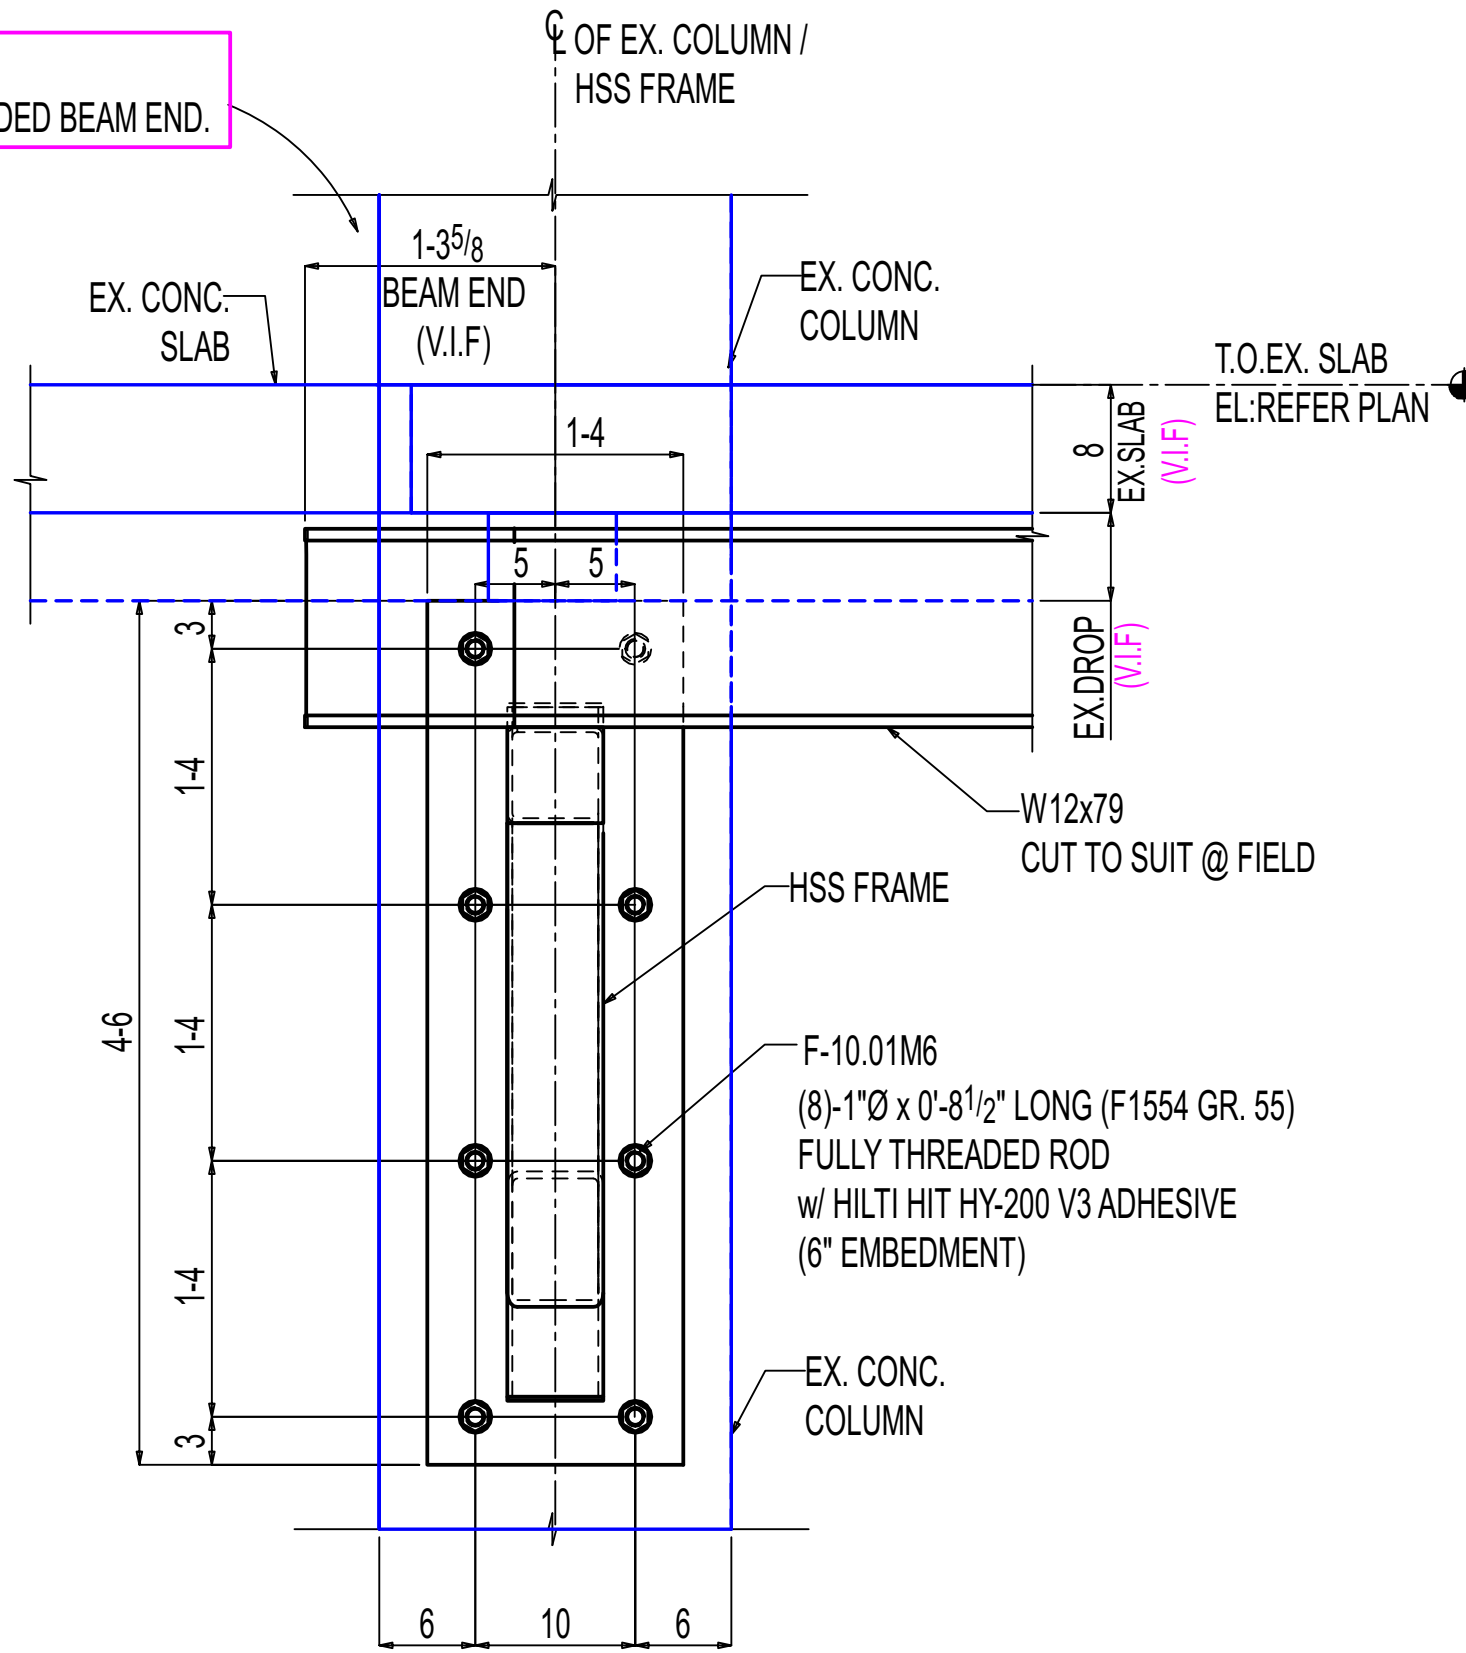


D-D

E-10.00
(REF:13 & 14/S312)

OTHERS NOT SHOWN FOR CLARITY

SHOP / ERECTOR NOTE:
LOCATE EXISTING REBAR PRIOR TO FABRICATION OF PLATE.
DO NOT DRILL THROUGH REBAR.

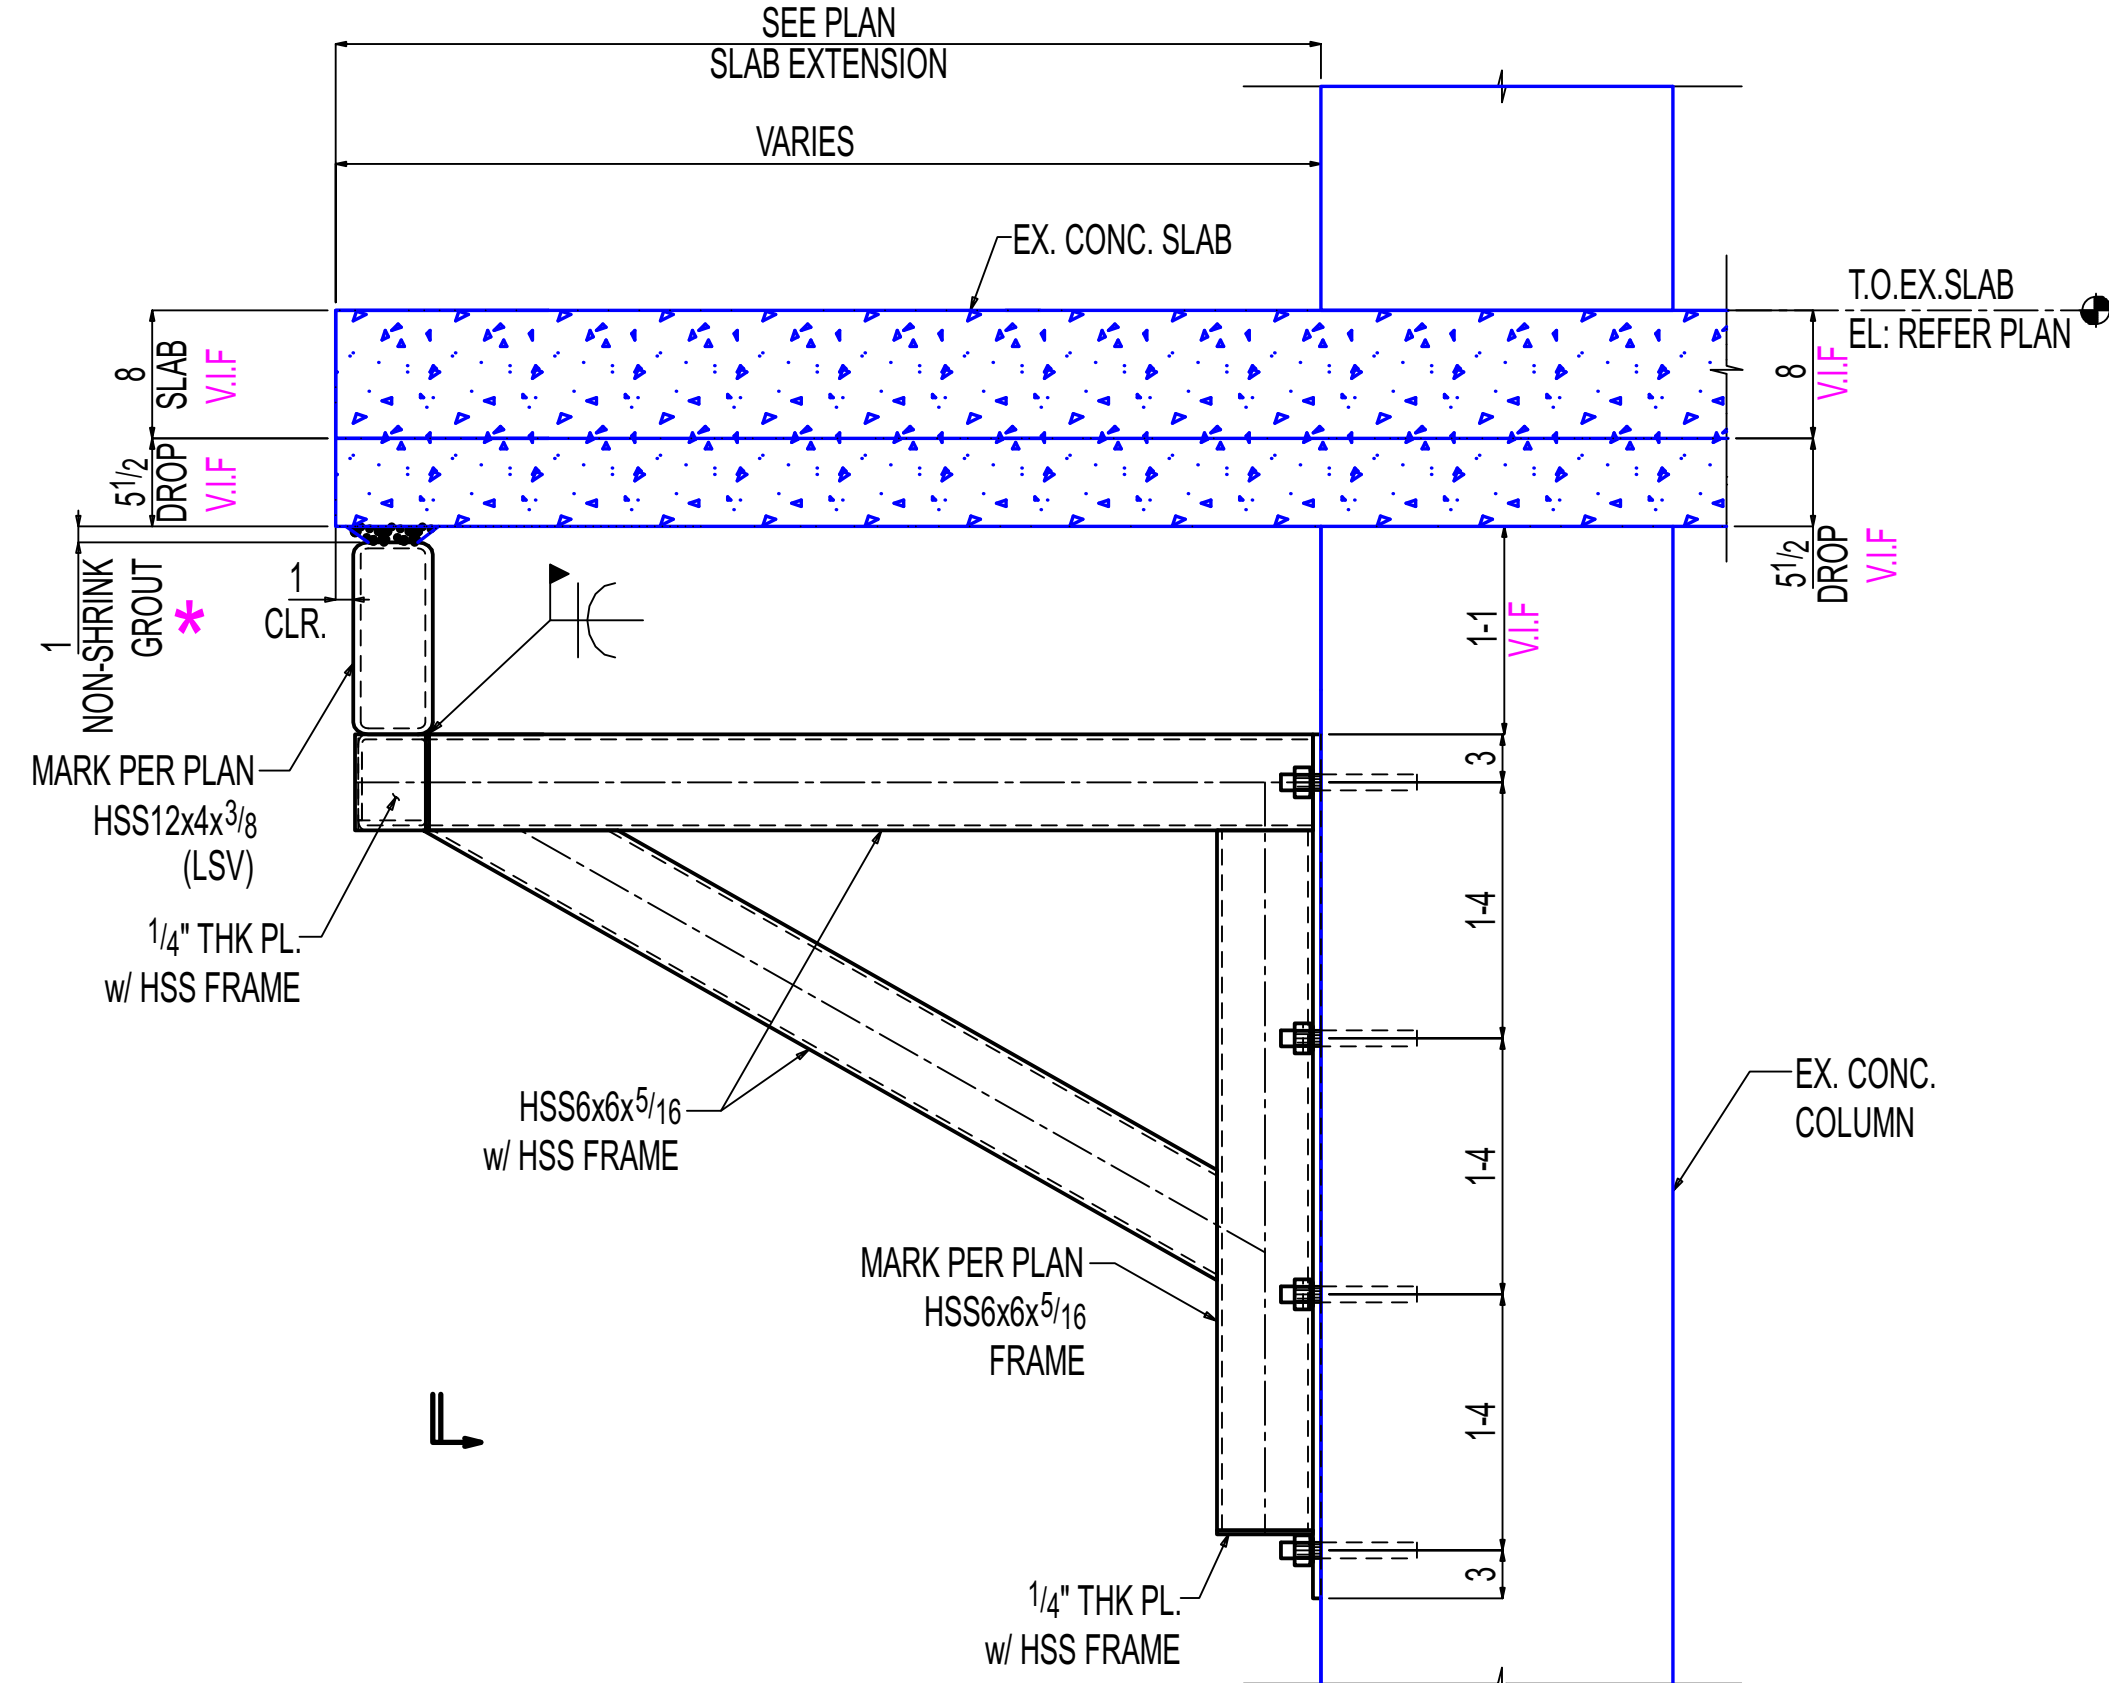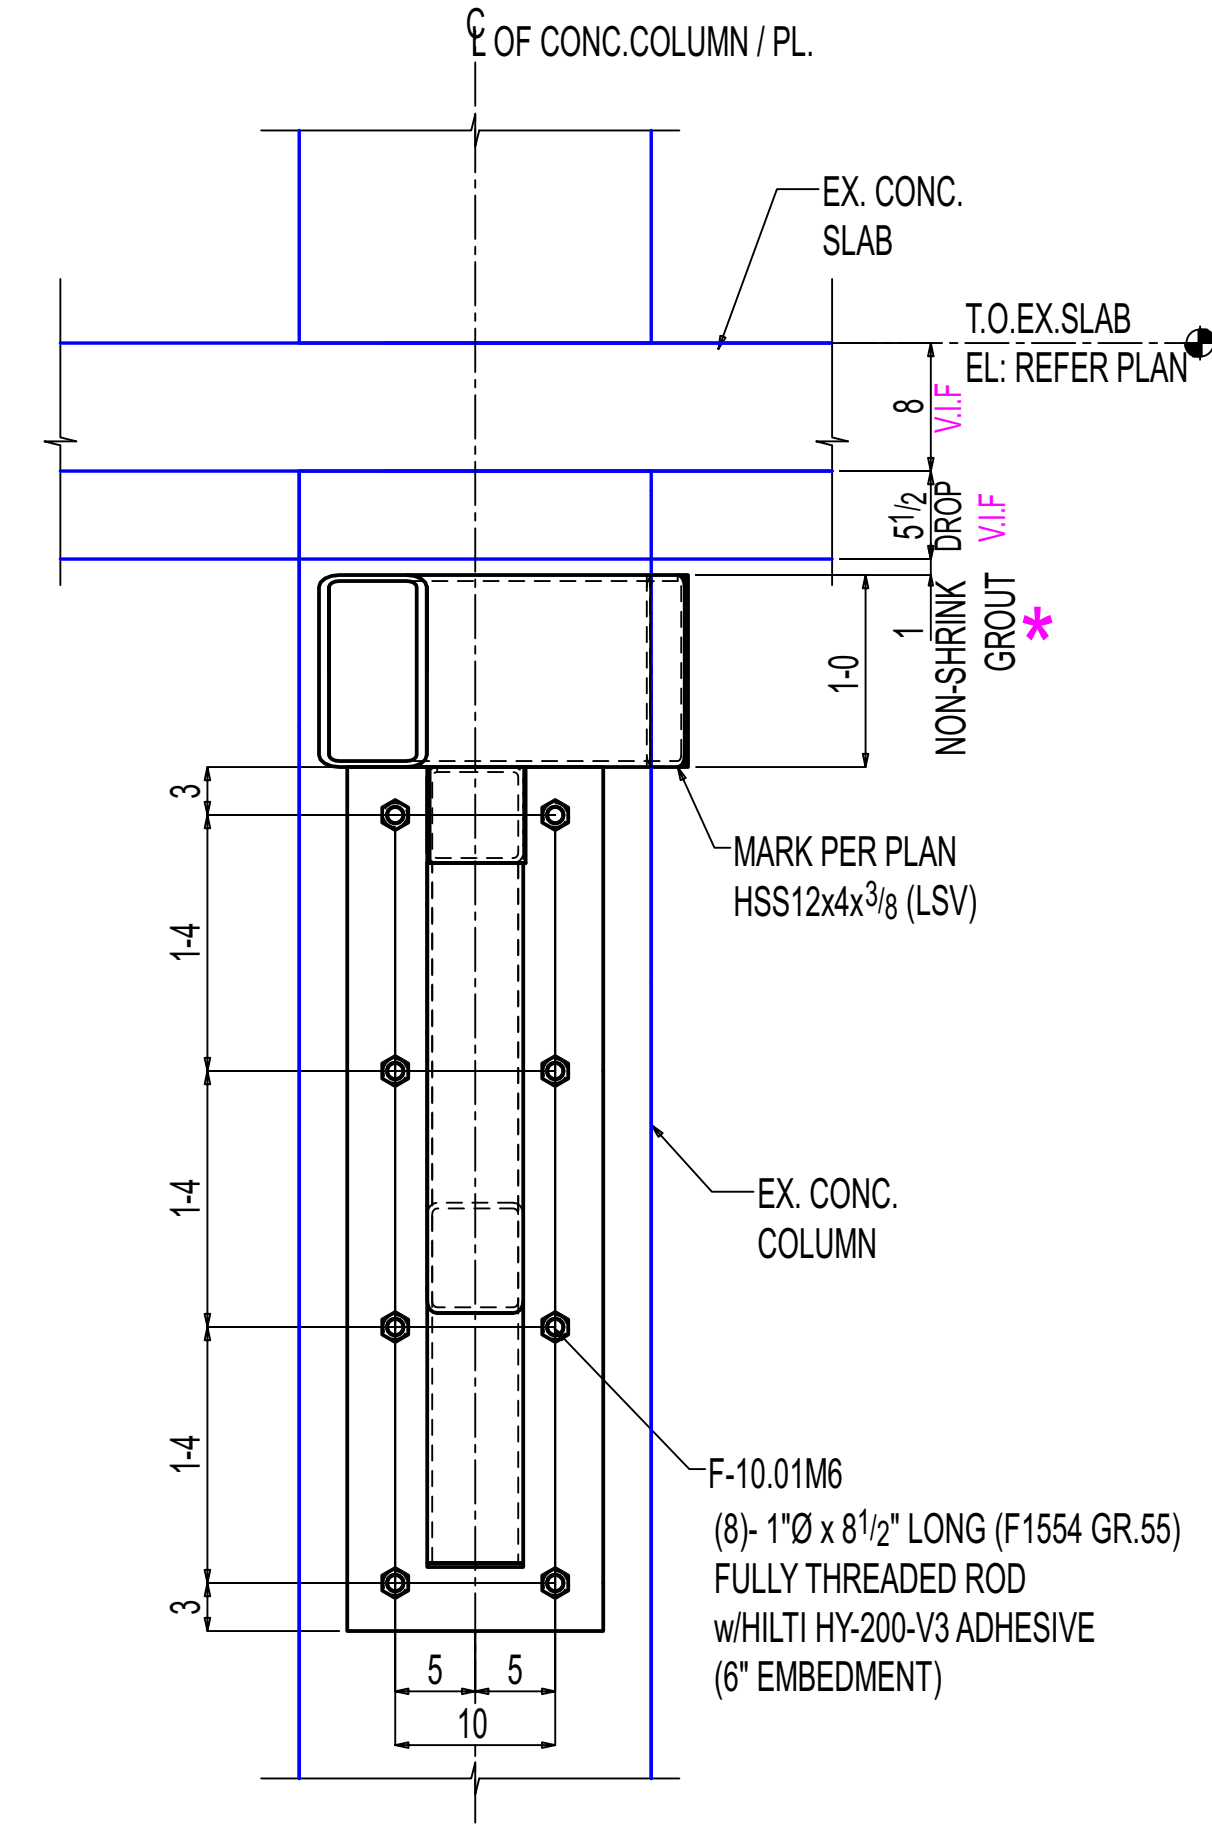

F-F

E-10.00A
(REF:6/S316)

OTHERS NOT SHOWN FOR CLARITY

General Notes

- *Structural steel shall conform to ASTM-A992.
- *Structural SQR/RND tubing conform to ASTM A500 Grade C
- *Pipe shall conform to ASTM A53, Grade B.
- *Channels, Angles and plates shall conform to A36.
- *All bolts shall be 3/4" High strength in accordance with ASTM A325 (UNO)
- *Welding Electrodes for Carbon steel :E70xx

# of Copies	Revision/ Issue	Destination	Date
5	0	For Construction	11-14-2025
4	D	For Re-Approval	10-24-2025
3	C	For Re-Approval	09-19-2025
2	B	For Re-Approval	06-23-2025
1	A	For Approval	02-25-2025

IRON FABRICATION SERVICES, LLC.

3029 M. Street, NW, Suite 202
Washington, DC 20007
Tel: 202-800-5599
Fax: 202-478-0303

Project Name and Address
MARYLAND AVENUE

Location: **1250 MARYLAND AVENUE SW
WASHINGTON, DC 20024**

Contractor:
BALFOUR BEATTY


Approved for Fabrication by: Signature

Contract # **224009** Drawing # **E-10.02**

Contract Item: **LEVEL-04
SLAB EXTENSION**

Ref: **SOW-10: 3,4,5&6 / S307**

Date
01/20/2025
Scale
VARIES
Drawing Title:
**SOW #10 LEVEL-04 NEW
SLAB EXTENSION SUPPORT
SECTIONS**

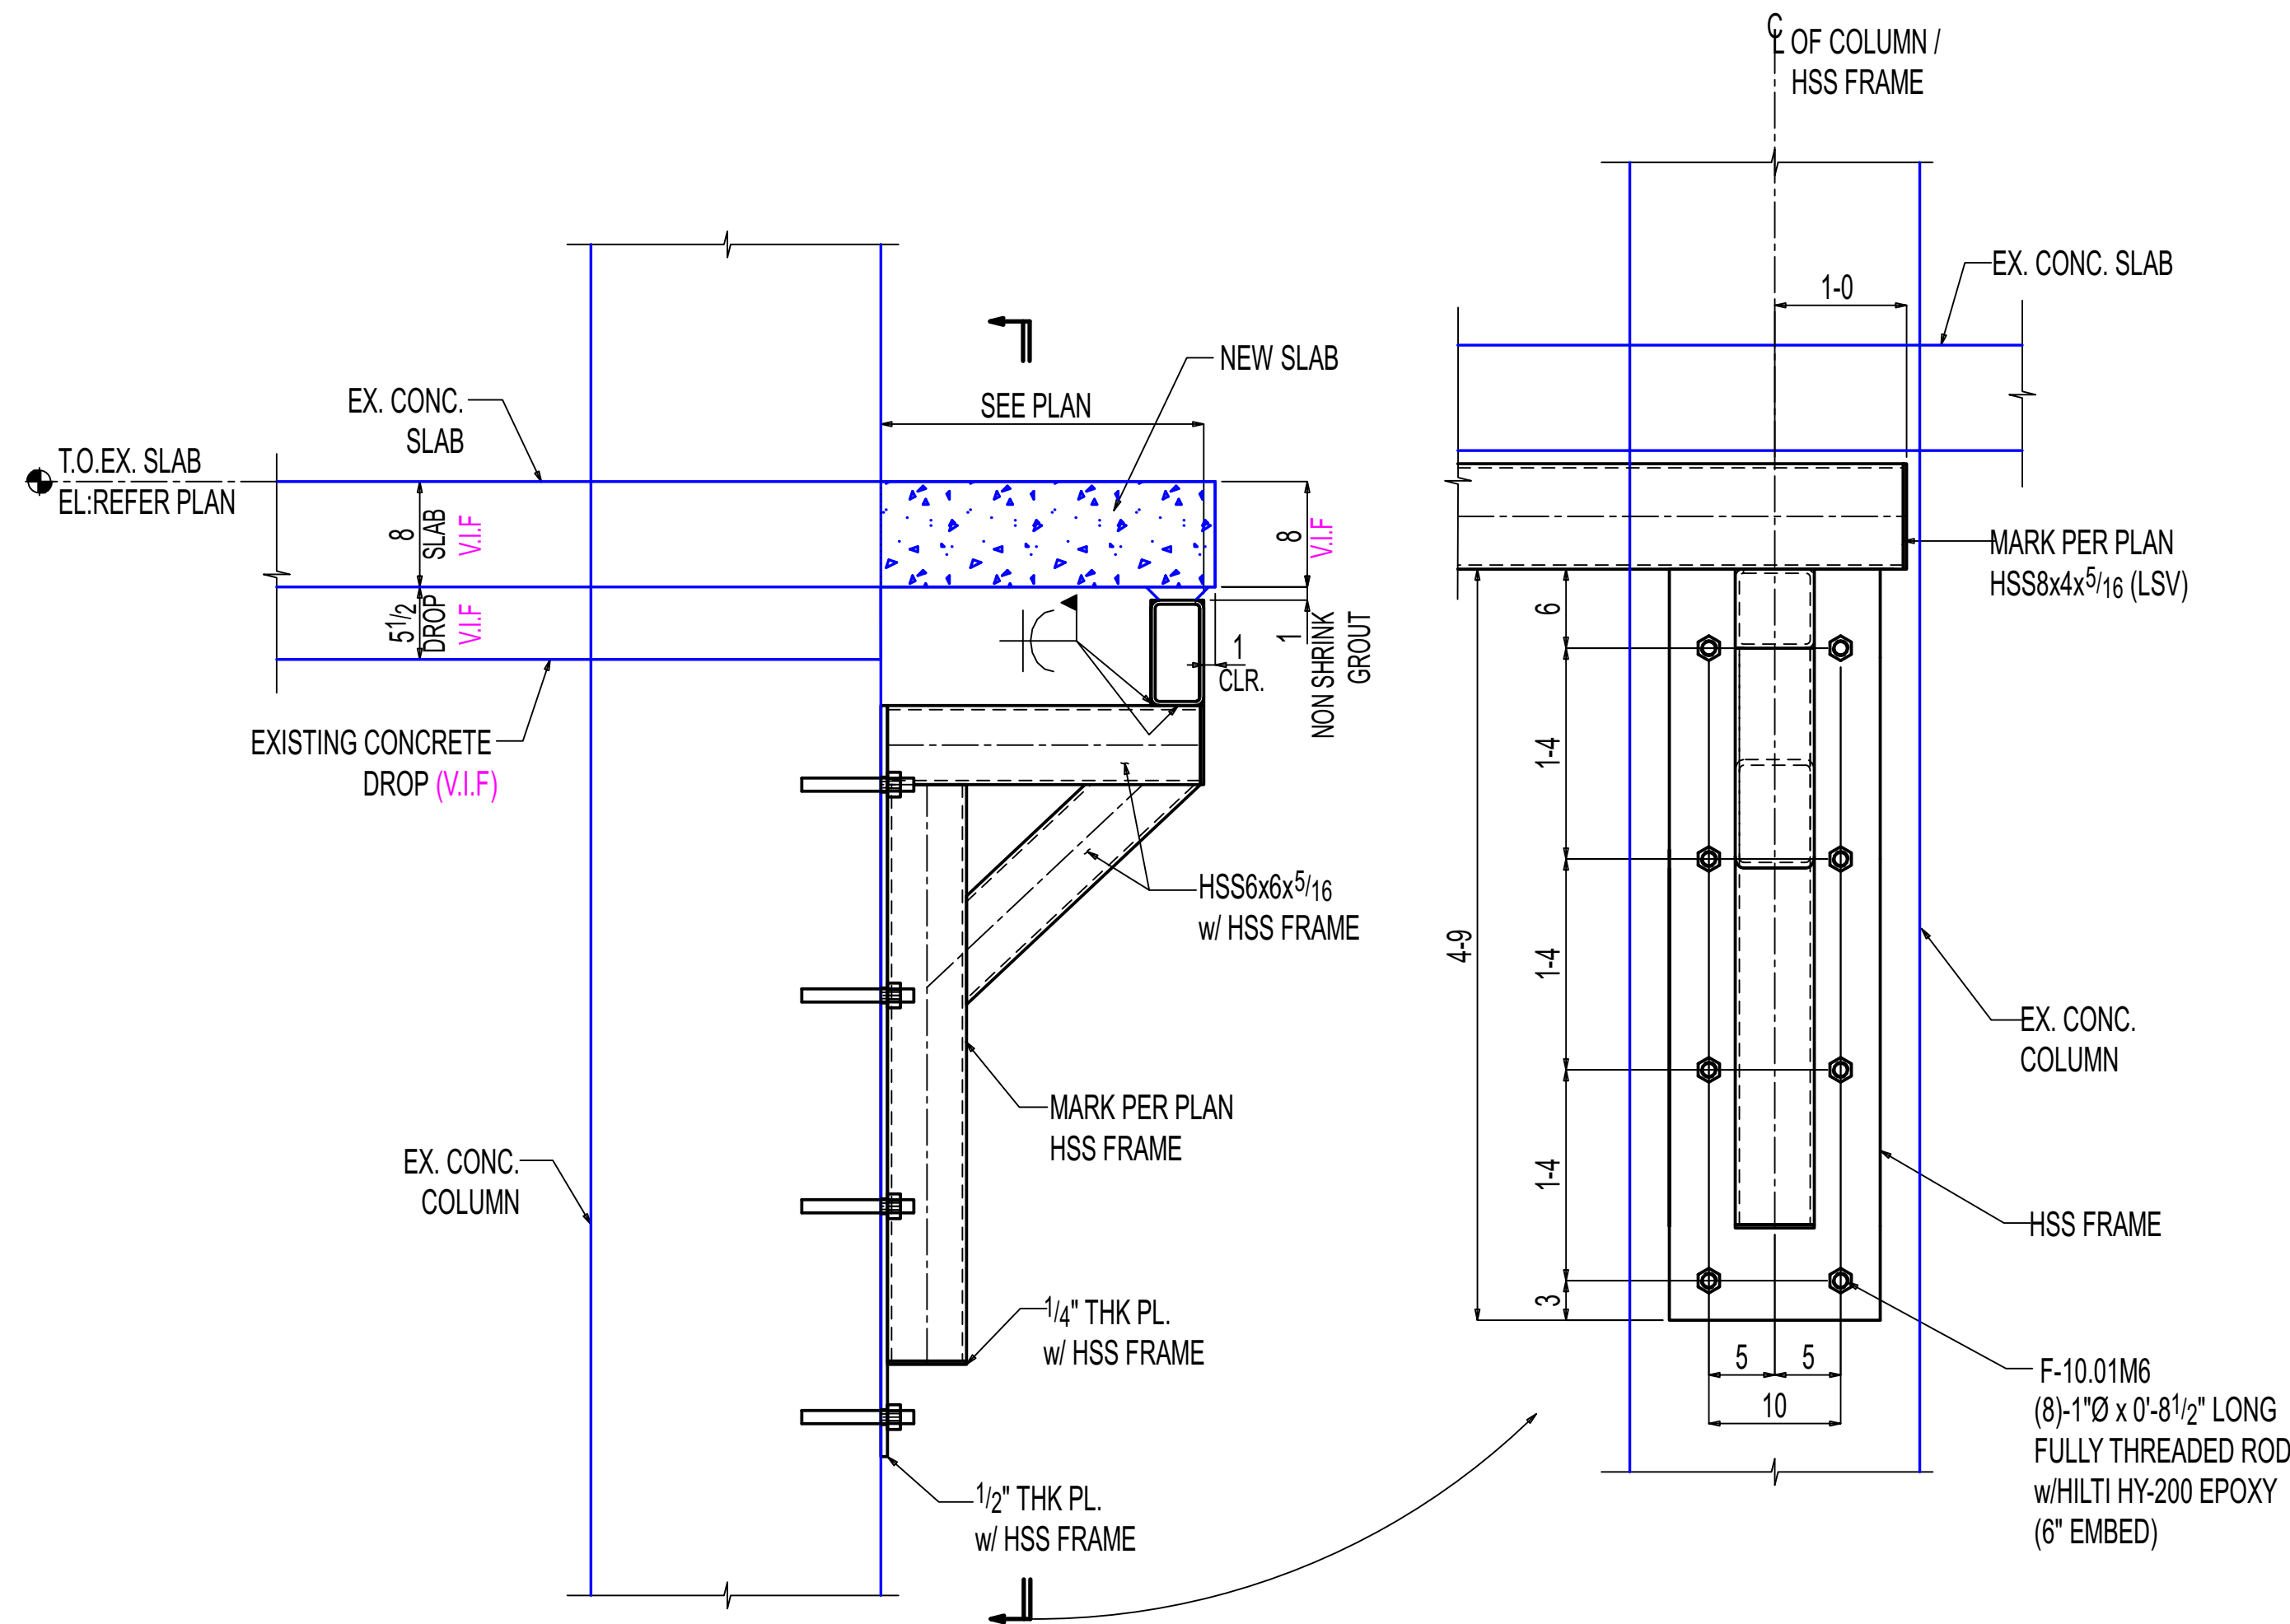


K-K

E-10.00

(REF: 10/S315)

OTHERS NOT SHOWN FOR CLARITY


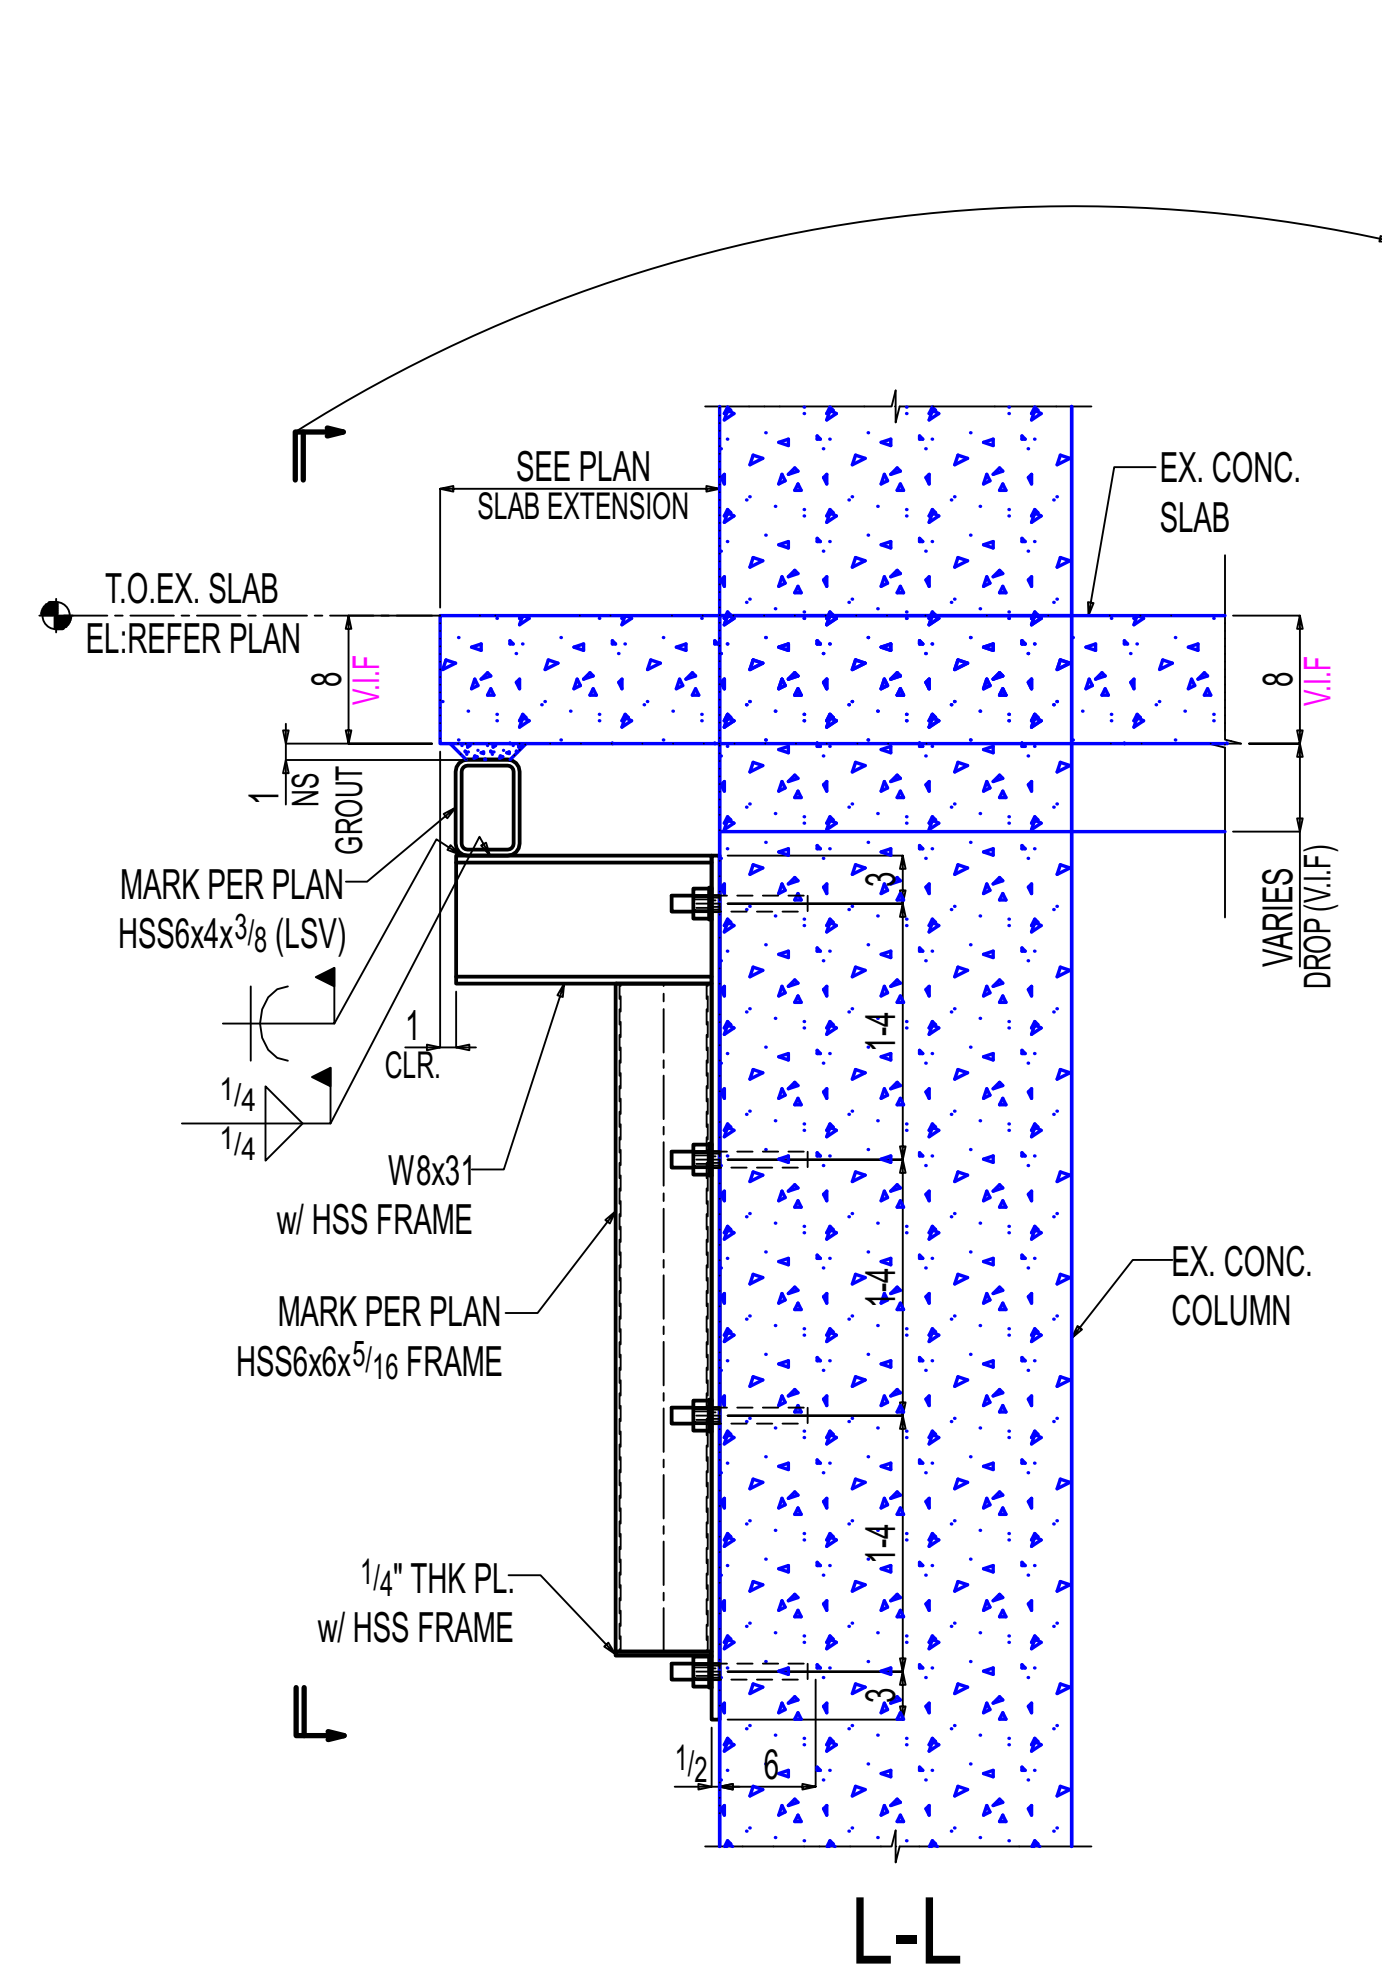


L-L

E-10.00

(REF: 10/S315)

OTHERS NOT SHOWN FOR CLARITY

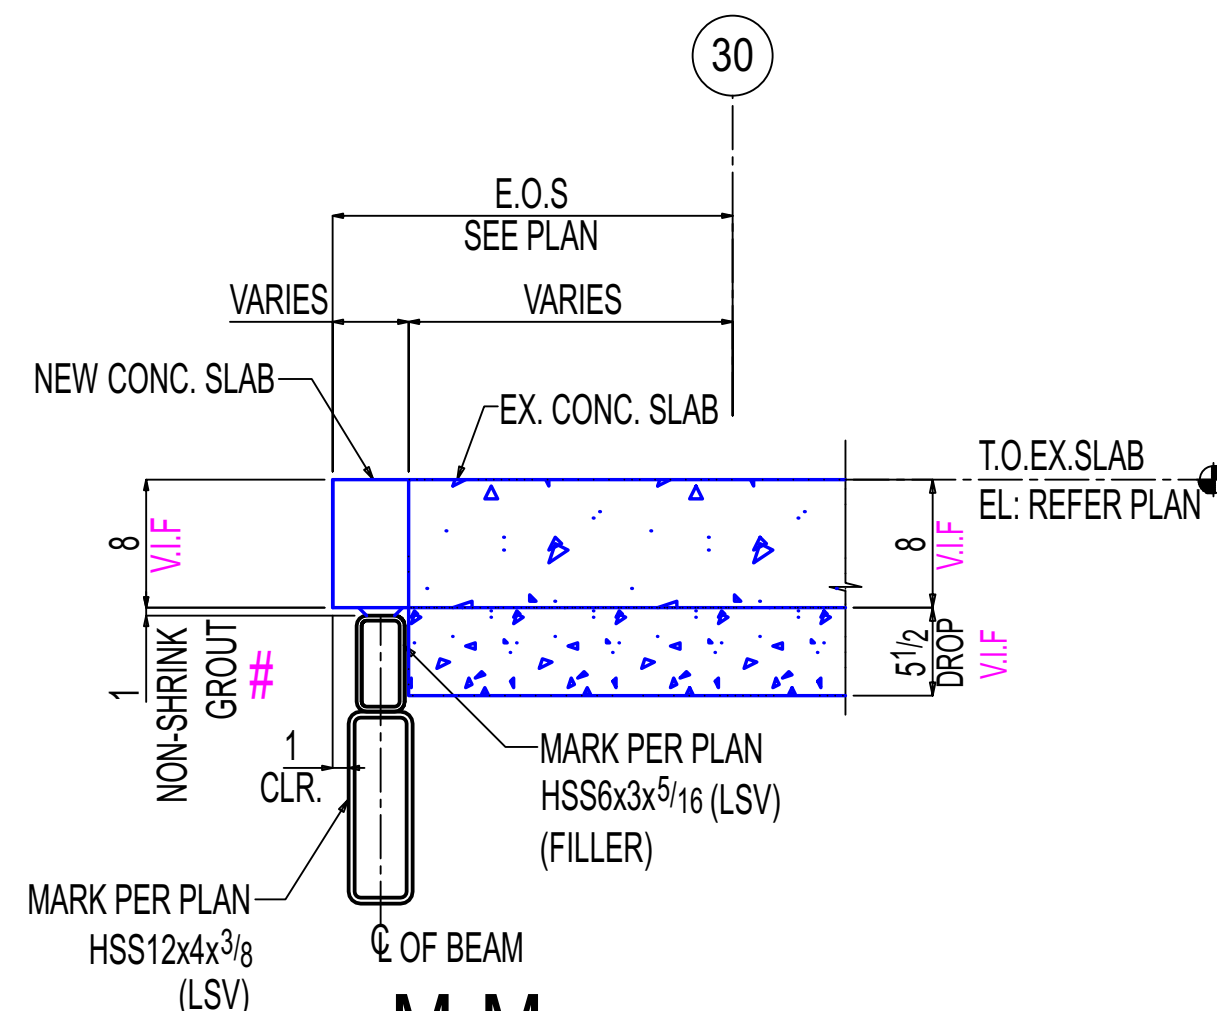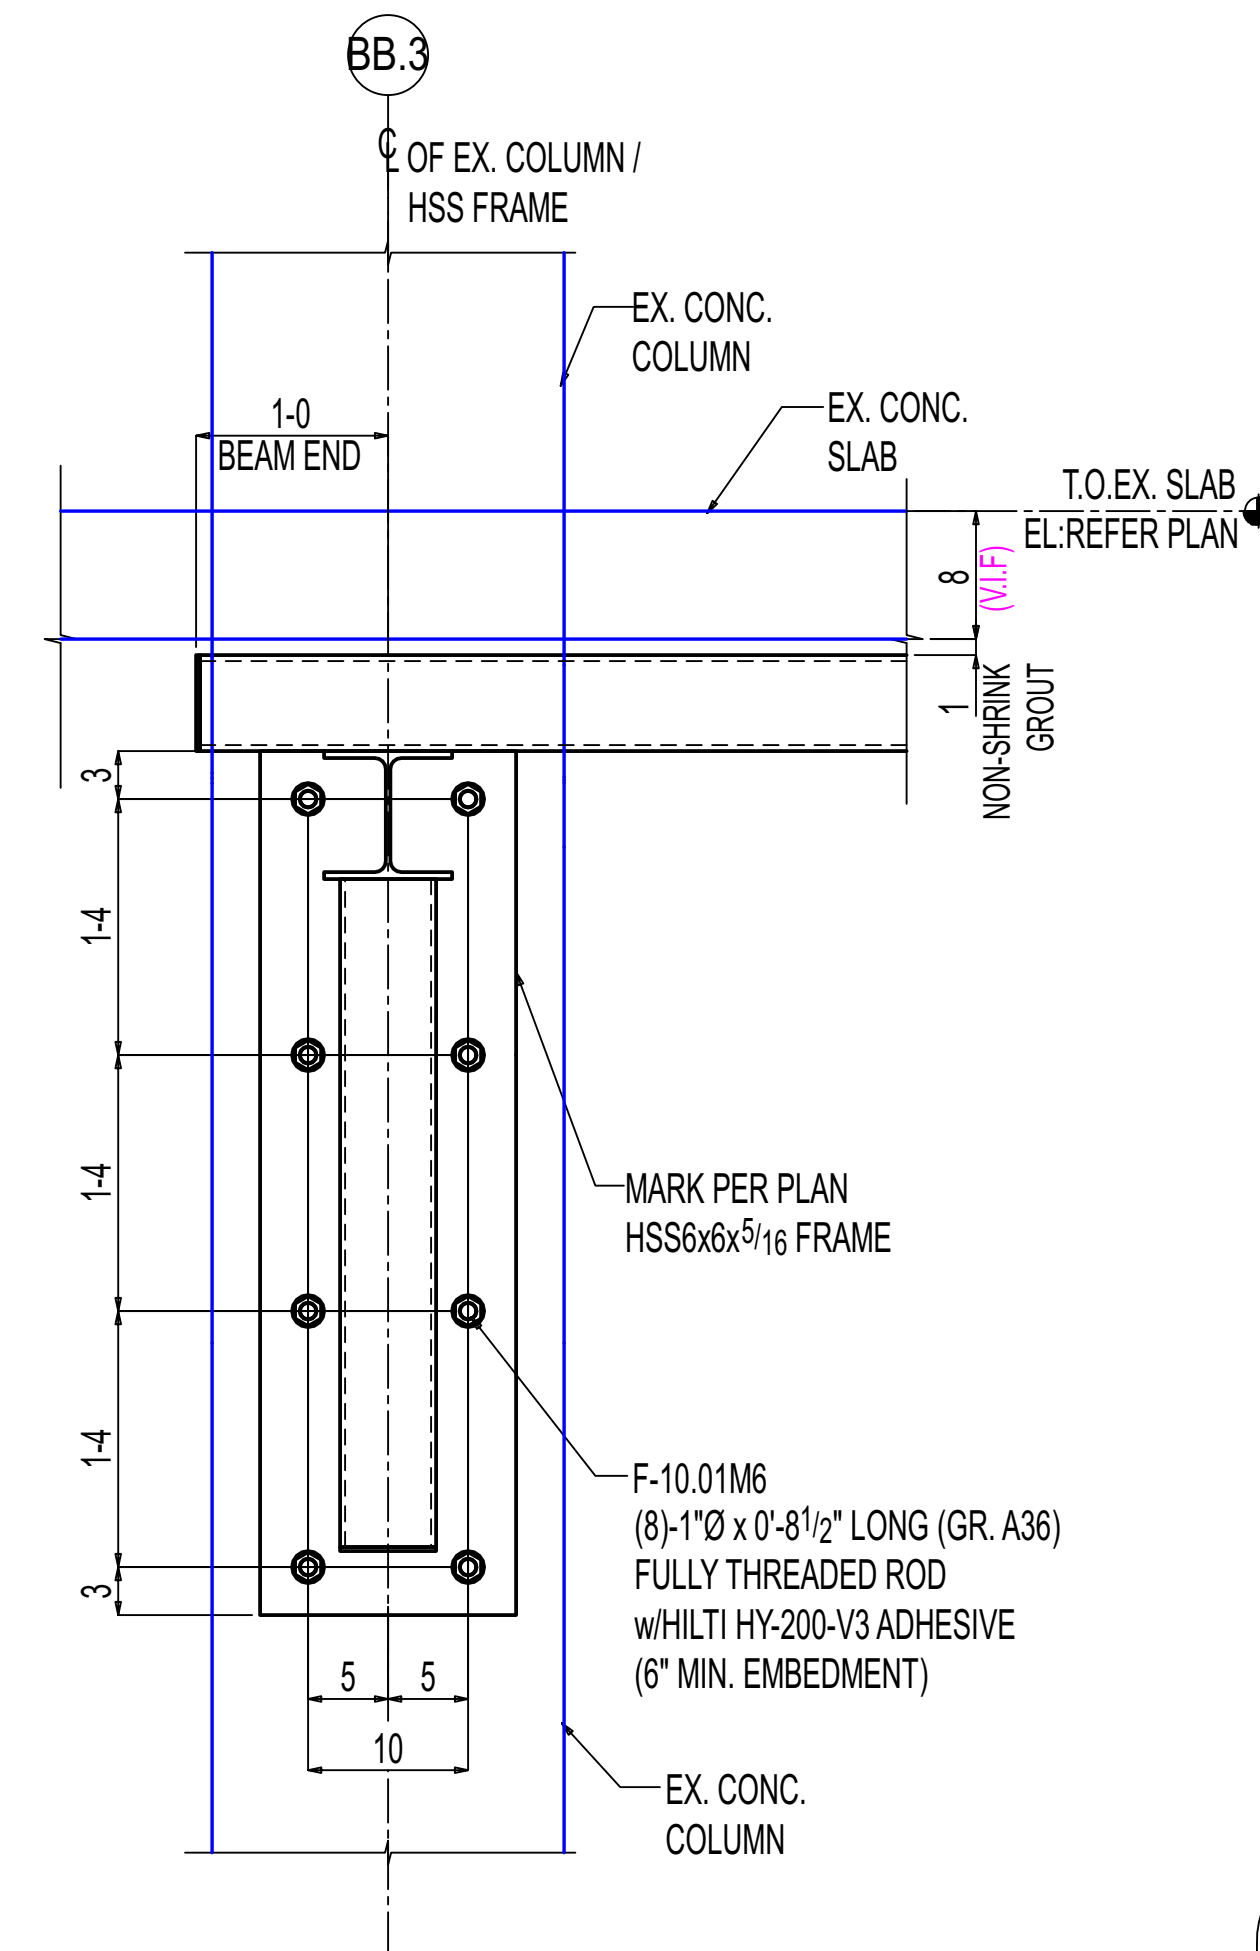


M-M

E-10.00A

(REF: 4/S315)

OTHERS NOT SHOWN FOR CLARITY

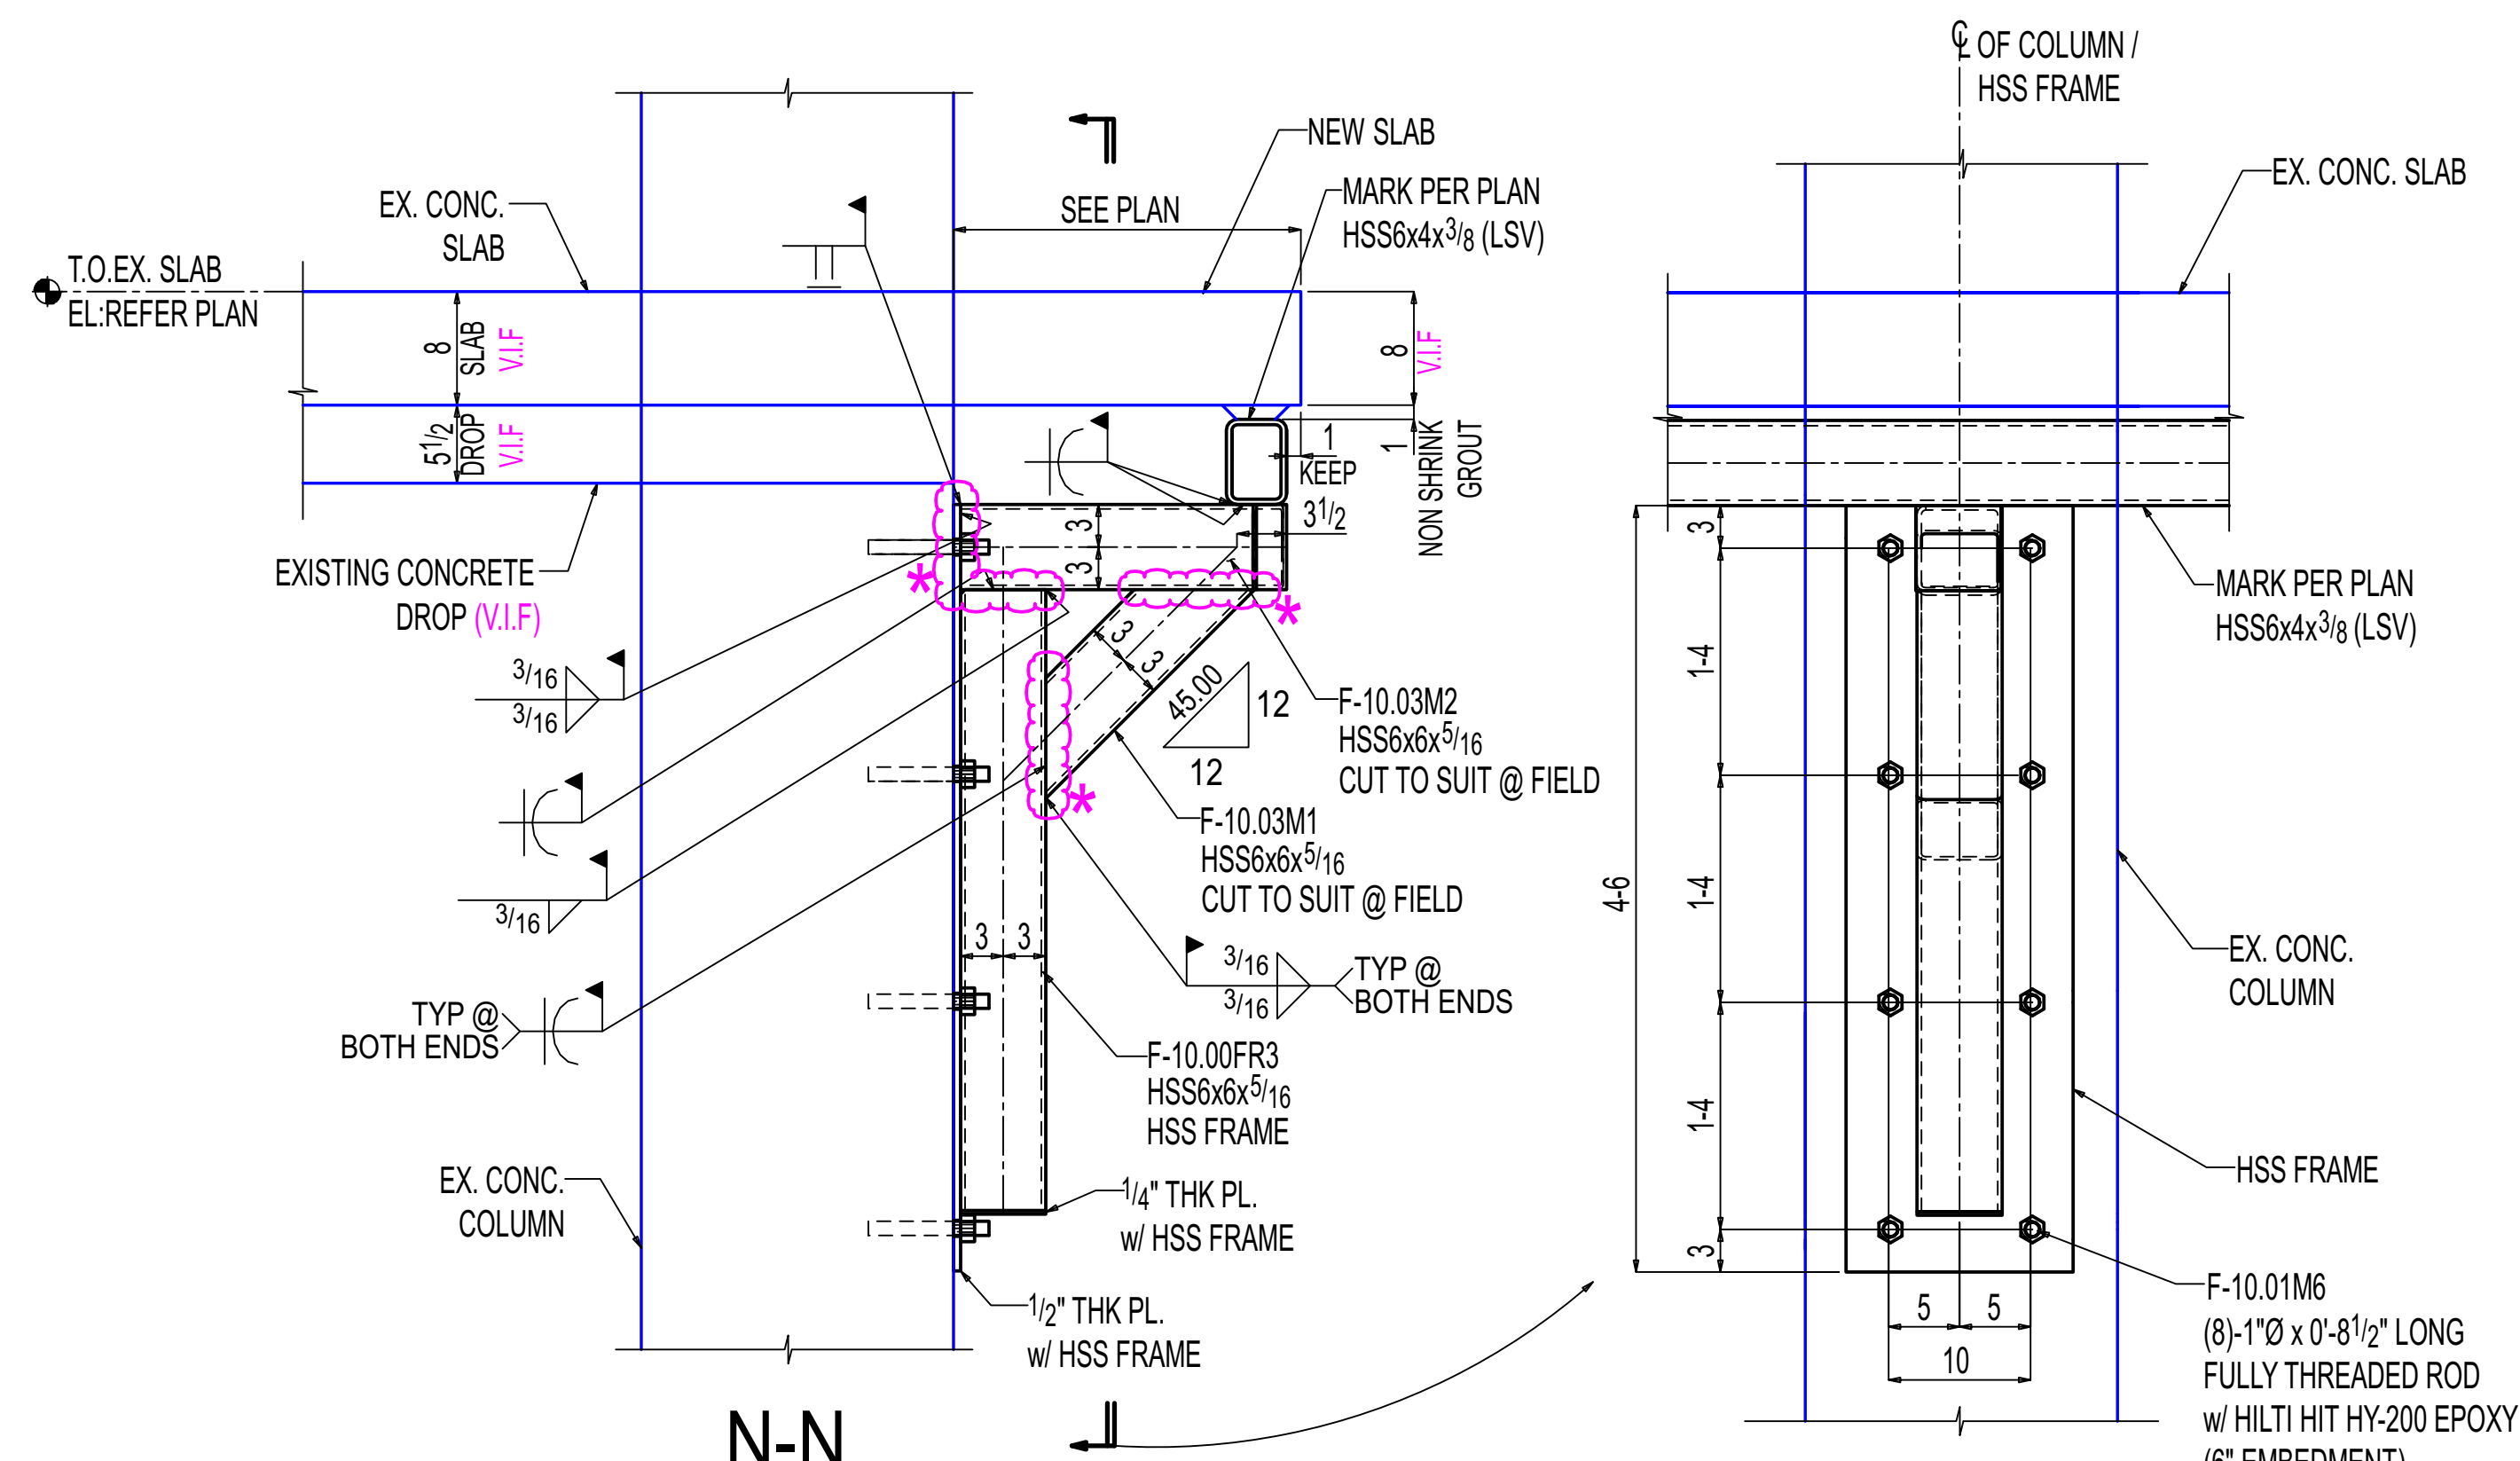

N-N

E-10.00

(REF: 10/S315)

OTHERS NOT SHOWN FOR CLARITY

ERECTOR NOTE:

* FIELD CUT HSS6x6 ENDS TO SUIT EXISTING DROP.

SHOP / ERECTOR NOTE:
LOCATE EXISTING REBAR PRIOR TO FABRICATION OF PLATE.
DO NOT DRILL THROUGH REBAR.

ERECTOR NOTE:
PROVIDE 1\"/>

General Notes

- *Structural steel shall conform to ASTM-A992.
- *Structural SQR/RND tubing conform to ASTM A500 Grade C
- *Pipe shall conform to ASTM A53, Grade B.
- *Channels, Angles and plates shall conform to A36.
- *All bolts shall be 3/4" High strength in accordance with ASTM A325 (UNO)
- *Welding Electrodes for Carbon steel :E70xx

# of Copies	Revision/ Issue	Destination	Date
3	0	For Construction	11-14-2025
2	B	For Re-Approval	10-24-2025
1	A	For Approval	09-19-2025

IRON FABRICATION SERVICES, LLC.

3029 M. Street, NW, Suite 202
Washington, DC 20007
Tel: 202-800-5599
Fax: 202-478-0303

Project Name and Address
MARYLAND AVENUE

Location: **1250 MARYLAND AVENUE SW
WASHINGTON, DC 20024**

Contractor:
BALFOUR BEATTY

Approved for Fabrication by: _____

Signature _____

Contract # **224009** Drawing # **E-10.04**

Contract Item: **LEVEL-04
SLAB EXTENSION**

Ref: **SOW-10: 3,4,5&6 / S307**

Date
01/20/2025

Scale
VARIES

Drawing Title:
**SOW #10 LEVEL-04 NEW
SLAB EXTENSION SUPPORT
SECTIONS**