



BILL OF MATERIAL							
LINE #	QTY	PC	MARK	DESCRIPTION		LENGTH	WEIGHT
	TOTAL						TOTAL
						REMARKS	ADVANCE
	ONE	F-10.02C1		COLUMN			329
	1	F-10.02C1		HSS6x6x ³ / ₈			284
	1	pl1970		PL1 ¹ / ₄ x7			45
				FIELD BOLTS			
	2			³ / ₄ Dia HILTI HAS V-36			
				w/ HILTI HIT HY-200 EPOXY			
				(3 ¹ / ₄ " EMBEDMENT)			
	ONE	F-10.02C2		COLUMN			353
	1	F-10.02C2		HSS6x6x ³ / ₈			271
	1	hss434		HSS4x4x ³ / ₁₆			23
	1	hss433		HSS4x4x ³ / ₁₆			16
	1	a171		L1 ¹ / ₂ x1x ³ / ₁₆			1
	2	pl350		PL ⁵ / ₈ x6 ¹ / ₂			41
	1	pl3522		PL1 ¹ / ₄ x4			1
				FIELD BOLTS			
	2			¹ / ₂ " Dia HILTI KWIK HUS-EZ			
				SCREW ANCHOR			
				(2 ³ / ₄ " EMBEDMENT)			
	ONE	F-10.02B1		BEAM			1430
	1	F-10.02B1		W12x79			1430
	ONE	F-10.02B2		BEAM			460
	1	F-10.02B2		HSS12x4x ³ / ₈			453
	2	pl3245		PL1 ¹ / ₄ x4			7

Total weight : 2572

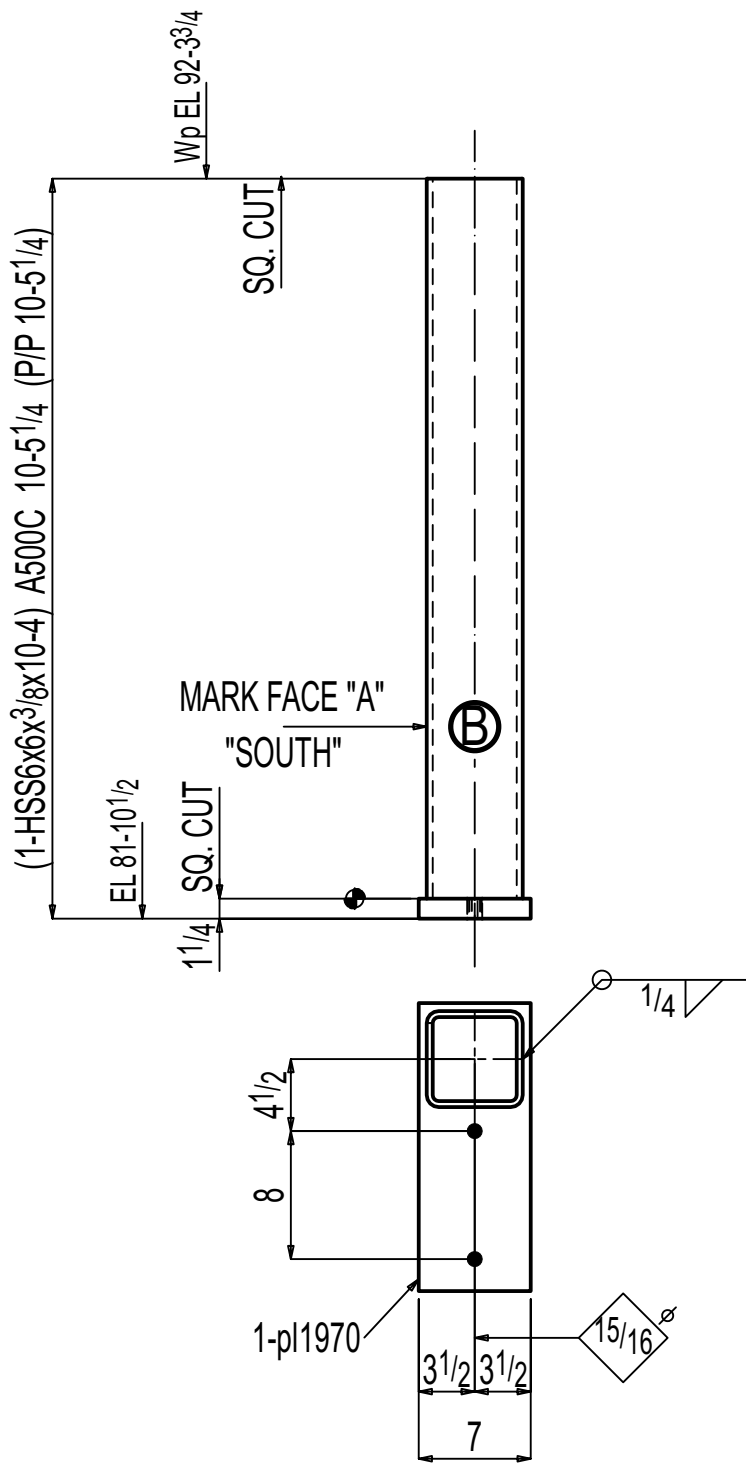


ONE COLUMN F-10.02C1

AT GRID:
EE & A

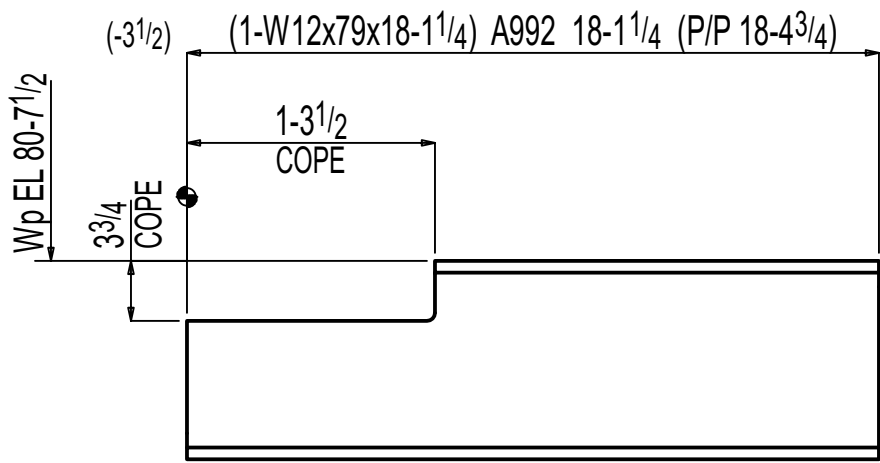


ONE BEAM F-10.02B1

W 12³/₈x1¹/₂
F 12¹/₈x3³/₄
K 1⁵/₈x1¹/₈

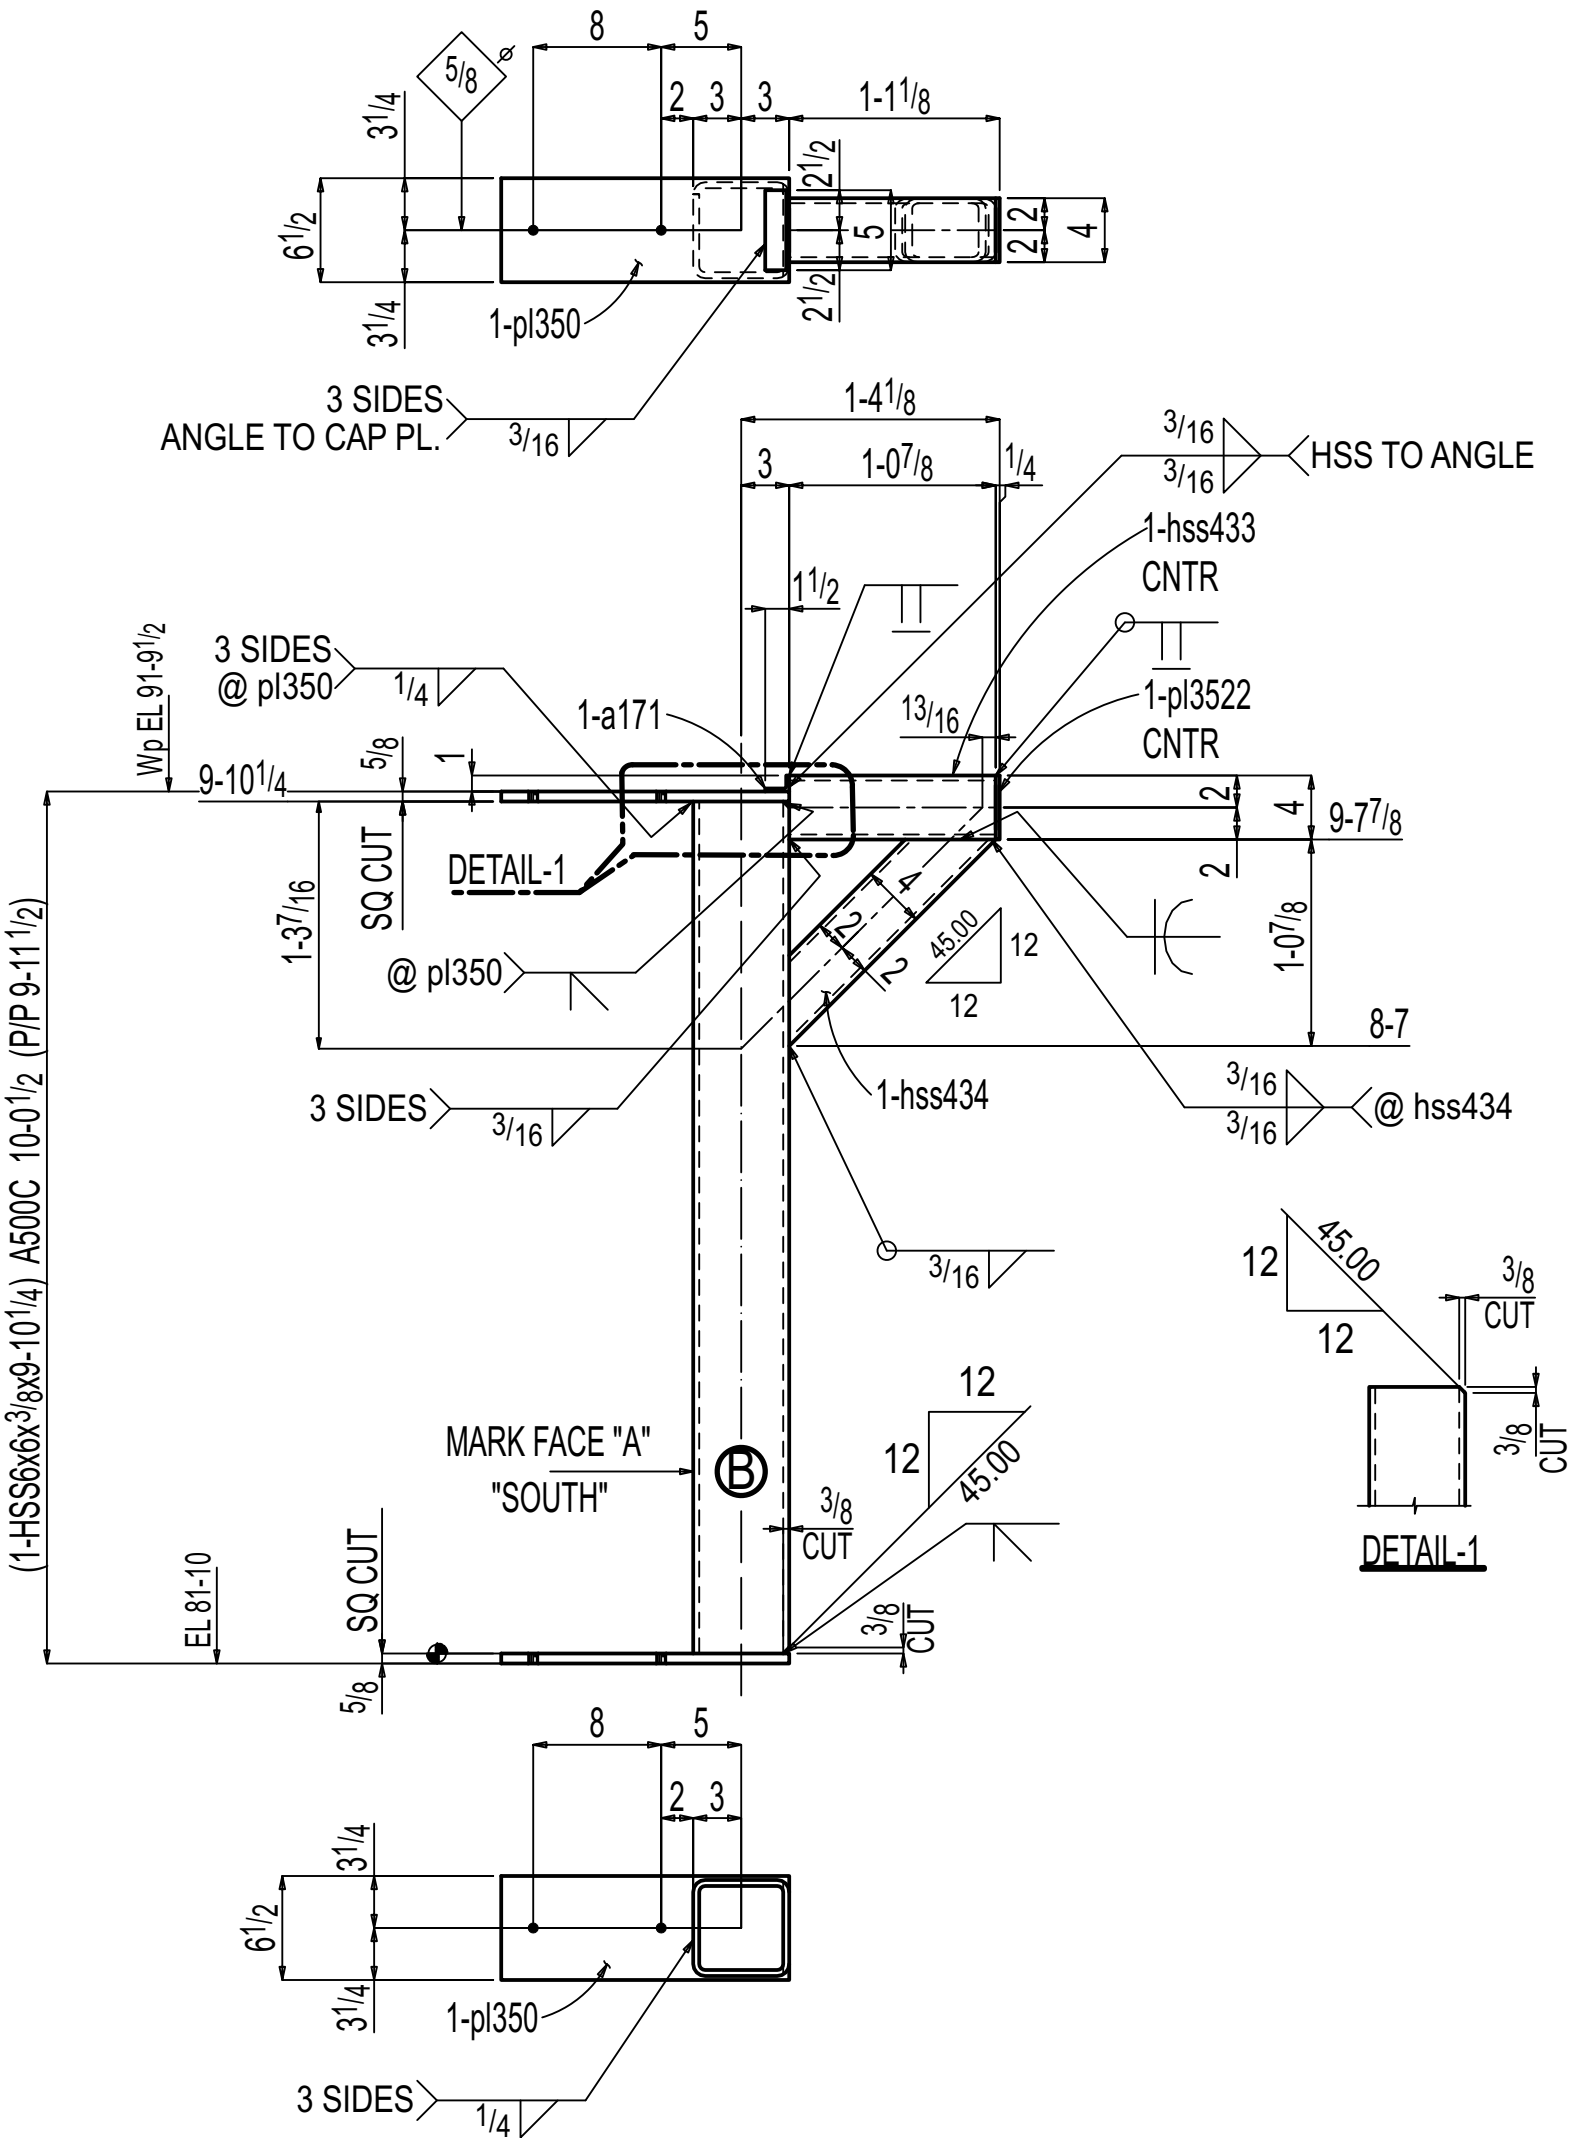

ONE COLUMN F-10.02C2

AT GRID:
AA & K

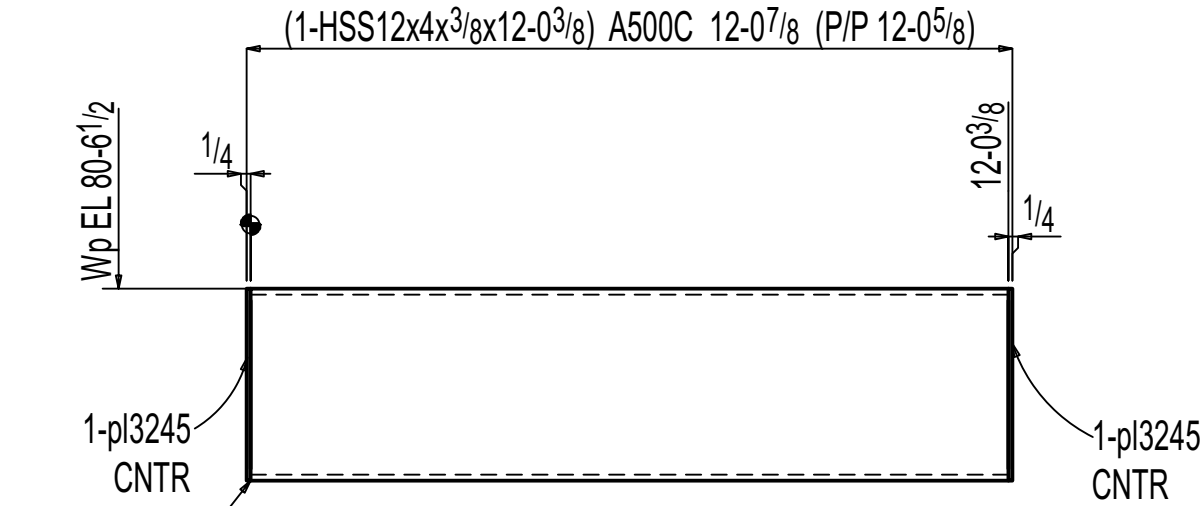

ONE BEAM F-10.02B2

PAINT :NO PAINT
PREPARATION :SSPC-SP3

General Notes			
*Structural steel shall conform to ASTM-A992.			
*Structural SQR/RND,tubing conform to ASTM A500 Grade C			
*Pipe shall conform to ASTM A53, Grade B.			
*Channels, Angles and plates shall conform to A36.			
*All bolts shall be ³ / ₄ " High strength in accordance with ASTM A325 (UNO)			
*Welding Electrodes for Carbon steel :E70xx			
5	0	For Fabrication	11-14-2025
4	D	For Re-Approval	10-24-2025
3	C	For Re-Approval	09-19-2025
2	B	Deleted	06-23-2025
1	A	For Approval	02-25-2025
# of Copies	Revision/ Issue	Destination	Date

IRON FABRICATION SERVICES, LLC.

3029 M. Street, NW, Suite 202
Washington, DC 20007
Tel: 202-800-5599
Fax: 202-478-0303

Project Name and Address
MARYLAND AVENUE

Location: **1250 MARYLAND AVENUE SW
WASHINGTON, DC 20024**

Contractor:
BALFOUR BEATTY

Approved for Fabrication by: Signature

Contract # **224009** Drawing # **F-10.02**

Contract Item: **COLUMN & BEAM**

Ref:
SOW - 10: E-10.00 - E-10.02

Date **01/ 23/ 2025** Drawing Title: **COLUMN & BEAM DETAIL**
Scale **VARIES**