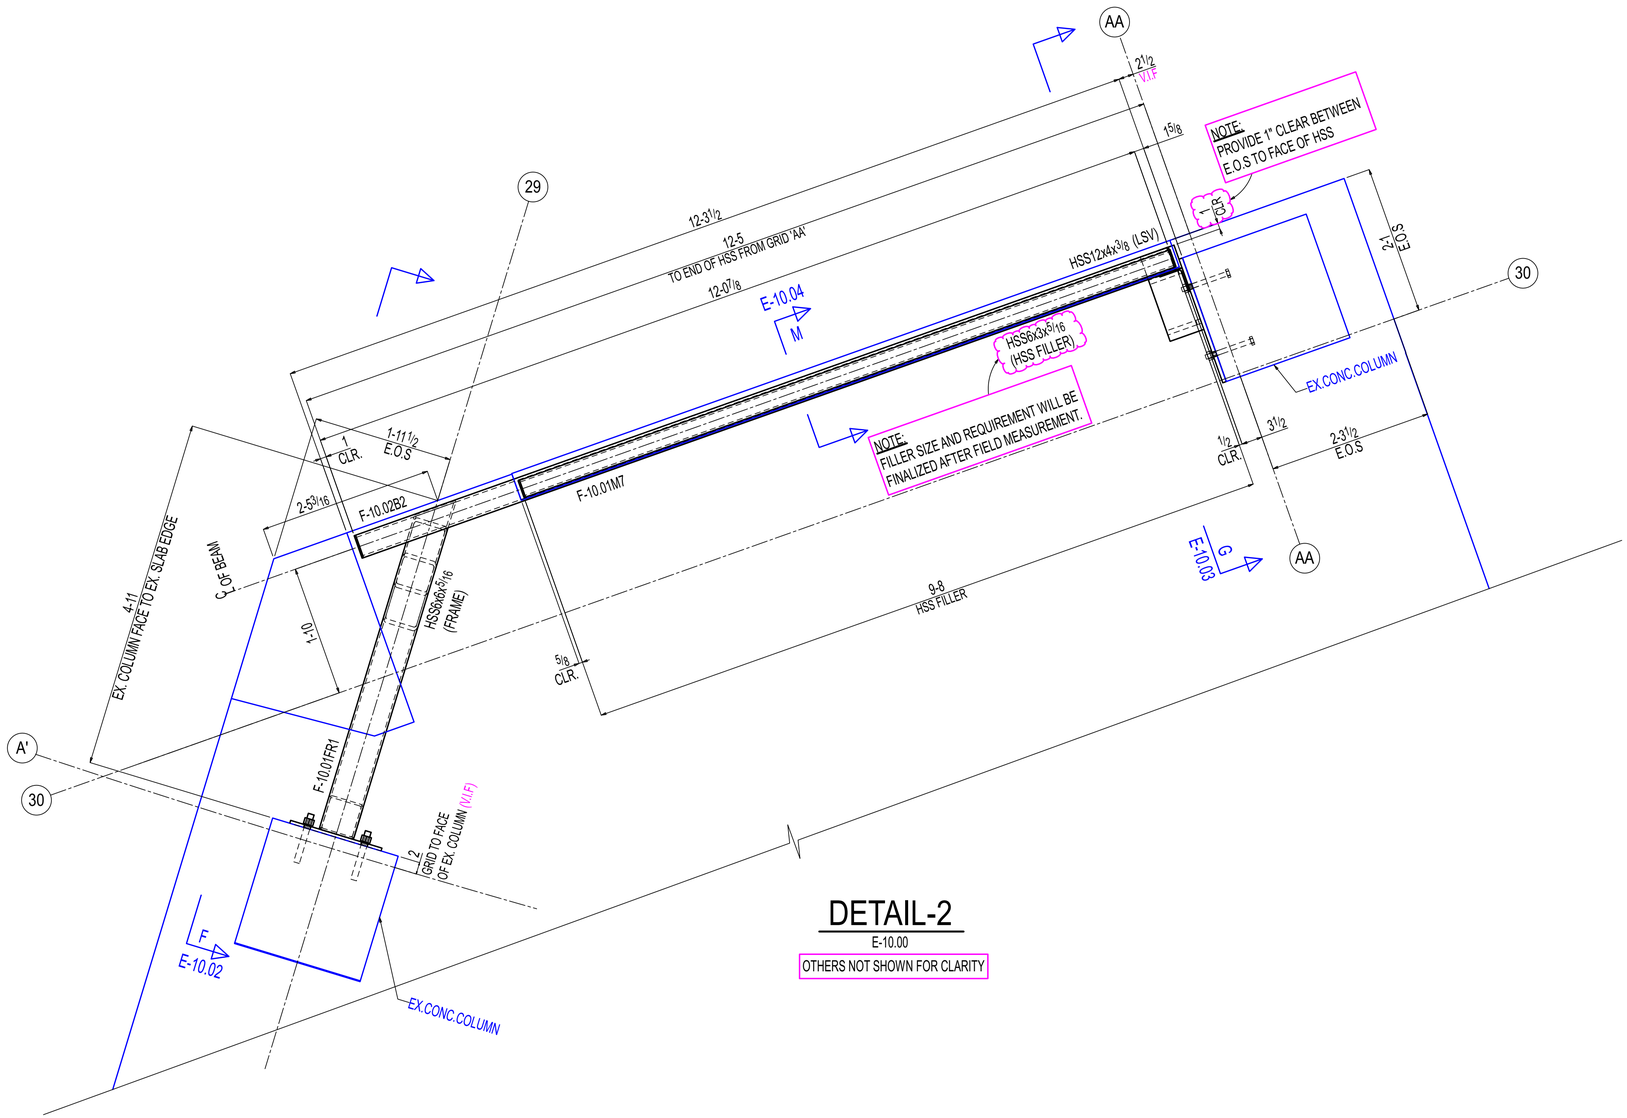

DETAIL-2

E-10.00

OTHERS NOT SHOWN FOR CLARITY

KEY PLAN

General Notes

*Structural steel shall conform to ASTM-A992.
*Structural SQR/RND.tubing conform to ASTM A500 Grade C
*Pipe shall conform to ASTM A53, Grade B.
*Channels, Angles and plates shall conform to A36.
*All bolts shall be 3/4" High strength in accordance with ASTM A325 (UNO)
*Welding Electrodes for Carbon steel :E70xx

# of Copies	Revision/ Issue	Destination	Date
1	0	For Construction	11-14-2025

IRON FABRICATION SERVICES, LLC.

3029 M. Street, NW, Suite 202
Washington, DC 20007
Tel: 202-800-5599
Fax: 202-478-0303

Project Name and Address
MARYLAND AVENUE

Location: **1250 MARYLAND AVENUE SW WASHINGTON, DC 20024**

Contractor:
BALFOUR BEATTY

Approved for Fabrication by:	Signature

Contract # **224009**

Drawing # **E-10.00A**

Contract Item: **LEVEL-04 SLAB EXTENSION**

Ref: **SOW-10: (S109,2/A054)**

Date **01/ 20/ 2025**

Drawing Title: **SOW #10 LEVEL-04 DETAIL VIEW**

Scale VARIES