
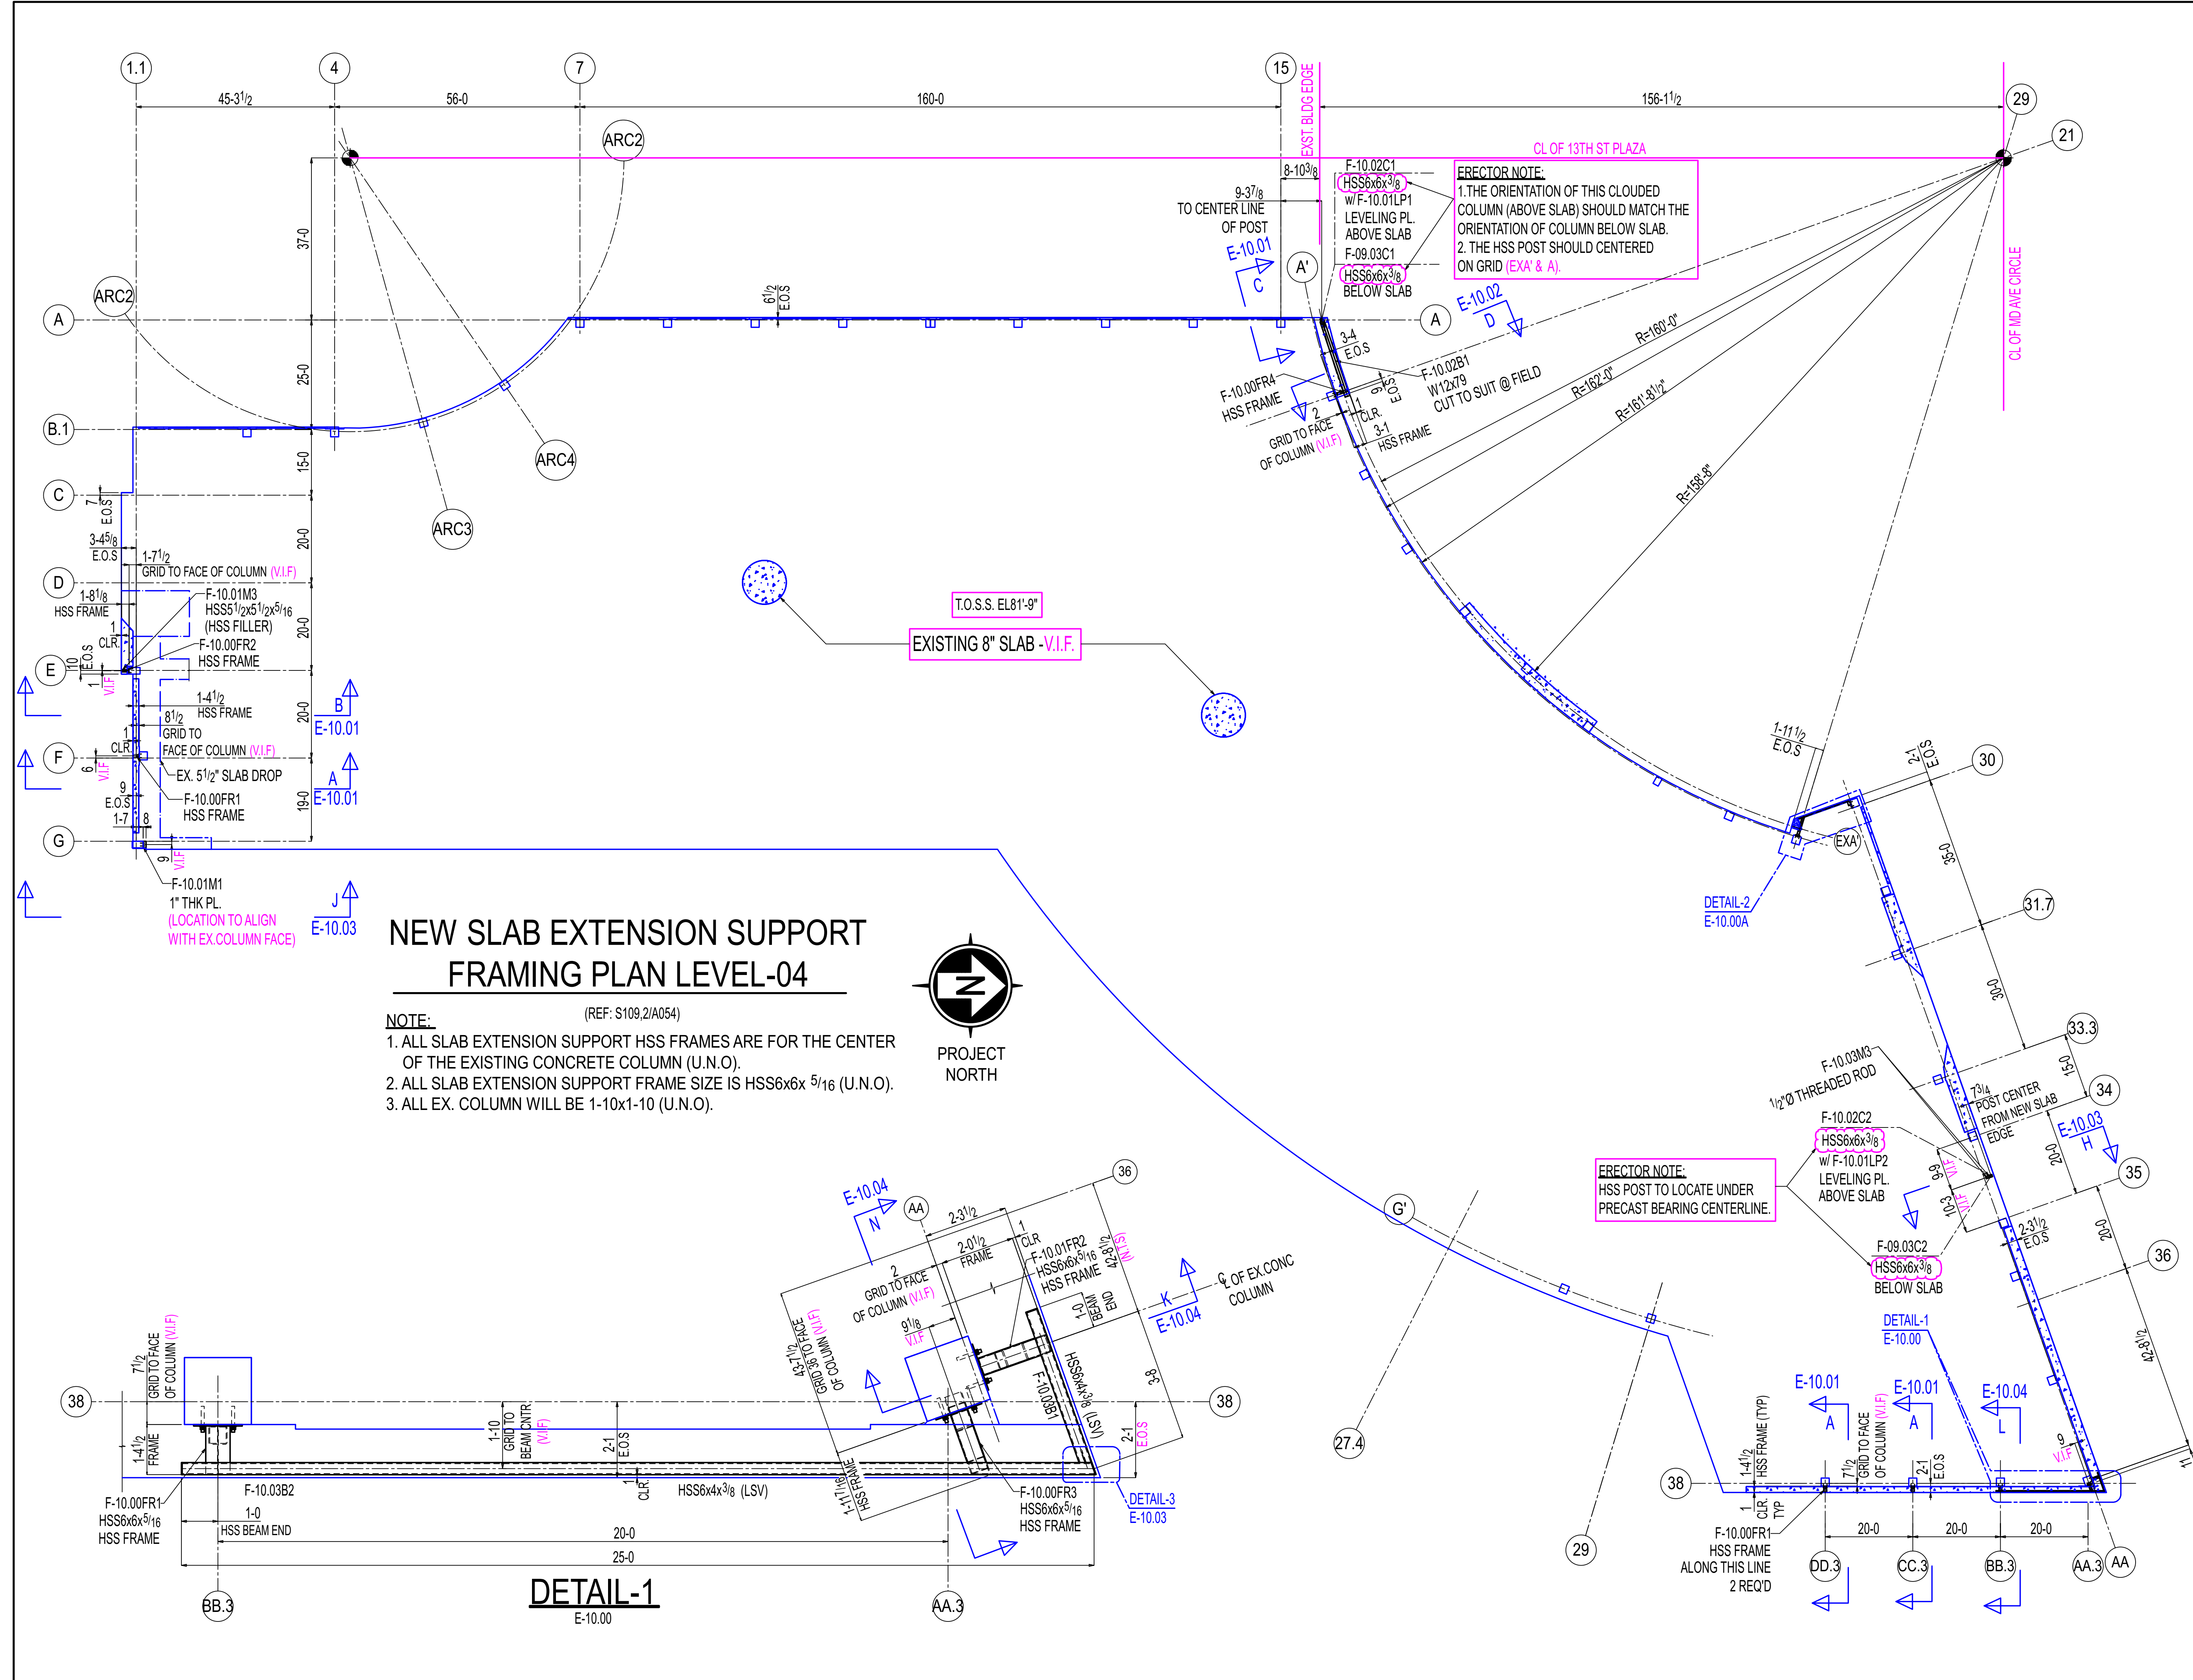


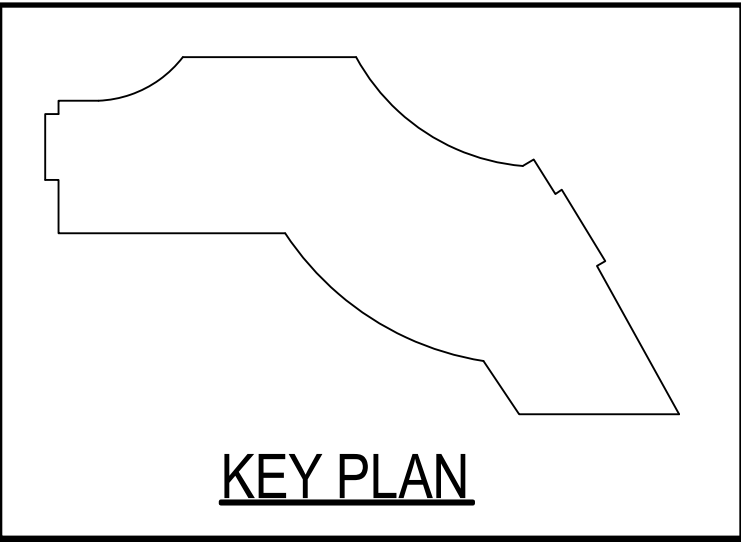


NEW SLAB EXTENSION SUPPORT FRAMING PLAN LEVEL-04

(REF: S109,2/A054)

NOTE:

1. ALL SLAB EXTENSION SUPPORT HSS FRAMES ARE FOR THE CENTER OF THE EXISTING CONCRETE COLUMN (U.N.O).
2. ALL SLAB EXTENSION SUPPORT FRAME SIZE IS HSS6x6x 5/16 (U.N.O).
3. ALL EX. COLUMN WILL BE 1-10x1-10 (U.N.O).

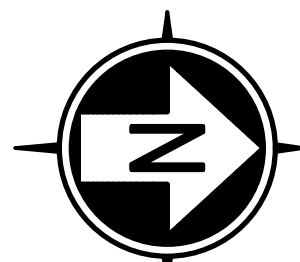

PROJECT
NORTH

General Notes			
*Structural steel shall conform to ASTM-A992.			
*Structural SQR/RND tubing conform to ASTM A500 Grade C			
*Pipe shall conform to ASTM A53, Grade B.			
*Channels, Angles and plates shall conform to A36.			
*All bolts shall be 3/4" High strength in accordance with ASTM A325 (UNO)			
*Welding Electrodes for Carbon steel :E70xx			
# of Copies	Revision/ Issue	Destination	Date
5	0	For Construction	11-14-2025
4	D	For Re-Approval	10-24-2025
3	C	For Re-Approval	09-19-2025
2	B	For Re-Approval	06-23-2025
1	A	For Approval	02-25-2025

IRON FABRICATION SERVICES, LLC.

3029 M. Street, NW, Suite 202
Washington, DC 20007
Tel: 202-800-5599
Fax: 202-478-0303

Project Name and Address
MARYLAND AVENUE
Location: **1250 MARYLAND AVENUE SW
WASHINGTON, DC 20024**

Contractor:
BALFOUR BEATTY

Approved for Fabrication by: _____
Signature

Contract #	224009	Drawing #	E-10.00
Contract Item:	LEVEL-04 SLAB EXTENSION		
Ref:	SOW-10: (S109,2/A054)		
Date	01/ 20/ 2025	Drawing Title:	SOW #10 LEVEL-04 NEW SLAB EXTENSION SUPPORT FRAMING PLAN
Scale	VARIES		