


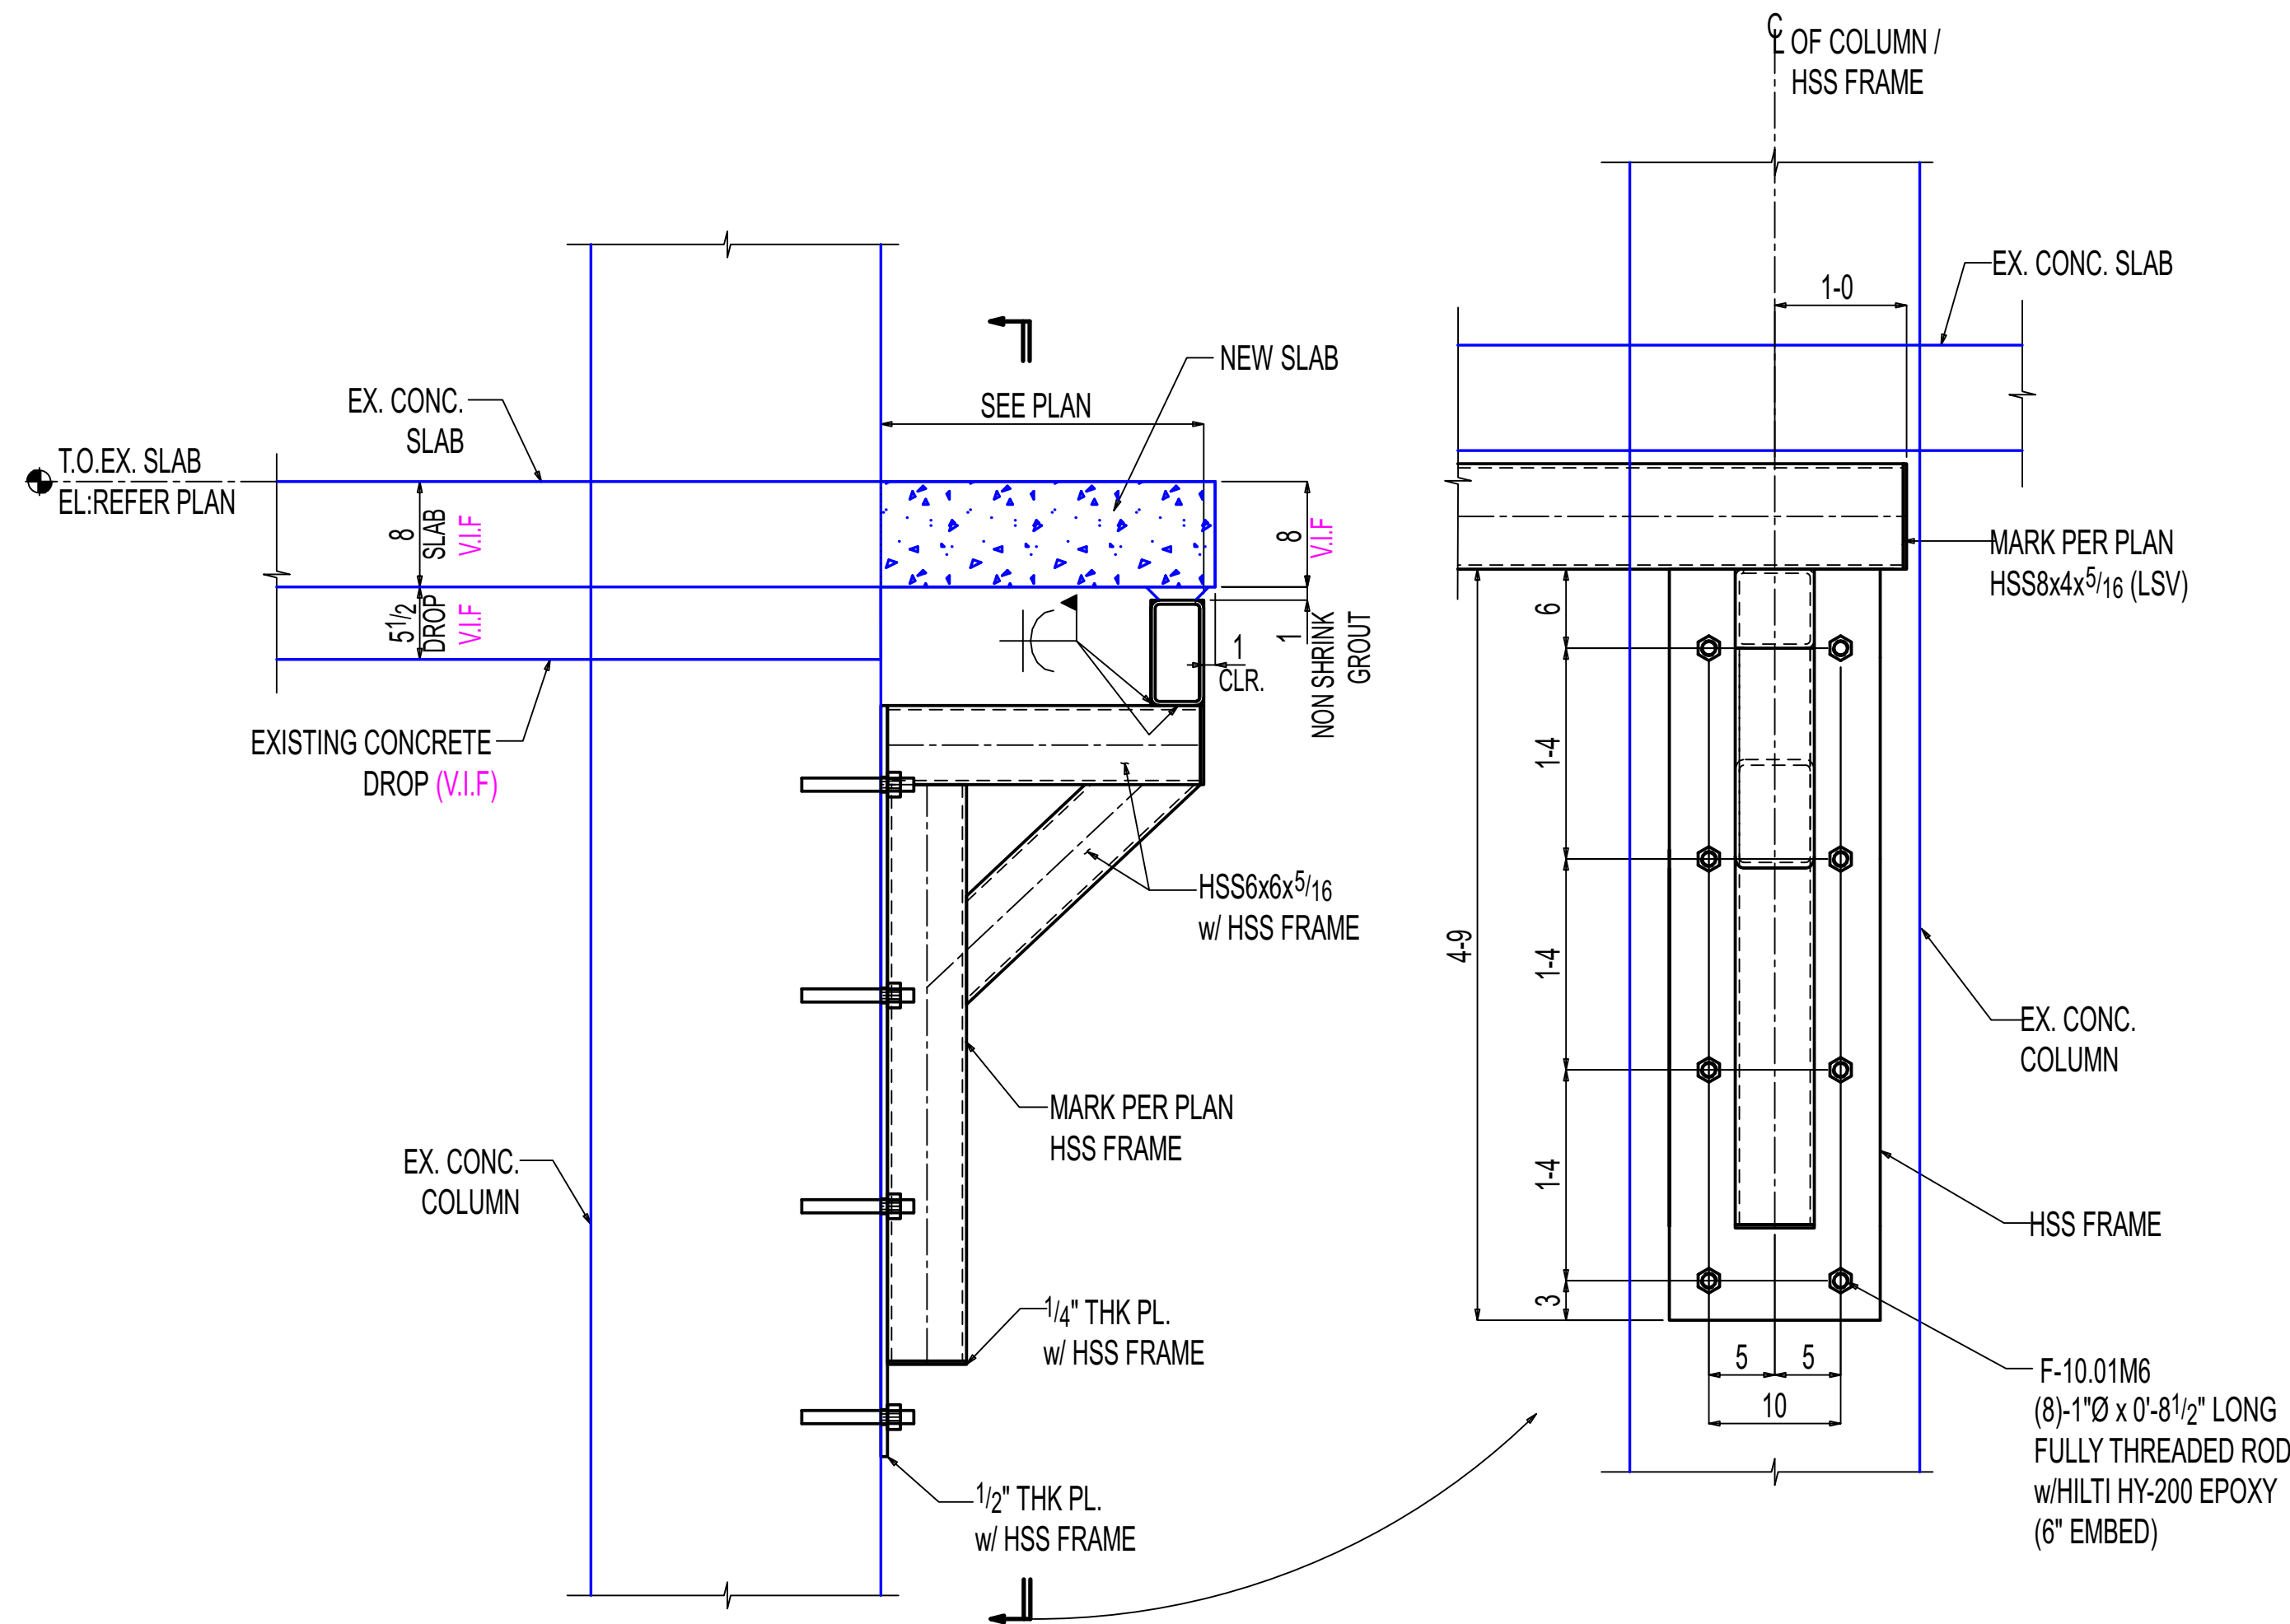


K-K

E-10.00

(REF: 10/S315)

OTHERS NOT SHOWN FOR CLARITY


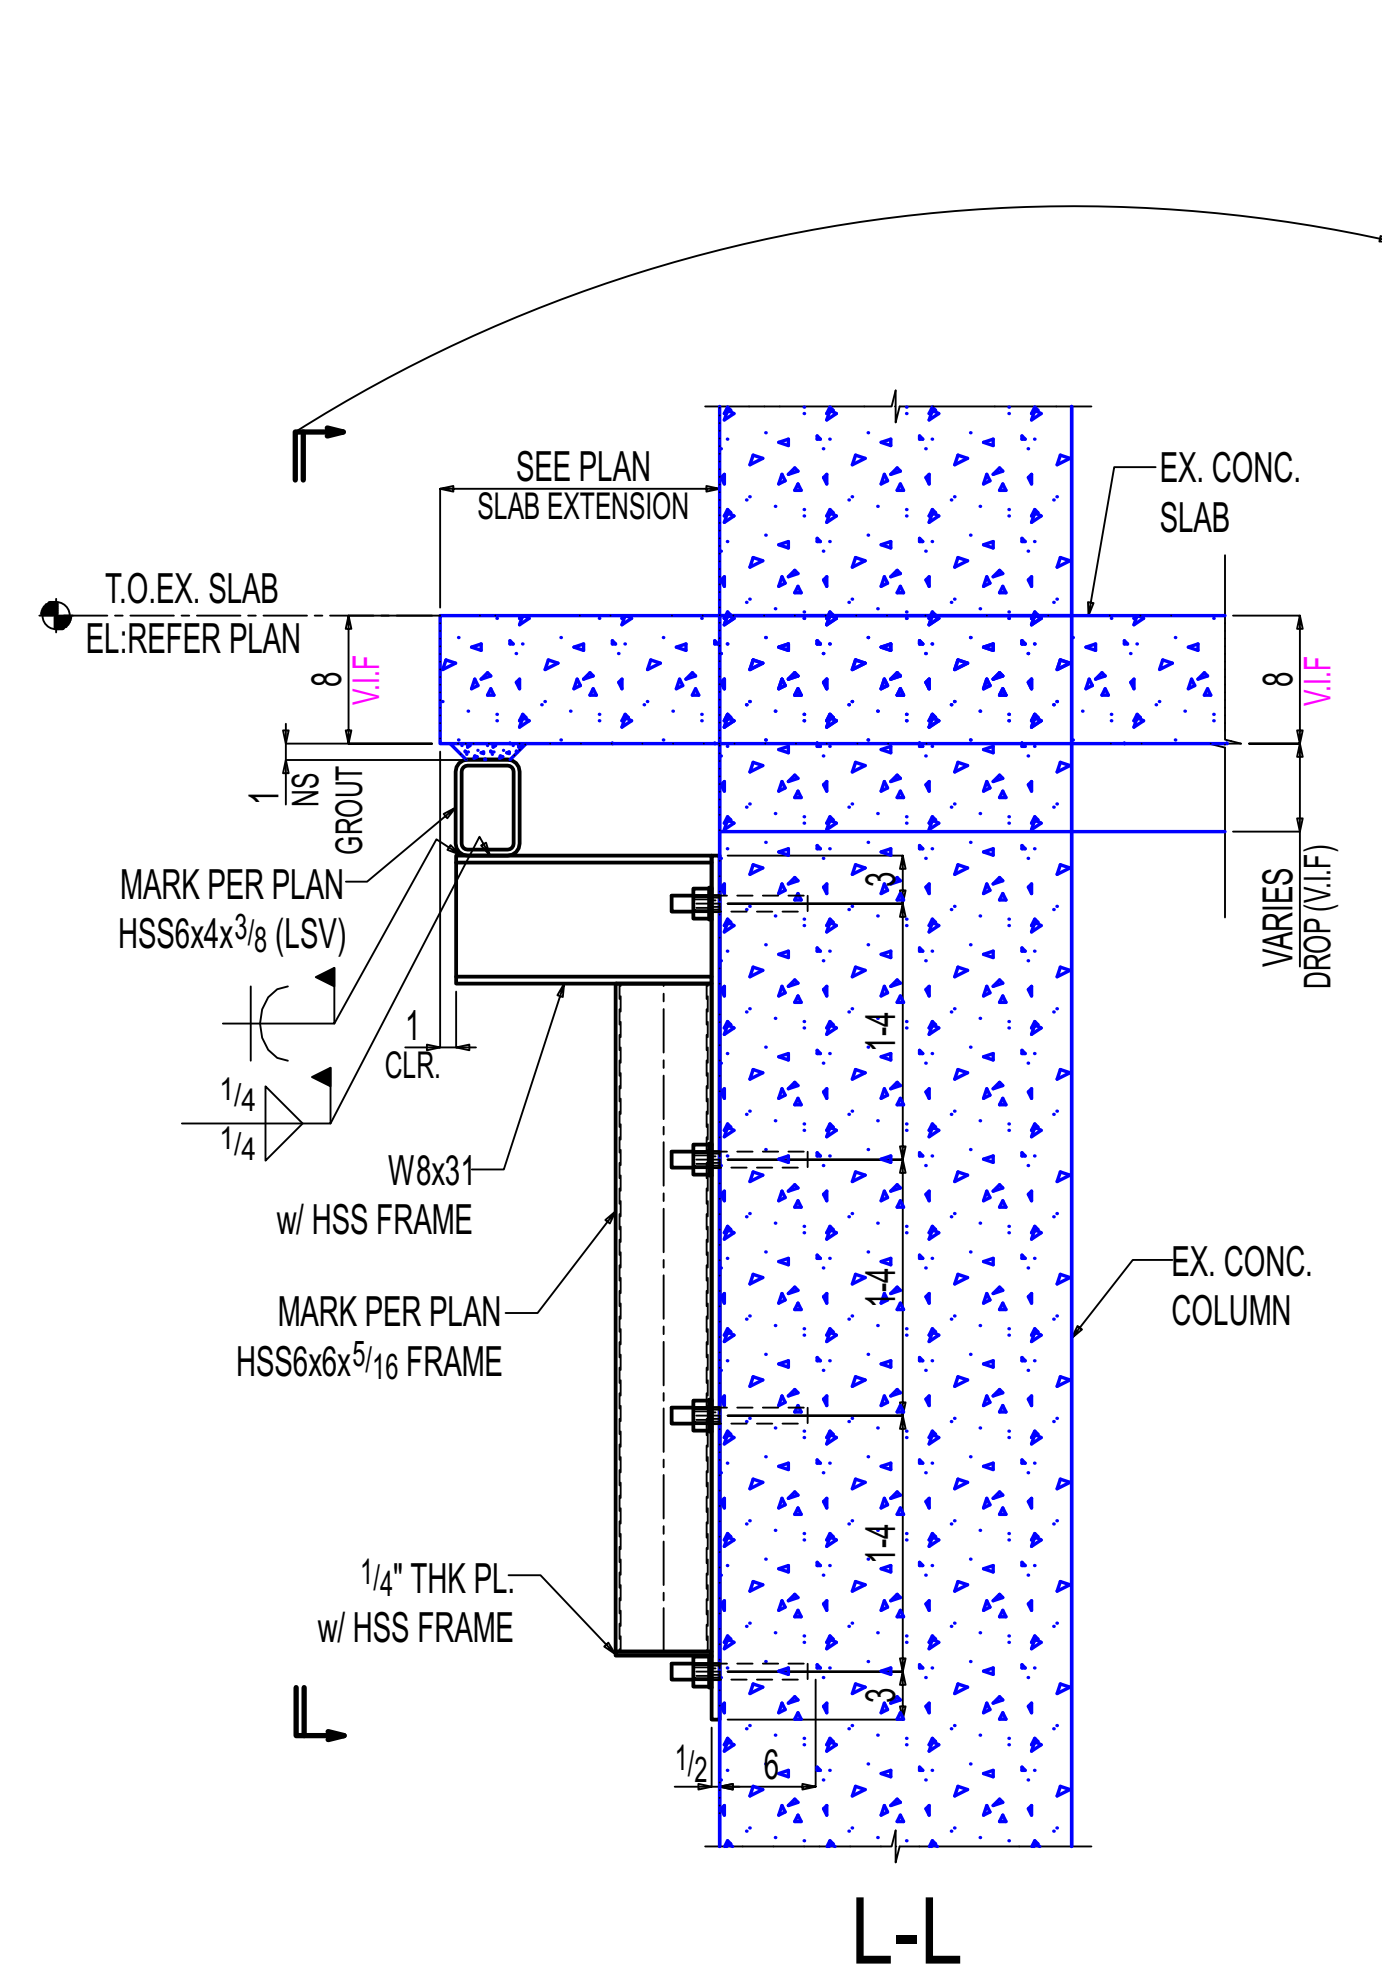


L-L

E-10.00

(REF: 10/S315)

OTHERS NOT SHOWN FOR CLARITY

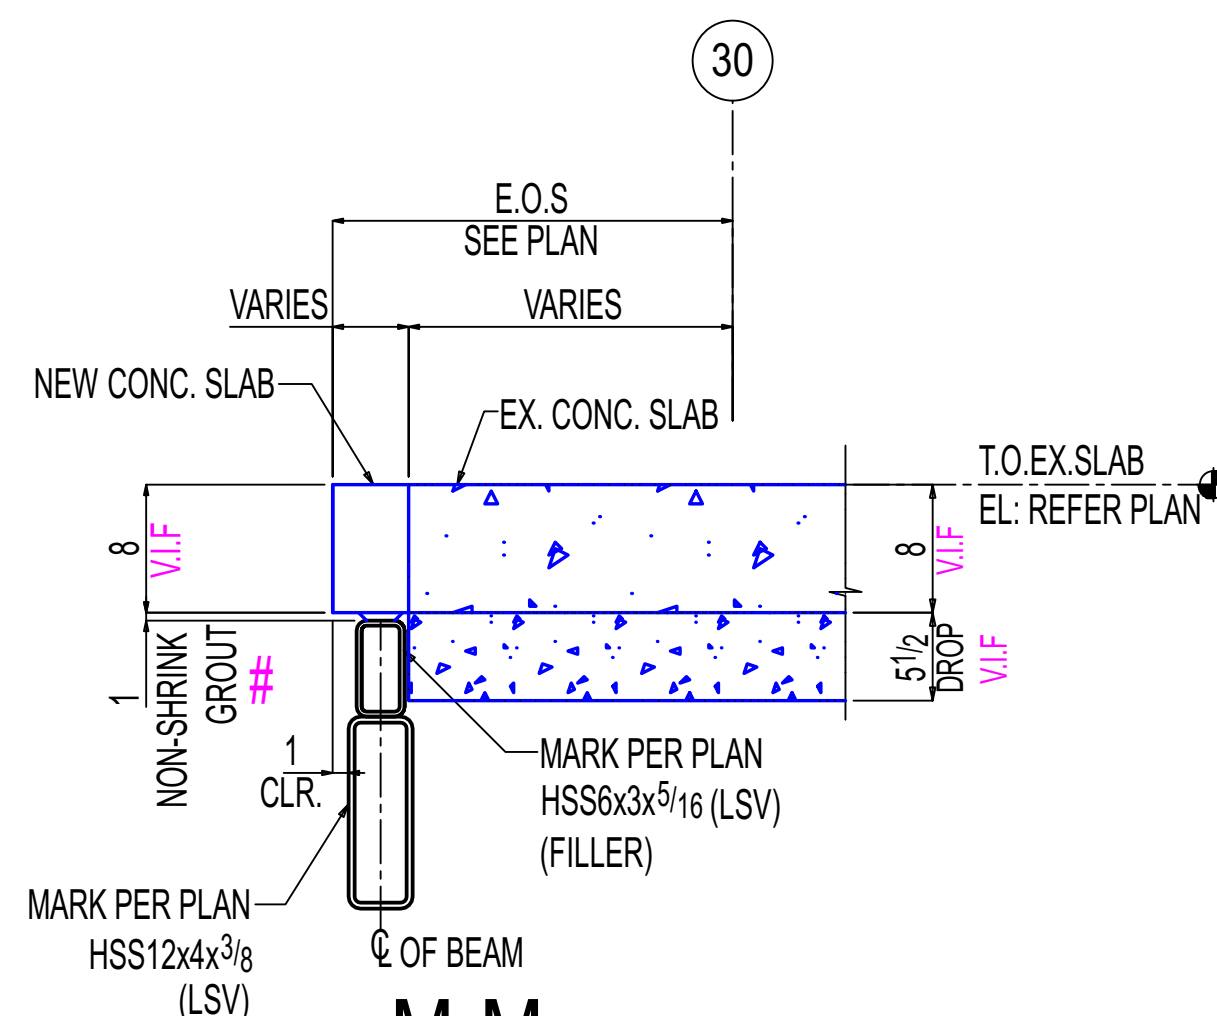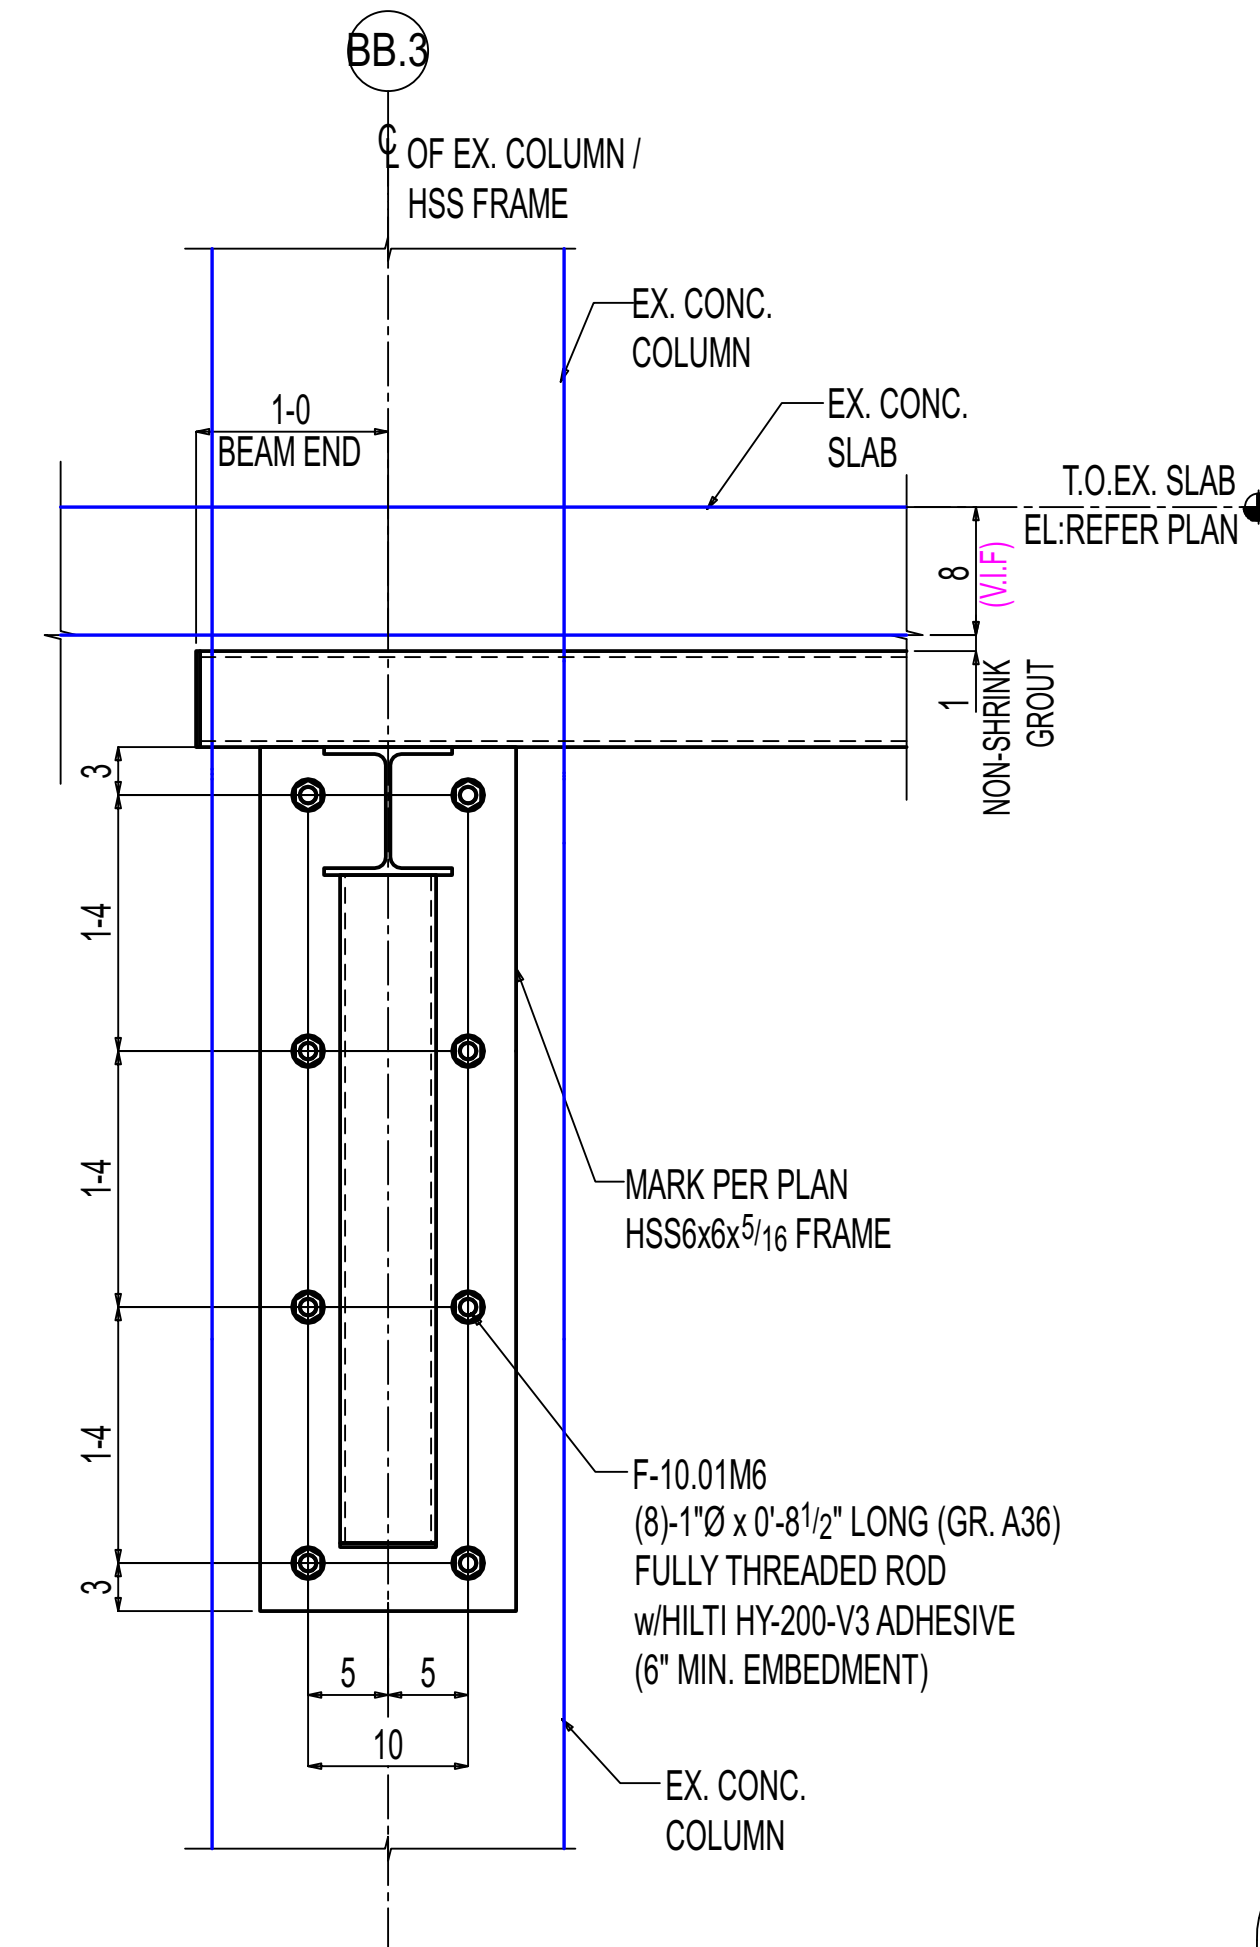


M-M

E-10.00A

(REF: 4/S315)

OTHERS NOT SHOWN FOR CLARITY

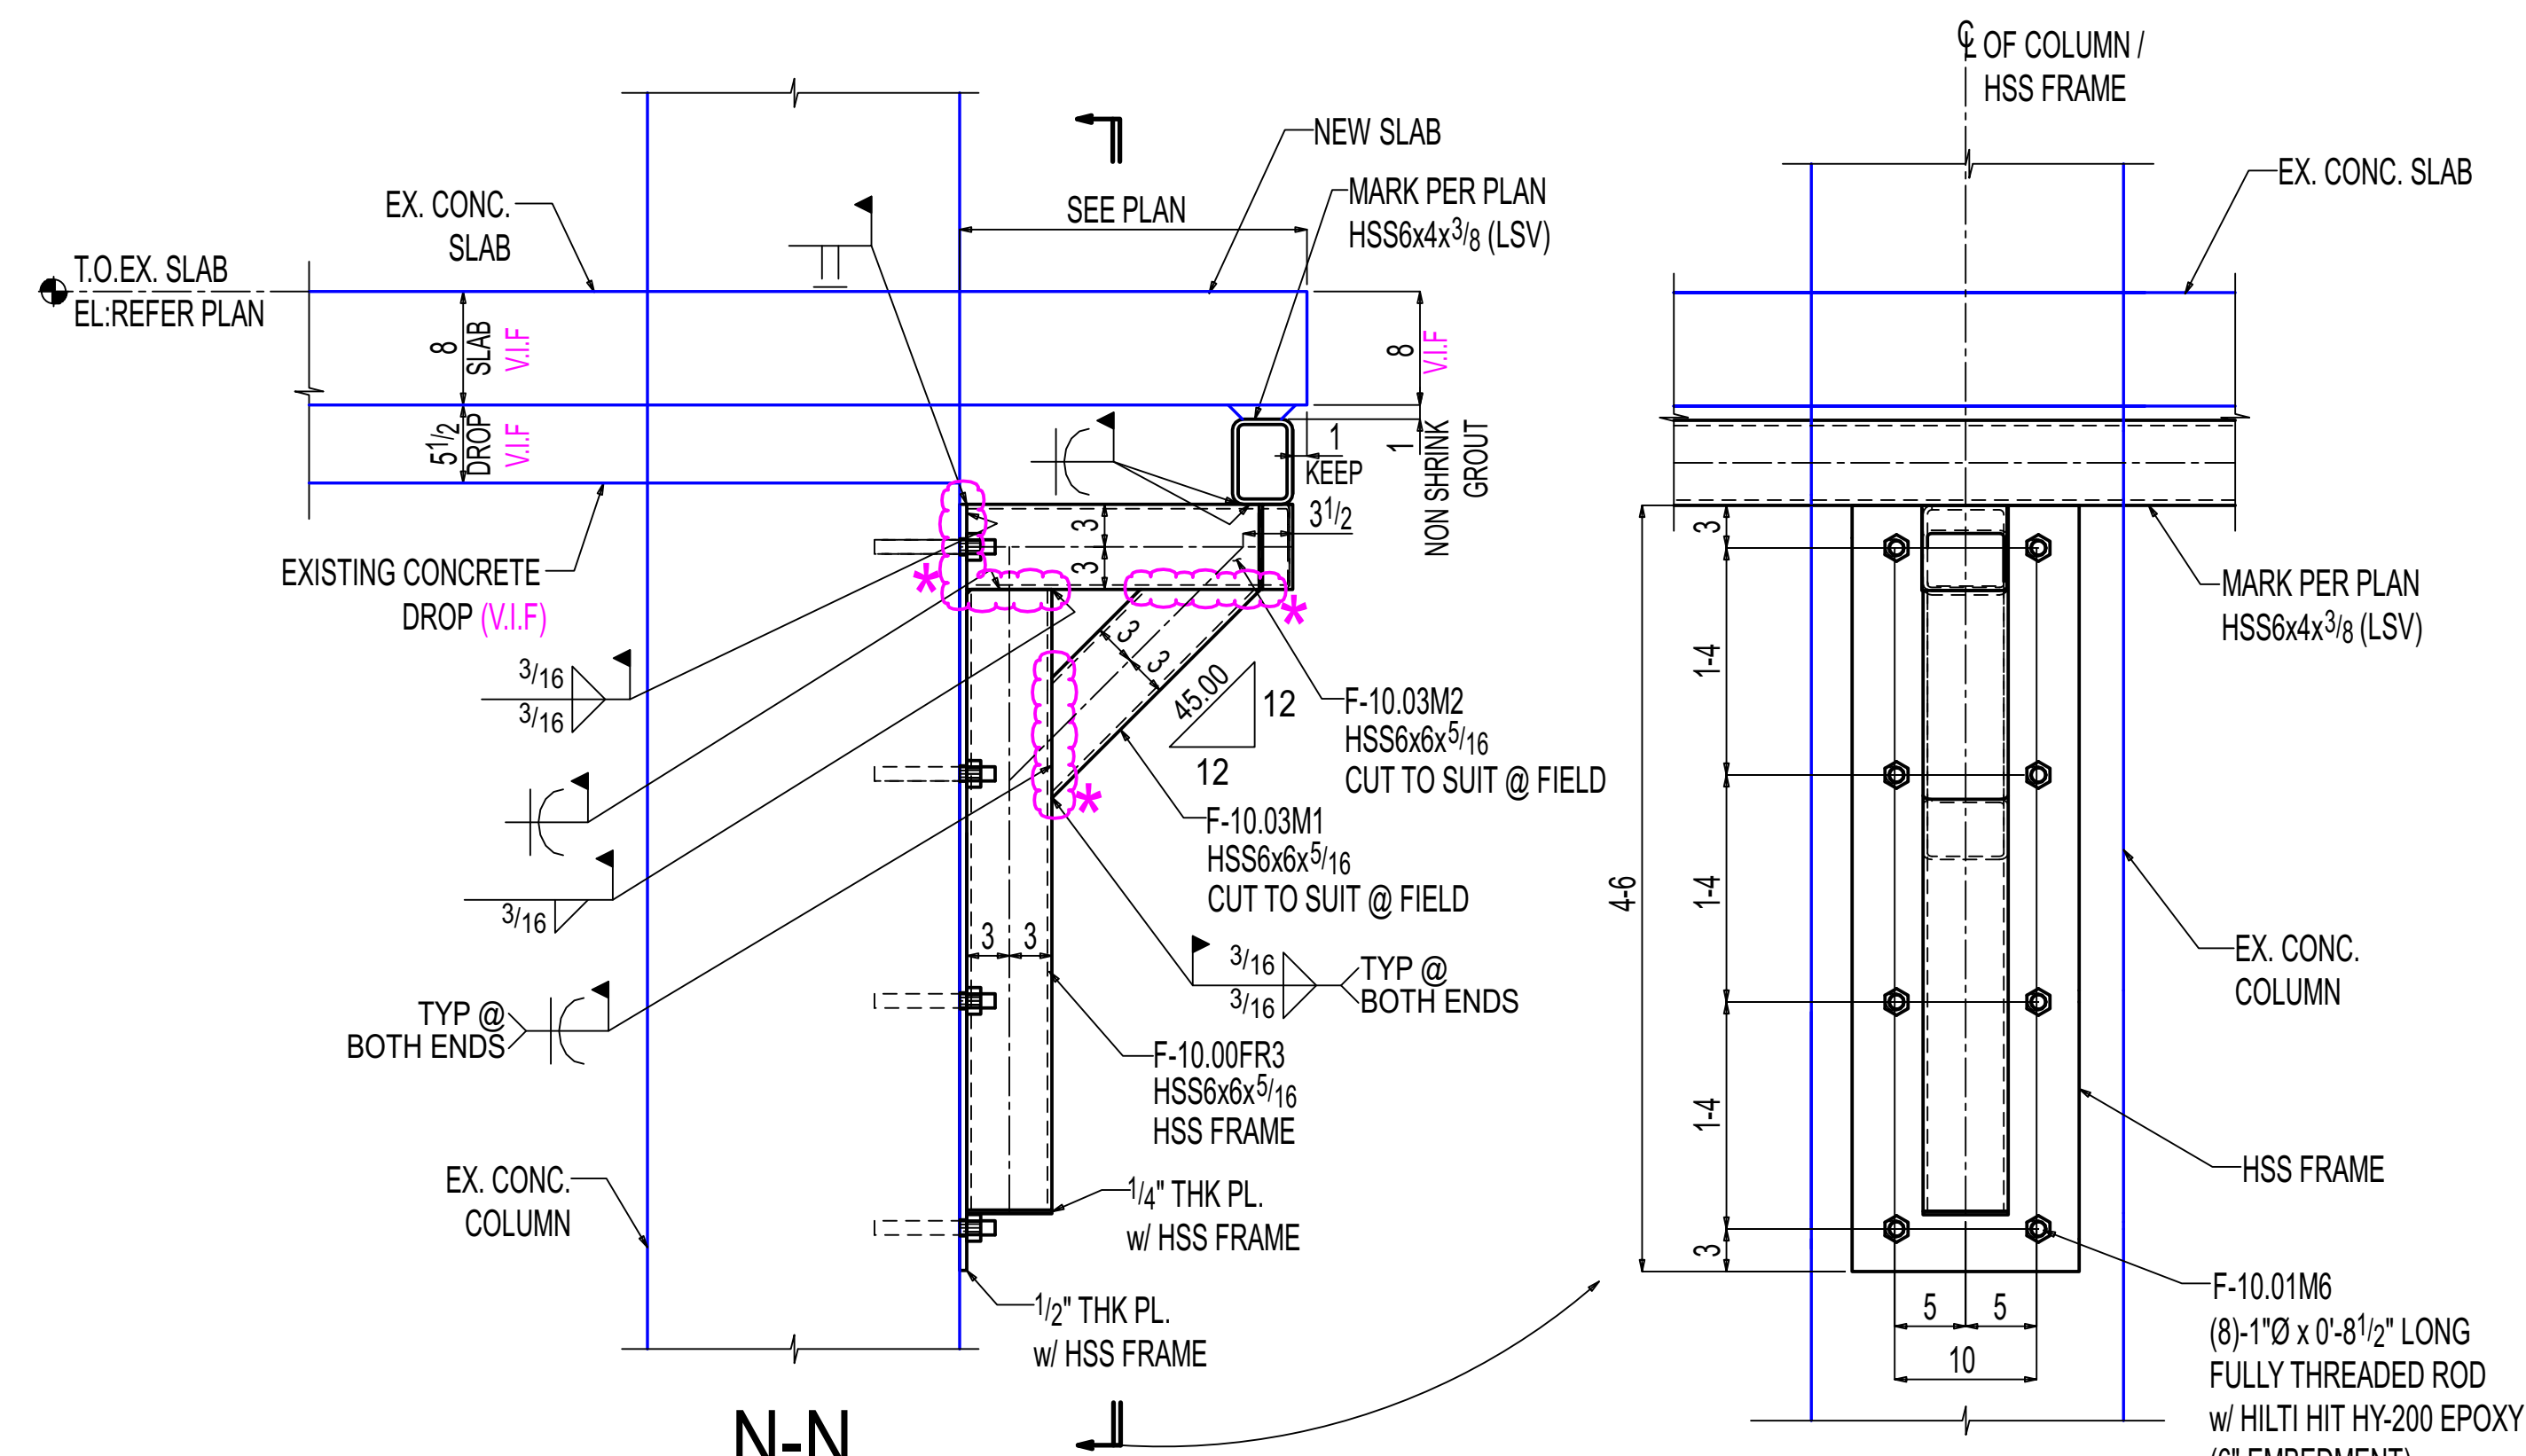

N-N

E-10.00

(REF: 10/S315)

OTHERS NOT SHOWN FOR CLARITY

ERECTOR NOTE:

* FIELD CUT HSS6x6 ENDS TO SUIT EXISTING DROP.

SHOP / ERECTOR NOTE:
LOCATE EXISTING REBAR PRIOR TO FABRICATION OF PLATE.
DO NOT DRILL THROUGH REBAR.

ERECTOR NOTE:
PROVIDE 1\"/>

General Notes

- *Structural steel shall conform to ASTM-A992.
- *Structural SQR/RND tubing conform to ASTM A500 Grade C
- *Pipe shall conform to ASTM A53, Grade B.
- *Channels, Angles and plates shall conform to A36.
- *All bolts shall be 3/4\" High strength in accordance with ASTM A325 (UNO)
- *Welding Electrodes for Carbon steel :E70xx

# of Copies	Revision/ Issue	Destination	Date
3	0	For Construction	11-14-2025
2	B	For Re-Approval	10-24-2025
1	A	For Approval	09-19-2025

IRON FABRICATION SERVICES, LLC.

3029 M. Street, NW, Suite 202
Washington, DC 20007
Tel: 202-800-5599
Fax: 202-478-0303

Project Name and Address
MARYLAND AVENUE

Location: **1250 MARYLAND AVENUE SW
WASHINGTON, DC 20024**

Contractor:
BALFOUR BEATTY

Approved for Fabrication by: _____

Signature _____

Contract # **224009** Drawing # **E-10.04**

Contract Item: **LEVEL-04
SLAB EXTENSION**

Ref: **SOW-10: 3,4,5&6 / S307**

Date
01/20/2025

Scale
VARIES

Drawing Title:
**SOW #10 LEVEL-04 NEW
SLAB EXTENSION SUPPORT
SECTIONS**