

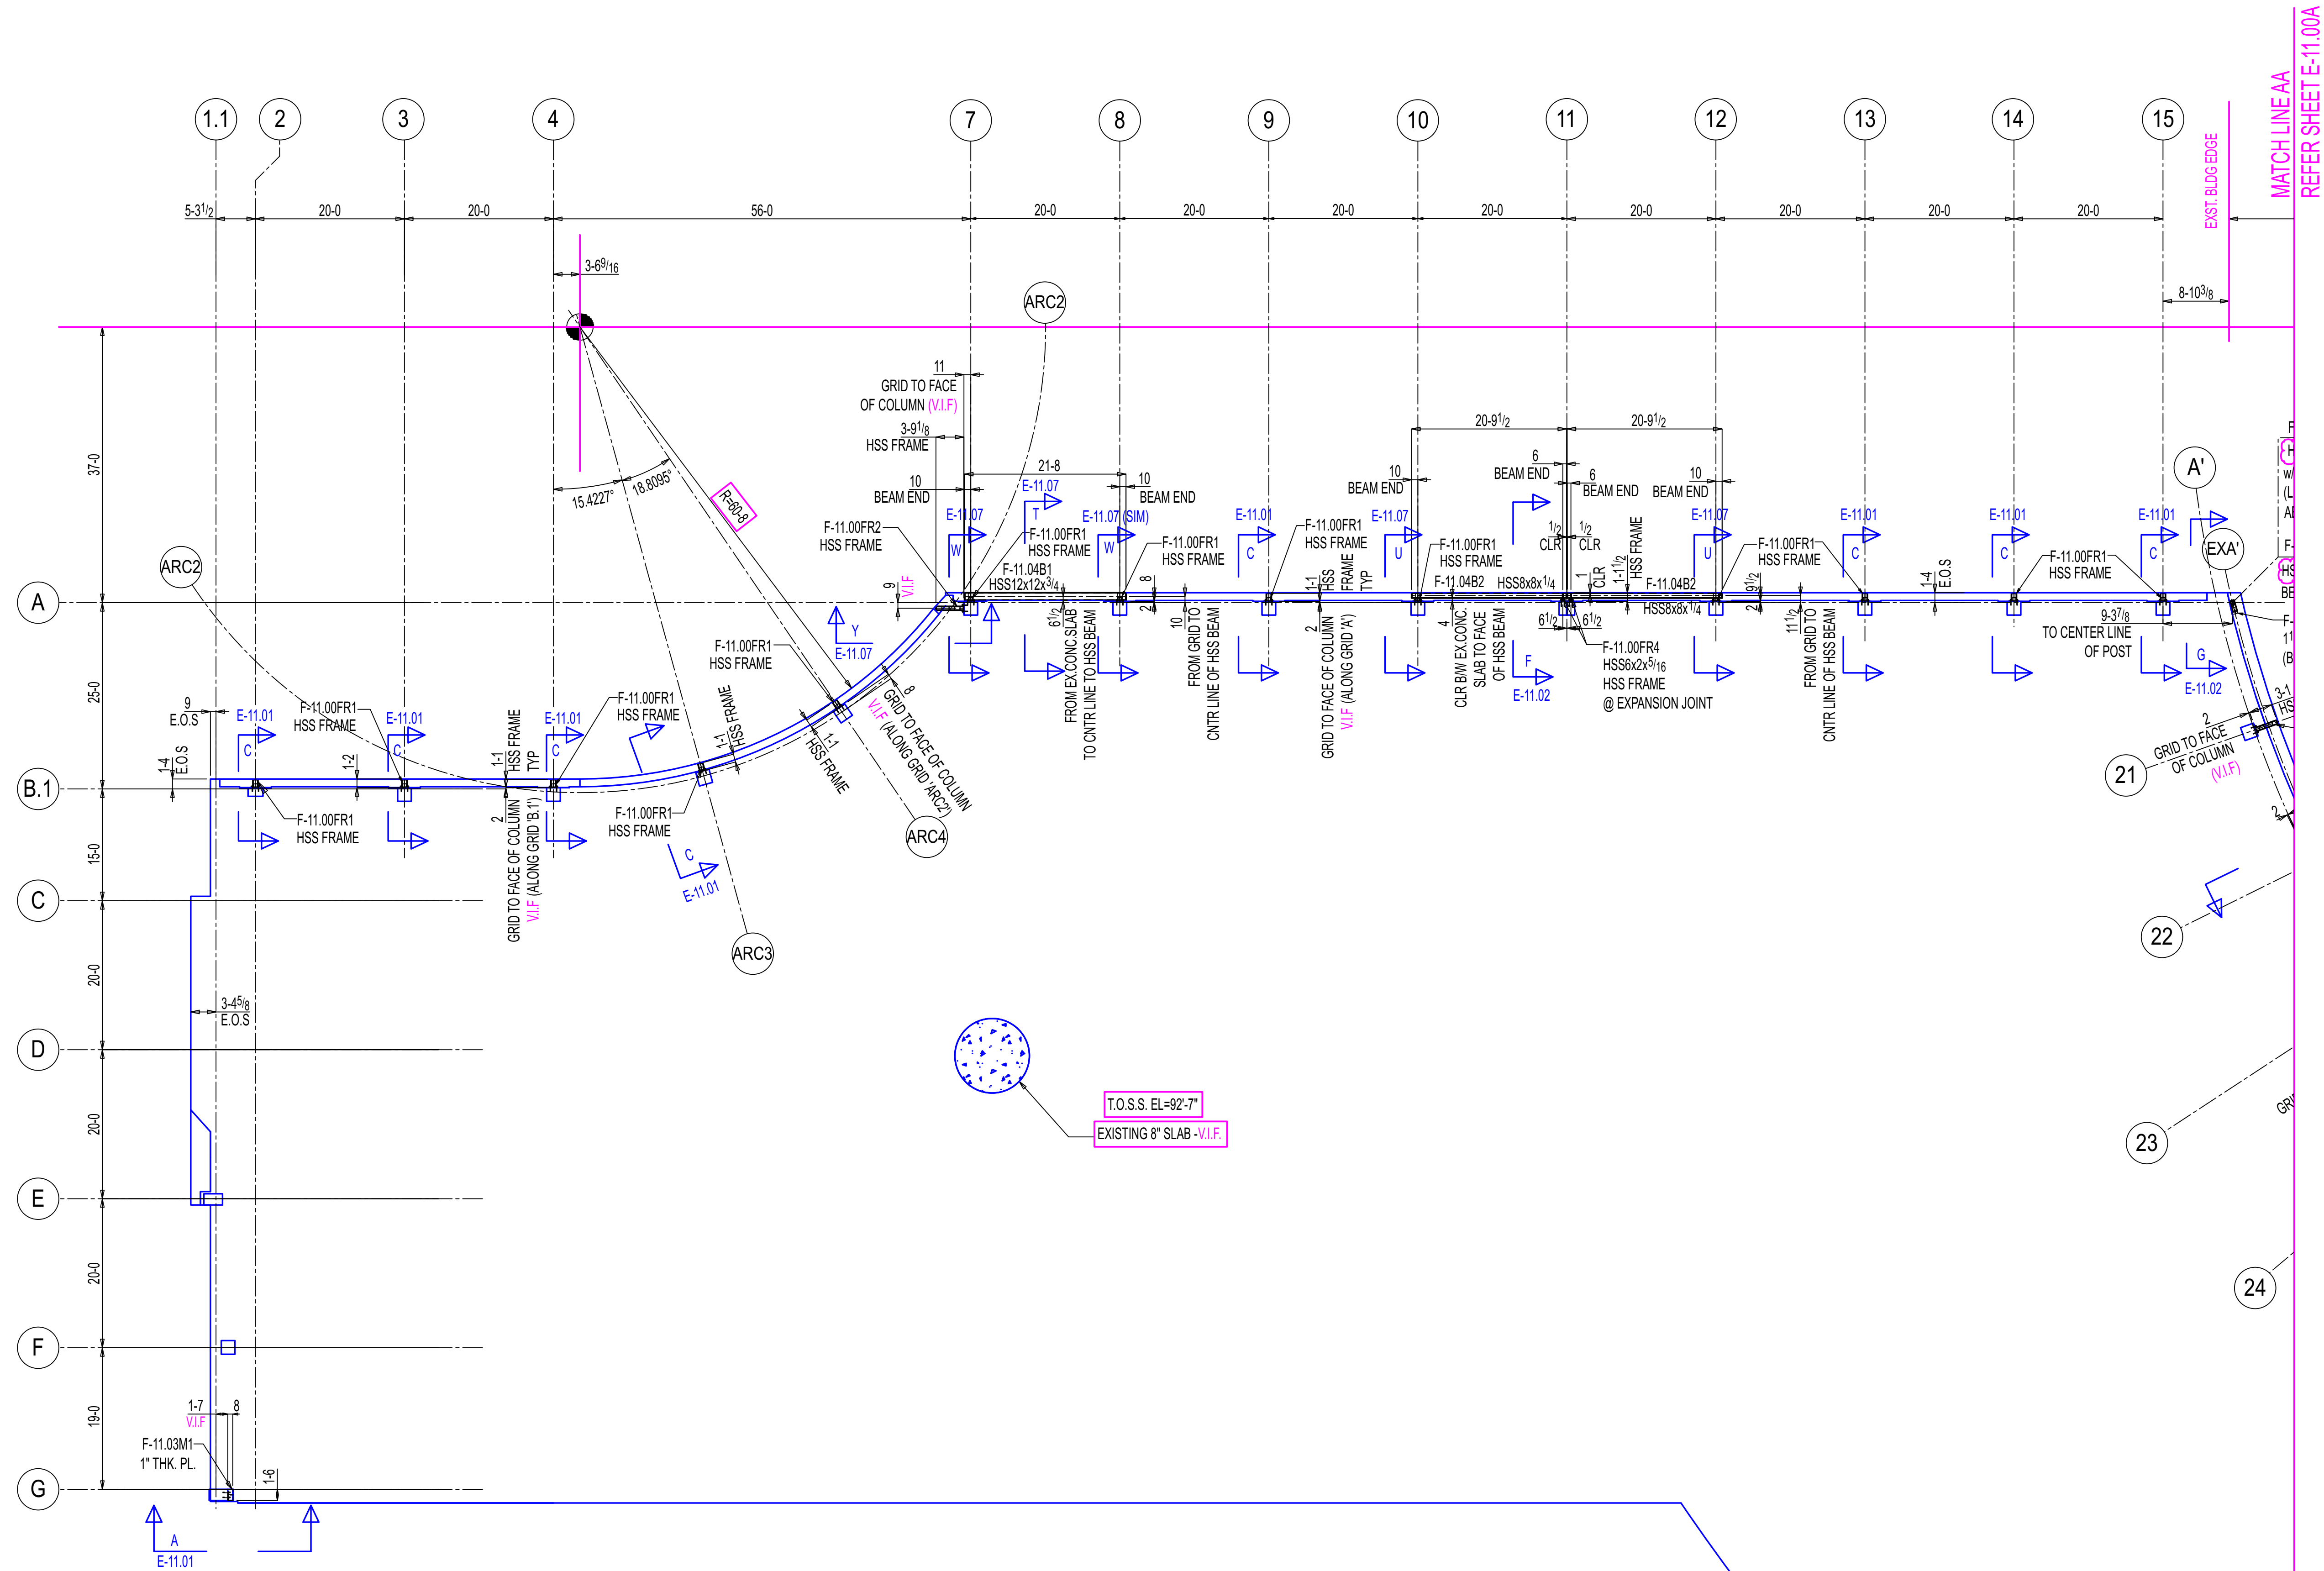


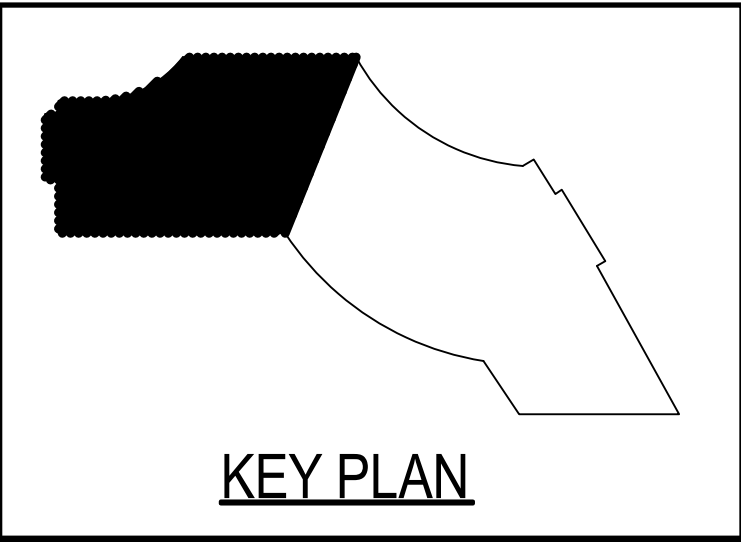

NEW SLAB EXTENSION SUPPORT FRAMING PLAN LEVEL-05

- NOTE:
1. ALL SLAB EXTENSION SUPPORT HSS FRAMES ARE FOR THE CENTER OF THE EXISTING CONCRETE COLUMN (U.N.O.).
 2. ALL SLAB EXTENSION SUPPORT FRAME SIZE IS HSS6x6x 5/16 (U.N.O.).

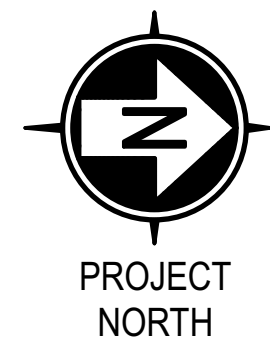

General Notes			
*Structural steel shall conform to ASTM-A992.			
*Structural SQR/RND tubing conform to ASTM A500 Grade C			
*Pipe shall conform to ASTM A53, Grade B.			
*Channels, Angles and plates shall conform to A36.			
*All bolts shall be 3/4" High strength in accordance with ASTM A325 (UNO)			
*Welding Electrodes for Carbon steel :E70xx			
# of Copies	Revision/ Issue	Destination	Date
5	0	For Construction	11-14-2025
4	D	For Re-Approval	10-24-2025
3	C	For Re-Approval	09-19-2025
2	B	For Re-Approval	06-23-2025
1	A	For Approval	02-25-2025

IRON FABRICATION SERVICES, LLC.

3029 M. Street, NW, Suite 202
Washington, DC 20007
Tel: 202-800-5599
Fax: 202-478-0303


Project Name and Address
MARYLAND AVENUE

Location: **1250 MARYLAND AVENUE SW
WASHINGTON, DC 20024**

Contractor:
BALFOUR BEATTY

Approved for Fabrication by: _____
Signature

Contract #	224009	Drawing #	E-11.00
Contract Item:	LEVEL-05 SLAB EXTENSION		
Ref:	SOW-11: (S110,1/A055)		
Date	01/20/2025	Drawing Title:	SOW #11 LEVEL-05 NEW SLAB EXTENSION SUPPORT FRAMING PLAN
Scale	VARIES		

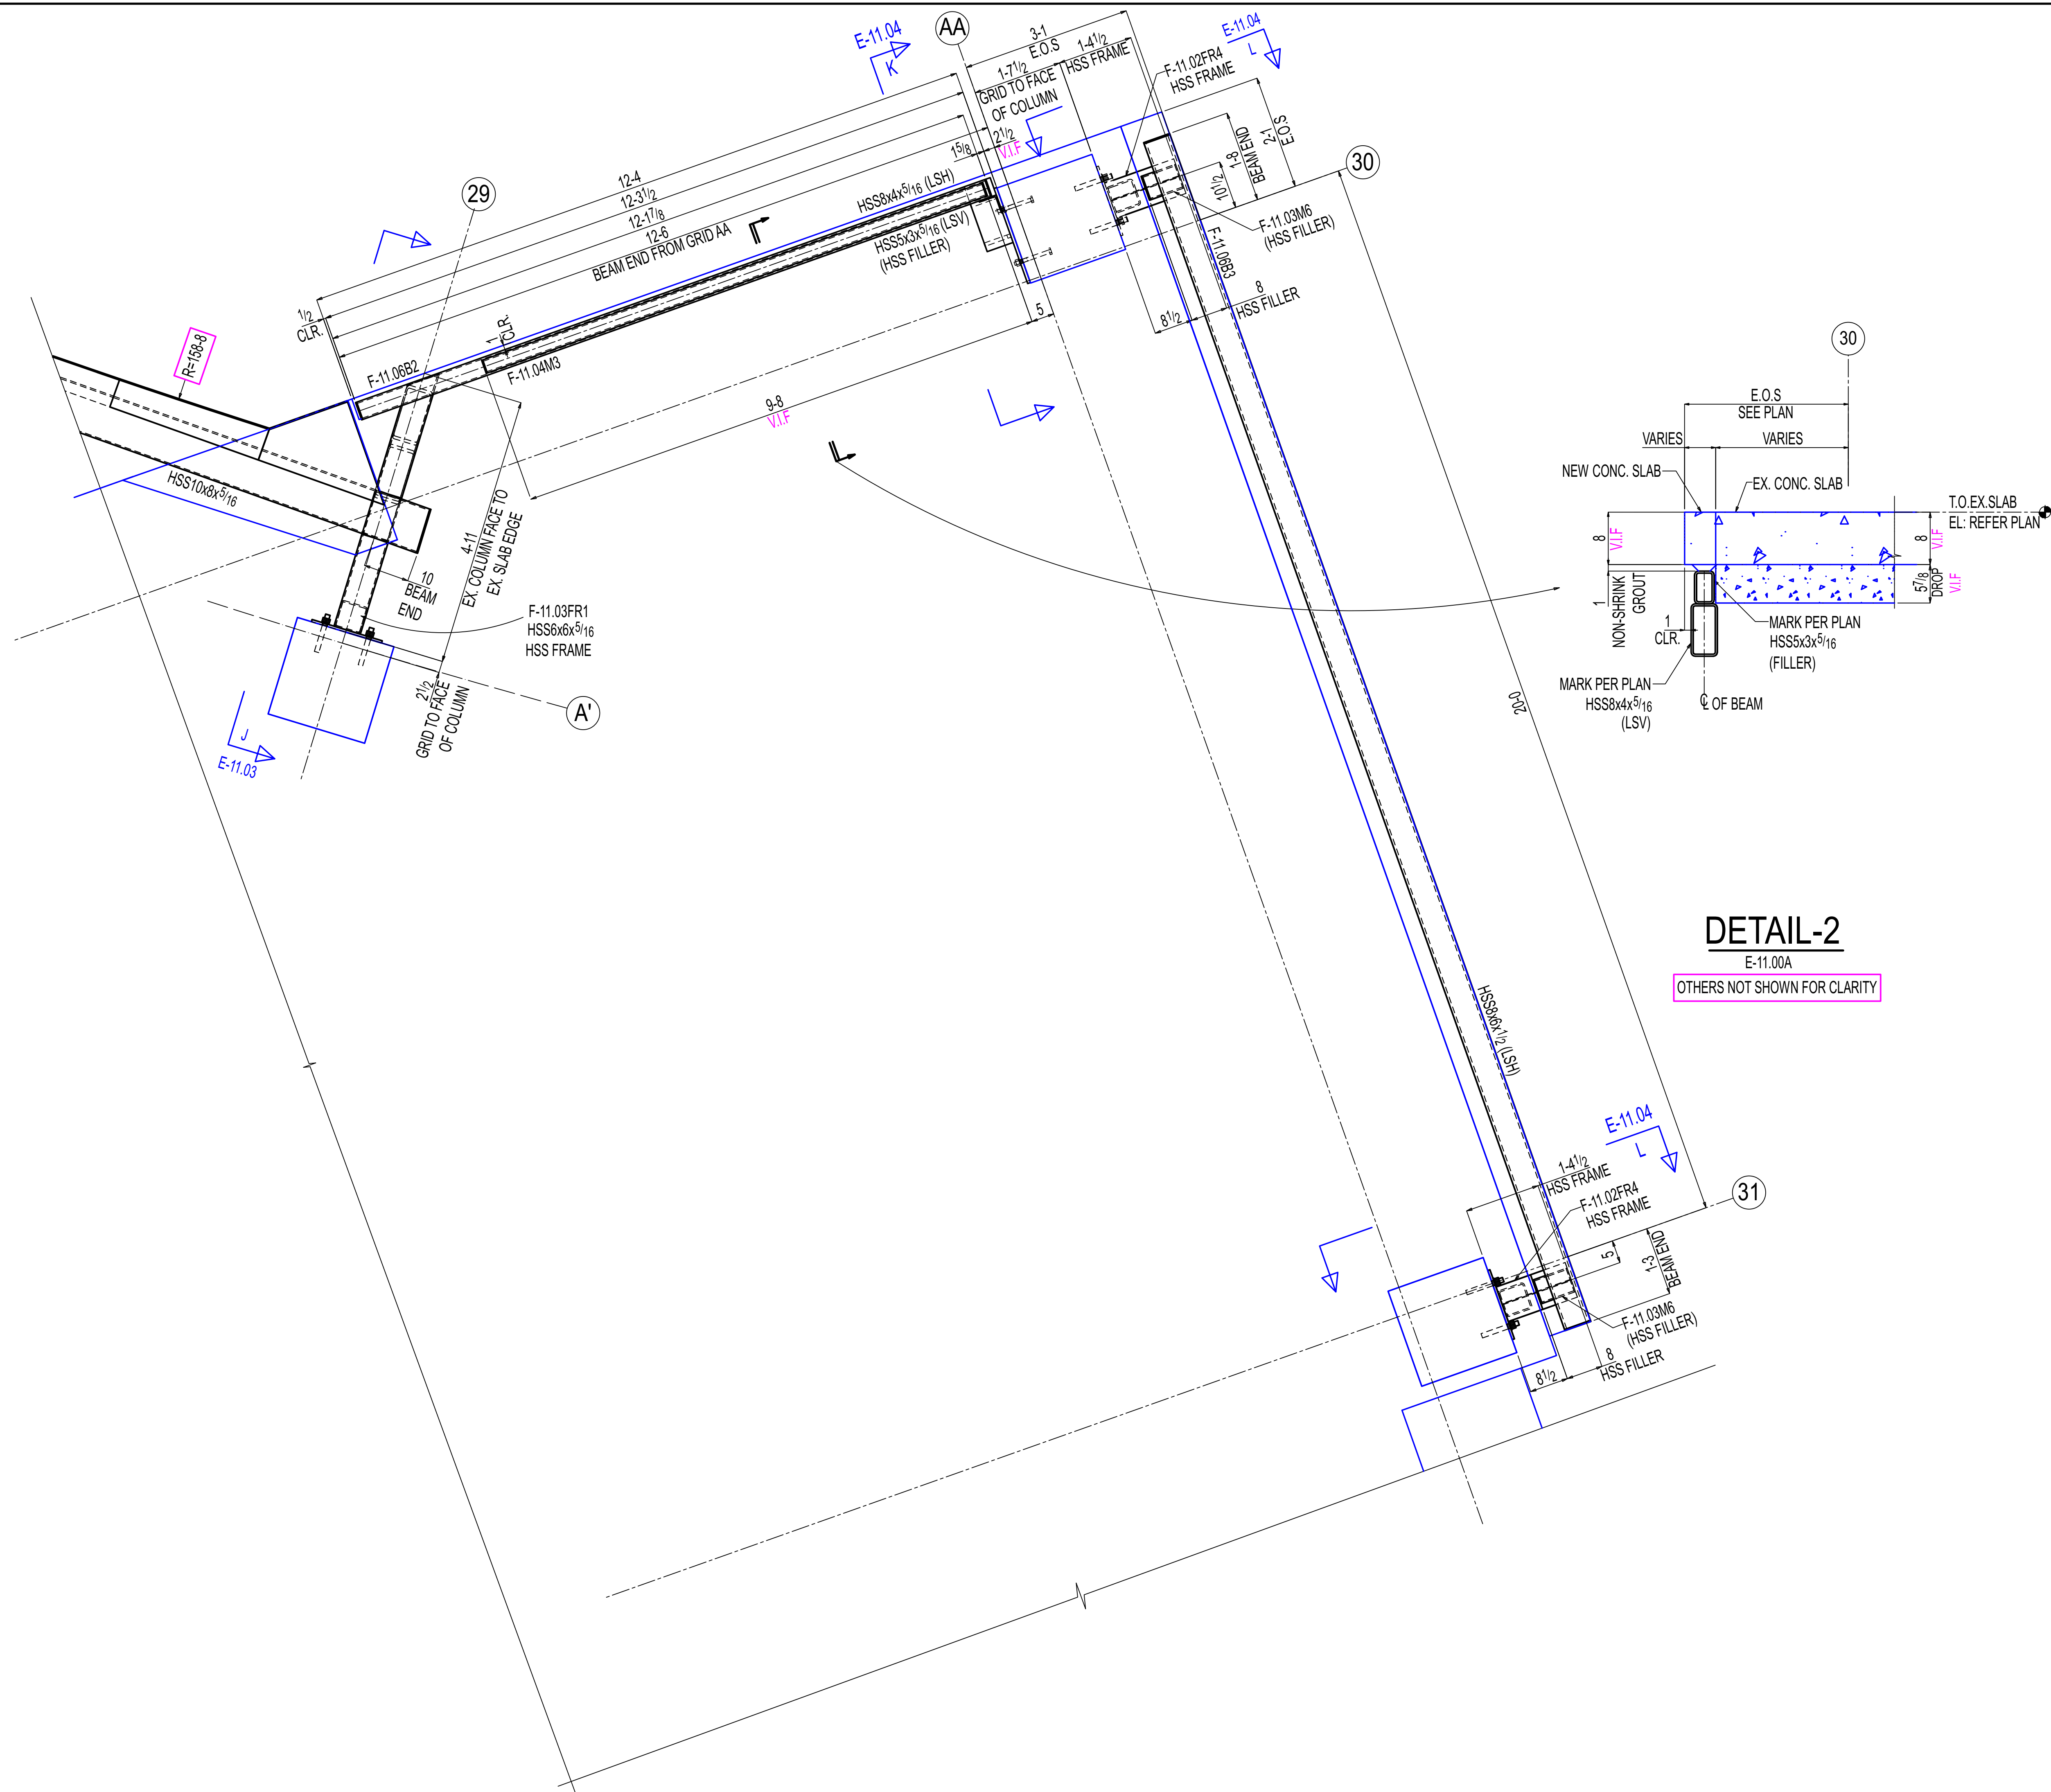

E-11.00A

OTHERS NOT SHOWN FOR CLARITY

- *Structural steel shall conform to ASTM-A992.
- *Structural SQR/RND tubing conform to ASTM A500 Grade C
- *Pipe shall conform to ASTM A53, Grade B.
- *Channels, Angles and plates shall conform to A36.
- *All bolts shall be 3/4" High strength in accordance with ASTM A325 (UNO)
- *Welding Electrodes for Carbon steel :E70xx


1	0	For Construction	11-14-2025
# of Copies	Revision/Issue	Destination	Date



3029 M. Street, NW, Suite 202
Washington, DC 20007
Tel: 202-800-5599
Fax: 202-478-0303

Location: **1250 MARYLAND AVENUE SW**
WASHINGTON, DC 20024

Approved for Fabrication by:	Signature
------------------------------	-----------

Contract # 224009		Drawing # E-11.00B
Contract Item: LEVEL-05 SLAB EXTENSION		
Ref: SOW-11: (S110,1/A055)		
Date 01/20/2025	Drawing Title: SOW #11 LEVEL-05 DETAIL VIEW	
Scale VARIAS		

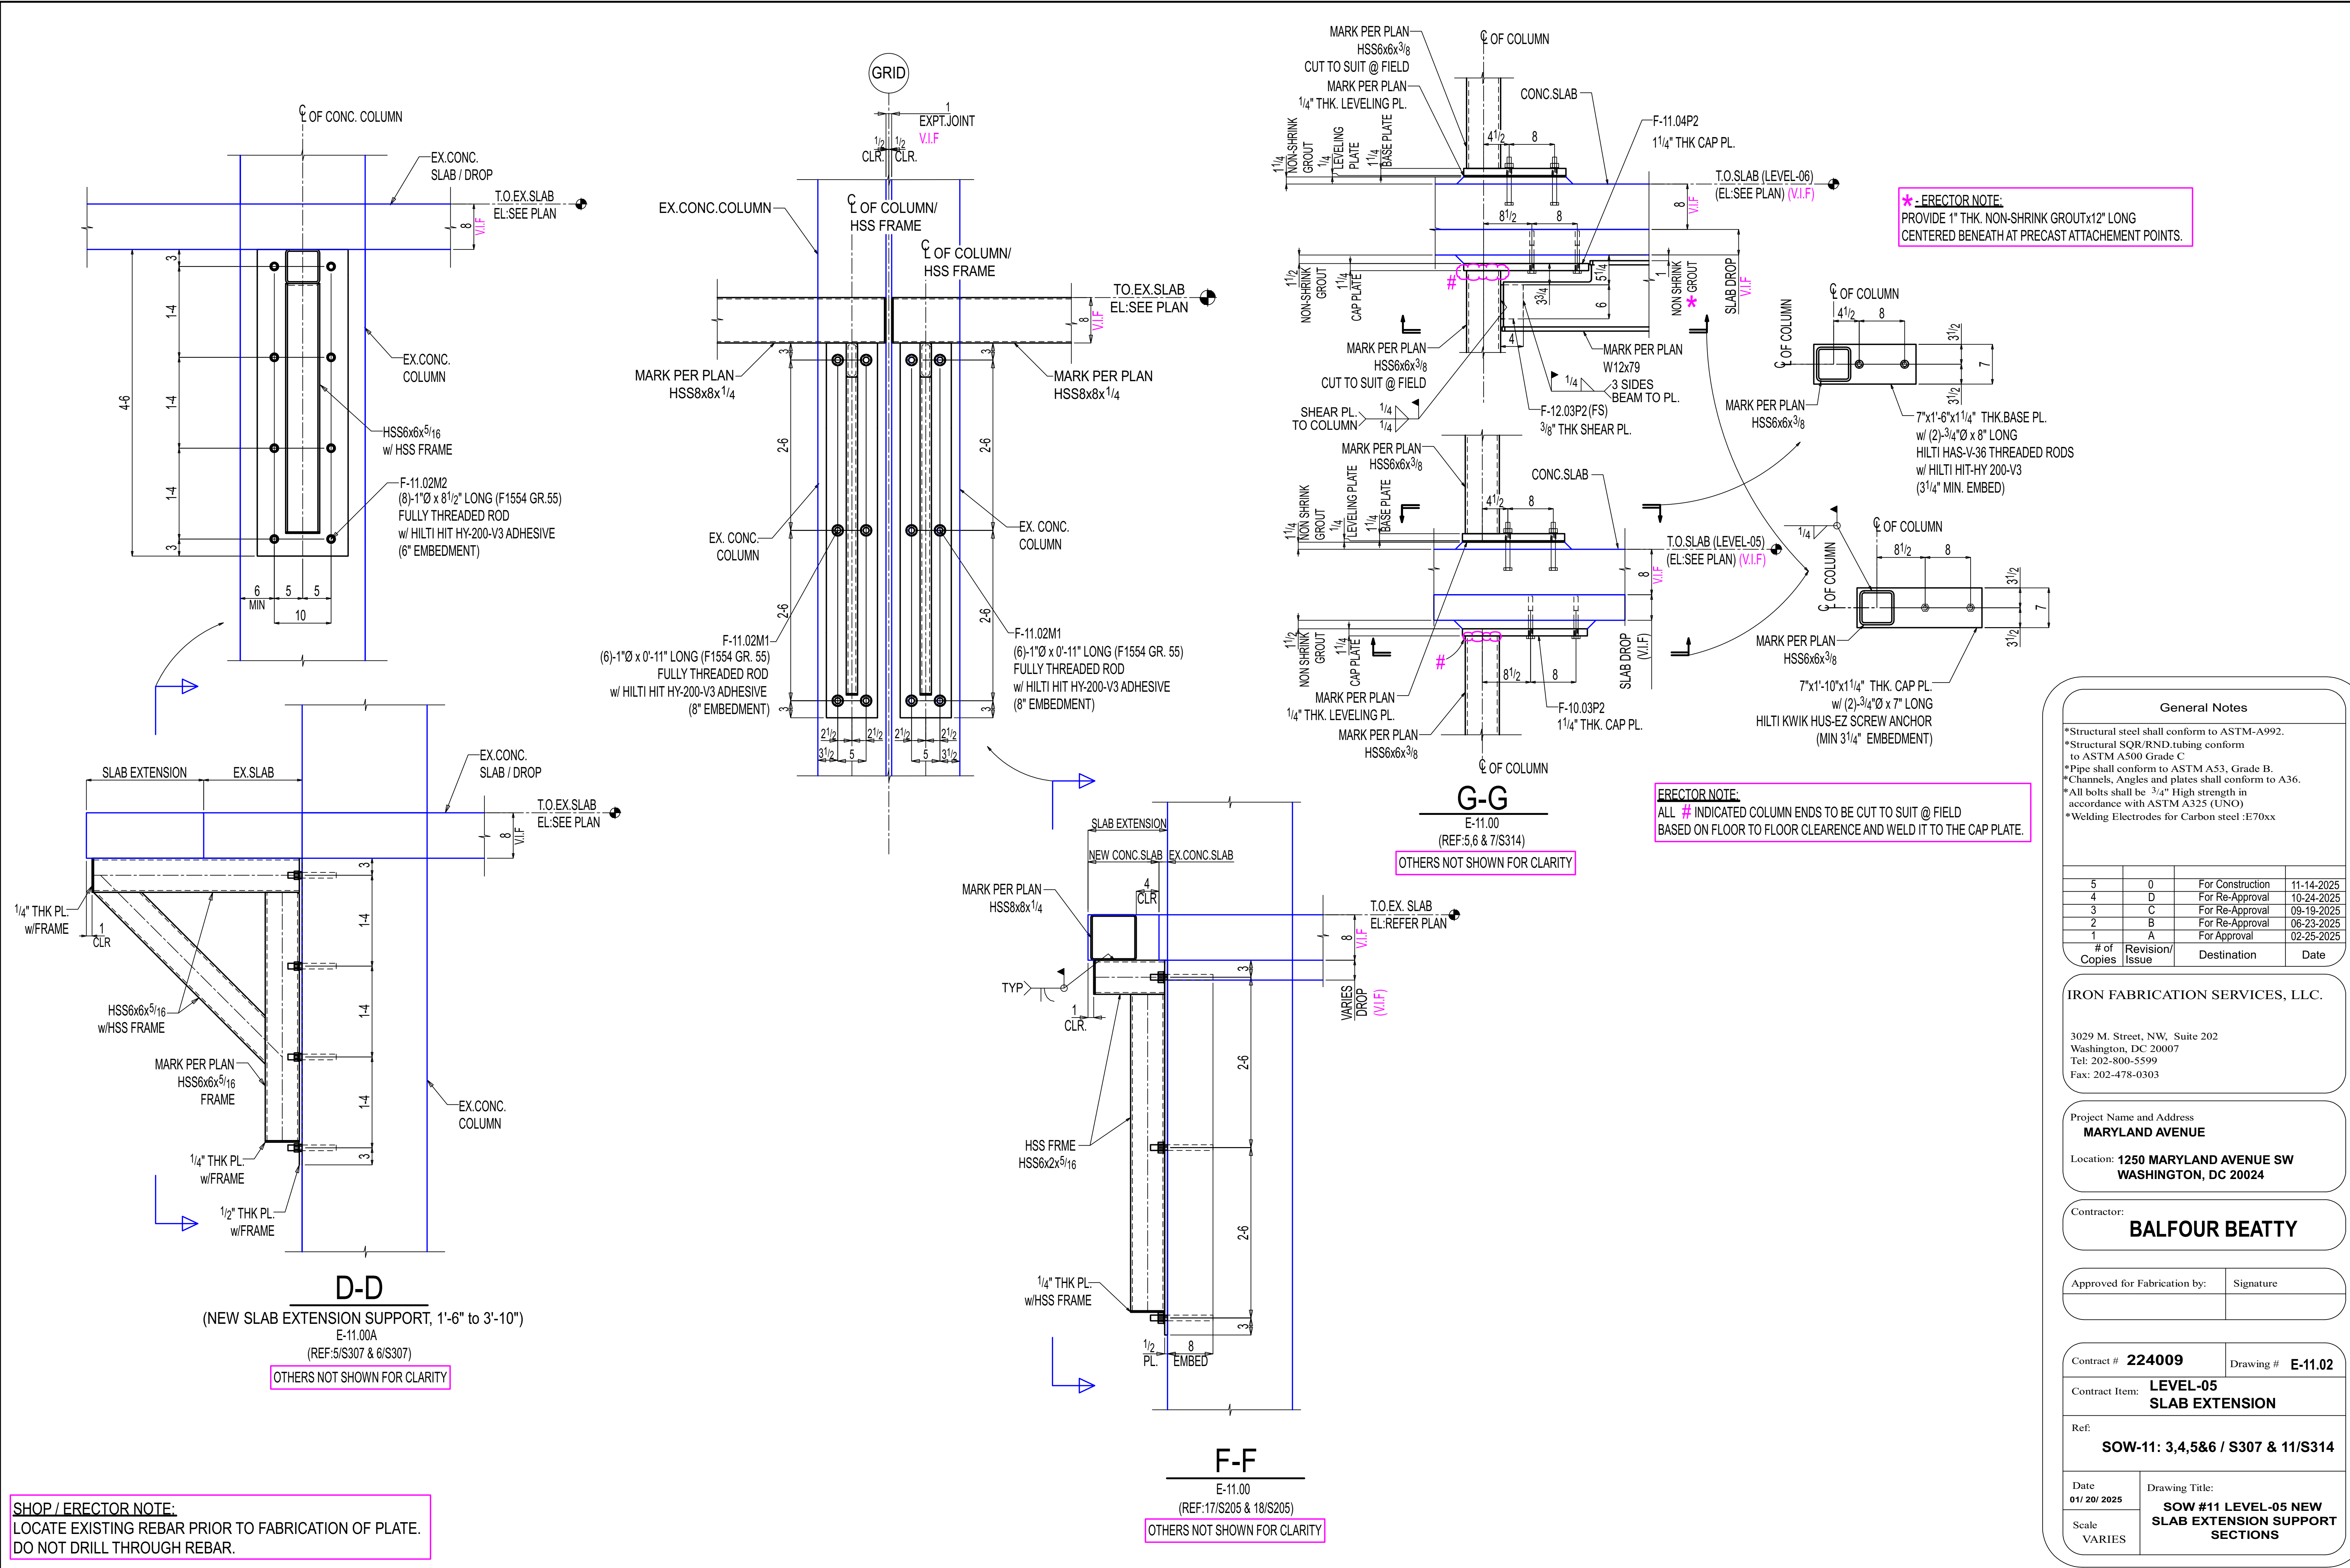

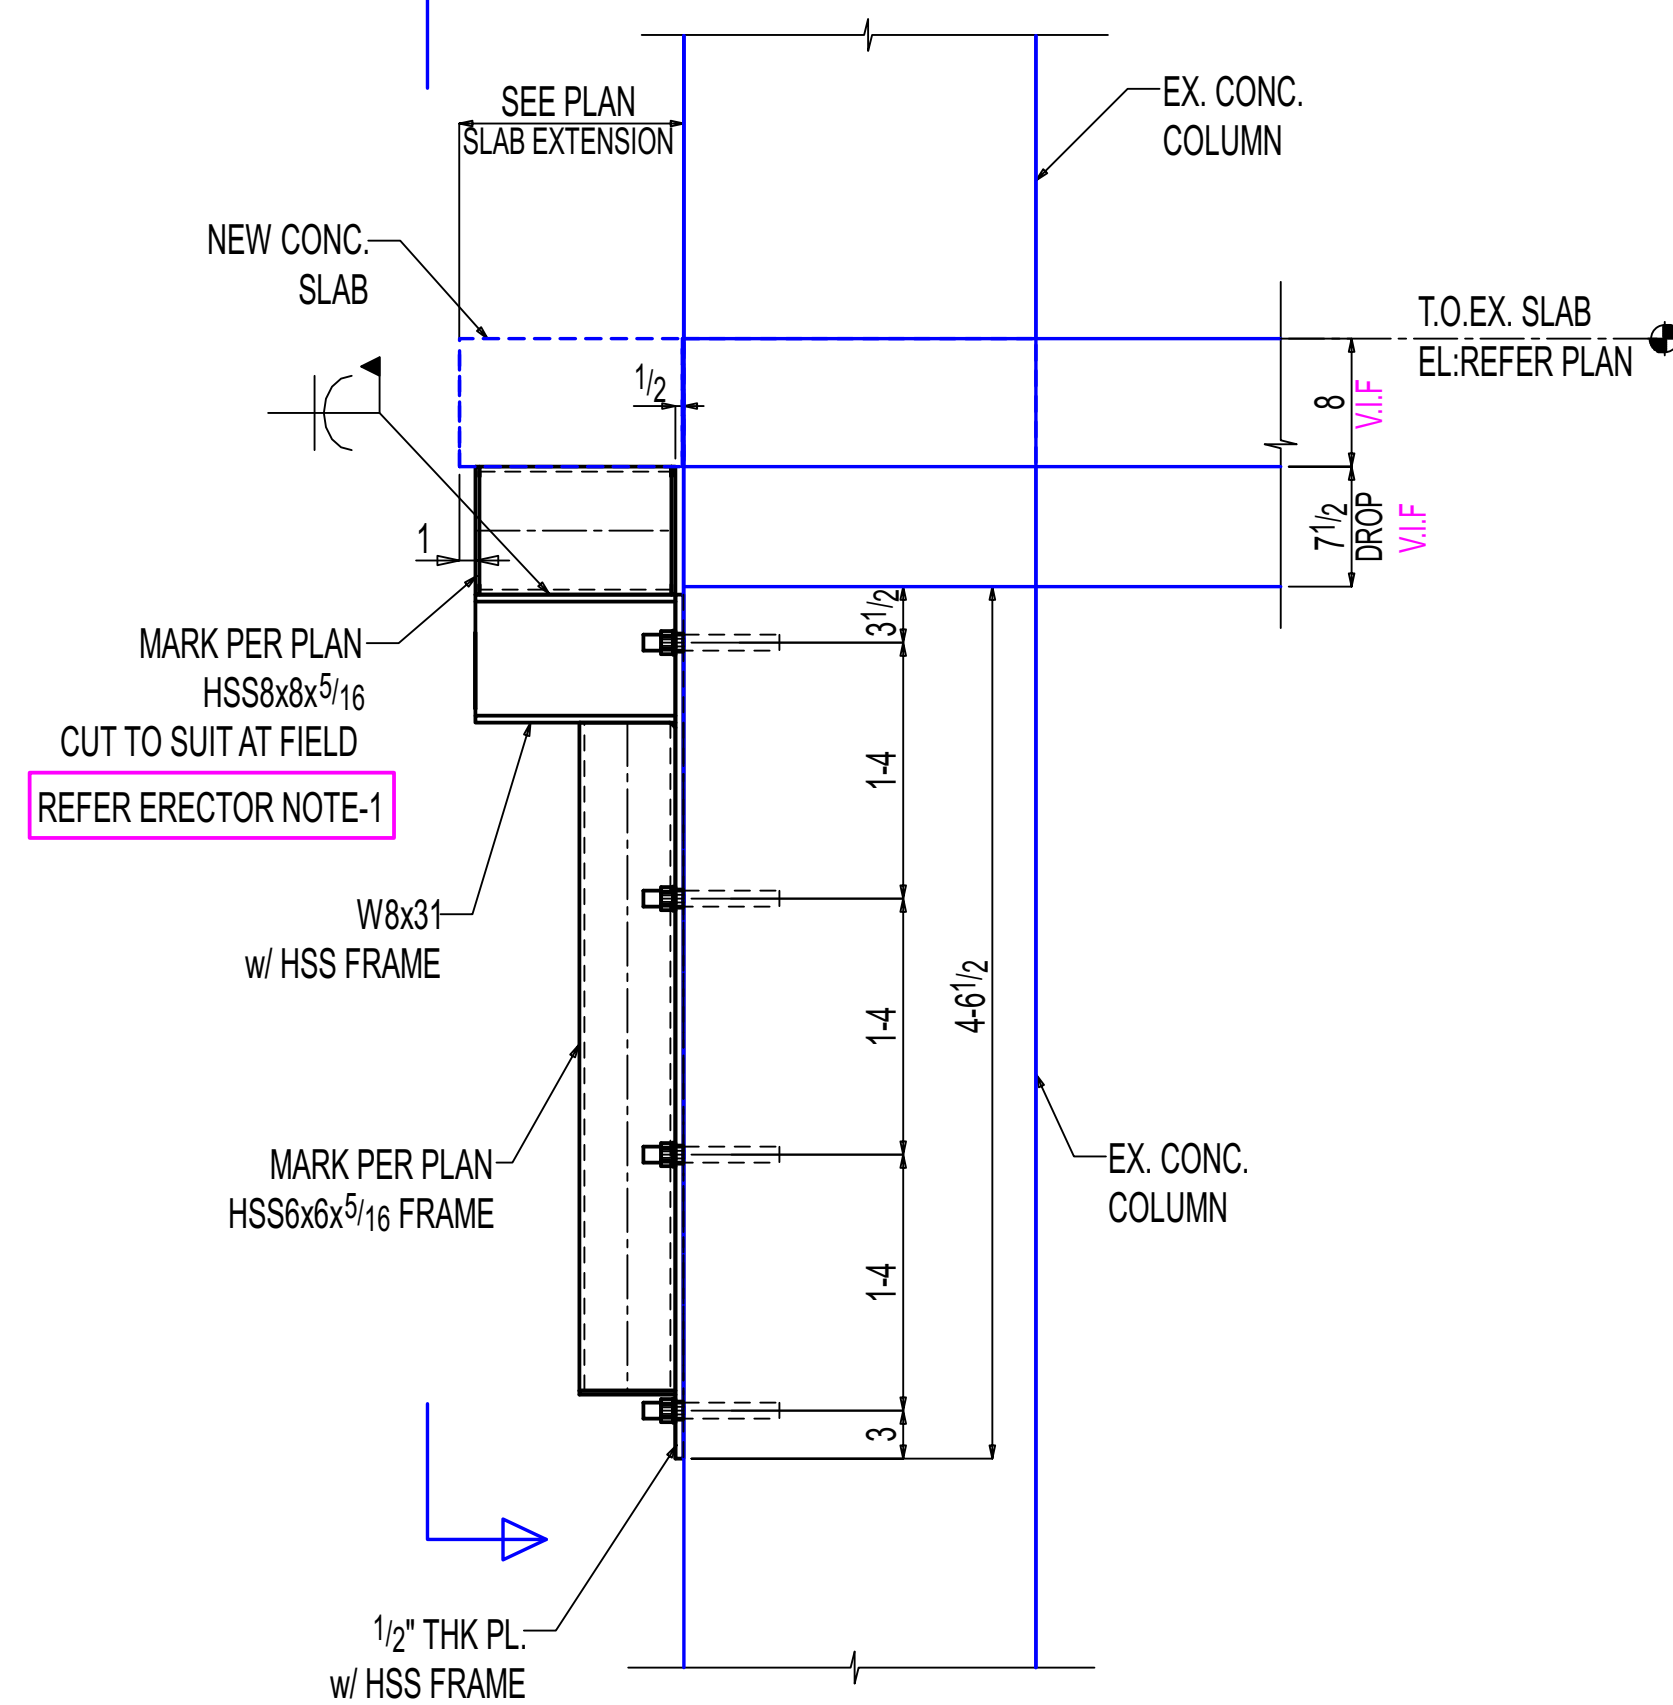
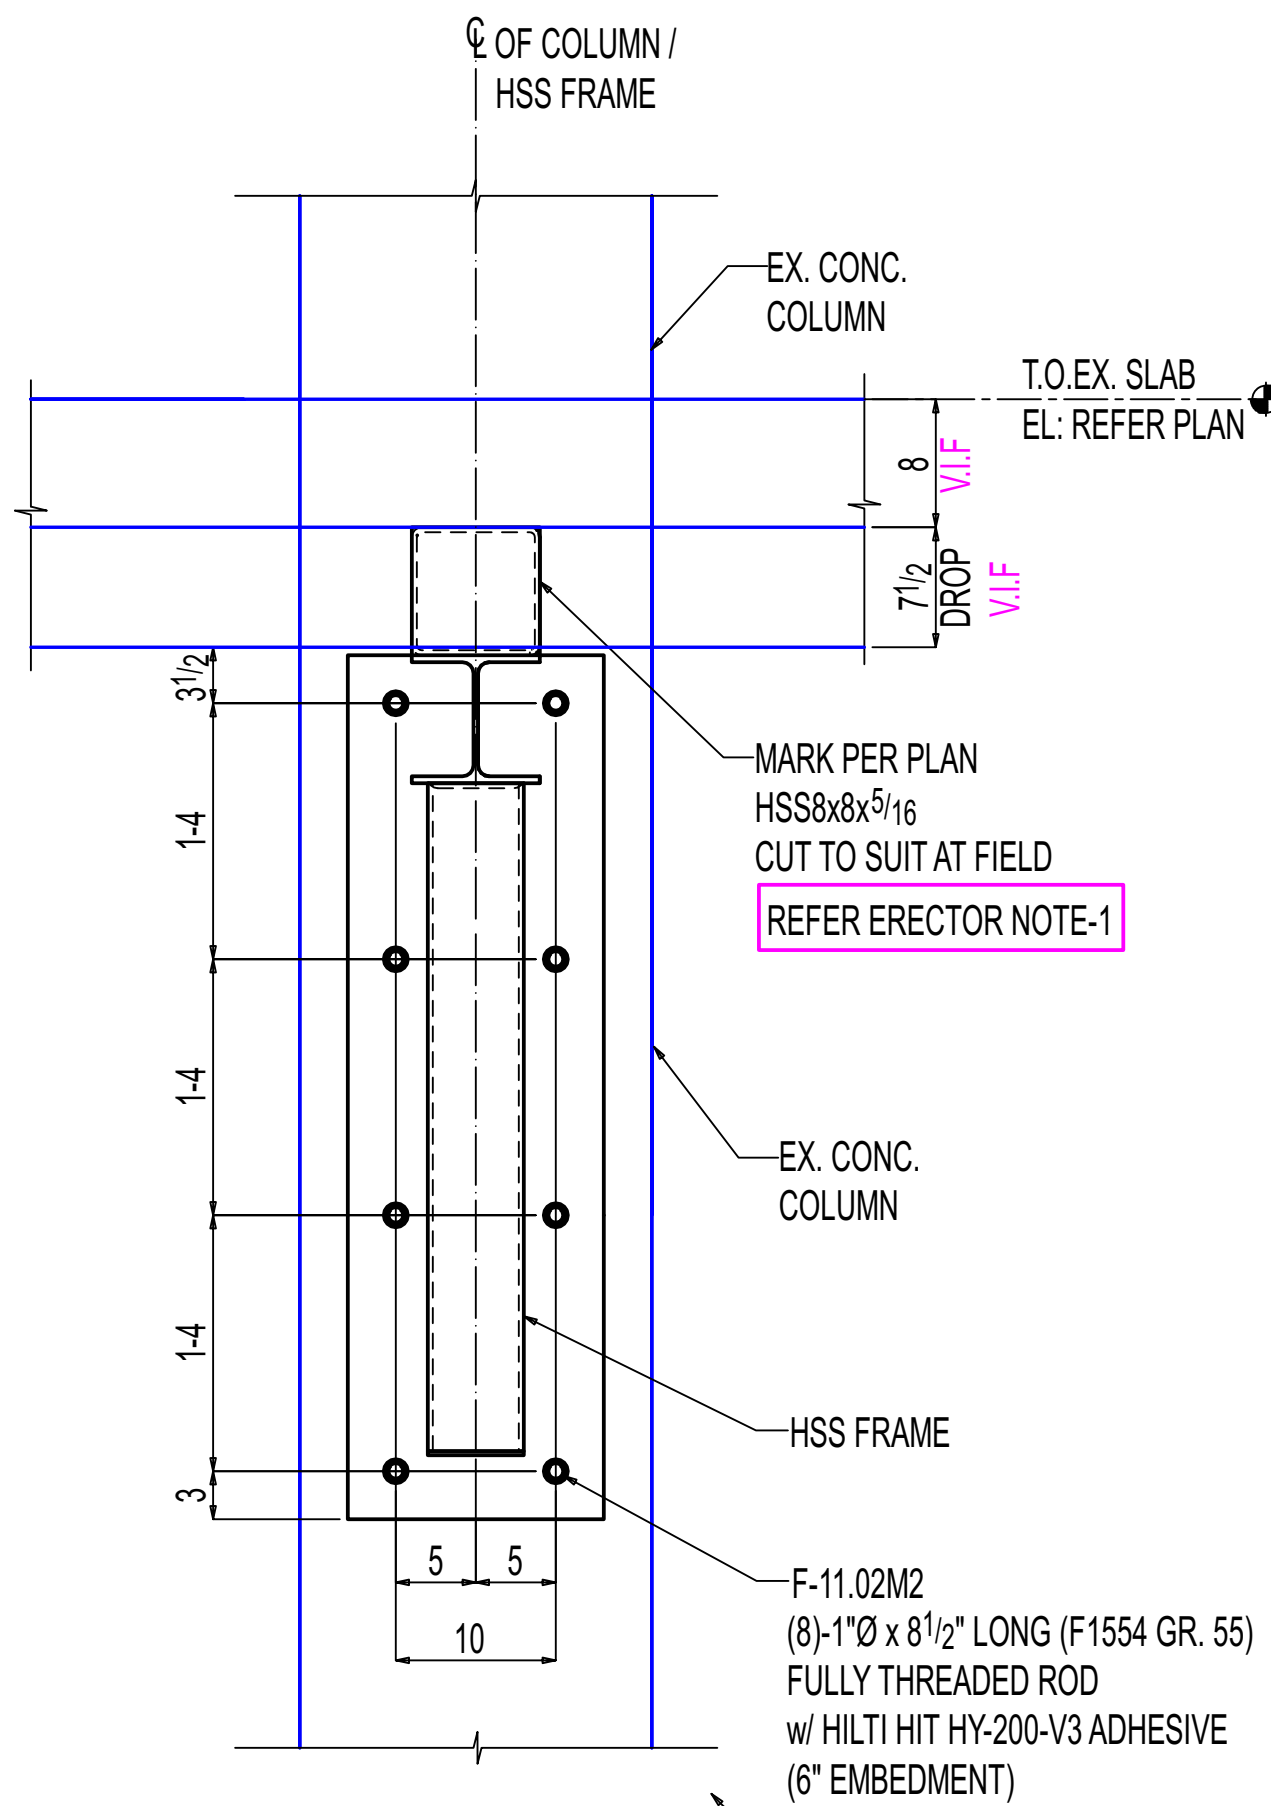


H-H

E-11.00A
(REF:10/S314)

OTHERS NOT SHOWN FOR CLARTY

*** ERECTOR NOTE:**
PROVIDE 1" NON-SHRINK GROUT x 12" LONG CENTERED BENEATH AT PRECAST ATTACHMENT POINTS.

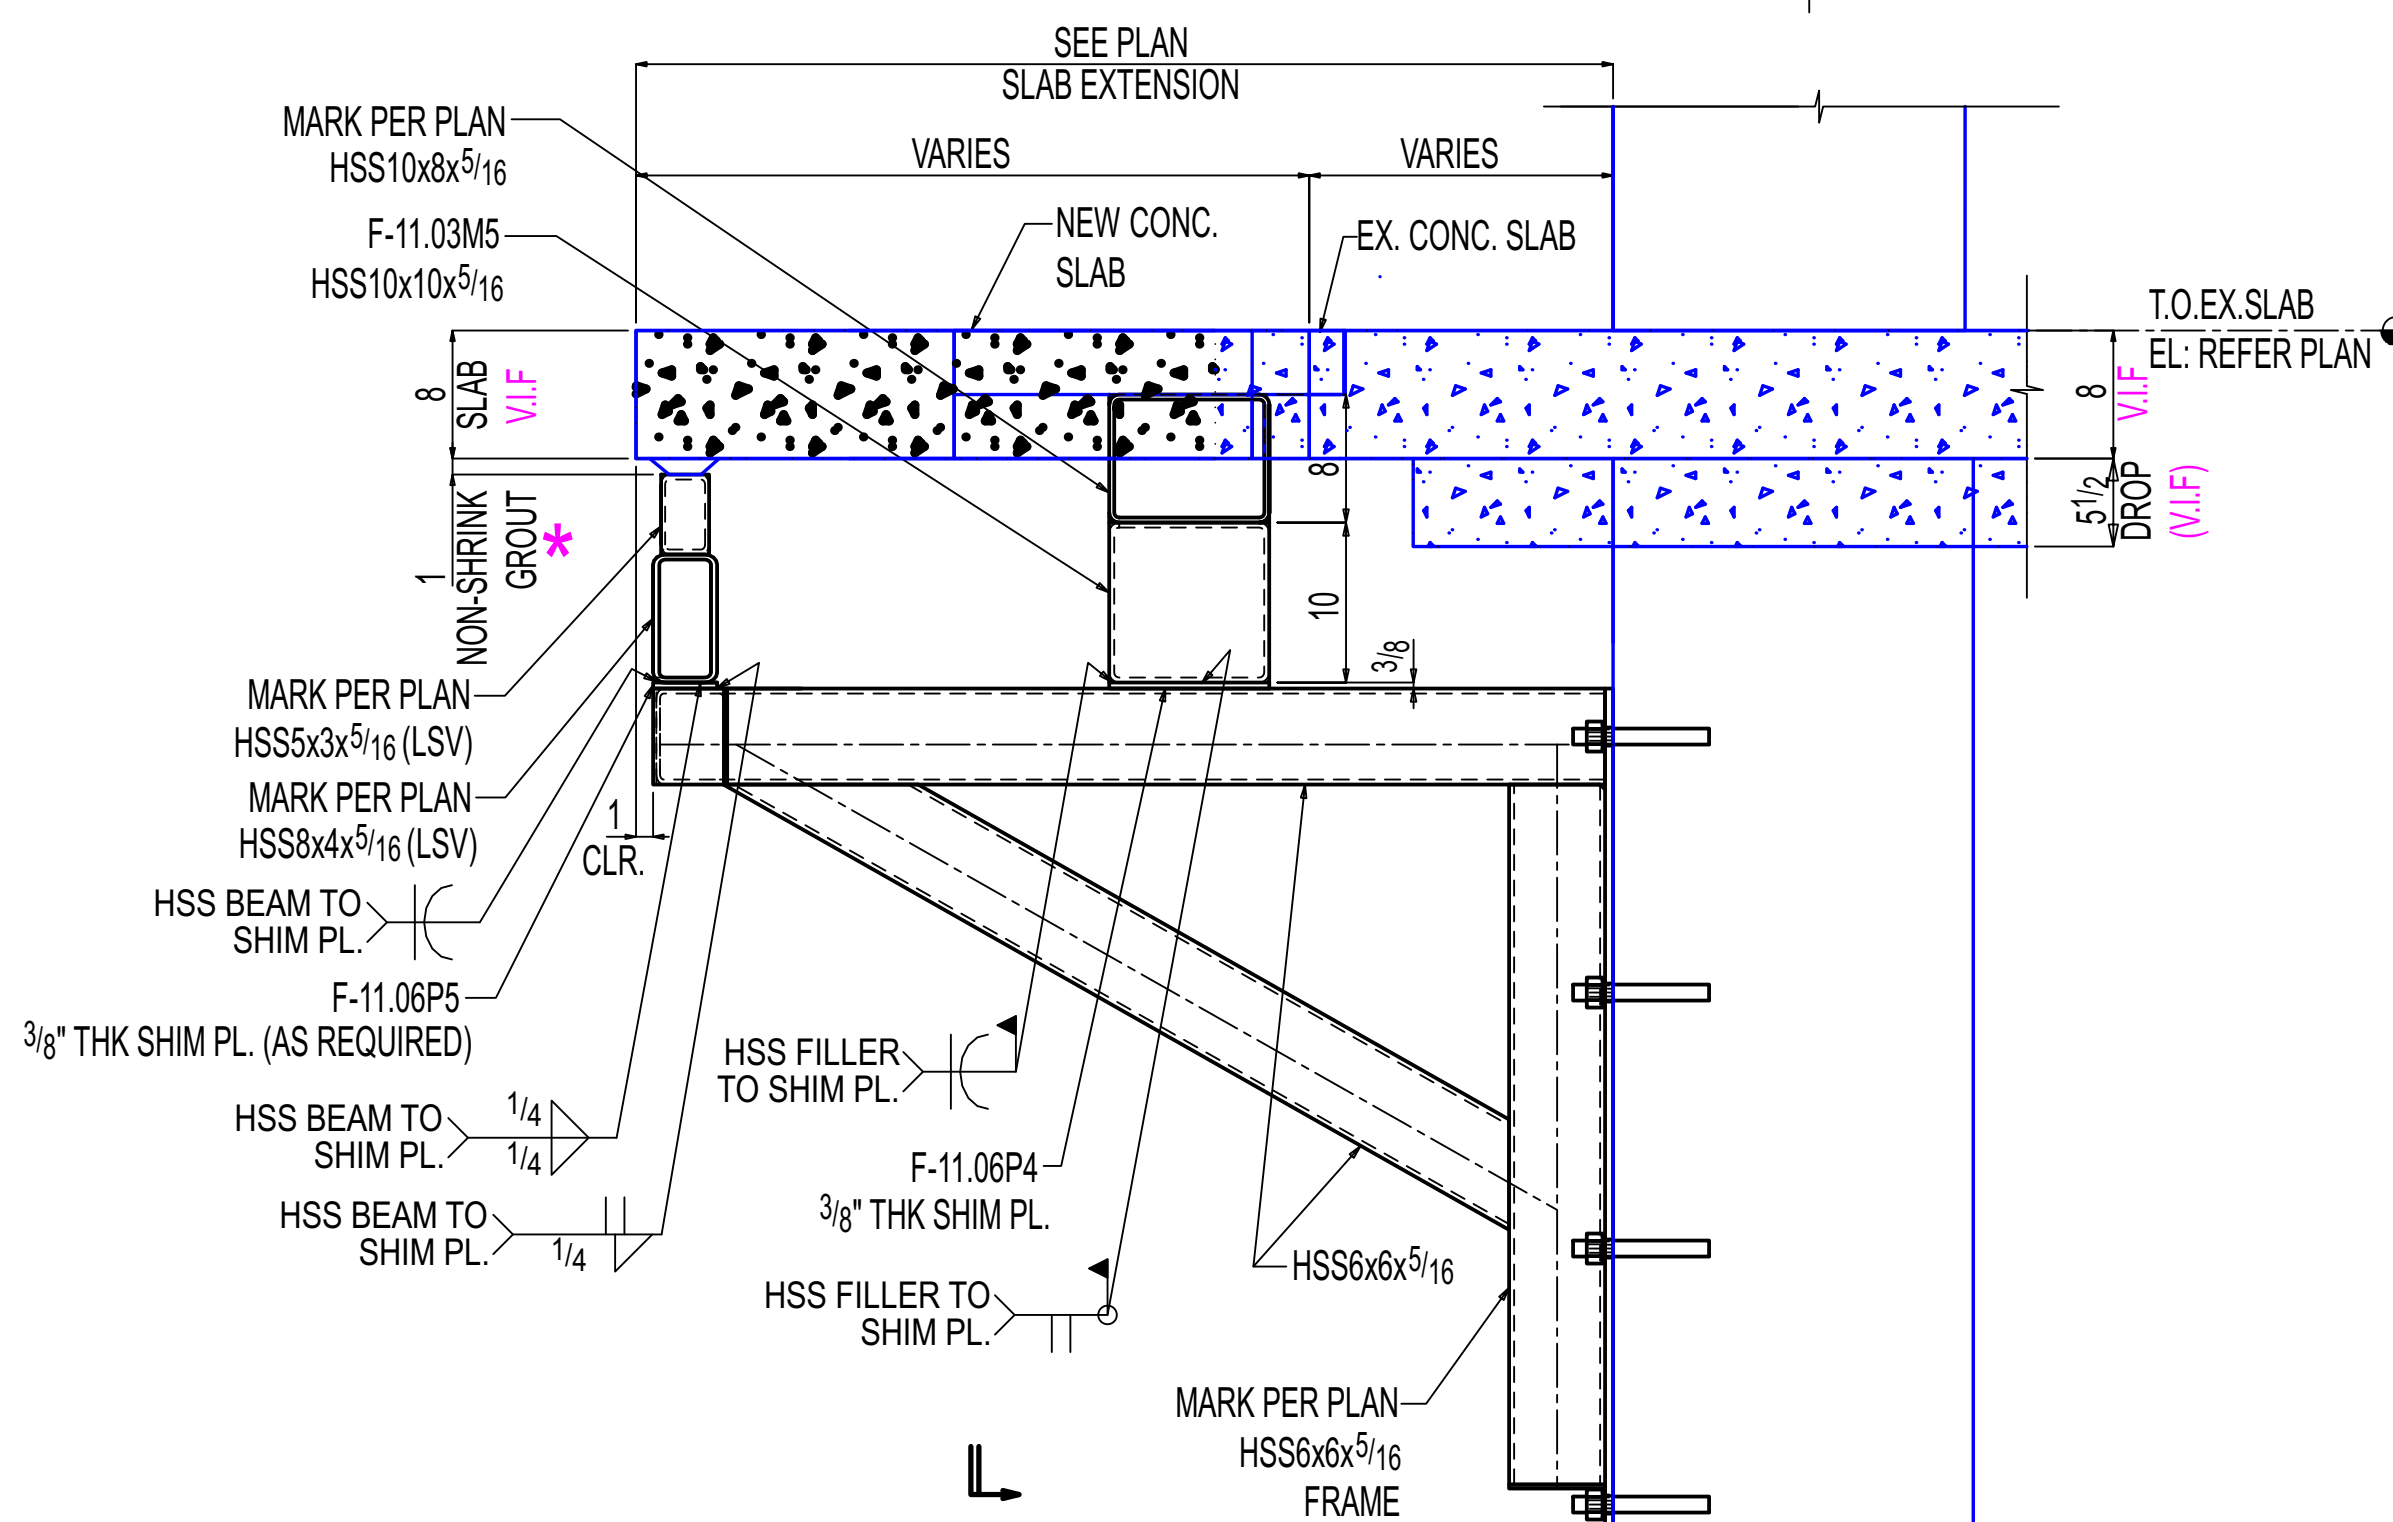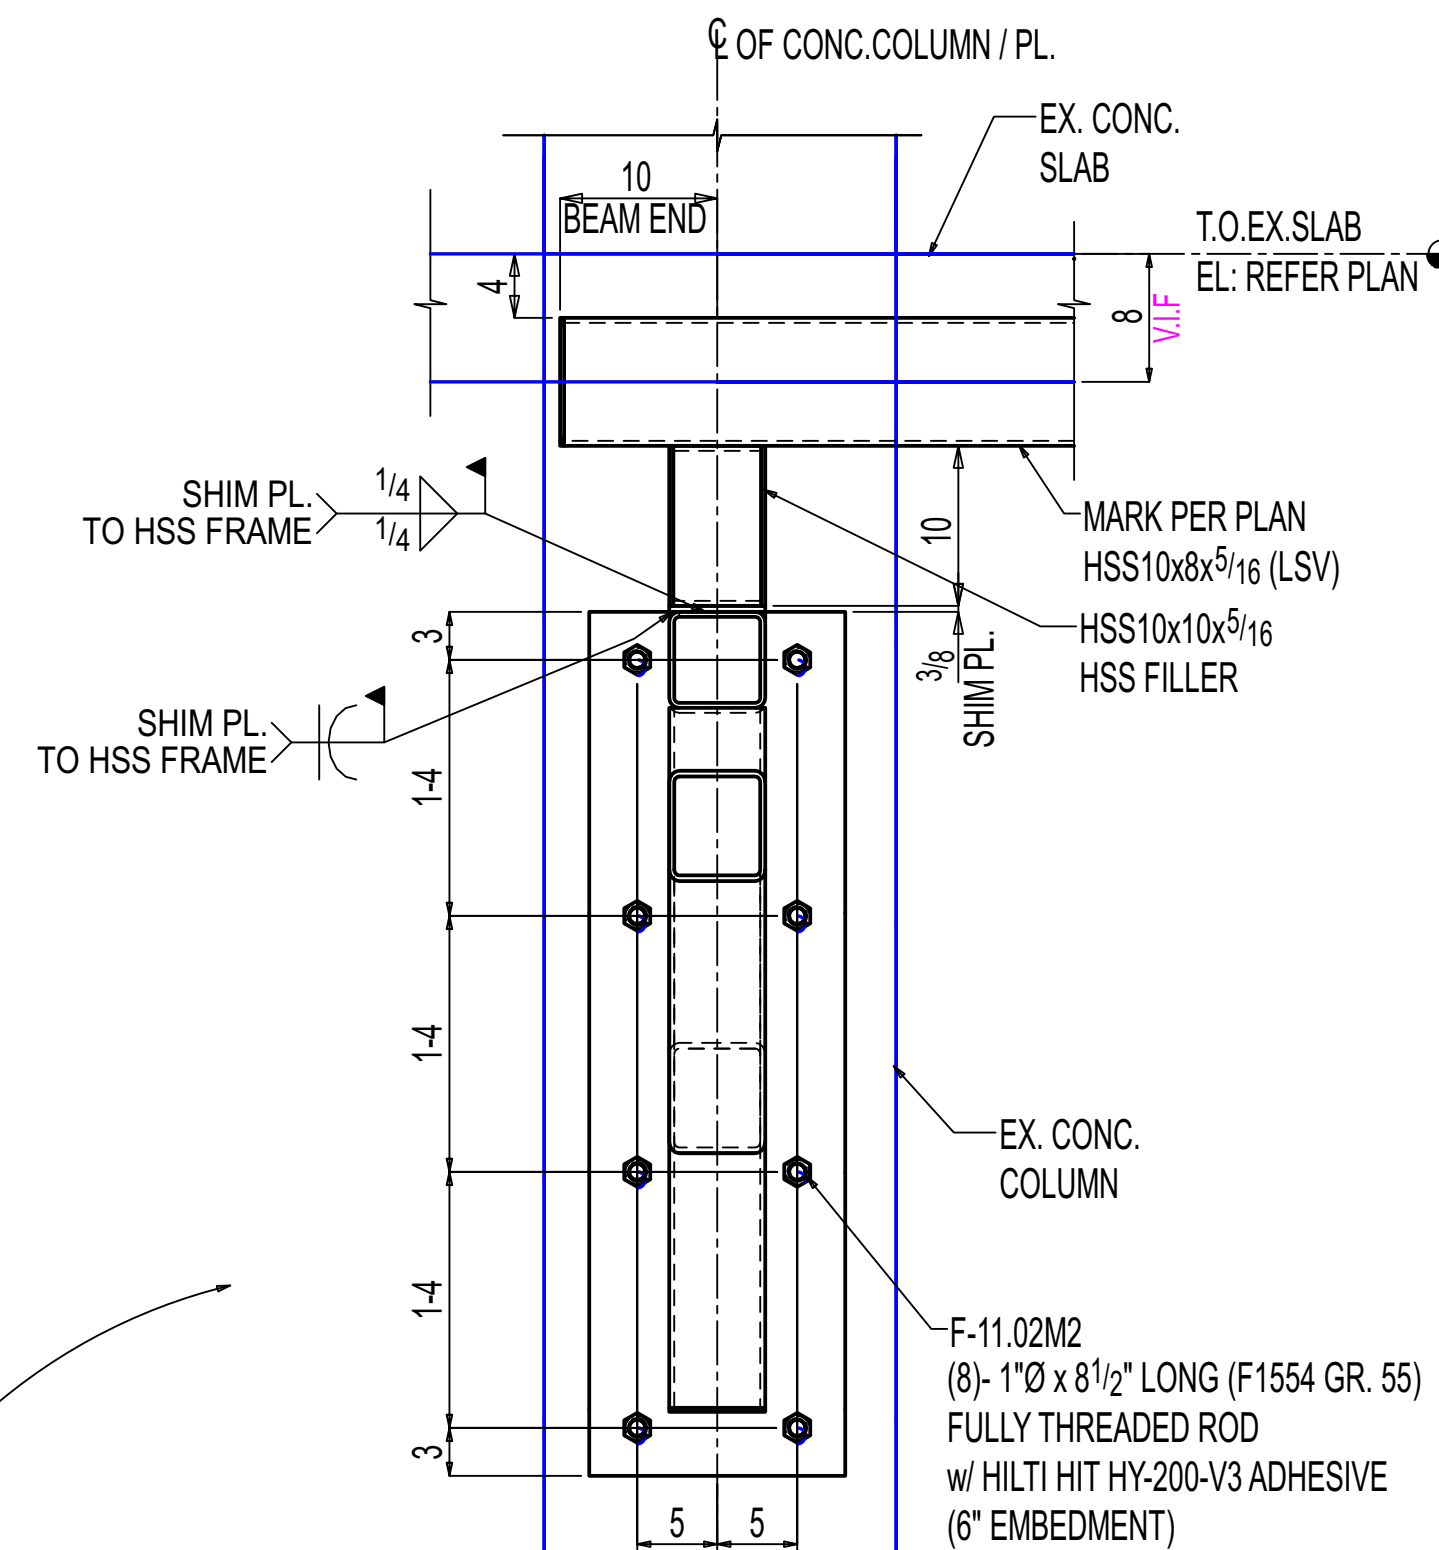

J-J

E-11.00B & E-11.05
(REF:6/S316)

OTHERS NOT SHOWN FOR CLARTY

SHOP / ERECTOR NOTE:
LOCATE EXISTING REBAR PRIOR TO FABRICATION OF PLATE. DO NOT DRILL THROUGH REBAR.

ERECTOR NOTE-1:
ADJUST HSS FILLER DEPTH IN FIELD BY CUT THE HSS FILLER TO MATCH EXISTING SLAB DROP THICKNESS, AND WELD TO THE TOP OF HSS FRAME AT SITE PRIOR TO ERECTING THE HSS FRAME.

General Notes

- *Structural steel shall conform to ASTM-A992.
- *Structural SQR/RND tubing conform to ASTM A500 Grade C
- *Pipe shall conform to ASTM A53, Grade B.
- *Channels, Angles and plates shall conform to A36.
- *All bolts shall be 3/4" High strength in accordance with ASTM A325 (UNO)
- *Welding Electrodes for Carbon steel :E70xx

# of Copies	Revision/ Issue	Destination	Date
4	0	For Construction	11-14-2025
3	C	For Re-Approval	10-24-2025
2	B	For Re-Approval	09-19-2025
1	A	For Approval	06-23-2025

IRON FABRICATION SERVICES, LLC.

3029 M. Street, NW, Suite 202
Washington, DC 20007
Tel: 202-800-5599
Fax: 202-478-0303

Project Name and Address

MARYLAND AVENUE
Location: **1250 MARYLAND AVENUE SW WASHINGTON, DC 20024**

Contractor:

BALFOUR BEATTY


Approved for Fabrication by:	Signature
------------------------------	-----------

Contract # **224009** Drawing # **E-11.03**

Contract Item: **LEVEL-05 SLAB EXTENSION**


Ref: **SOW-11: 3,4,5&6 / S307**

Date 01/20/2025	Drawing Title: SOW #11 LEVEL-05 NEW SLAB EXTENSION SUPPORT SECTIONS
Scale VARIES	

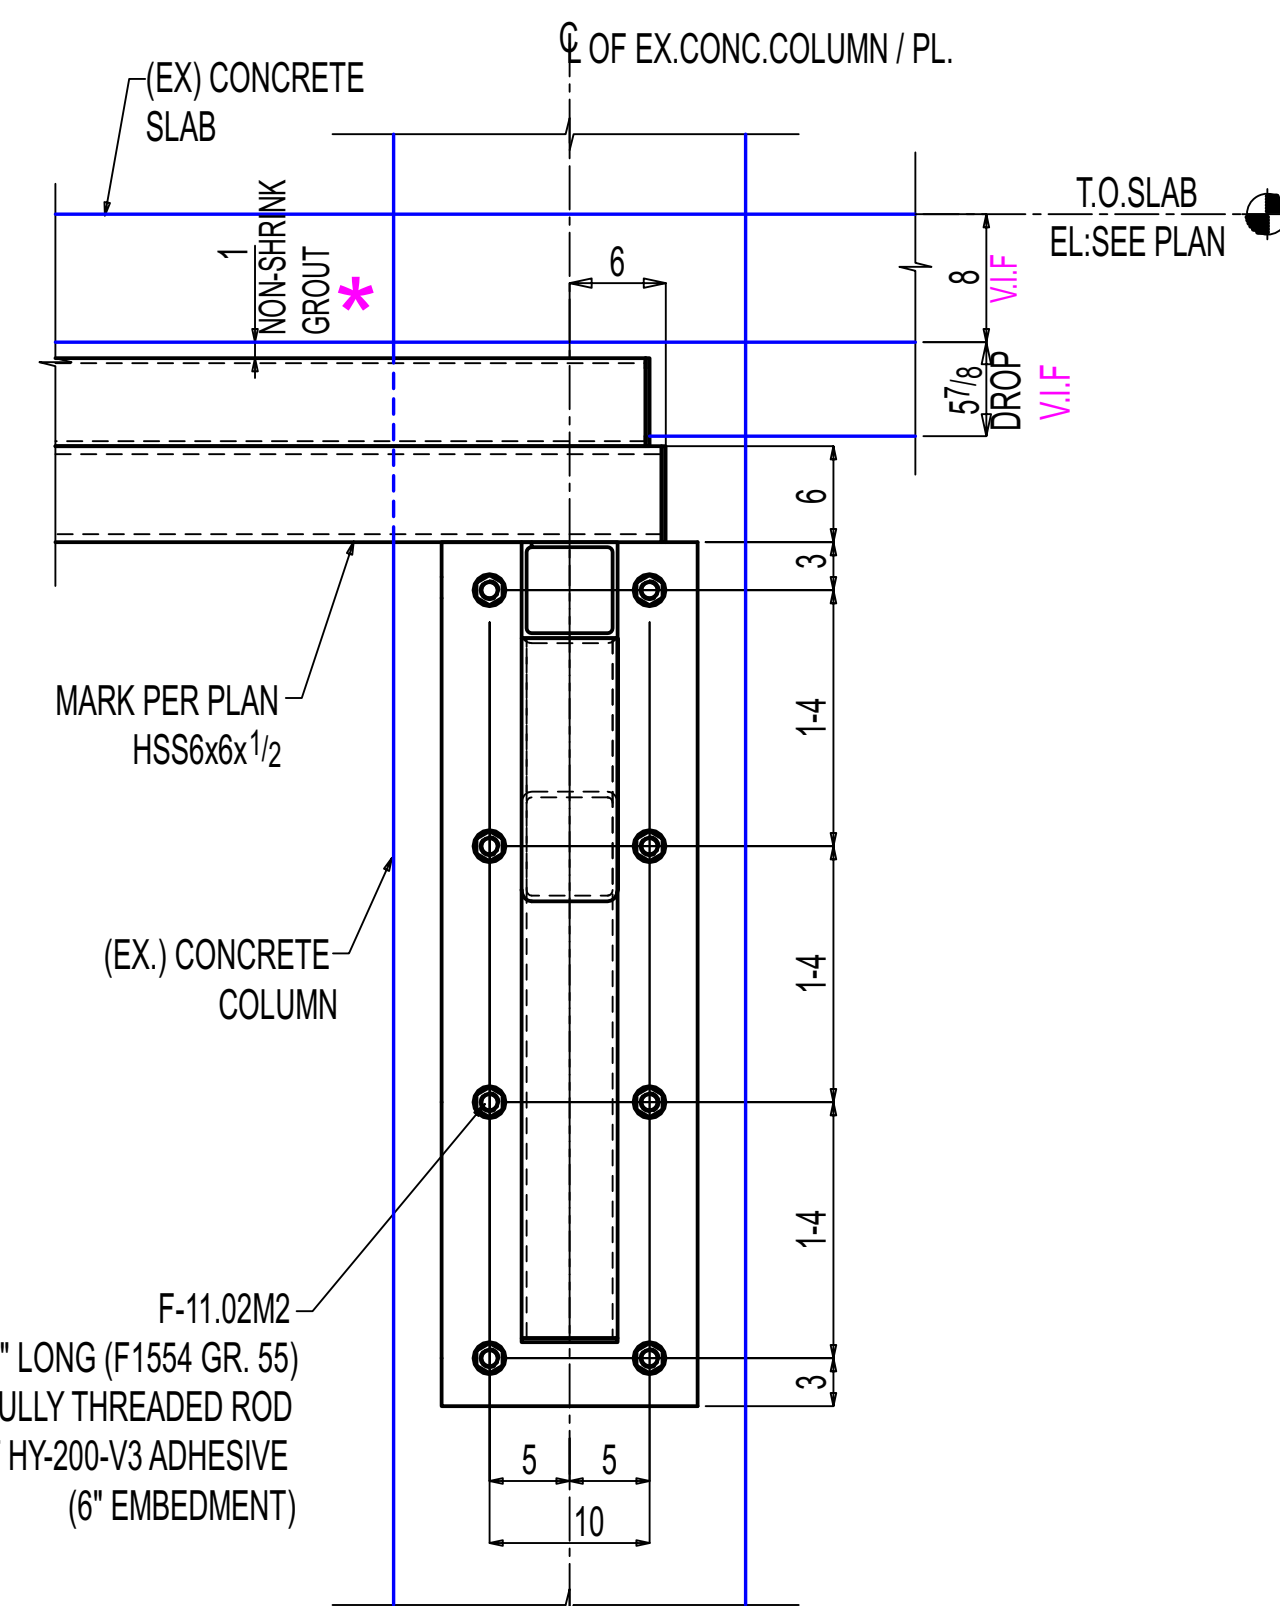

OTHERS NOT SHOWN FOR CLARITY

OTHERS NOT SHOWN FOR CLARITY

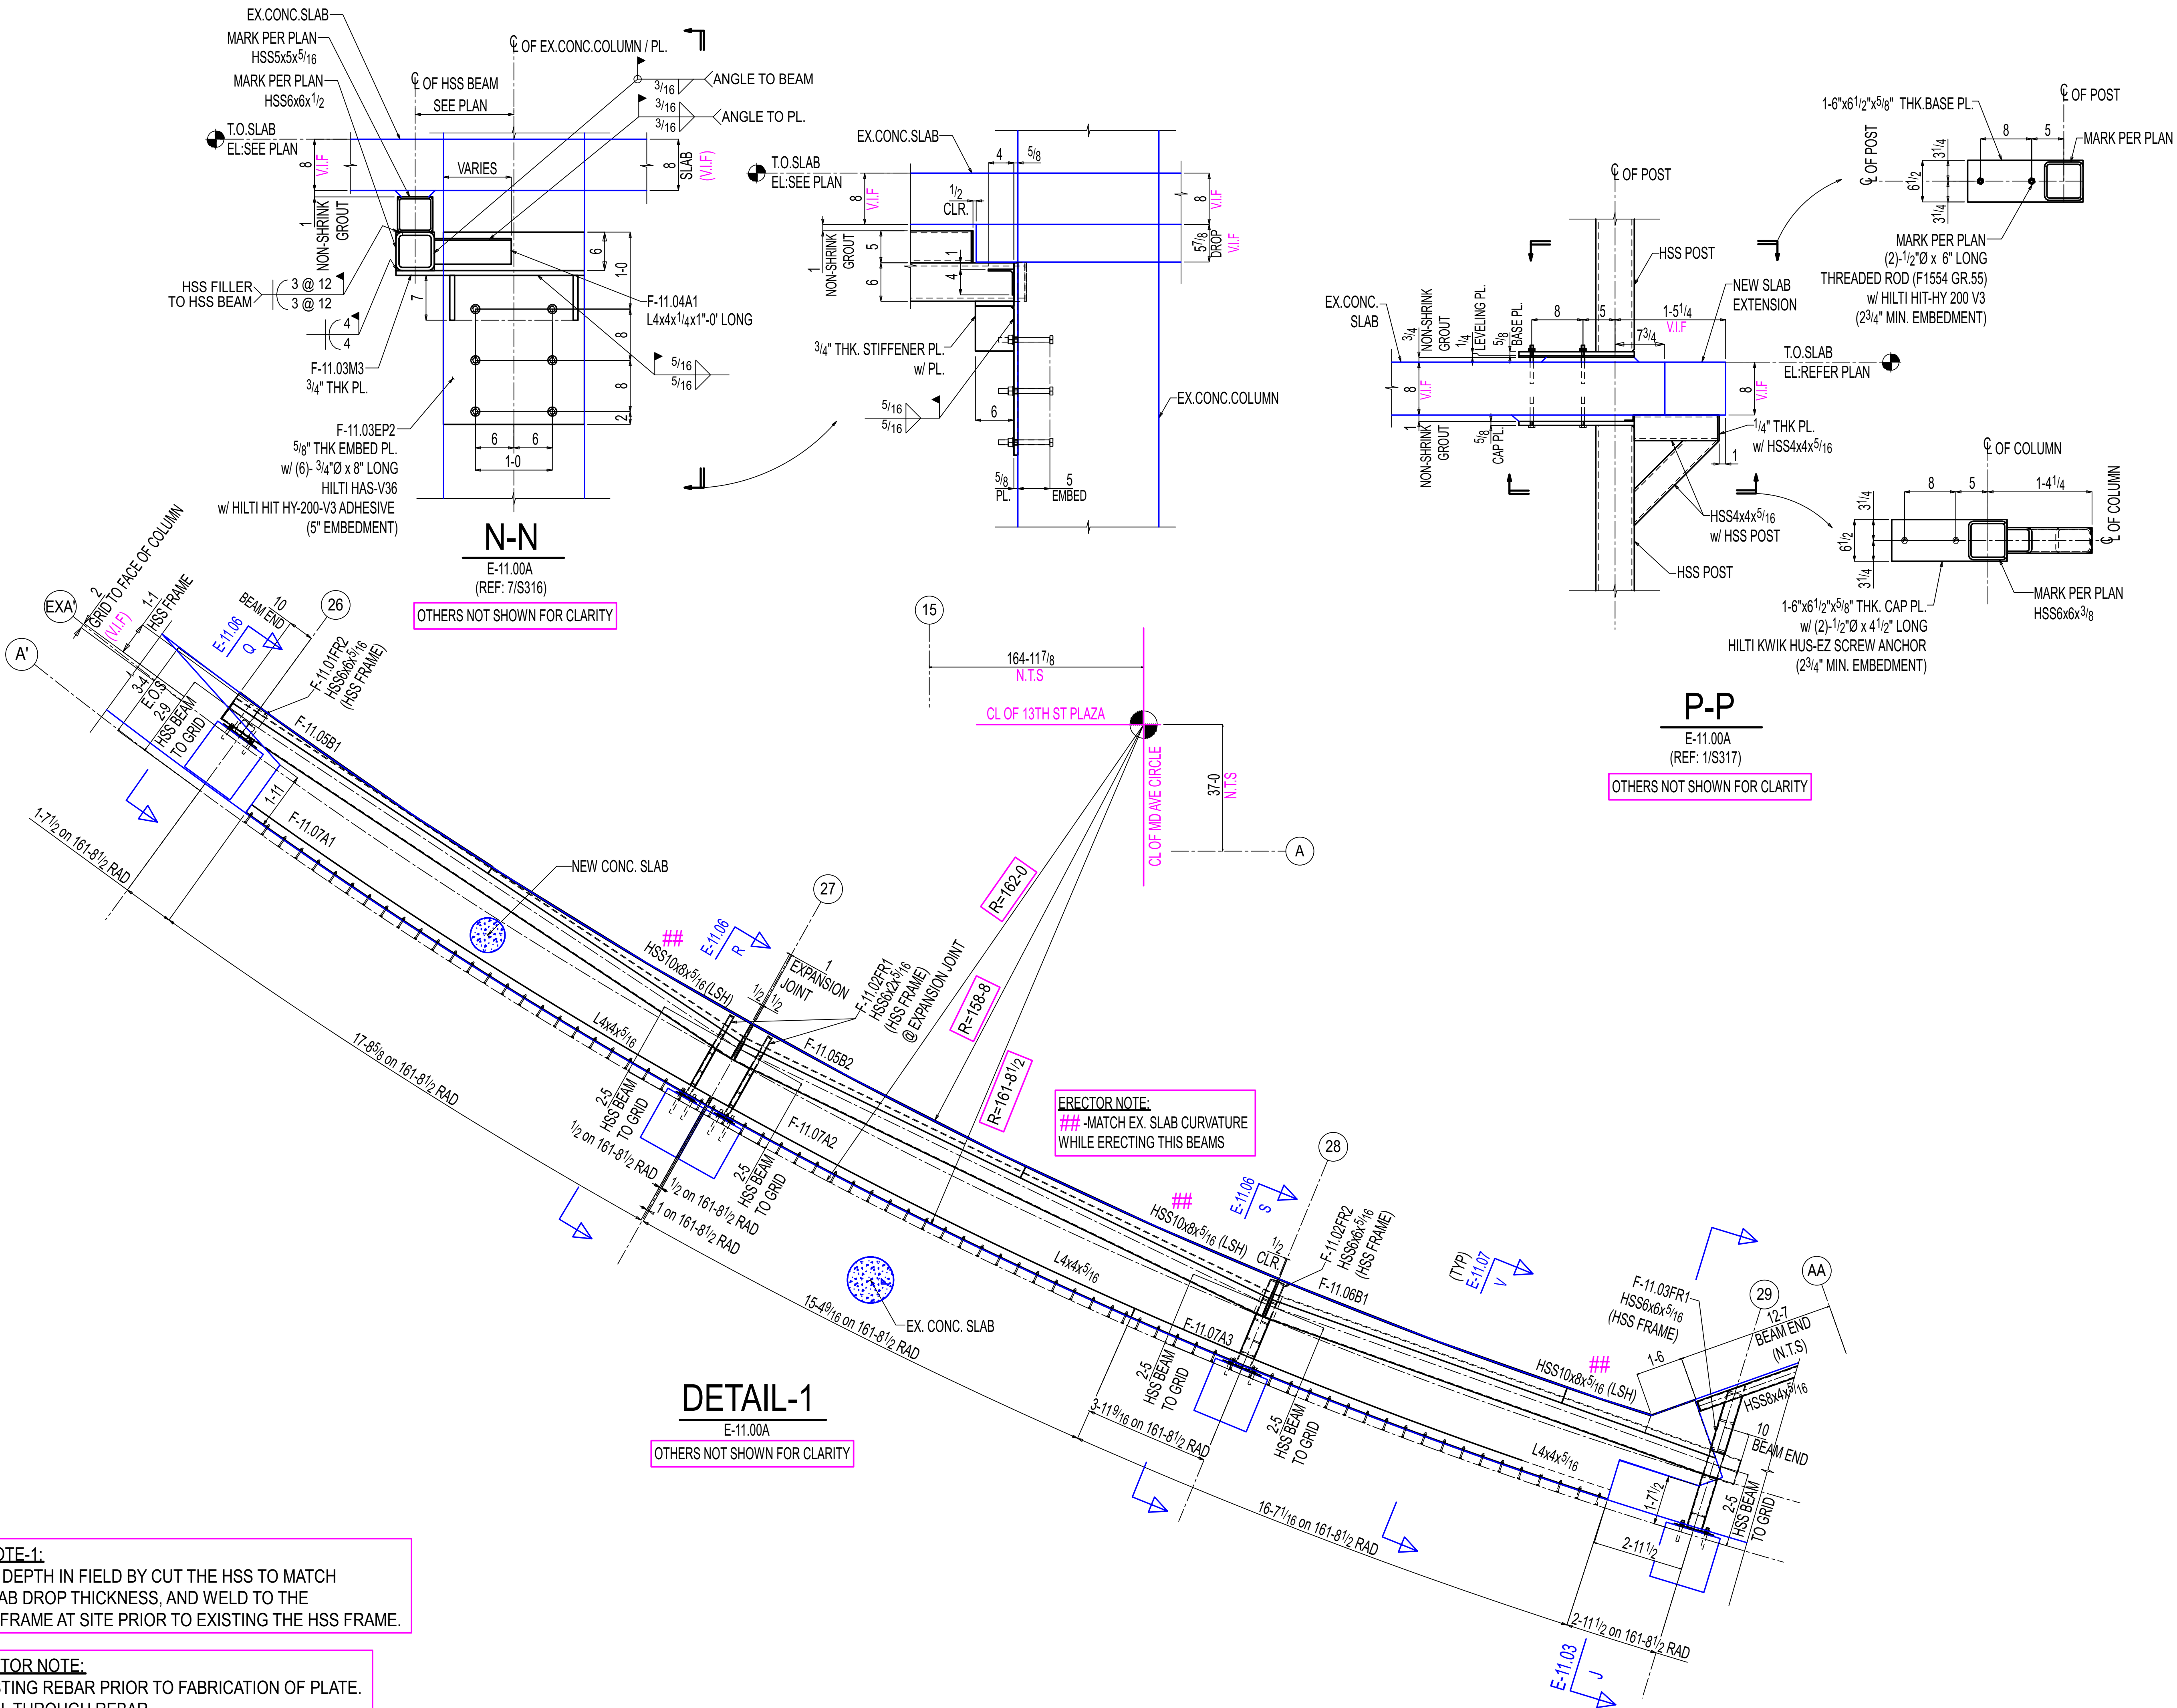

General Notes			
*Structural steel shall conform to ASTM-A992.			
*Structural SQR/RND.tubing conform to ASTM A500 Grade C			
*Pipe shall conform to ASTM A53, Grade B.			
*Channels, Angles and plates shall conform to A36.			
*All bolts shall be 3/4" High strength in accordance with ASTM A325 (UNO)			
*Welding Electrodes for Carbon steel :E70xx			
3	0	For Construction	11-14-2025
2	B	For Re-Approval	10-24-2025
1	A	For Approval	09-19-2025
# of Copies	Revision/ Issue	Destination	Date

IRON FABRICATION SERVICES, LLC.

3029 M. Street, NW, Suite 202
Washington, DC 20007
Tel: 202-800-5599
Fax: 202-478-0303

Project Name and Address
MARYLAND AVENUE
Location: **1250 MARYLAND AVENUE SW
WASHINGTON, DC 20024**

Contractor:
BALFOUR BEATTY


Approved for Fabrication by: Signature

Contract # **224009** Drawing # **E-11.05**

Contract Item: **LEVEL-05
SLAB EXTENSION**

Ref: **SOW-11: 3,4,5&6 / S307**

Date
01/20/2025
Drawing Title:
**SOW #11 LEVEL-05 NEW
SLAB EXTENSION SUPPORT
SECTIONS**
Scale
VARIES

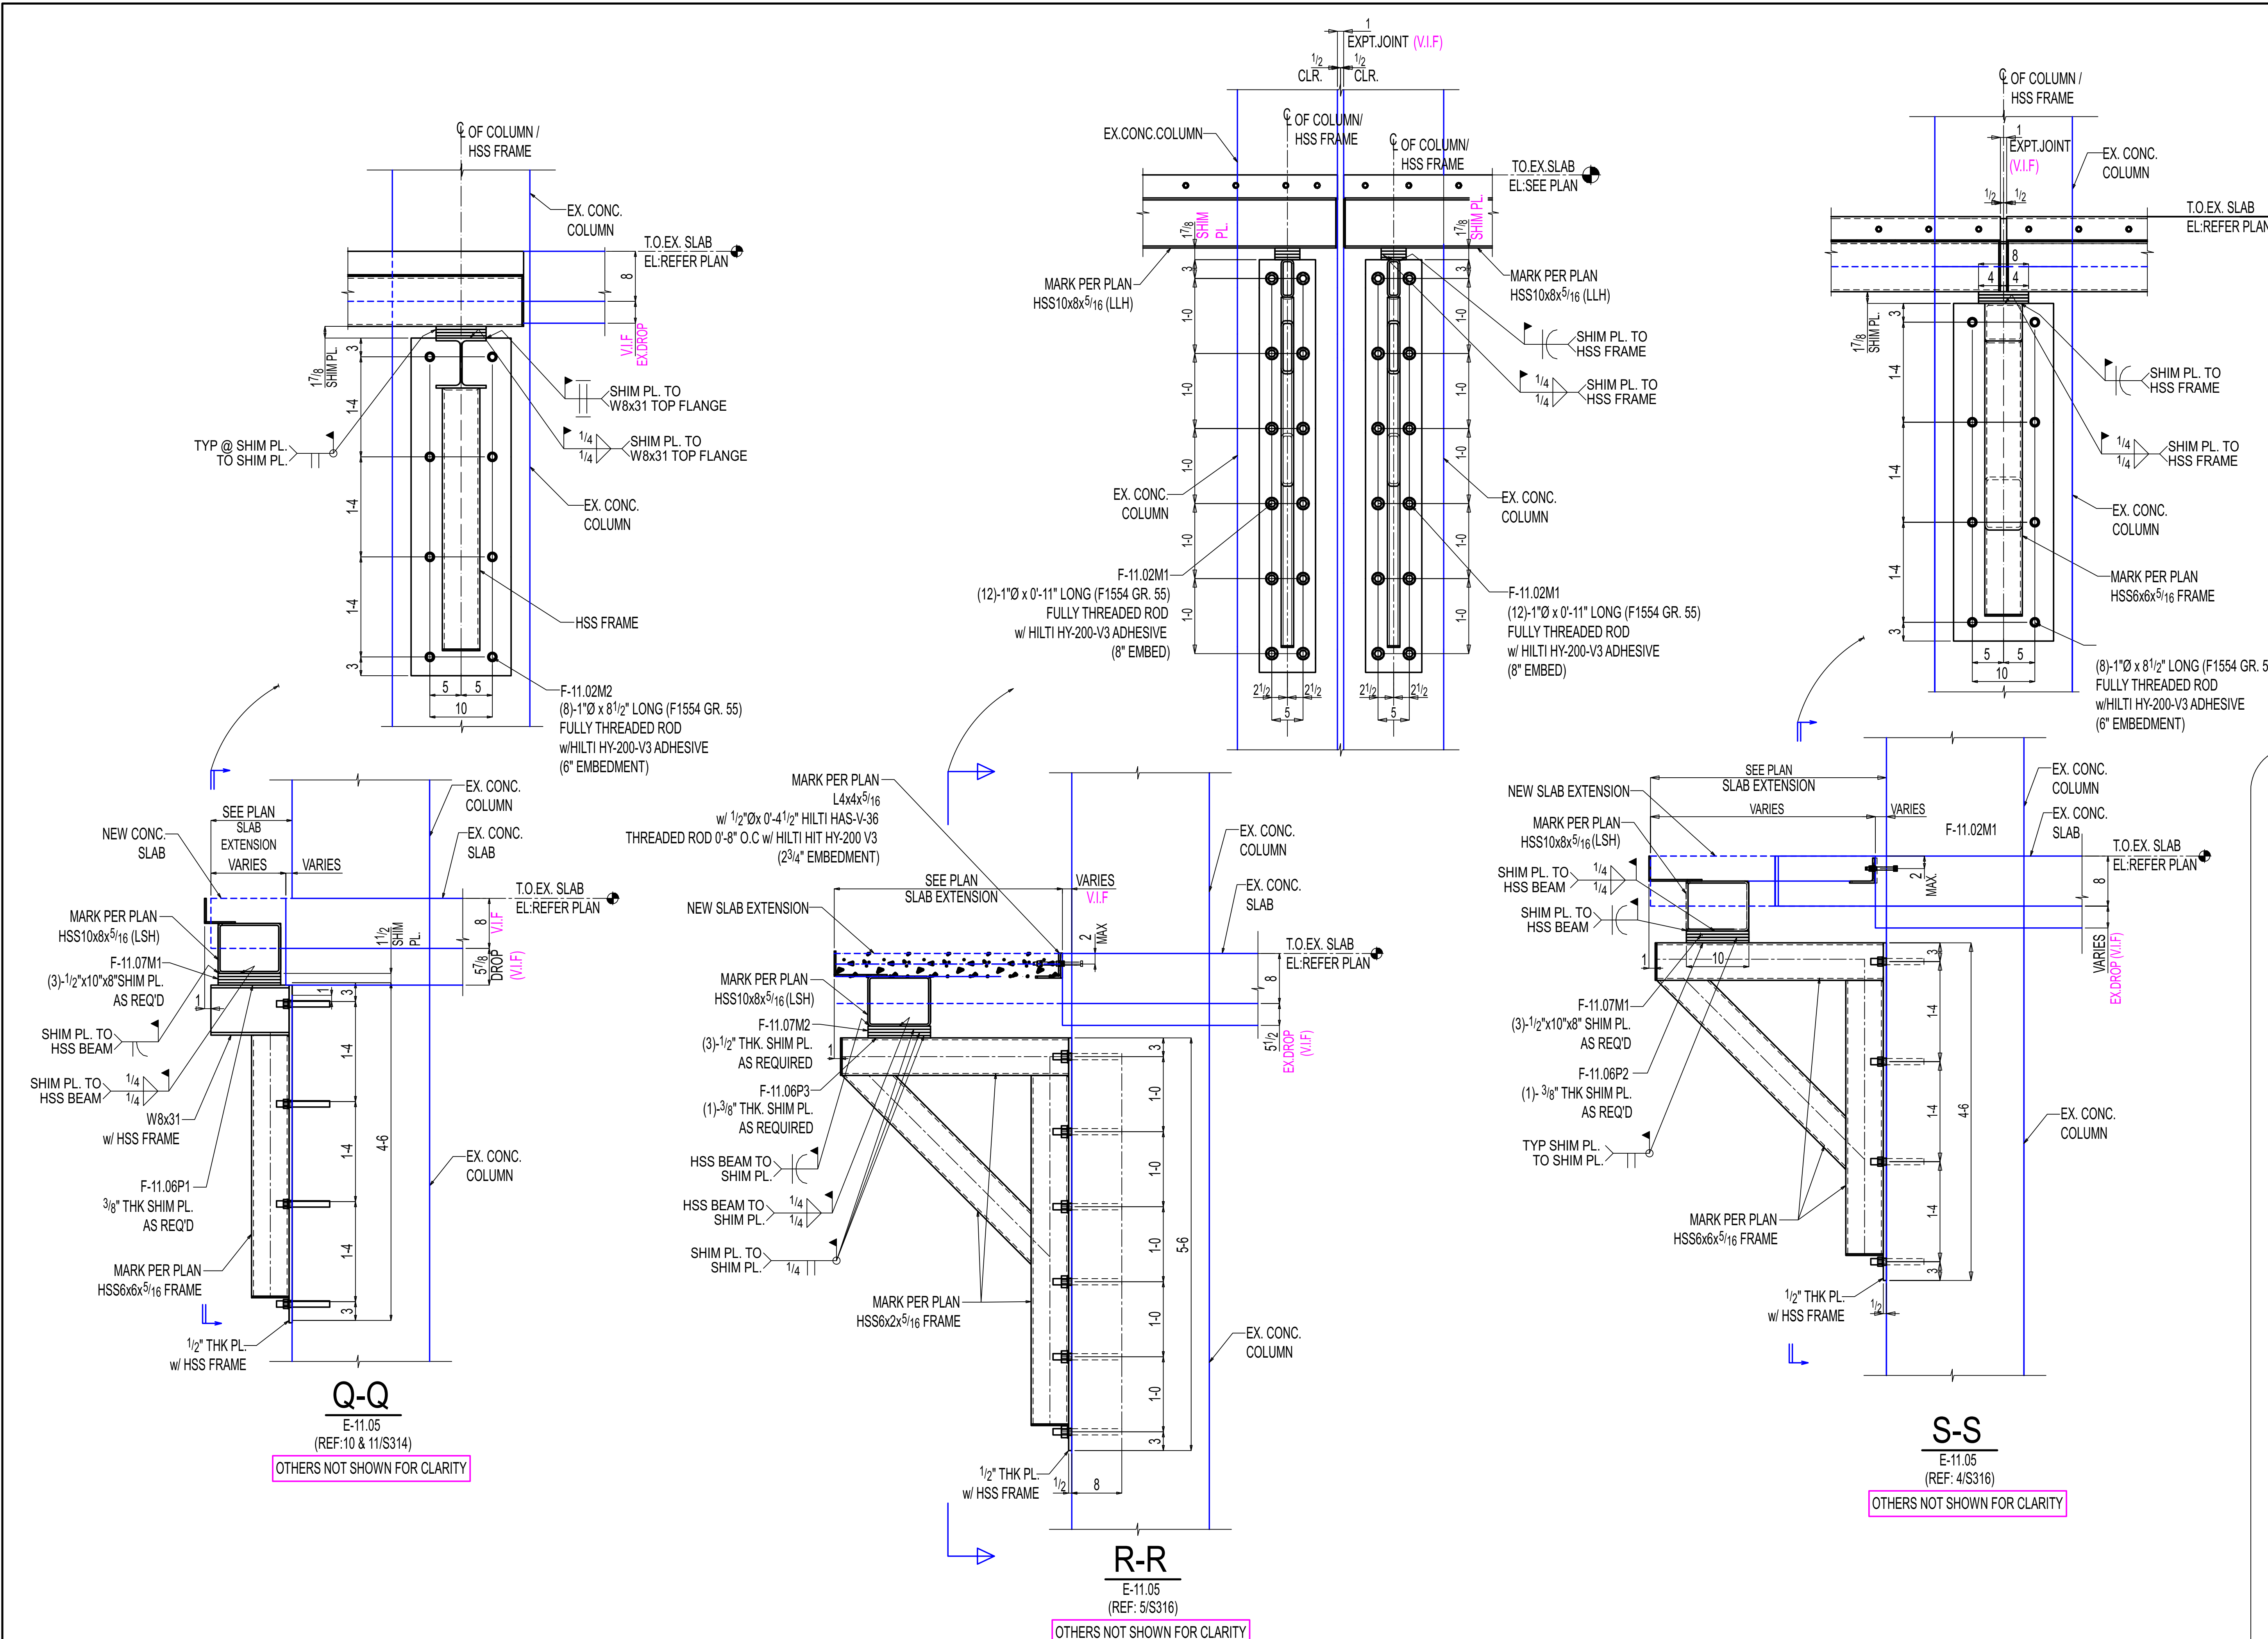

SHOP / ERECTOR NOTE:
LOCATE EXISTING REBAR PRIOR TO FABRICATION OF PLATE.
DO NOT DRILL THROUGH REBAR.

General Notes

- *Structural steel shall conform to ASTM-A992.
- *Structural SQR/RND tubing conform to ASTM A500 Grade C
- *Pipe shall conform to ASTM A53, Grade B.
- *Channels, Angles and plates shall conform to A36.
- *All bolts shall be 3/4" High strength in accordance with ASTM A325 (UNO)
- *Welding Electrodes for Carbon steel :E70xx

# of Copies	Revision/ Issue	Destination	Date
3	0	For Construction	11-14-2025
2	B	For Re-Approval	10-24-2025
1	A	For Approval	09-19-2025

IRON FABRICATION SERVICES, LLC.

3029 M. Street, NW, Suite 202
Washington, DC 20007
Tel: 202-800-5599
Fax: 202-478-0303


Project Name and Address
MARYLAND AVENUE

Location: **1250 MARYLAND AVENUE SW
WASHINGTON, DC 20024**





Contractor:
BALFOUR BEATTY

Approved for Fabrication by:	Signature
------------------------------	-----------

Contract # 224009	Drawing # E-11.06
Contract Item: LEVEL-05 SLAB EXTENSION	
Ref: SOW-11: 3,4,5&6 / S307	
Date 01/20/2025	Drawing Title: SOW #11 LEVEL-05 NEW SLAB EXTENSION SUPPORT SECTIONS
Scale VARIES	

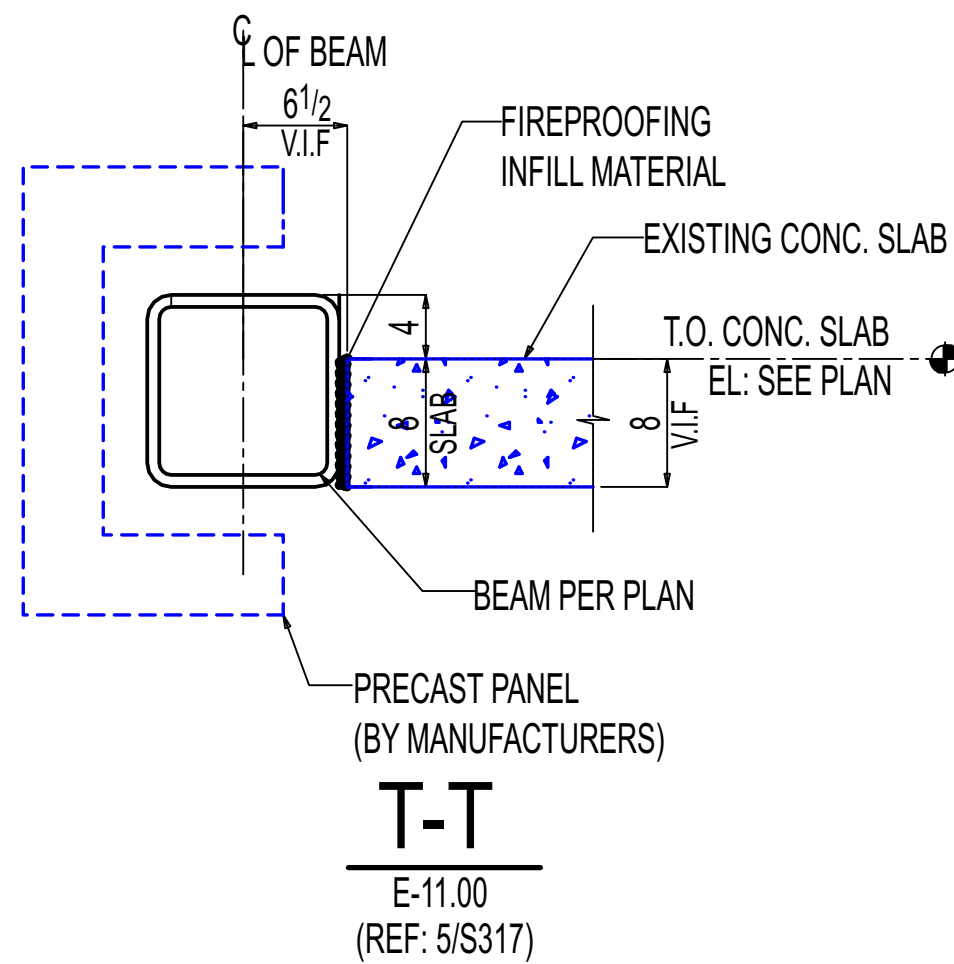

NOTE:
1. PRECAST CONNECTION TO HSS BEAM BY PRECAST MANUFACTURER.

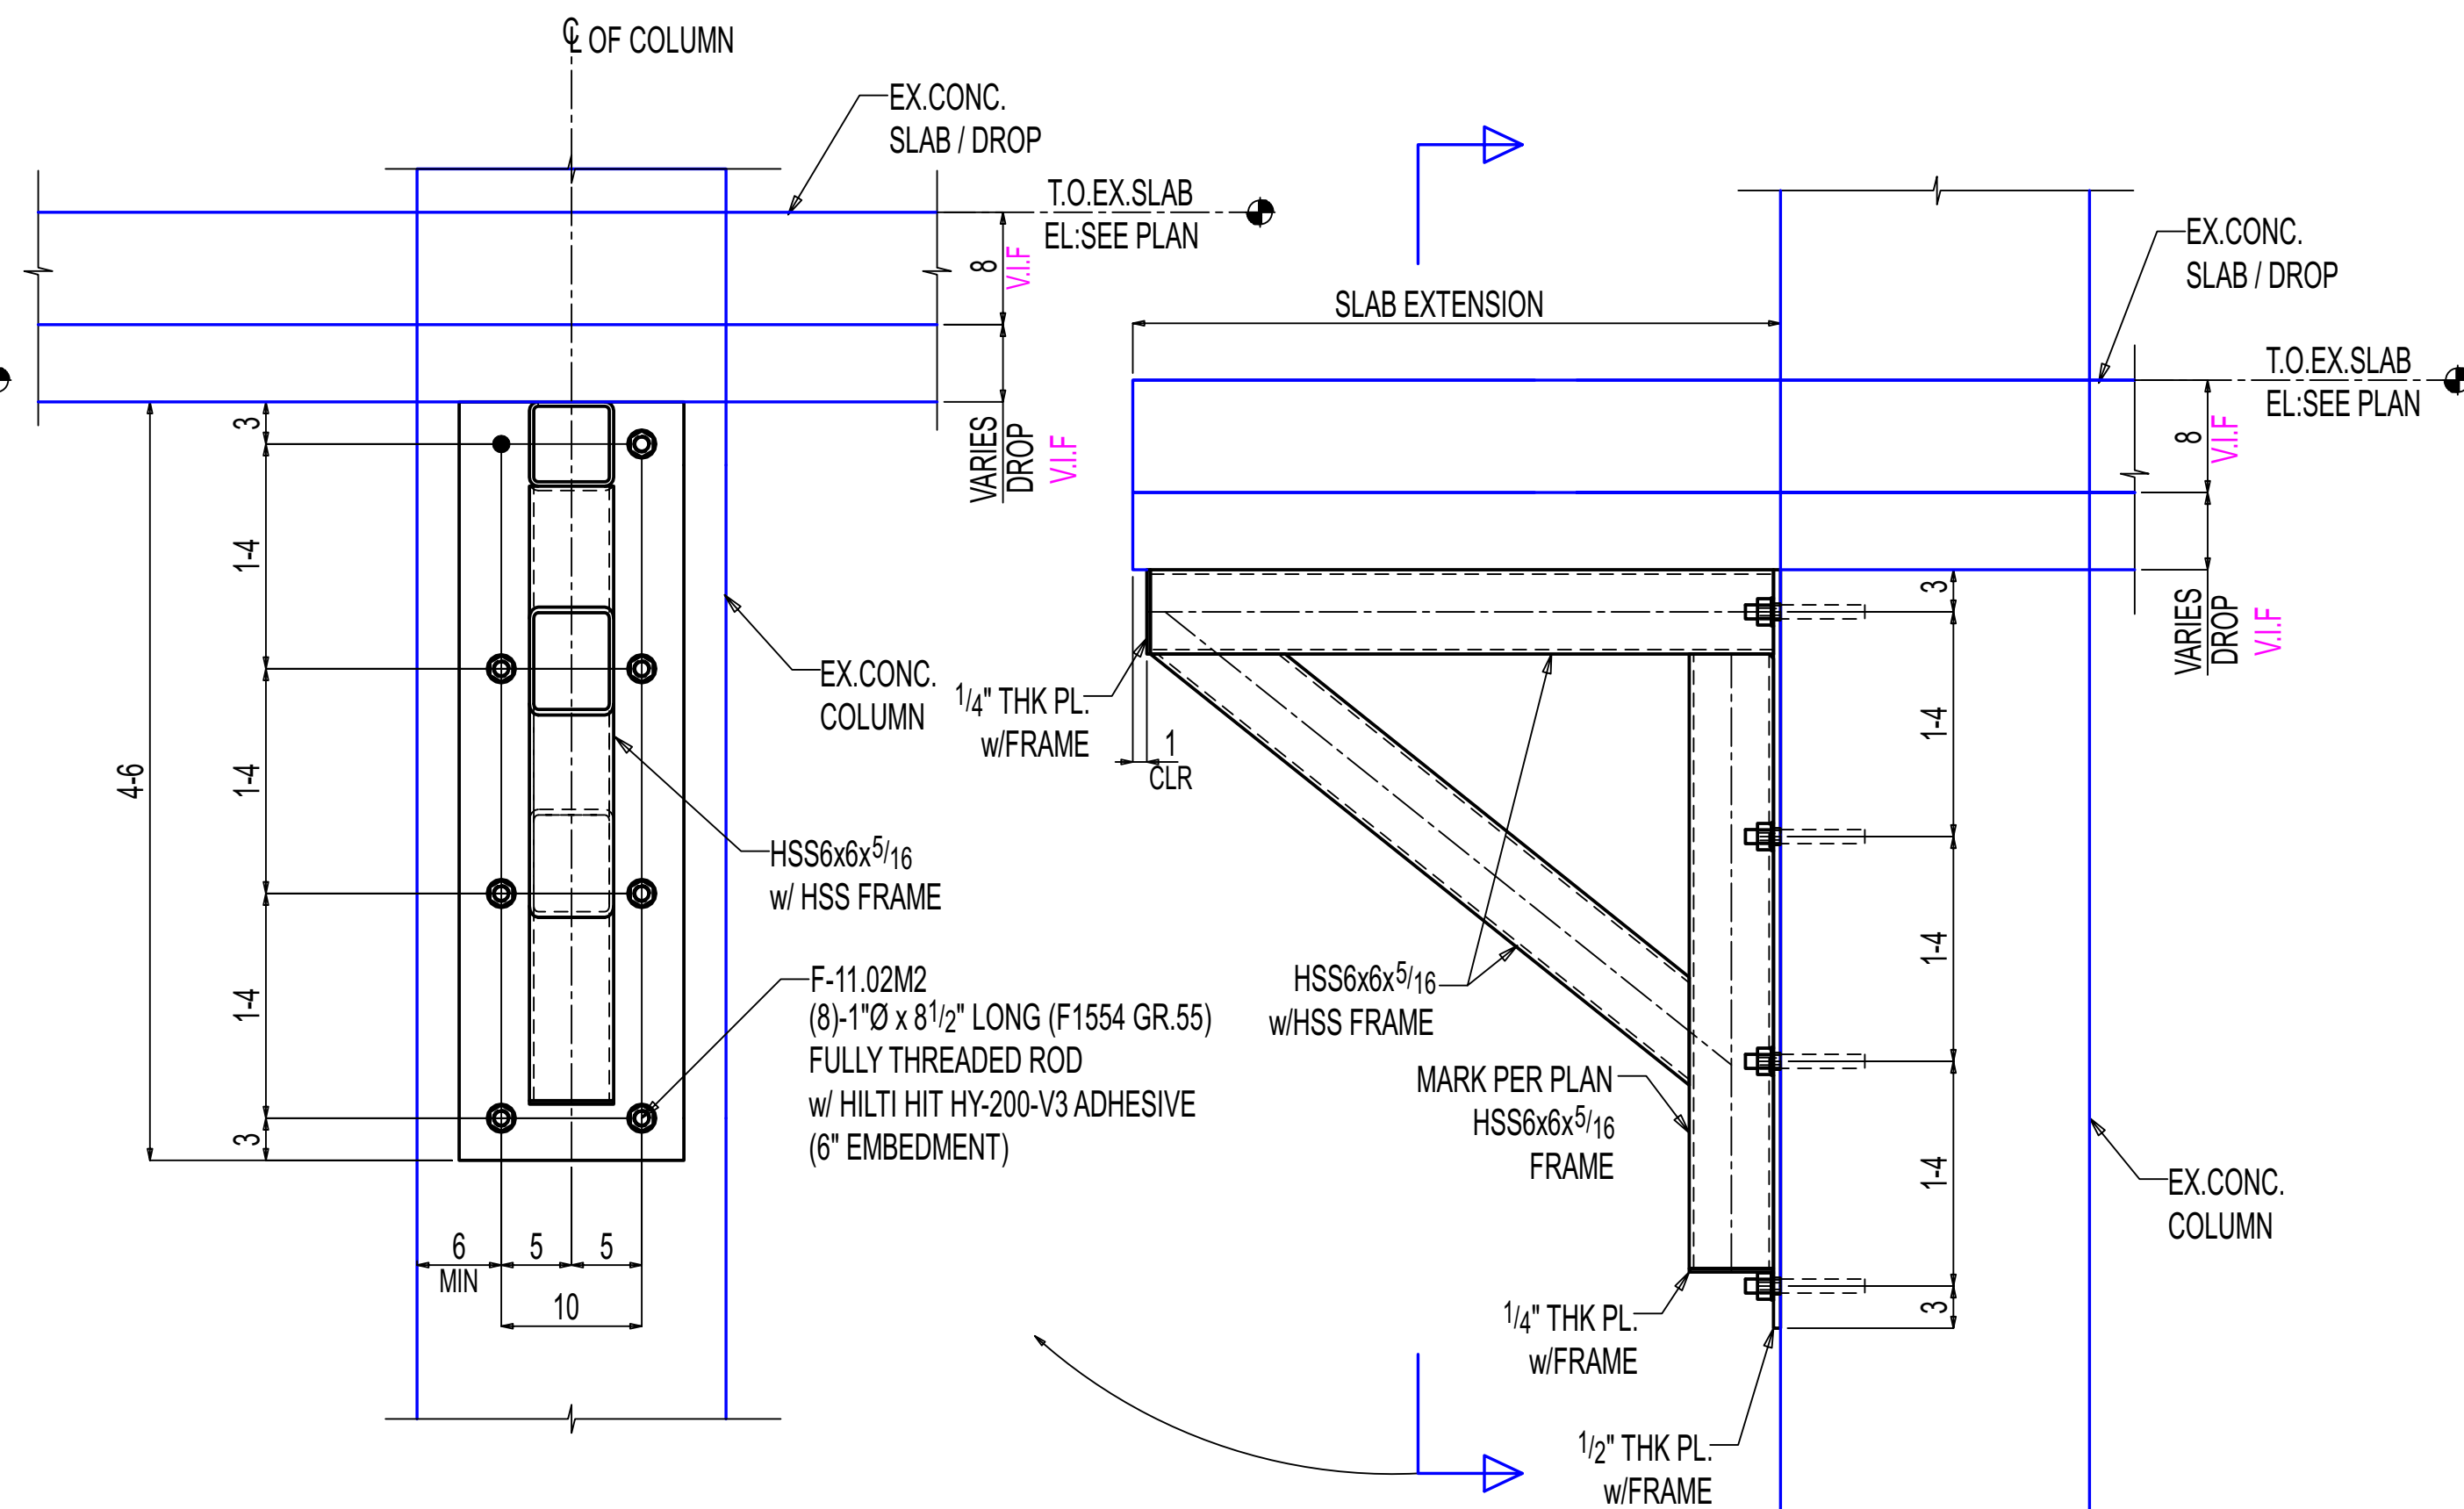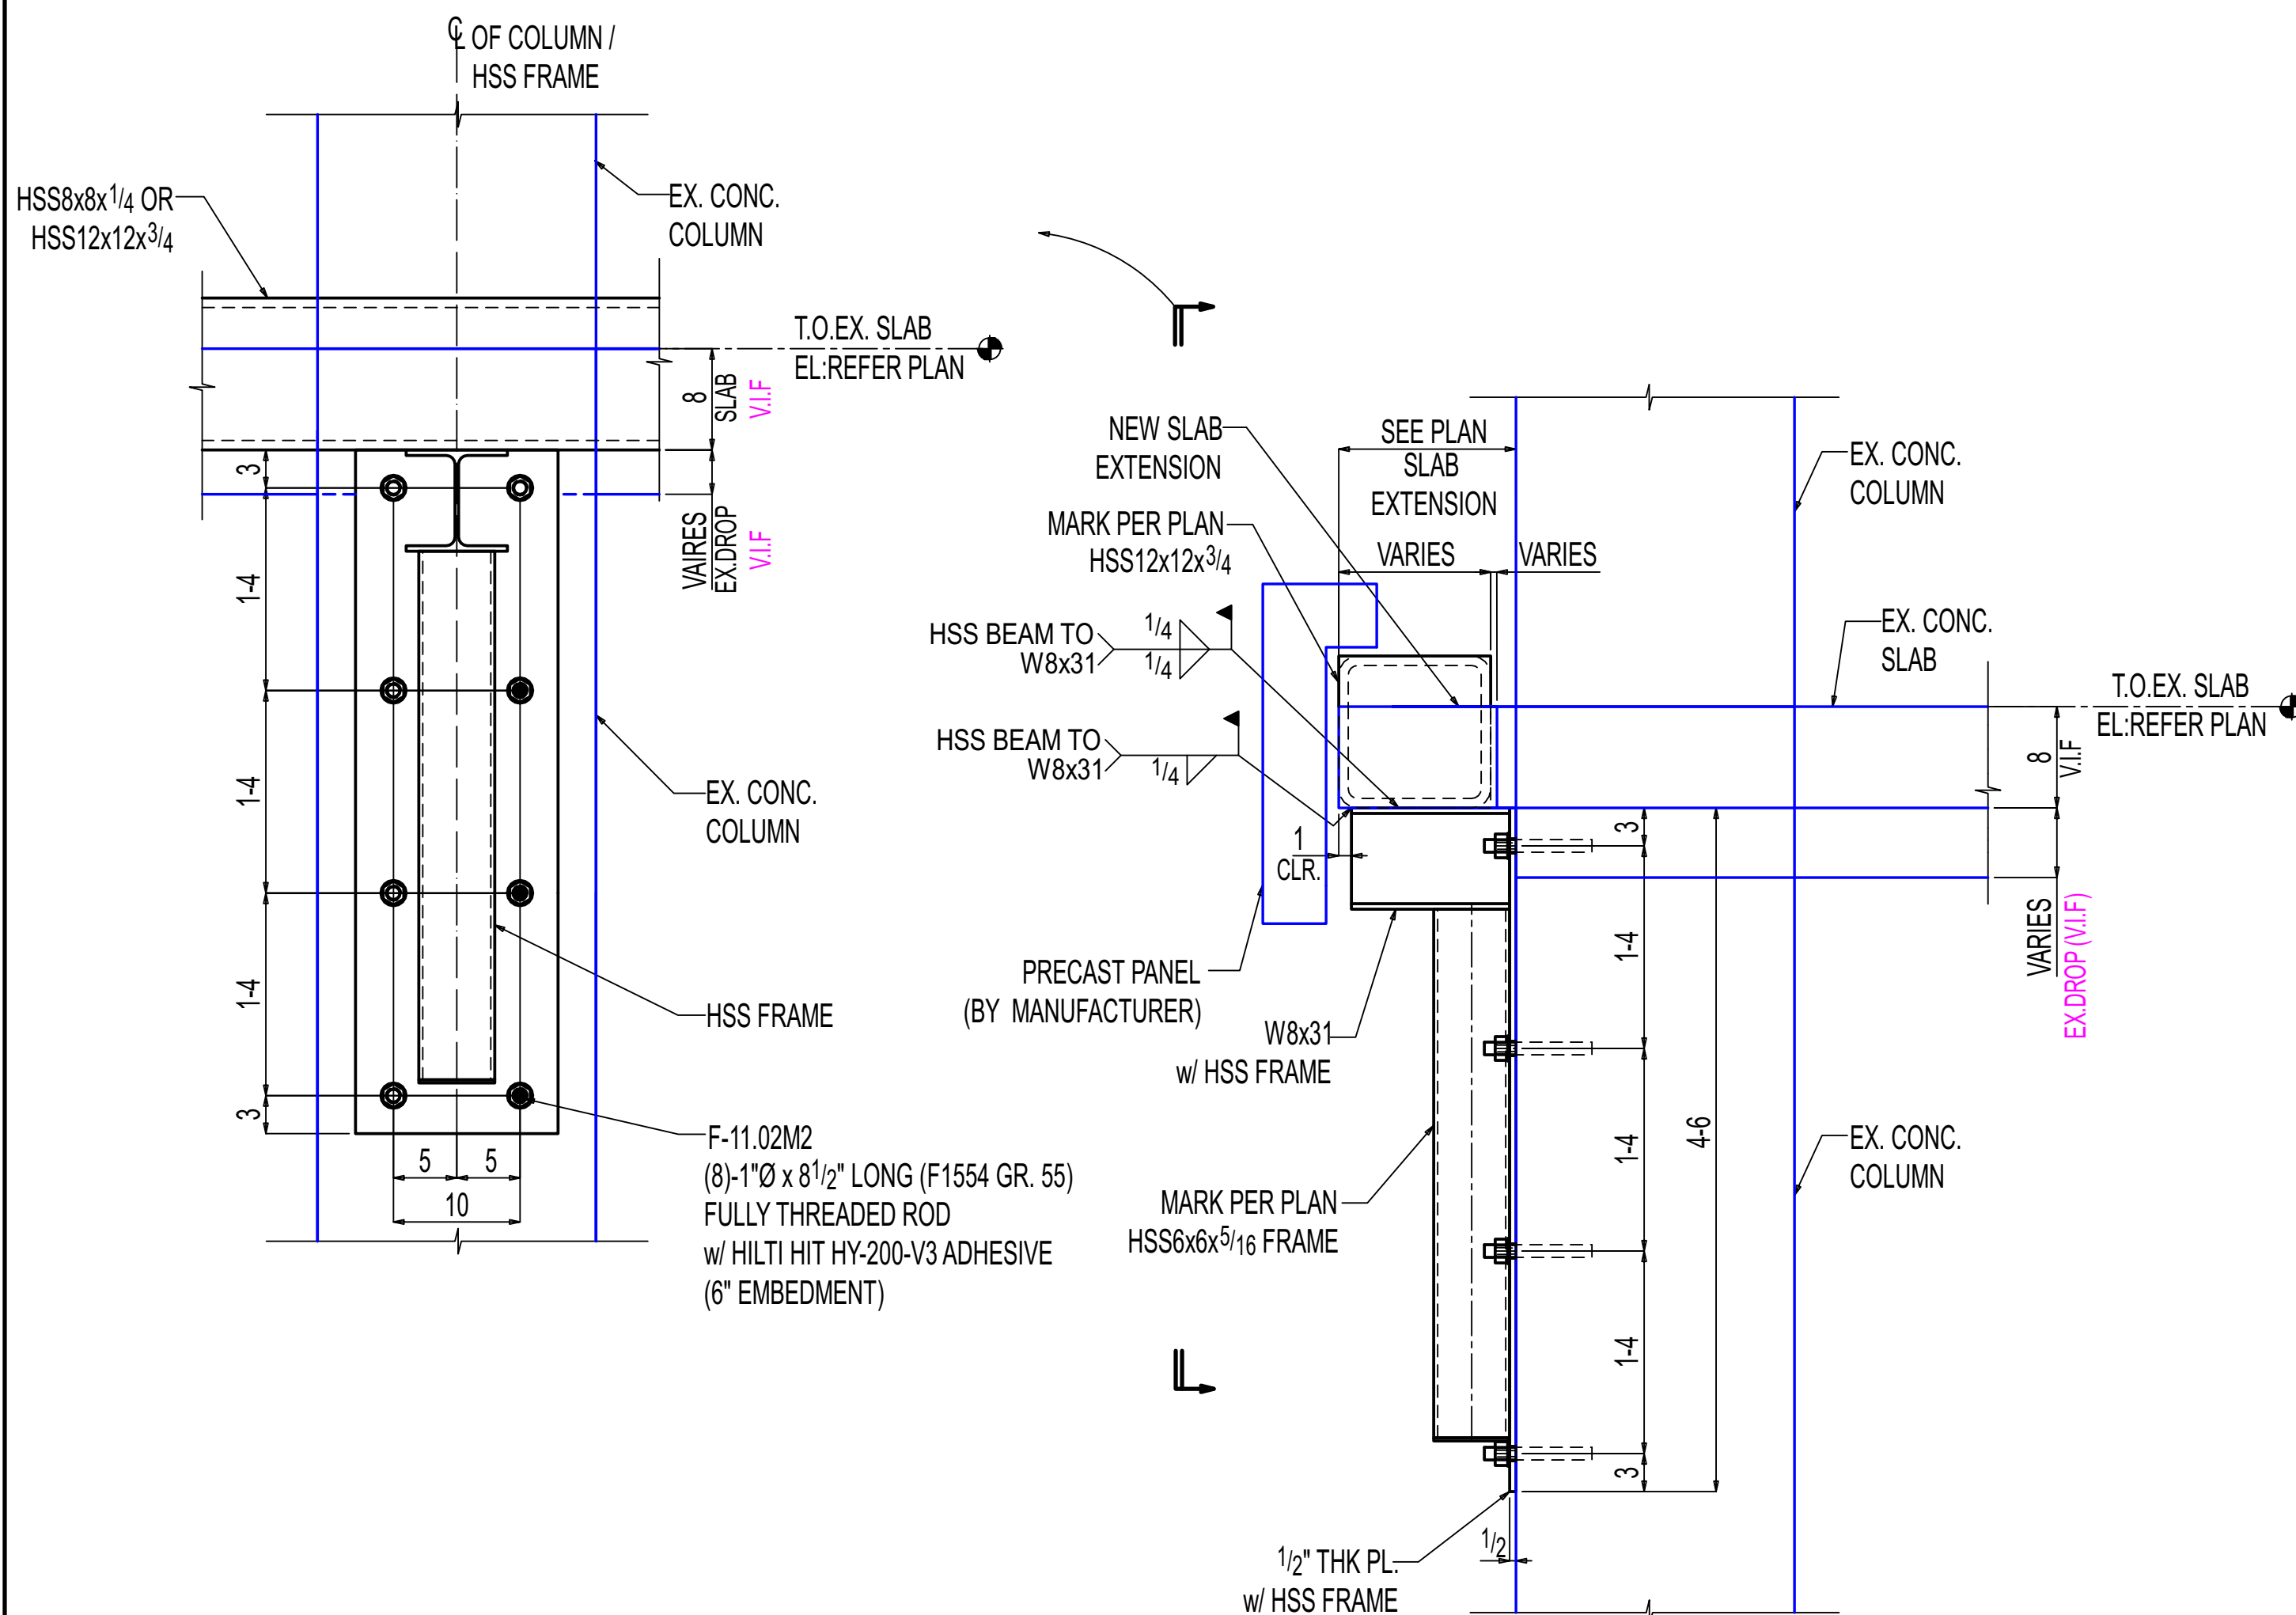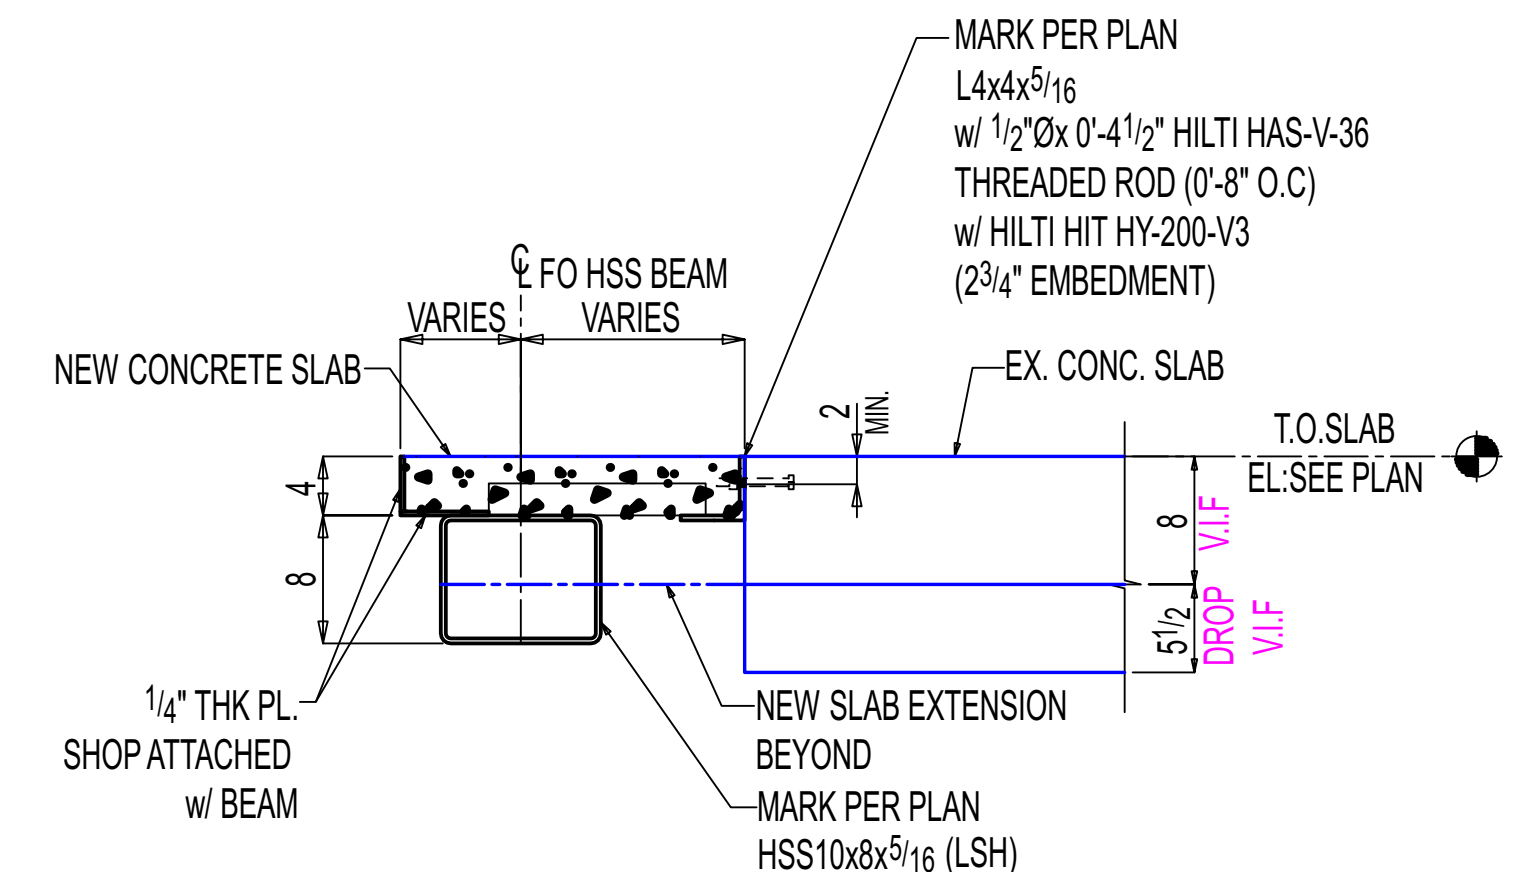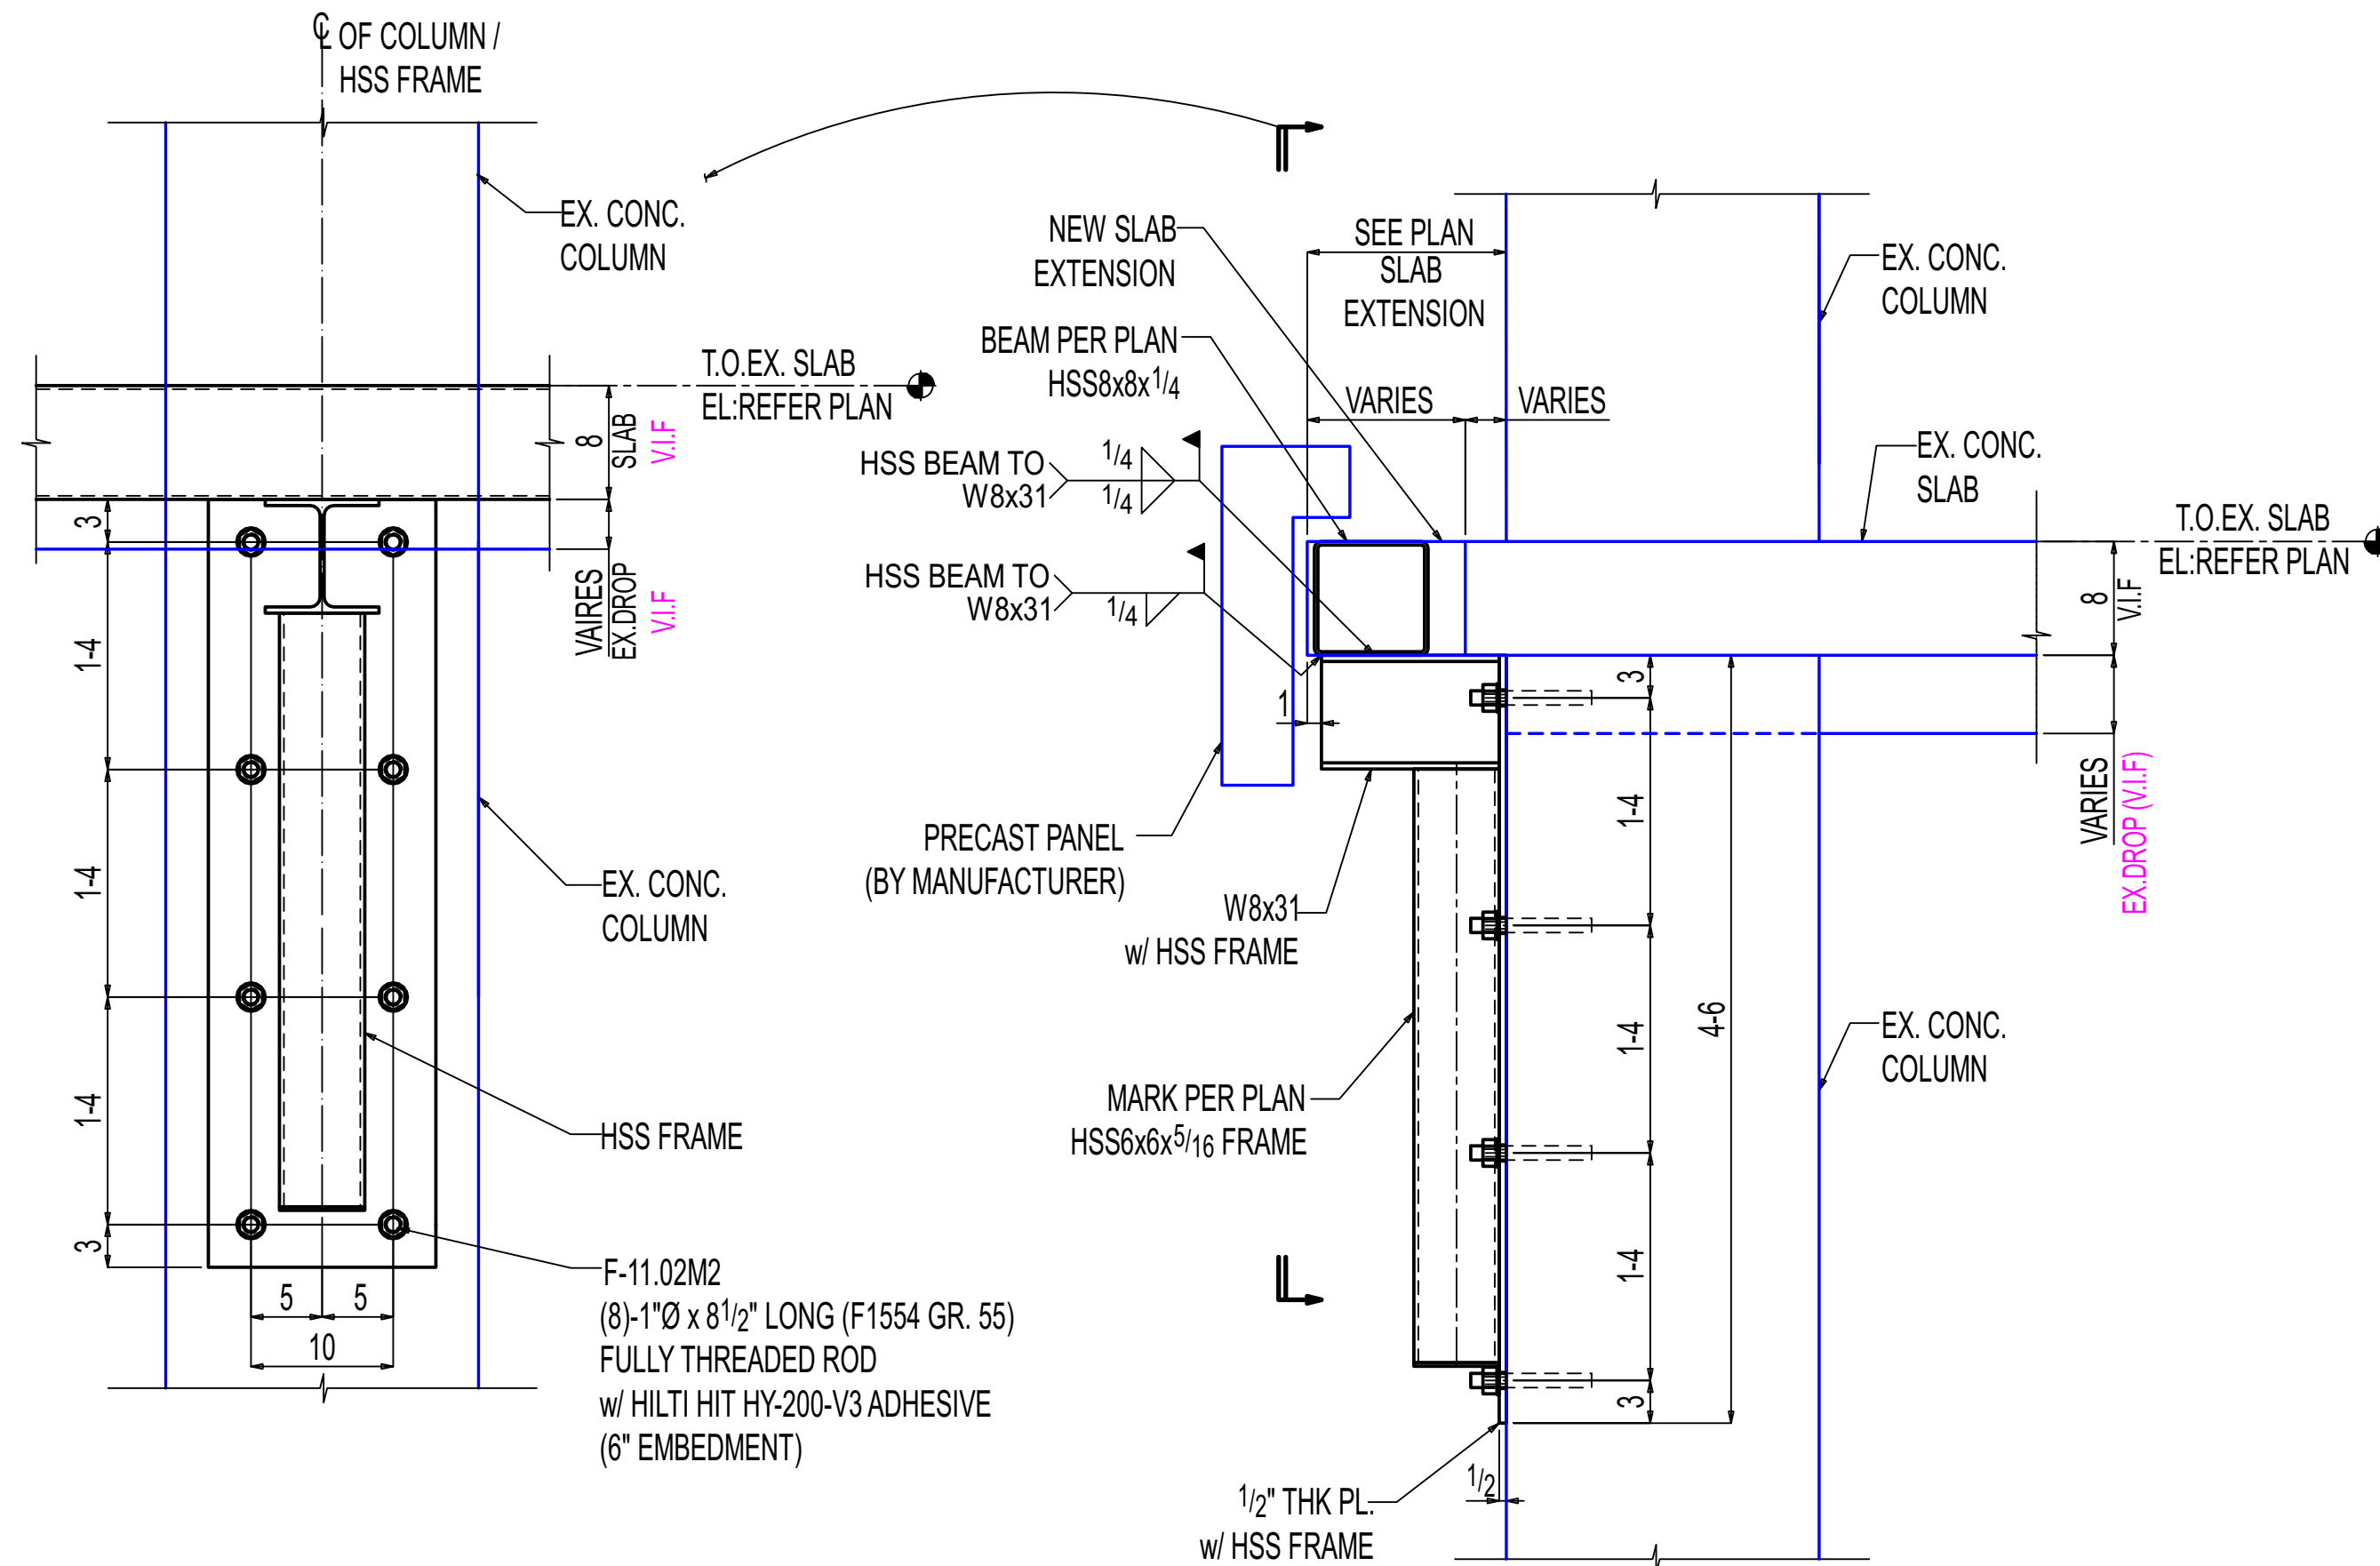

SHOP / ERECTOR NOTE:
LOCATE EXISTING REBAR PRIOR TO FABRICATION OF PLATE.
DO NOT DRILL THROUGH REBAR.

General Notes			
*Structural steel shall conform to ASTM-A992.			
*Structural SQR/RND tubing conform to ASTM A500 Grade C.			
*Pipe shall conform to ASTM A53, Grade B.			
*Channels, Angles and plates shall conform to A36.			
*All bolts shall be 3/4" High strength in accordance with ASTM A325 (UNO)			
*Welding Electrodes for Carbon steel :E70xx			
# of Copies	Revision/ Issue	Destination	Date
3	0	For Construction	11-14-2025
2	B	For Re-Approval	10-24-2025
1	A	For Approval	09-19-2025

IRON FABRICATION SERVICES, LLC.

3029 M. Street, NW, Suite 202
Washington, DC 20007
Tel: 202-800-5599
Fax: 202-478-0303

Project Name and Address
MARYLAND AVENUE

Location: **1250 MARYLAND AVENUE SW
WASHINGTON, DC 20024**

Contractor:
BALFOUR BEATTY

Approved for Fabrication by: _____
Signature

Contract #	224009	Drawing #	E-11.07
Contract Item:	LEVEL-05 SLAB EXTENSION		
Ref:	SOW-11: 3,4,5&6 / S307		
Date	01/20/2025	Drawing Title:	SOW #11 LEVEL-05 NEW SLAB EXTENSION SUPPORT SECTIONS
Scale	VARIES		