



BILL OF MATERIAL							
LINE #	QTY	PC	MARK	DESCRIPTION	LENGTH	WEIGHT	ADVANCE
	TOTAL					TOTAL	MILL #
ONE	F-11.03FR1	FRAME				438	
1	F-11.03FR1	HSS6x6x ⁵ / ₁₆		3	7 ³ / ₄	A500C	85
1	hss350	HSS6x6x ⁵ / ₁₆		4	11 ⁵ / ₁₆	A500C	115
1	hss351	HSS6x6x ⁵ / ₁₆		4	8 ⁷ / ₁₆	A500C	110
1	pl818	PL ¹ / ₂ x16		4	6	A36	123
1	pl2416	PL ¹ / ₂ x6		0	7 ⁷ / ₁₆	A36	3
1	pl696	PL ¹ / ₂ x6		0	6	A36	3
ONE	F-11.03M1	PLATE				189	
1	F-11.03M1	PL1x18		2	1	A36	128
1	pl238	PL1x8		1	6	A36	41
3	pl240	PL ¹ / ₂ x7		0	7	A36	21
ONE	F-11.03M2	PLATE				37	
1	F-11.03M2	PL ³ / ₄ x6		1	3	A36	19
2	pl3640	PL ³ / ₄ x6		0	7	A36	18
ONE	F-11.03M3	PLATE				55	
1	F-11.03M3	PL ³ / ₄ x6		2	5 ³ / ₈	A36	38
2	pl599	PL ³ / ₄ x6		0	7	A36	18
ONE	F-11.03M4	HSS				41	
1	F-11.03M4	HSS6x6x ⁵ / ₁₆		1	0	A500C	32
2	pl3643	PL ¹ / ₂ x8		0	8	A36	9
ONE	F-11.03M5	HSS				33	
1	F-11.03M5	HSS10x10x ⁵ / ₁₆		0	5 ¹ / ₂	A500C	18
2	pl538	PL ¹ / ₂ x10		0	10	A36	14
2	F-11.03M6	HSS				35	
2	F-11.03M6	HSS ¹ / ₂ x5 ¹ / ₂ x ⁵ / ₁₆		0	7 ¹ / ₂	A500C	27
4	pl698	PL ¹ / ₂ x5 ¹ / ₂		0	5 ¹ / ₂	A36	9
6	F-11.03M10	PLATE WASHER				8	
6	F-11.03M10	PL ¹ / ₂ x3		0	3	A36	8
ONE	F-11.03EP1	EMBED PLATE				230	
1	F-11.03EP1	PL ⁵ / ₈ x22		4	11	A36	230
10		FIELD BOLTS					
		³ / ₄ Dia HILTI HAS V-36		0	8	+1HD WASH	
		w/ HILTI HIT HY-200 V3				(5" EMBEDMENT)	
		ADHESIVE					
ONE	F-11.03EP2	EMBED PLATE				117	
1	F-11.03EP2	PL ⁵ / ₈ x22		2	6	A36	117
6		FIELD BOLTS					
		³ / ₄ Dia HILTI HAS V-36		0	8		
		w/ HILTI HIT HY-200 V3				(5" EMBEDMENT)	
		ADHESIVE					
ONE	F-11.03LP1	LEVELING PLATE				9	
1	F-11.03LP1	PL ¹ / ₂ x7		1	6	A36	9
ONE	F-11.03LP2	LEVELING PLATE				8	
1	F-11.03LP2	PL ¹ / ₂ x6 ¹ / ₂		1	6	A36	8


Total weight : 1201

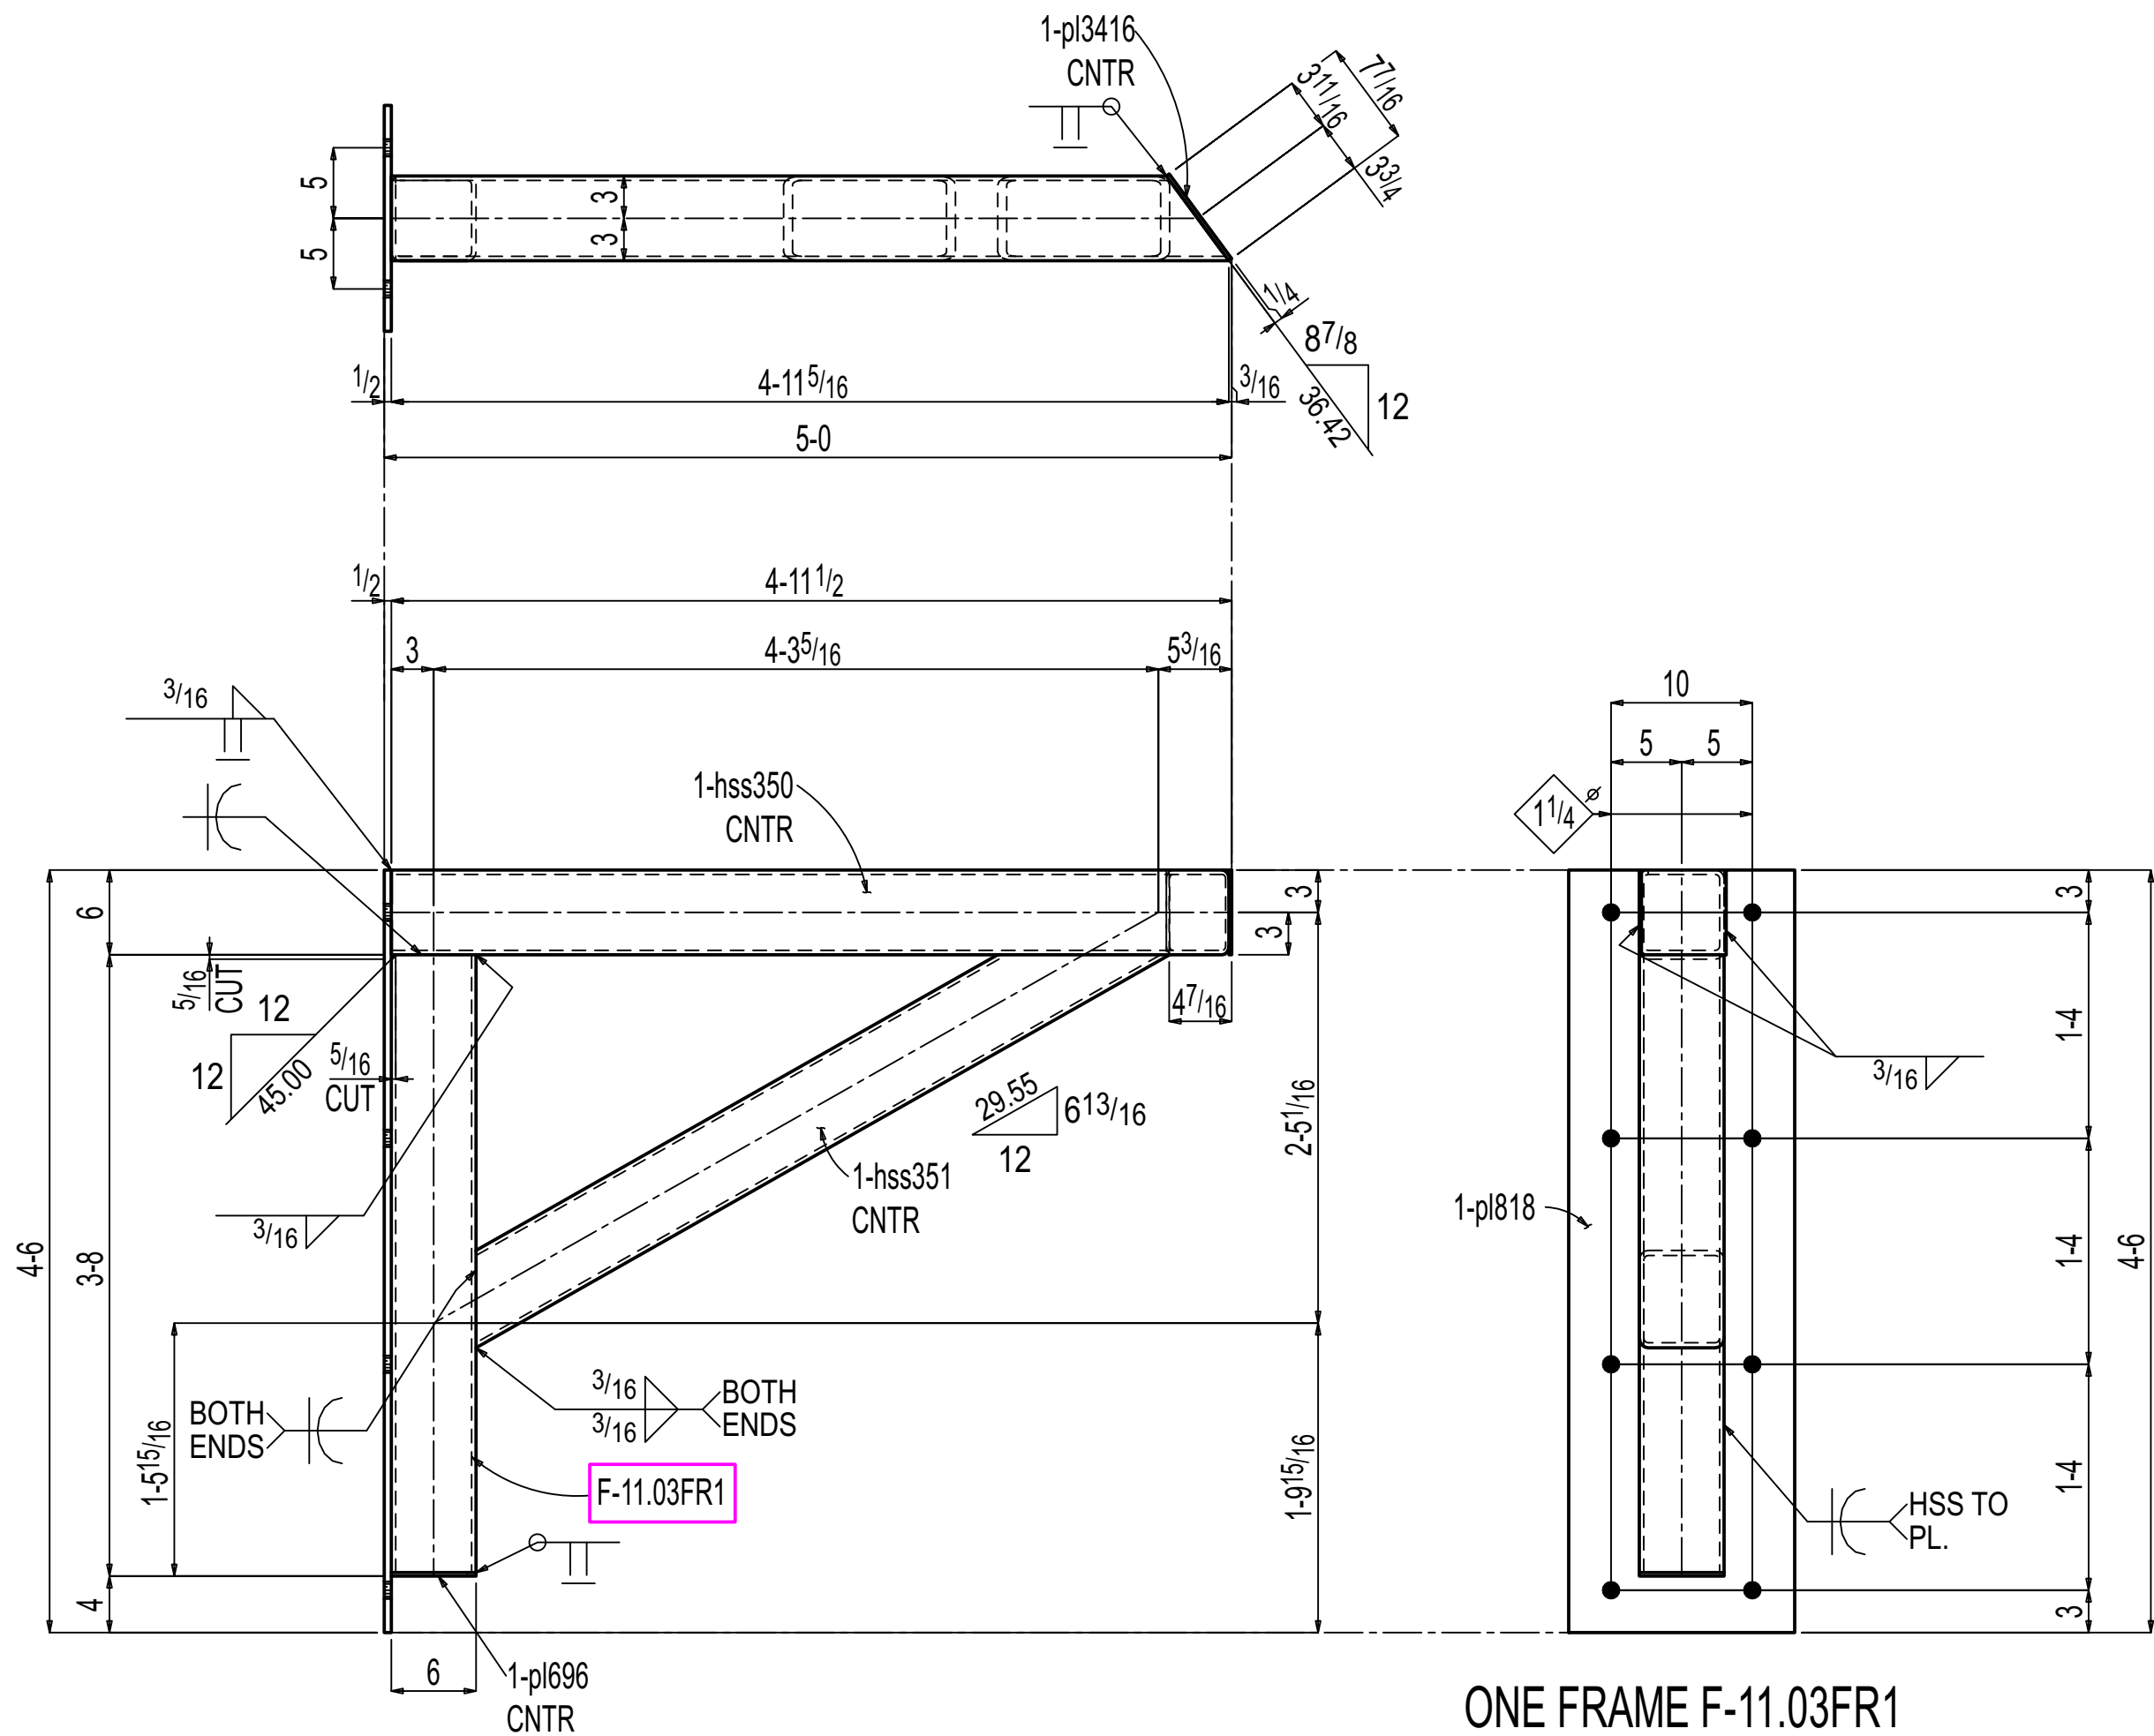


ONE FRAME F-11.03FR1

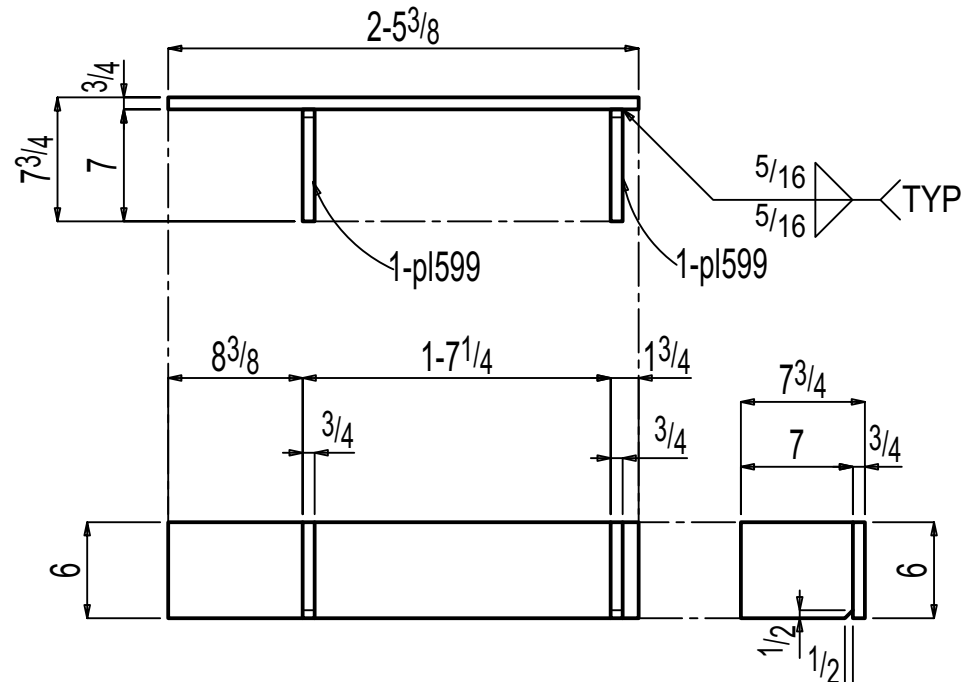


ONE PLATE F-11.03M3

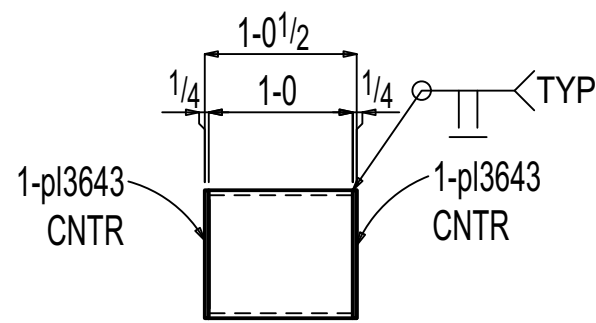


ONE HSS F-11.03M4

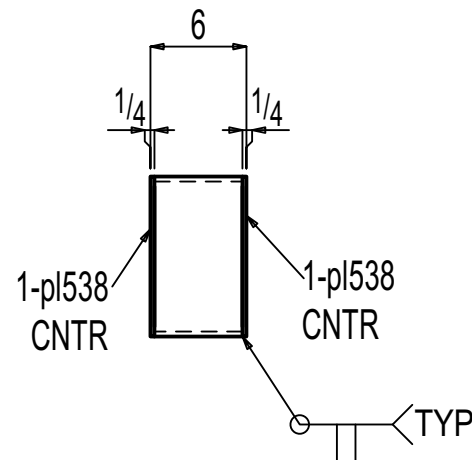


ONE HSS F-11.03M5

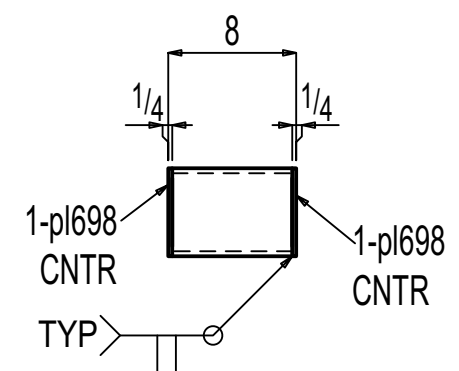


2 HSES F-11.03M6

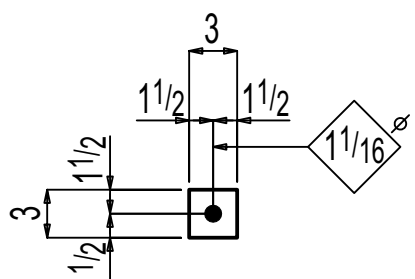


6 PLATE WASHERS F-11.03M10

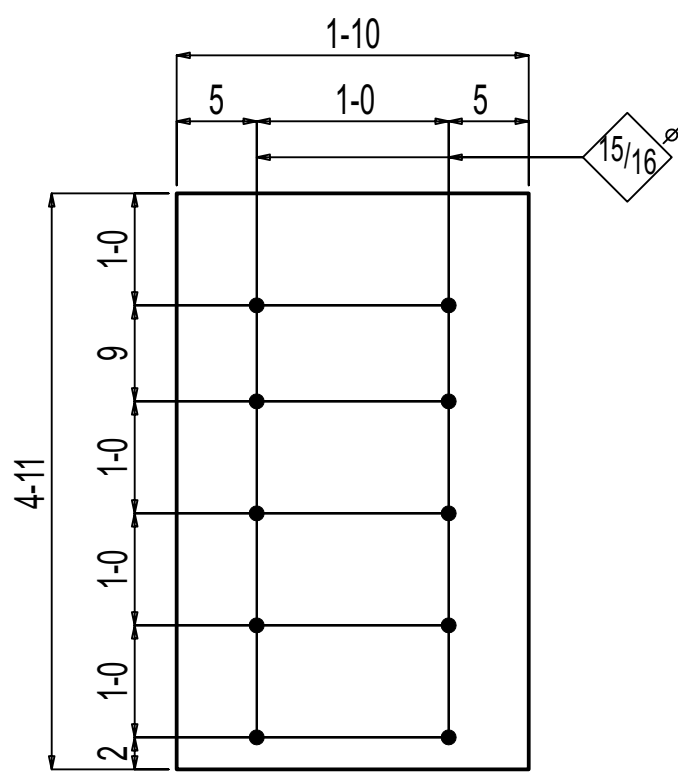


ONE EMBED PLATE F-11.03EP1

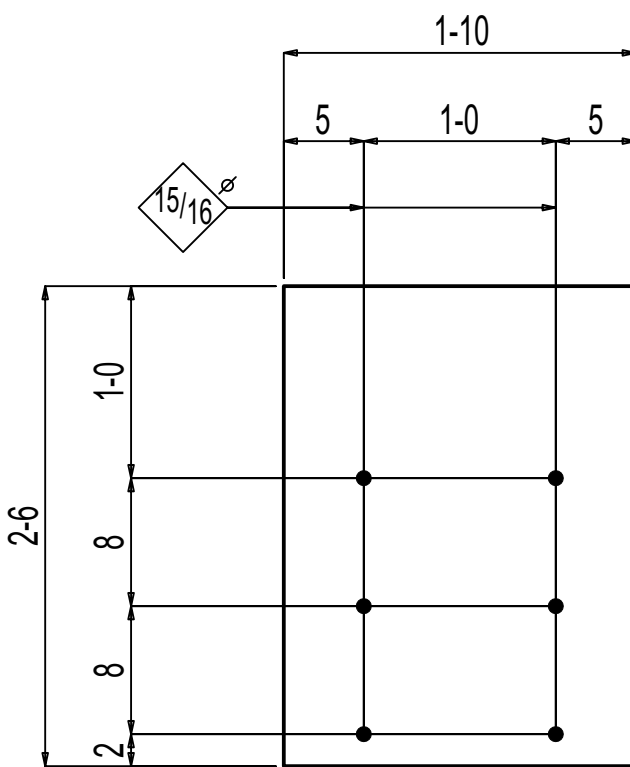

ONE EMBED PLATE F-11.03EP2

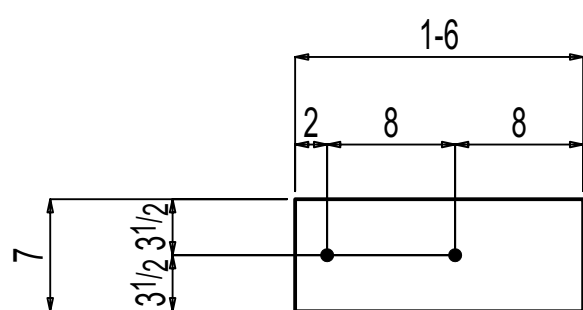

ONE LEVELING PLATE F-11.03LP1

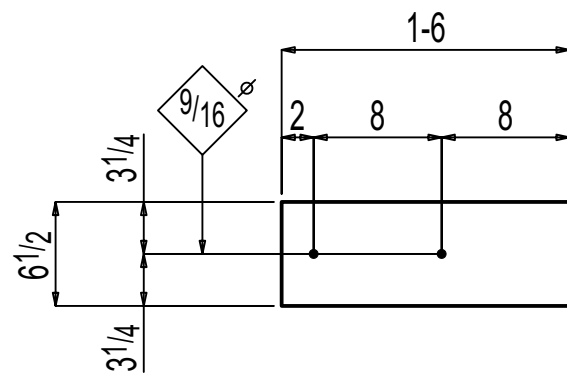

ONE LEVELING PLATE F-11.03LP2

PAINT PREPARATION :NO PAINT
PREPARATION :SSPC-SP3

General Notes			
*Structural steel shall conform to ASTM-A992.			
*Structural SQR/RND,tubing conform to ASTM A500 Grade C			
*Pipe shall conform to ASTM A53, Grade B.			
*Channels, Angles and plates shall conform to A36.			
*All bolts shall be ³ / ₄ " High strength in accordance with ASTM A325 (UNO)			
*Welding Electrodes for Carbon steel :E70xx			
5	0	For Fabrication	11-14-2025
4	D	For Re-Approval	10-24-2025
3	C	For Re-Approval	09-19-2025
2	B	For Re-Approval	06-23-2025
1	A	For Approval	02-25-2025
# of Copies	Revision/ Issue	Destination	Date

IRON FABRICATION SERVICES, LLC.

3029 M. Street, NW, Suite 202
Washington, DC 20007
Tel: 202-800-5599
Fax: 202-478-0303

Project Name and Address
MARYLAND AVENUE

Location: **1250 MARYLAND AVENUE SW
WASHINGTON, DC 20024**

Contractor:

BALFOUR BEATTY

Approved for Fabrication by:

Signature

Contract # **224009**

Drawing # **F-11.03**

Contract Item: **FRAME**

Ref:

SOW - 11: E-11.00 - E-11.02

Date

01/ 23/ 2025

Drawing Title:

**FRAME & MISCELLANEOUS
DETAIL**

Scale

VARIES