
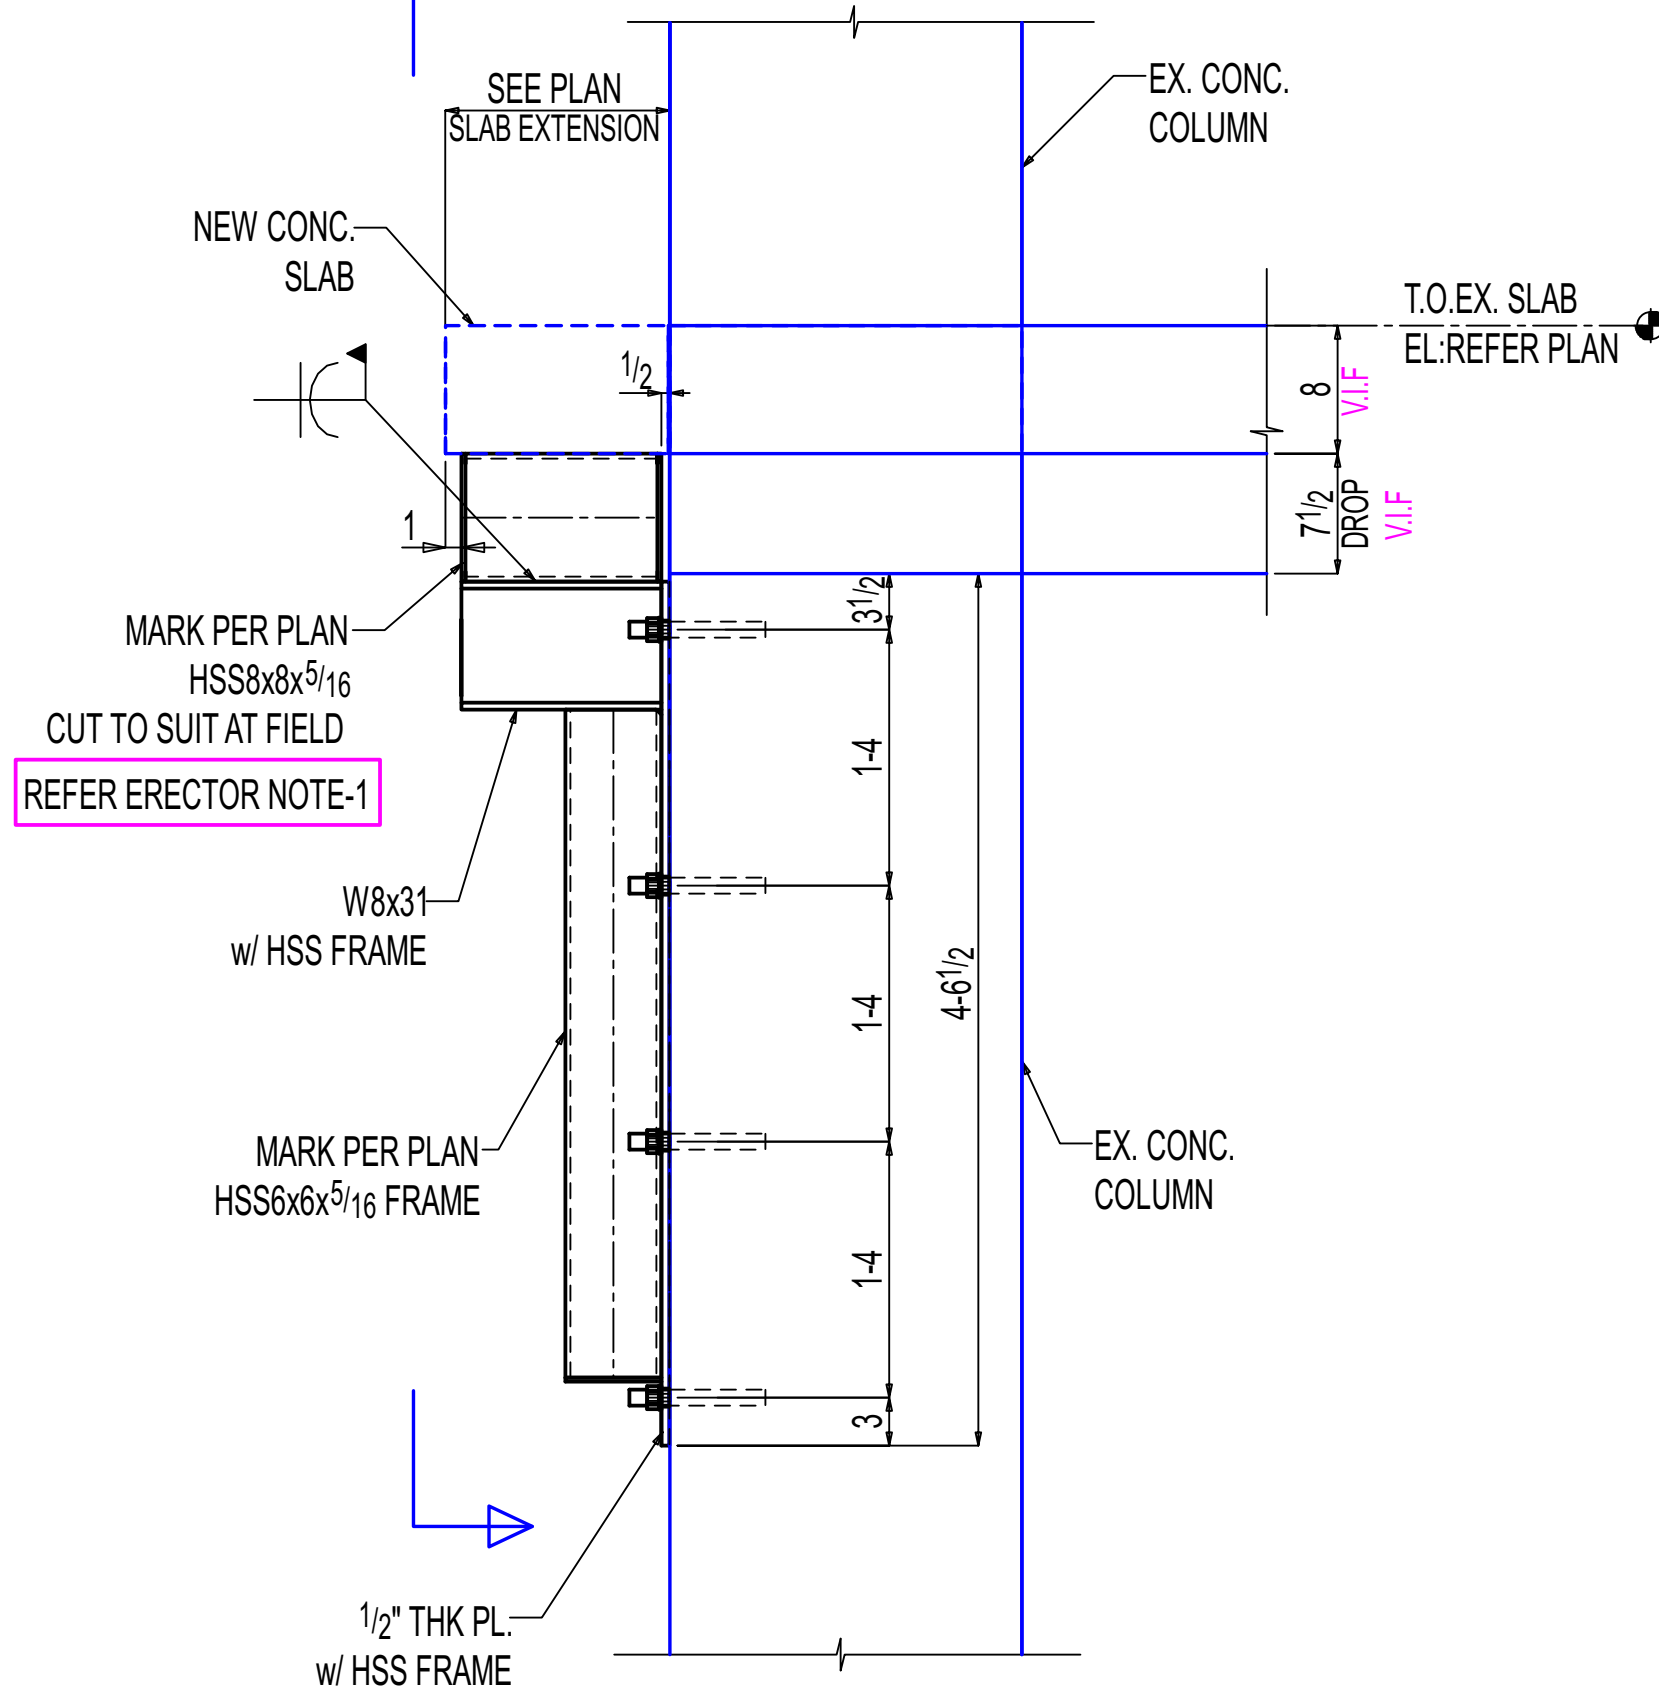



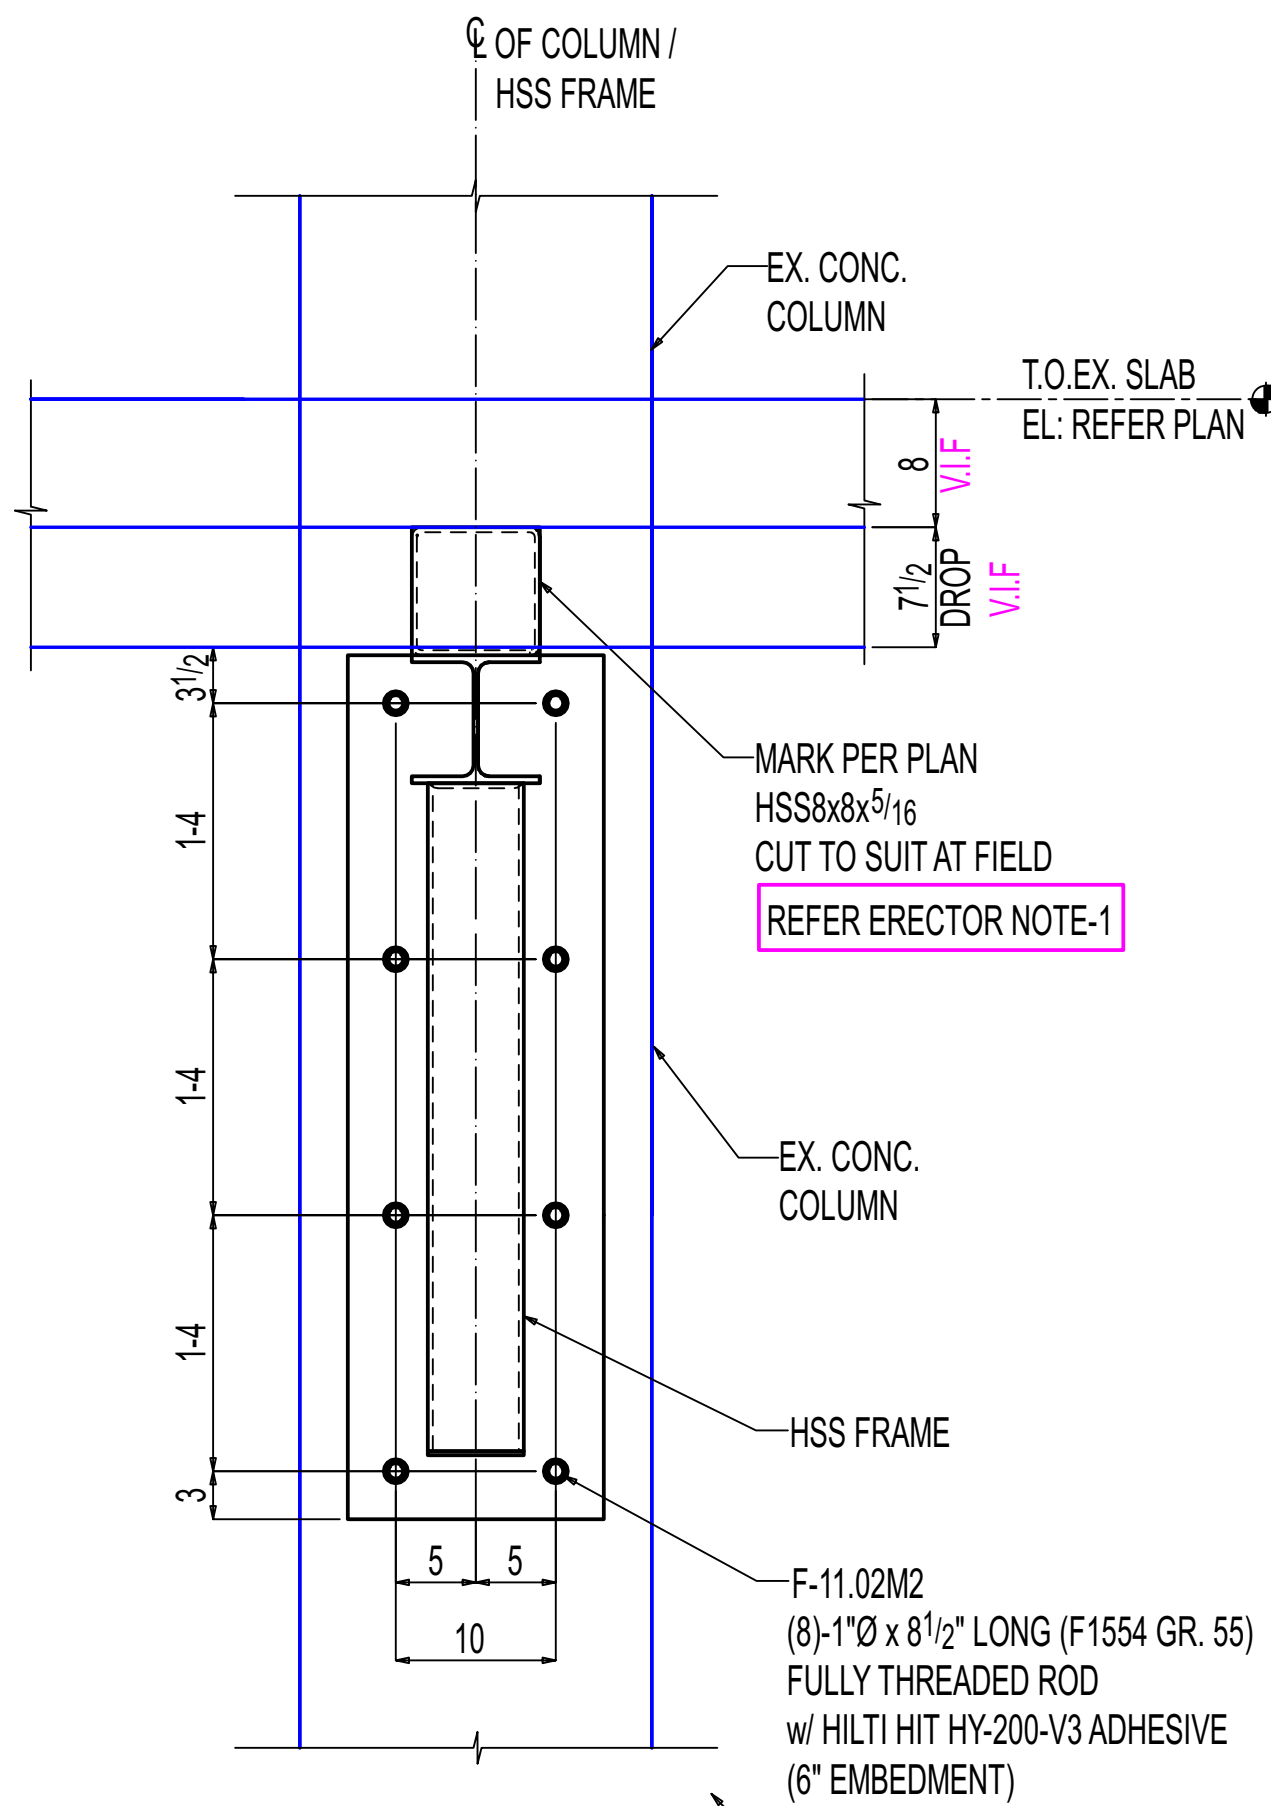


H-H

E-11.00A
(REF:10/S314)

OTHERS NOT SHOWN FOR CLARTY

*** ERECTOR NOTE:**
PROVIDE 1" NON-SHRINK GROUT x 12" LONG CENTERED BENEATH AT PRECAST ATTACHMENT POINTS.

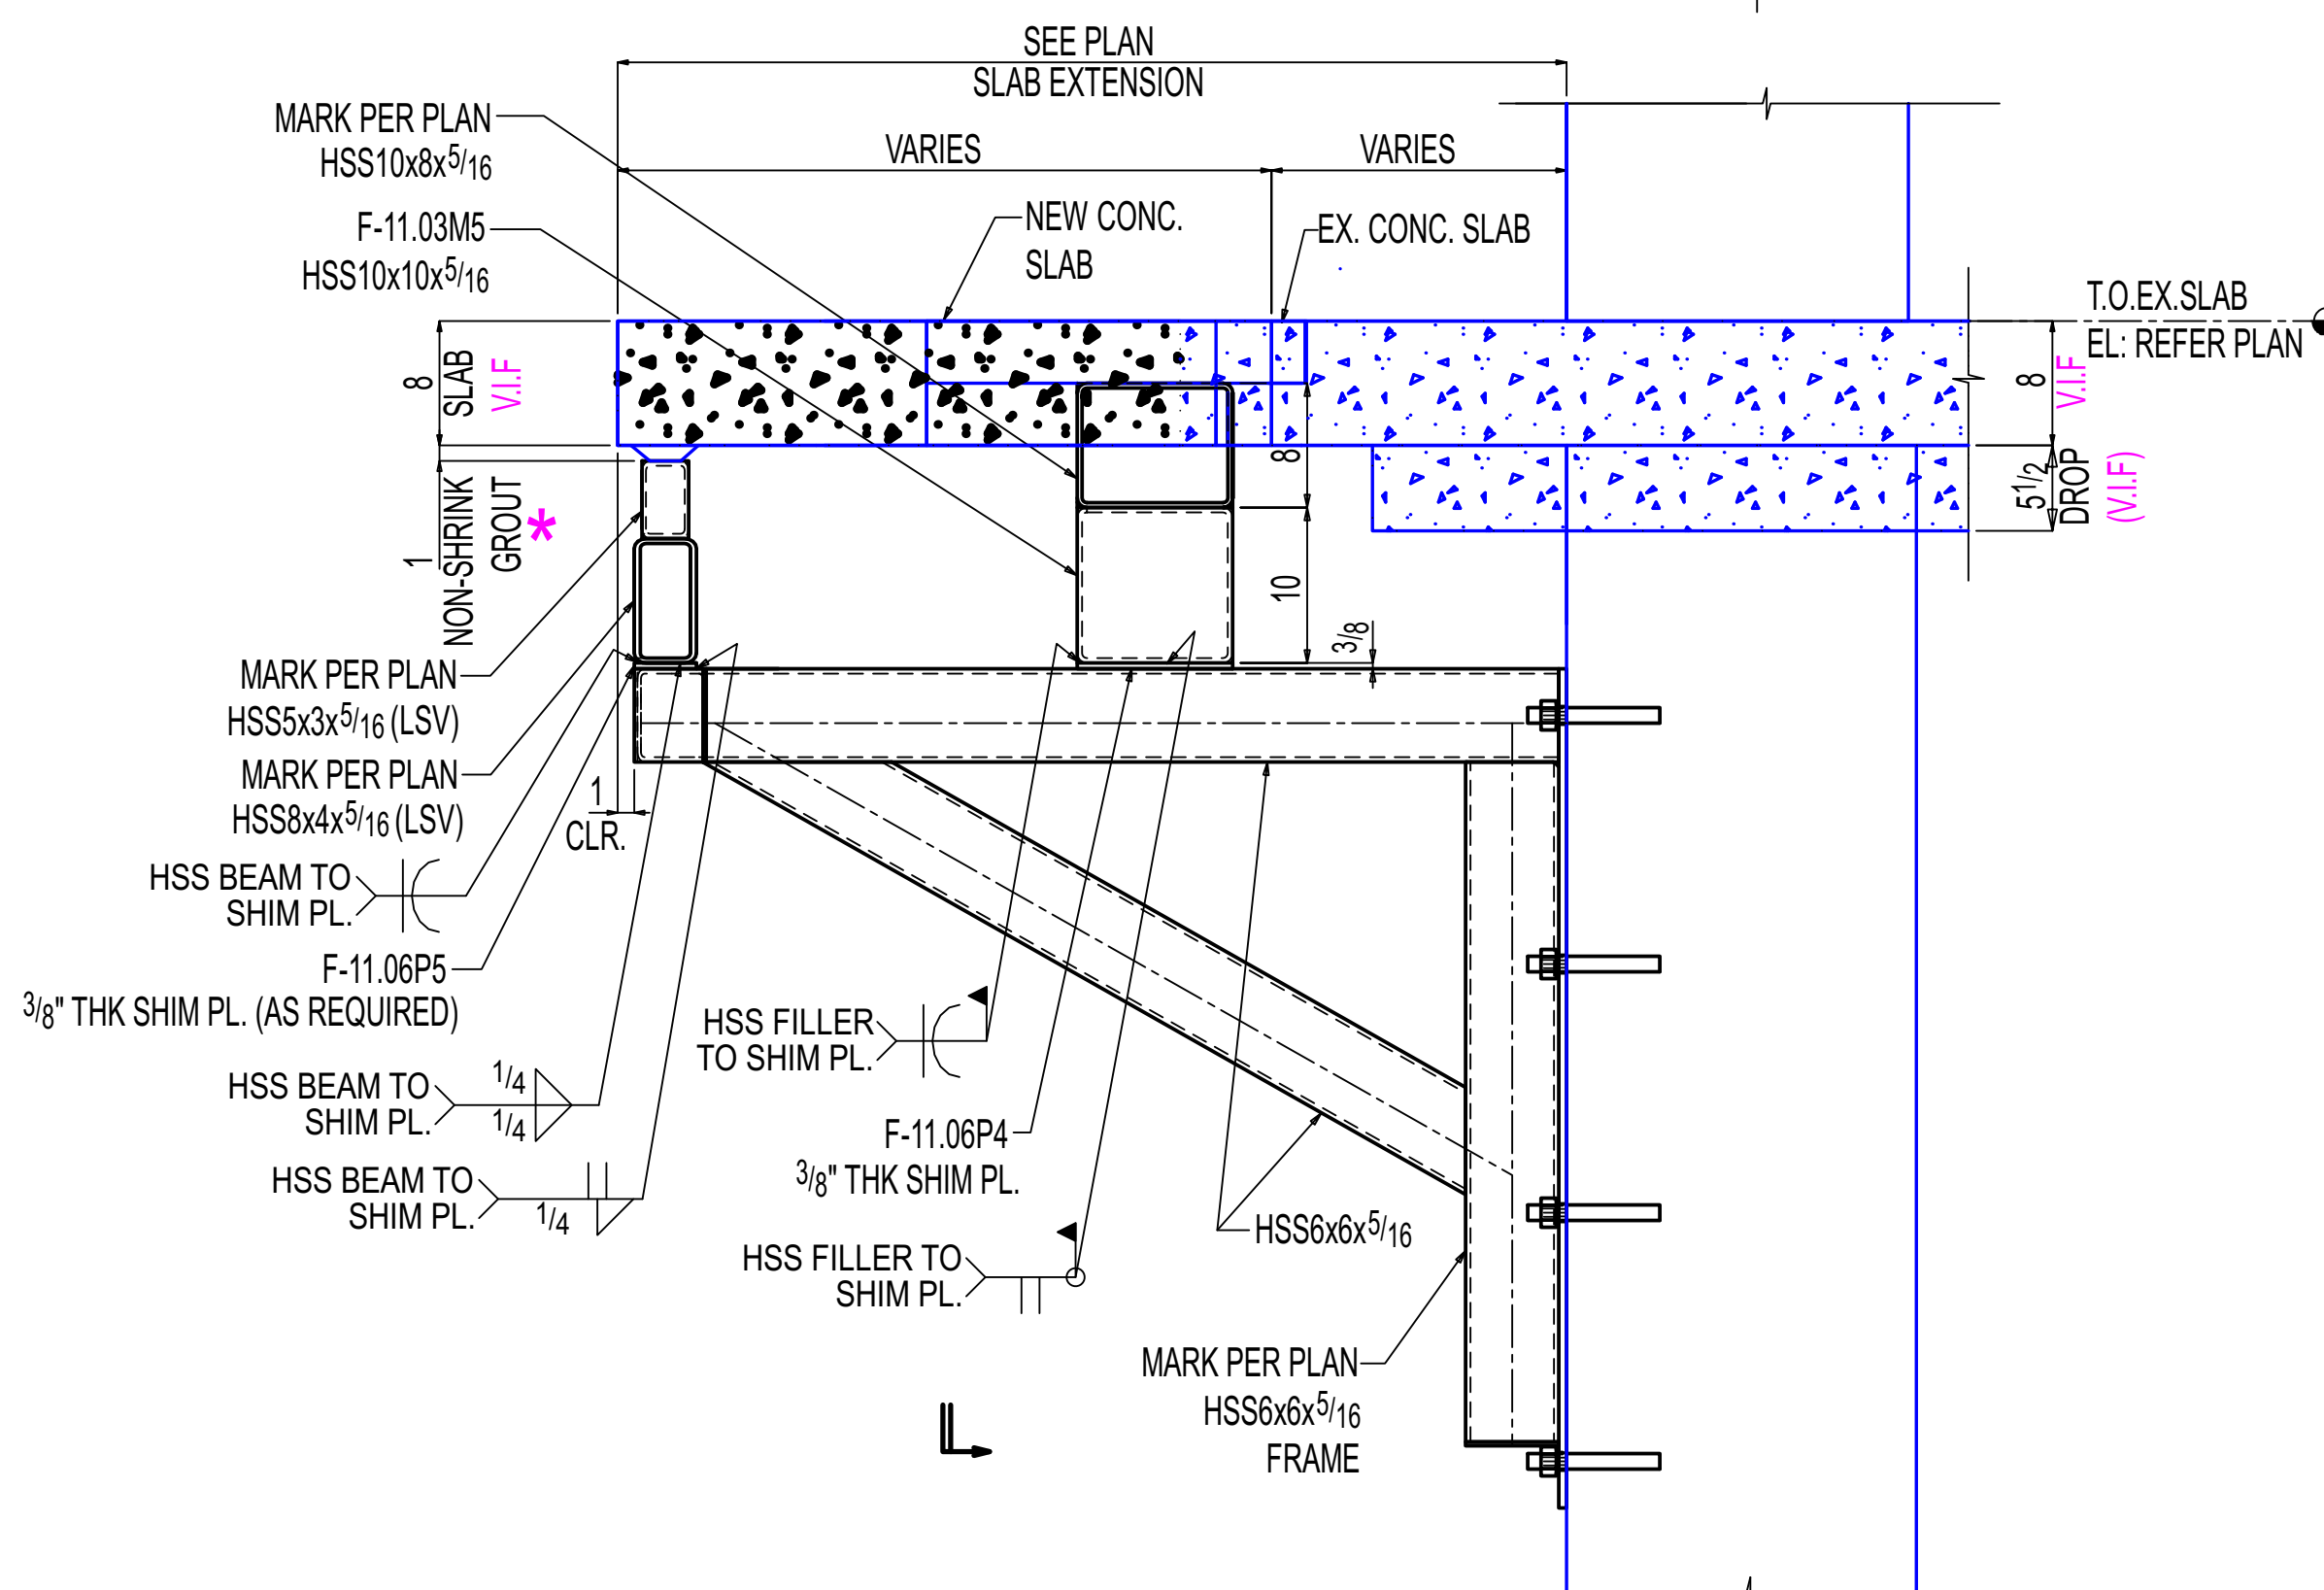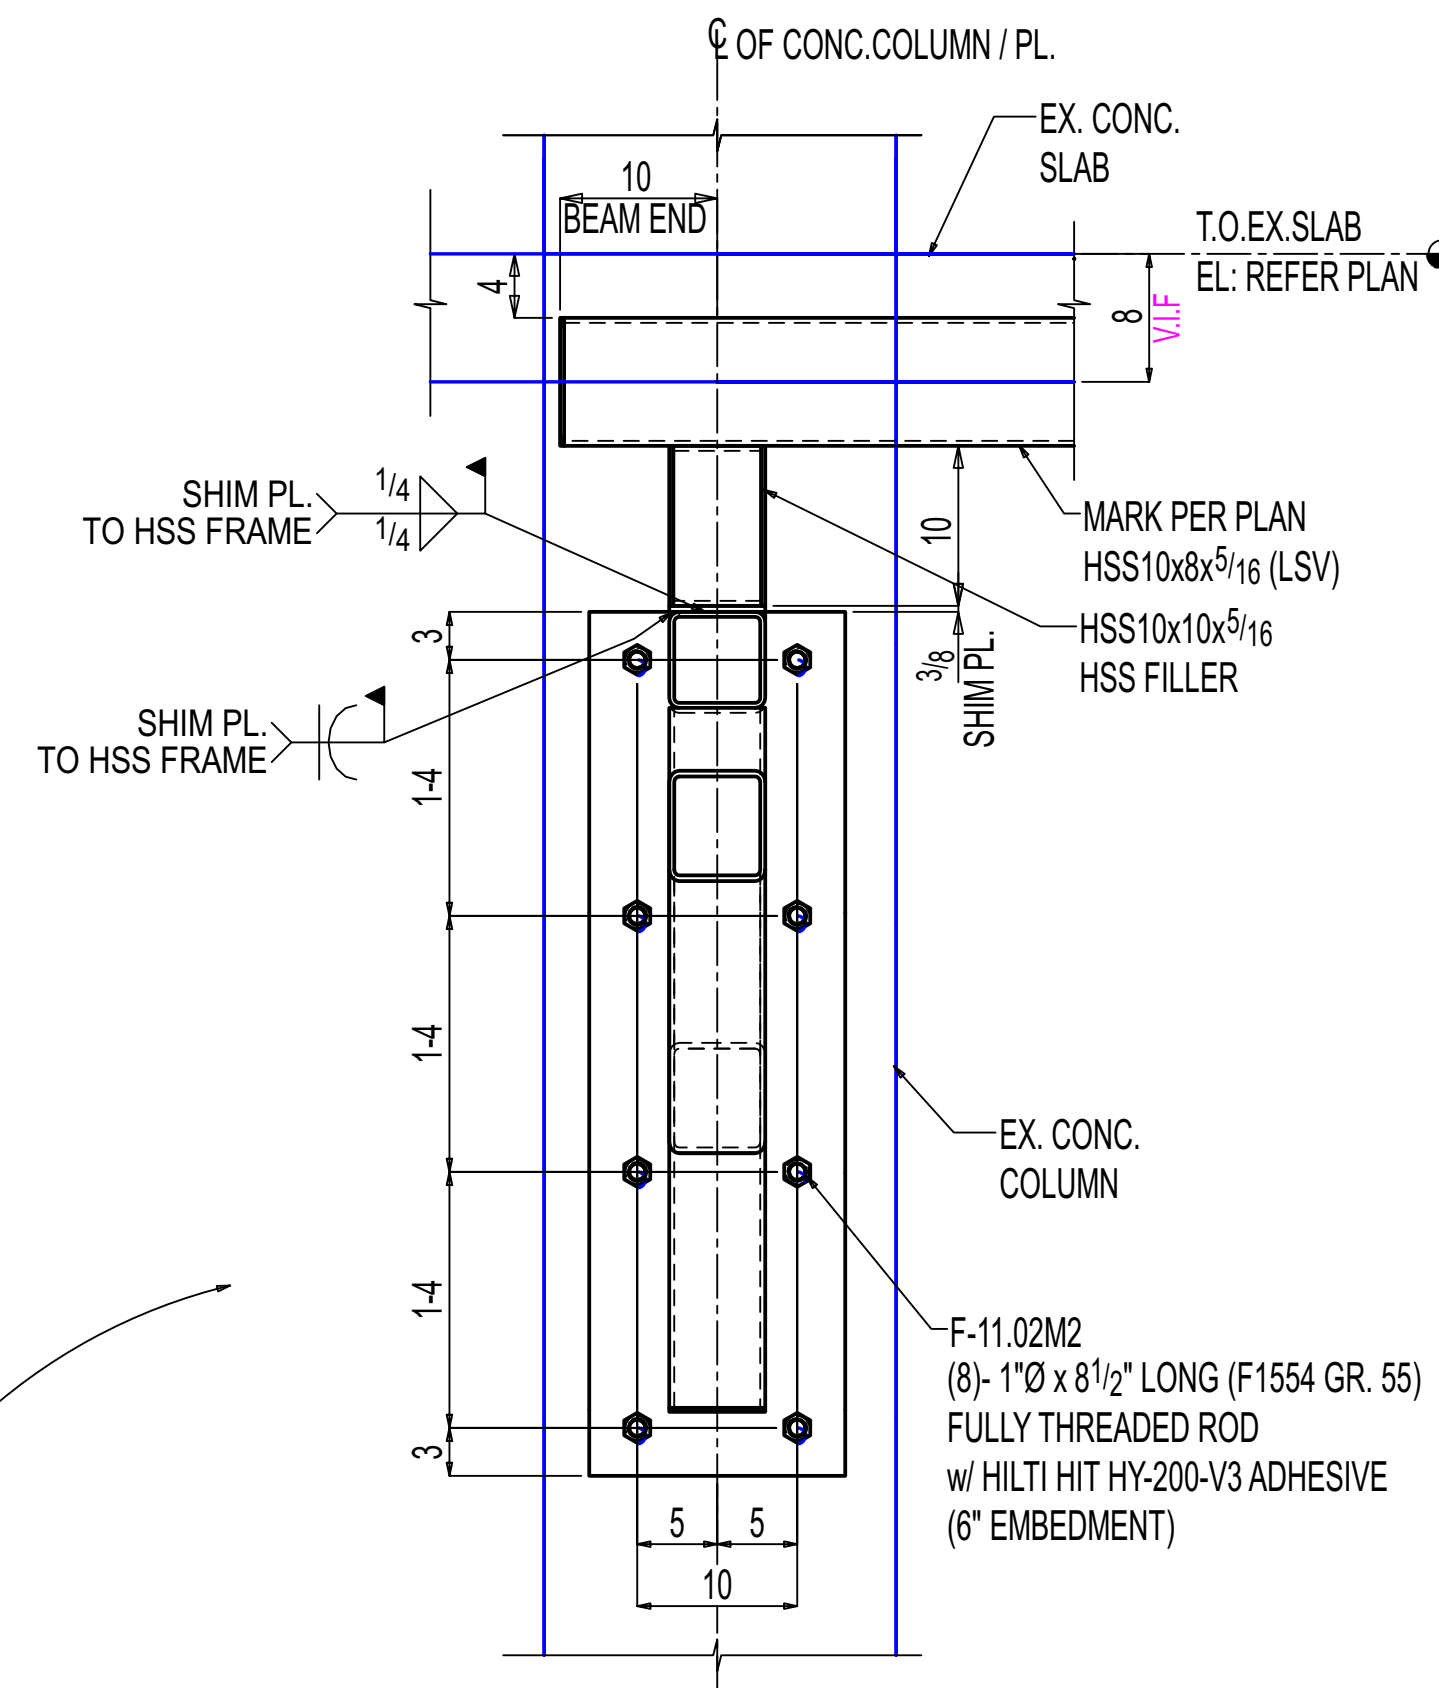

J-J

E-11.00B & E-11.05
(REF:6/S316)

OTHERS NOT SHOWN FOR CLARTY

SHOP / ERECTOR NOTE:
LOCATE EXISTING REBAR PRIOR TO FABRICATION OF PLATE. DO NOT DRILL THROUGH REBAR.

ERECTOR NOTE-1:
ADJUST HSS FILLER DEPTH IN FIELD BY CUT THE HSS FILLER TO MATCH EXISTING SLAB DROP THICKNESS, AND WELD TO THE TOP OF HSS FRAME AT SITE PRIOR TO ERECTING THE HSS FRAME.

General Notes

- *Structural steel shall conform to ASTM-A992.
- *Structural SQR/RND.tubing conform to ASTM A500 Grade C
- *Pipe shall conform to ASTM A53, Grade B.
- *Channels, Angles and plates shall conform to A36.
- *All bolts shall be 3/4" High strength in accordance with ASTM A325 (UNO)
- *Welding Electrodes for Carbon steel :E70xx

# of Copies	Revision/ Issue	Destination	Date
4	0	For Construction	11-14-2025
3	C	For Re-Approval	10-24-2025
2	B	For Re-Approval	09-19-2025
1	A	For Approval	06-23-2025

IRON FABRICATION SERVICES, LLC.

3029 M. Street, NW, Suite 202
Washington, DC 20007
Tel: 202-800-5599
Fax: 202-478-0303

Project Name and Address

MARYLAND AVENUE
Location: **1250 MARYLAND AVENUE SW WASHINGTON, DC 20024**

Contractor:

BALFOUR BEATTY

Approved for Fabrication by:	Signature
------------------------------	-----------

Contract #	224009	Drawing #	E-11.03
------------	---------------	-----------	----------------

Contract Item: **LEVEL-05 SLAB EXTENSION**

Ref: **SOW-11: 3,4,5&6 / S307**

Date	01/20/2025	Drawing Title:	SOW #11 LEVEL-05 NEW SLAB EXTENSION SUPPORT SECTIONS
Scale	VARIES		