


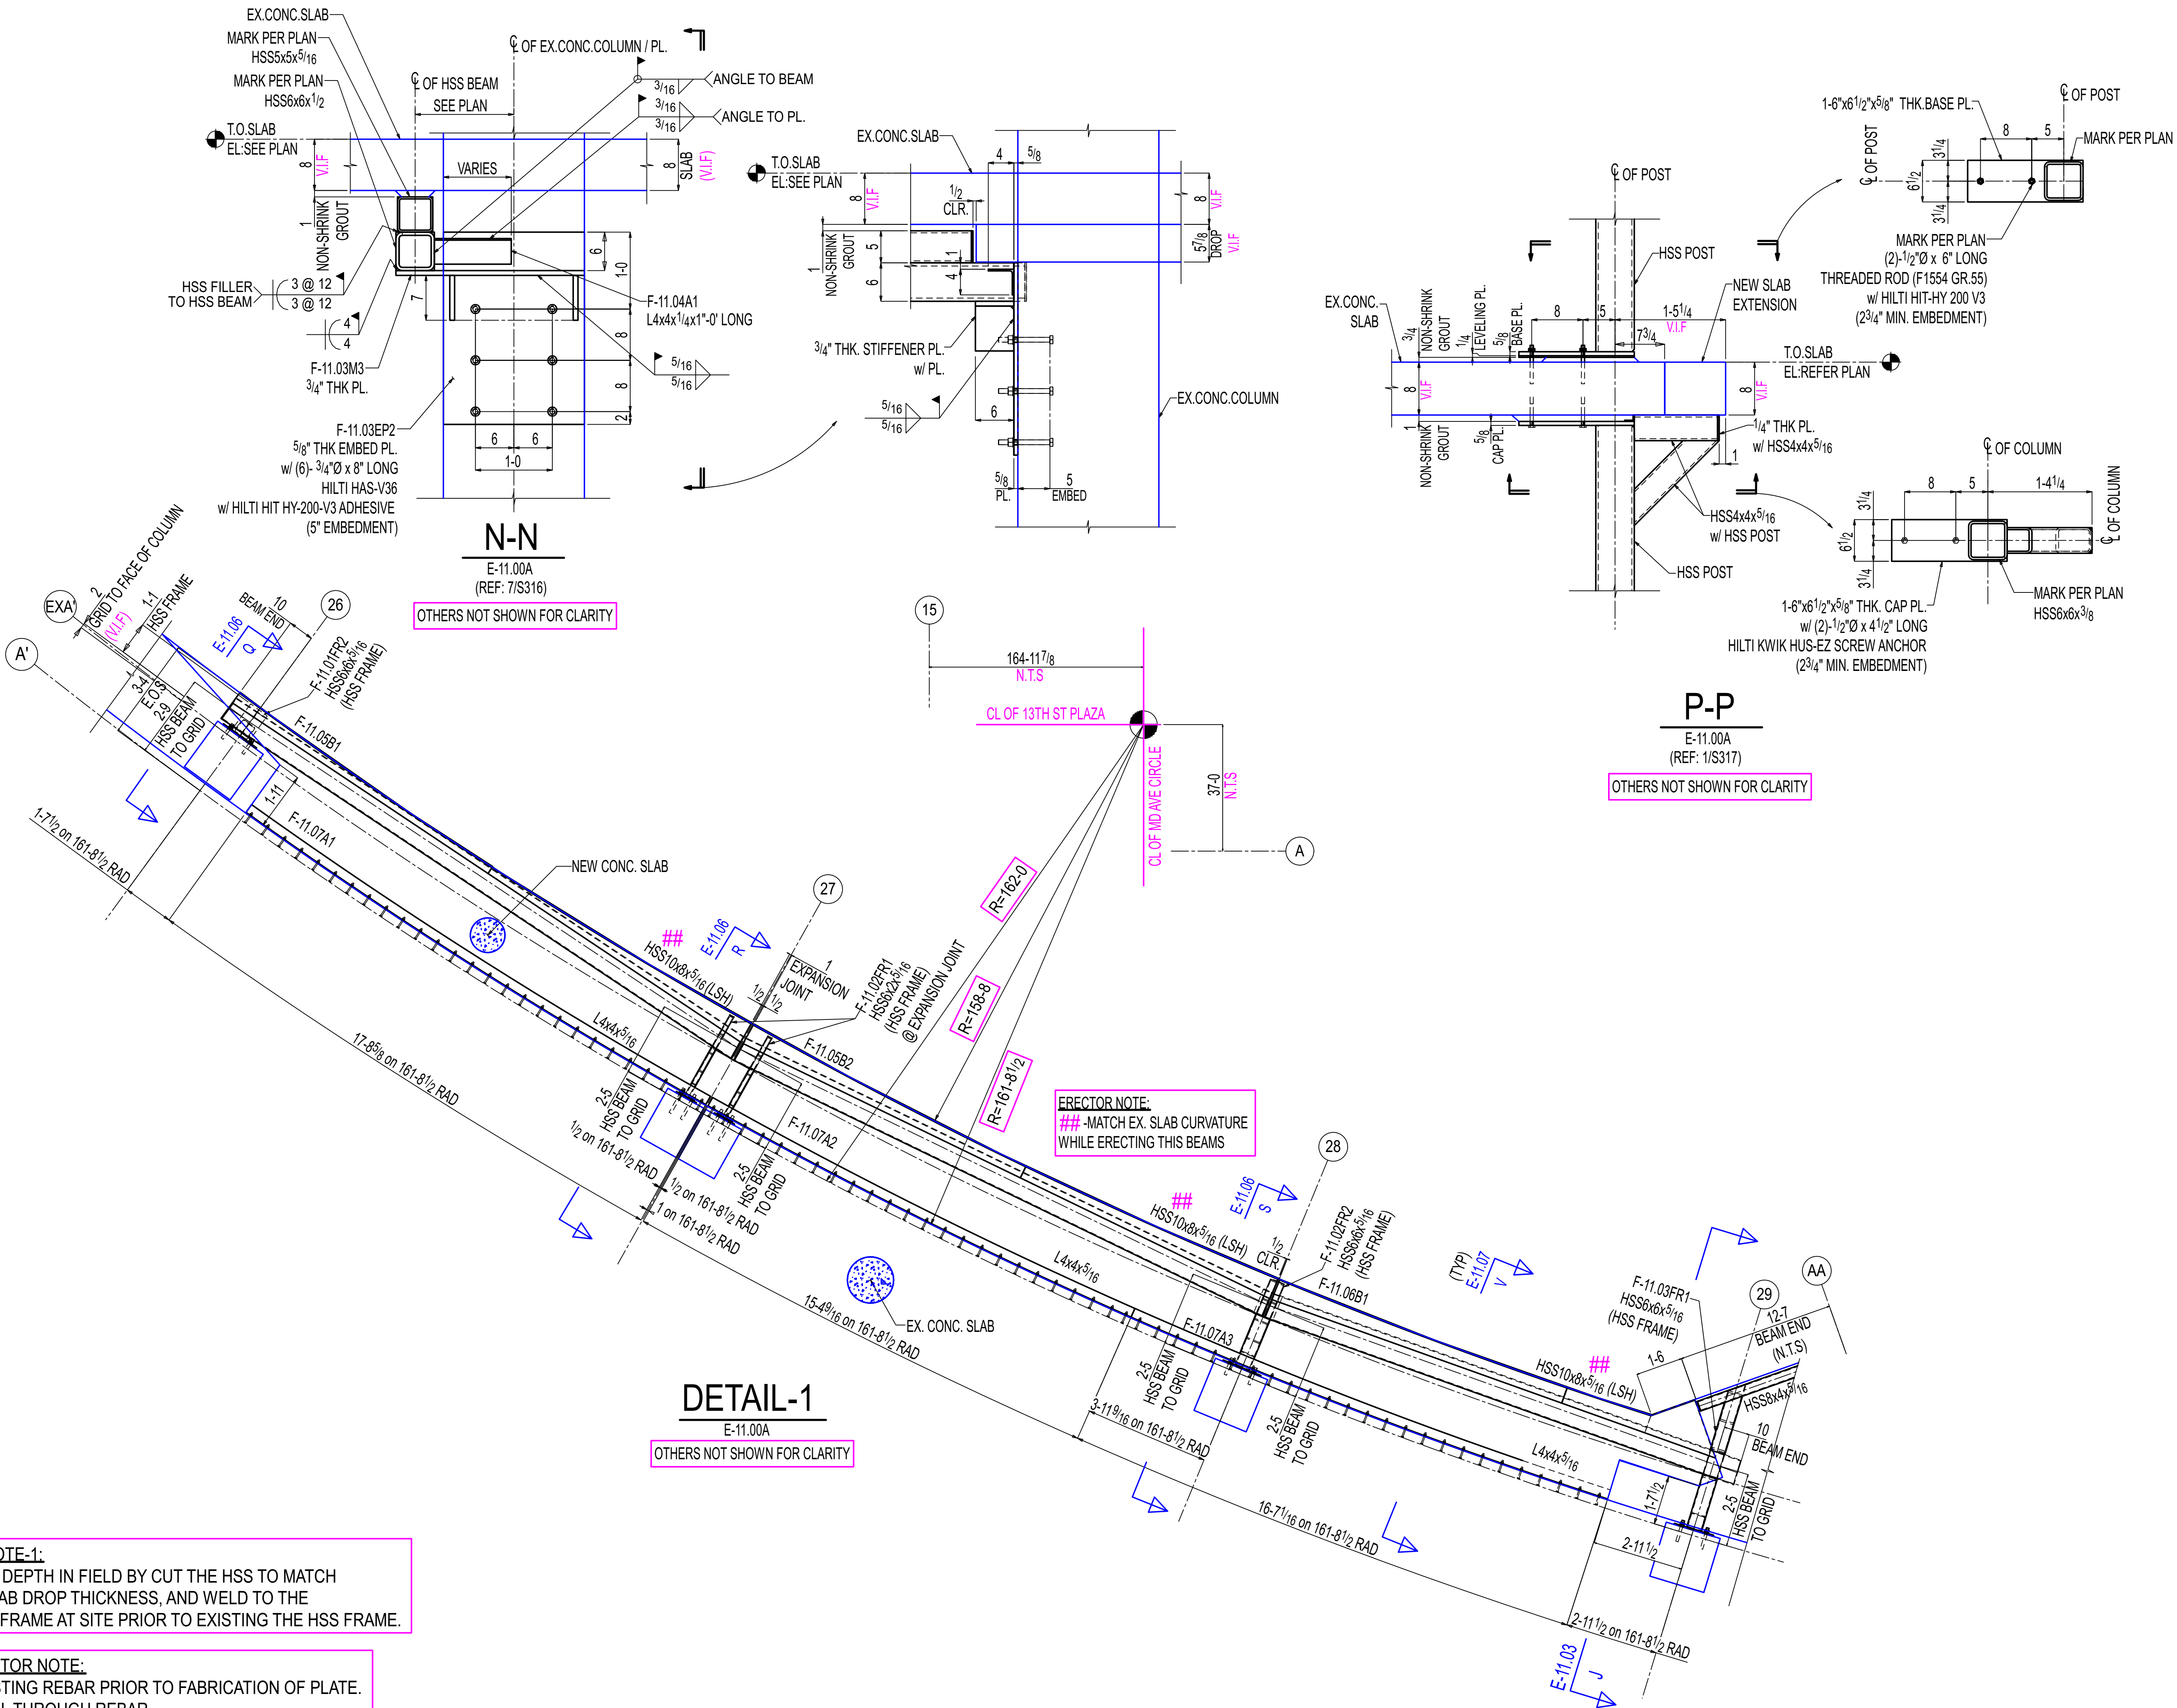

General Notes

- *Structural steel shall conform to ASTM-A992.
- *Structural SQR/RND tubing conform to ASTM A500 Grade C
- *Pipe shall conform to ASTM A53, Grade B.
- *Channels, Angles and plates shall conform to A36.
- *All bolts shall be 3/4" High strength in accordance with ASTM A325 (UNO)
- *Welding Electrodes for Carbon steel :E70xx

# of Copies	Revision/ Issue	Destination	Date
3	0	For Construction	11-14-2025
2	B	For Re-Approval	10-24-2025
1	A	For Approval	09-19-2025

IRON FABRICATION SERVICES, LLC.

3029 M. Street, NW, Suite 202
Washington, DC 20007
Tel: 202-800-5599
Fax: 202-478-0303

Project Name and Address
MARYLAND AVENUE

Location: **1250 MARYLAND AVENUE SW
WASHINGTON, DC 20024**

Contractor:
BALFOUR BEATTY

Approved for Fabrication by:	Signature
------------------------------	-----------

Contract # 224009	Drawing # E-11.05
Contract Item: LEVEL-05 SLAB EXTENSION	
Ref: SOW-11: 3,4,5&6 / S307	
Date 01/20/2025	Drawing Title: SOW #11 LEVEL-05 NEW SLAB EXTENSION SUPPORT SECTIONS
Scale VARIES	