


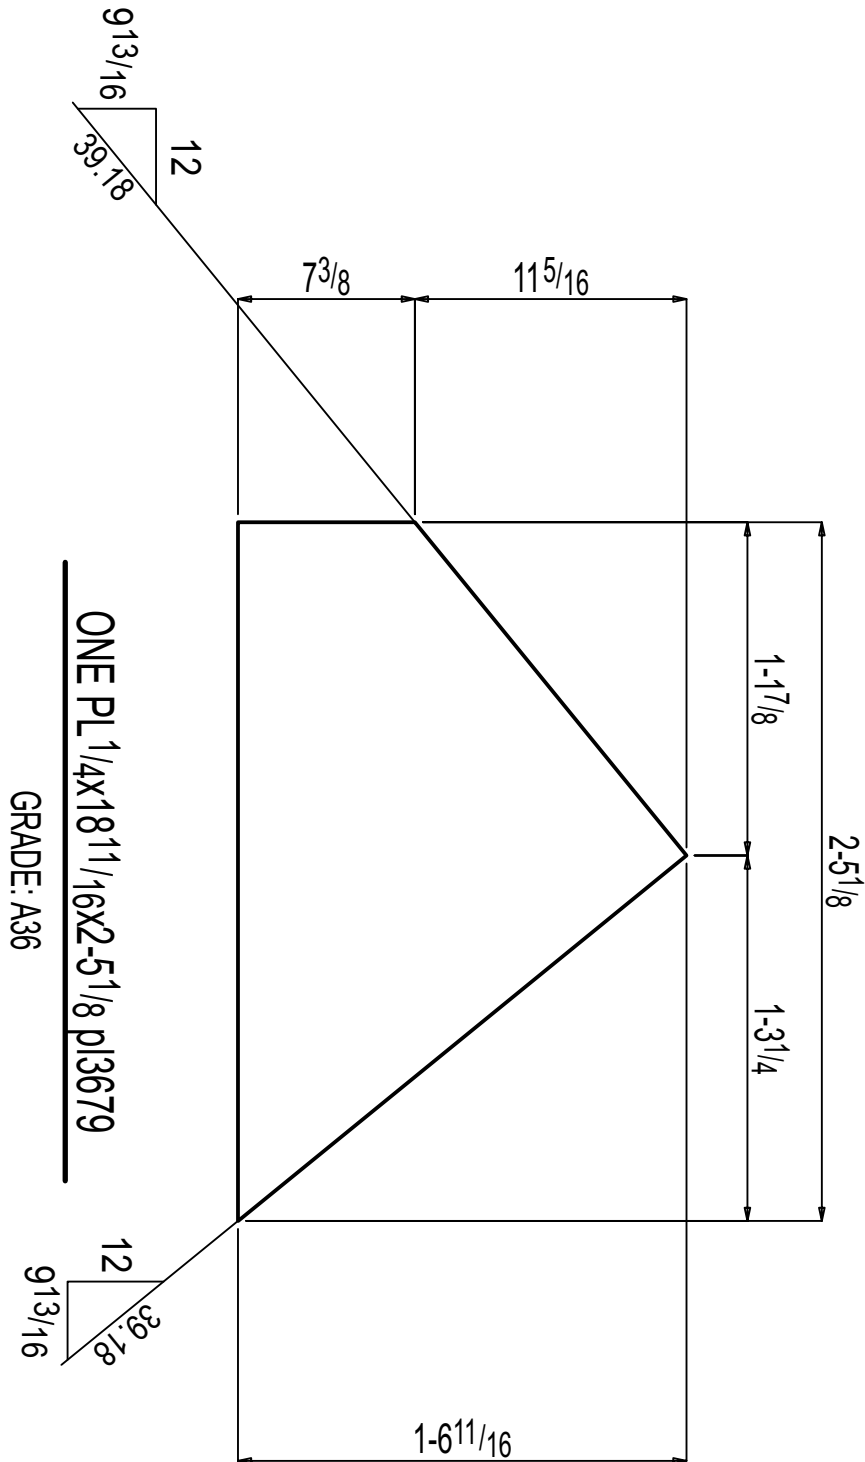

General Notes

*Structural steel shall conform to ASTM-A992.
 *Structural SQR/RND.tubing conform to ASTM A500 Grade C
 *Pipe shall conform to ASTM A53, Grade B.
 *Channels, Angles and plates shall conform to A36.
 *All bolts shall be $\frac{3}{4}$ " High strength in accordance with ASTM A325 (UNO)
 *Welding Electrodes for Carbon steel :E70xx
 *Structural members are to be shop primer (U.N.O).
 *Surface Preparation-SSPC-SP3 UNO.
 *If welds exposed to view, should be ground smooth.

# of Copies	Revision/ Issue	Destination	Date
1	0	FOR FABRICATION	11-14-2025

IRON FABRICATION SERVICES, LLC.

3029 M. Street, NW, Suite 202
 Washington, DC 20007
 Tel: 202-800-5599
 Fax: 202-478-0303

Project Name and Address

MARYLAND AVENUE

Location: **1250 MARYLAND AVENUE SW
 WASHINGTON, DC 20024**

Contractor:

BALFOUR BEATTY

Approved for Fabrication by:

Signature

Contract # **224009**

Drawing # **p13679**

Contract Item: **PLATE**

Ref:

SOW -11:F-11.00-F-11.07

Date
01/23/2025

Drawing Title:
PLATE

Scale
VARIES

HOLE: $1\frac{3}{16}$ Ø (U.N.O)