


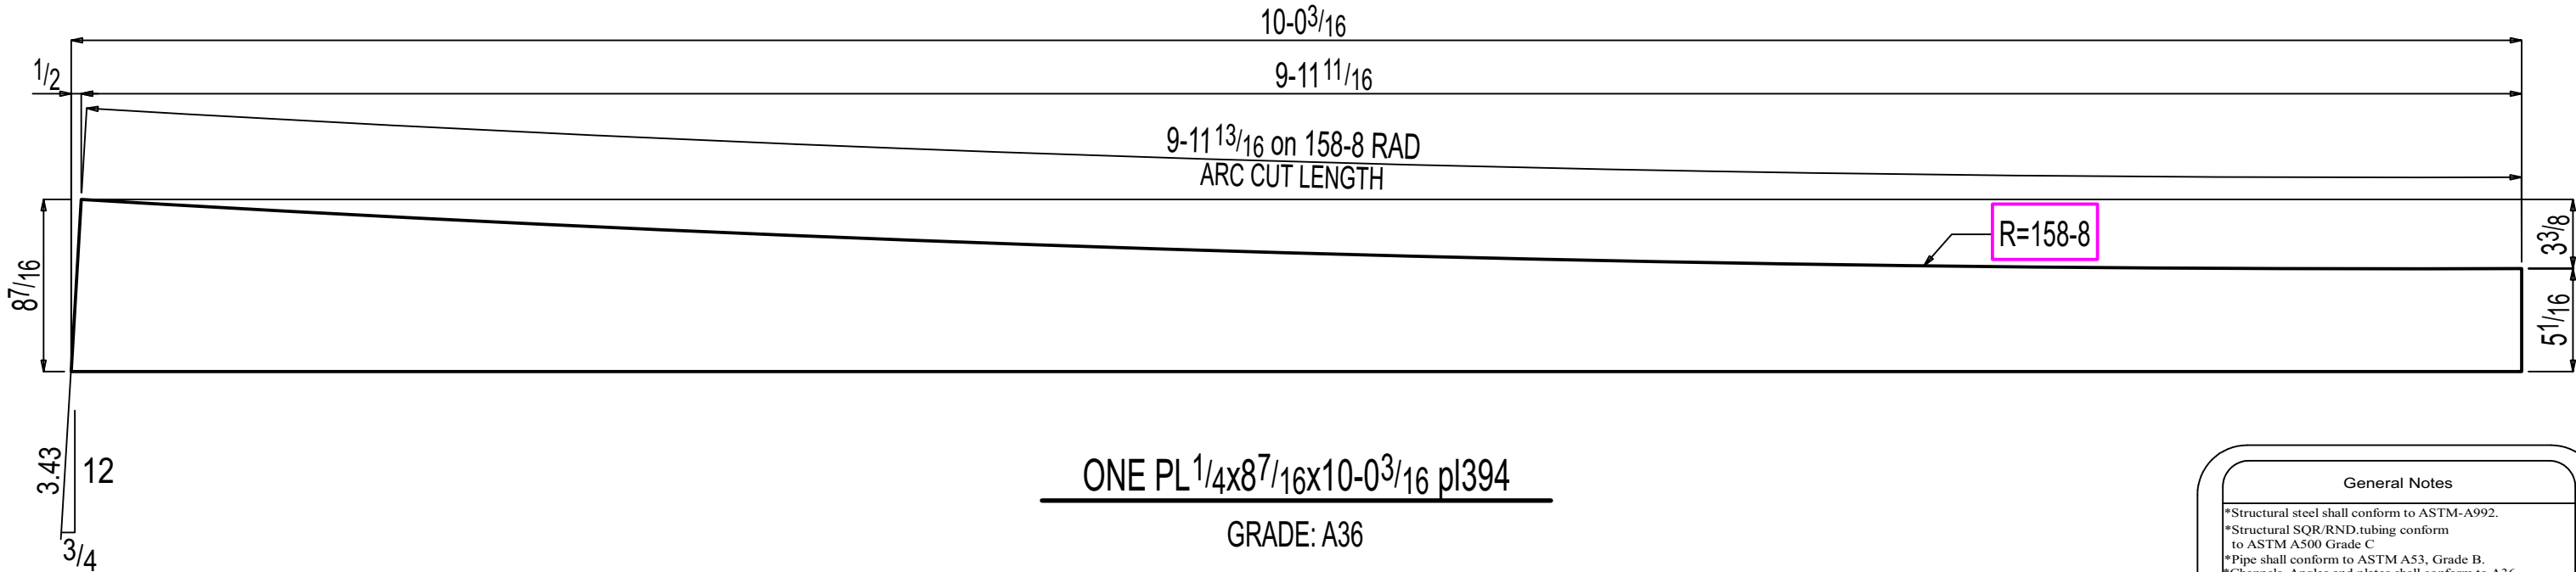

General Notes

- *Structural steel shall conform to ASTM-A992.
- *Structural SQR/RND.tubing conform to ASTM A500 Grade C
- *Pipe shall conform to ASTM A53, Grade B.
- *Channels, Angles and plates shall conform to A36.
- *All bolts shall be ³/₄" High strength in accordance with ASTM A325 (UNO)
- *Welding Electrodes for Carbon steel :E70xx
- *Structural members are to be shop primer (U.N.O).
- *Surface Preparation-SSPC-SP3 UNO.
- *If welds exposed to view, should be ground smooth.

1	0	FOR FABRICATION	11-14-2025
# of Copies	Revision/ Issue	Destination	Date

IRON FABRICATION SERVICES, LLC.

3029 M. Street, NW, Suite 202
Washington, DC 20007
Tel: 202-800-5599
Fax: 202-478-0303

Project Name and Address

MARYLAND AVENUE

Location: 1250 MARYLAND AVENUE SW
WASHINGTON, DC 20024

Contractor:

BALFOUR BEATTY

Approved for Fabrication by:	Signature

Contract #	224009	Drawing #	pl394
Contract Item: PLATE			
Ref: SOW -11:F-11.00-F-11.07			
Date 01/ 23/ 2025	Drawing Title: PLATE		
Scale VARIES			

HOLE:1³/₁₆ Ø (U.N.O)