



| BILL OF MATERIAL |           |                                                                 |             |                                     |                                             |        |         |  |  |
|------------------|-----------|-----------------------------------------------------------------|-------------|-------------------------------------|---------------------------------------------|--------|---------|--|--|
| LINE #           | QTY       | PC MARK                                                         | DESCRIPTION | LENGTH                              | REMARKS                                     | WEIGHT | ADVANCE |  |  |
|                  | TOTAL     |                                                                 |             |                                     |                                             | TOTAL  | MILL #  |  |  |
| ONE              | F-13.03B1 | BEAM                                                            |             |                                     |                                             | 919    |         |  |  |
| 1                | F-13.03B1 | HSS10x8x <sup>5</sup> / <sub>16</sub>                           |             | 19 10 <sup>13</sup> / <sub>16</sub> | A500C                                       | 718    |         |  |  |
| 2                | p13649    | PL <sup>1</sup> / <sub>4</sub> x8                               |             | 0 10                                | A36                                         | 11     |         |  |  |
| 1                | p1368     | PL <sup>1</sup> / <sub>4</sub> x7 <sup>13</sup> / <sub>16</sub> |             | 9 11 <sup>1</sup> / <sub>4</sub>    | A36                                         | 66     |         |  |  |
| 1                | p13652    | PL <sup>1</sup> / <sub>4</sub> x7 <sup>1</sup> / <sub>8</sub>   |             | 9 11 <sup>1</sup> / <sub>4</sub>    | A36                                         | 60     |         |  |  |
| 1                | fb229     | FL <sup>1</sup> / <sub>4</sub> x3 <sup>3</sup> / <sub>4</sub>   |             | 9 10 <sup>7</sup> / <sub>8</sub>    | A36                                         | 32     |         |  |  |
| 1                | fb230     | FL <sup>1</sup> / <sub>4</sub> x3 <sup>3</sup> / <sub>4</sub>   |             | 9 10 <sup>7</sup> / <sub>8</sub>    | A36                                         | 32     |         |  |  |
| ONE              | F-13.03B2 | BEAM                                                            |             |                                     |                                             | 969    |         |  |  |
| 1                | F-13.03B2 | HSS8x6x <sup>1</sup> / <sub>2</sub>                             |             | 22 10 <sup>1</sup> / <sub>2</sub>   | A500C                                       | 962    |         |  |  |
| 2                | p1476     | PL <sup>1</sup> / <sub>4</sub> x6                               |             | 0 8                                 | A36                                         | 7      |         |  |  |
| ONE              | F-13.03B3 | BEAM                                                            |             |                                     |                                             | 495    |         |  |  |
| 1                | F-13.03B3 | HSS6x6x <sup>1</sup> / <sub>2</sub>                             |             | 13 10 <sup>7</sup> / <sub>8</sub>   | A500C                                       | 490    |         |  |  |
| 2                | p1704     | PL <sup>1</sup> / <sub>4</sub> x6                               |             | 0 6                                 | A36                                         | 5      |         |  |  |
| ONE              | F-13.03M1 | HSS                                                             |             |                                     |                                             | 110    |         |  |  |
| 1                | F-13.03M1 | HSS6x6x <sup>3</sup> / <sub>16</sub>                            |             | 4 7 <sup>1</sup> / <sub>2</sub>     | A500C                                       | 108    |         |  |  |
| 1                | p1704     | PL <sup>1</sup> / <sub>4</sub> x6                               |             | 0 6                                 | A36                                         | 3      |         |  |  |
| ONE              | F-13.03M2 | HSS                                                             |             |                                     |                                             | 117    |         |  |  |
| 1                | F-13.03M2 | HSS6x6x <sup>3</sup> / <sub>16</sub>                            |             | 5 0                                 | A500C                                       | 117    |         |  |  |
| 2                | F-13.03M3 | HSS                                                             |             |                                     |                                             | 200    |         |  |  |
| 2                | F-13.03M3 | HSS6x6x <sup>3</sup> / <sub>16</sub>                            |             | 4 3 <sup>1</sup> / <sub>2</sub>     | A500C                                       | 200    |         |  |  |
| 2                | F-13.03M4 | HSS                                                             |             |                                     |                                             | 180    |         |  |  |
| 2                | F-13.03M4 | HSS6x6x <sup>3</sup> / <sub>16</sub>                            |             | 3 9                                 | A500C                                       | 175    |         |  |  |
| 2                | p1704     | PL <sup>1</sup> / <sub>4</sub> x6                               |             | 0 6                                 | A36                                         | 5      |         |  |  |
| ONE              | F-13.03A1 | ANGLE                                                           |             |                                     |                                             | 7      |         |  |  |
| 1                | F-13.03A1 | L4x4x <sup>1</sup> / <sub>4</sub>                               |             | 1 0                                 | A36                                         | 7      |         |  |  |
| ONE              | F-13.03P2 | PLATE                                                           |             |                                     |                                             | 55     |         |  |  |
| 1                | F-13.03P2 | PL <sup>1</sup> / <sub>4</sub> x7                               |             | 1 10                                | A36                                         | 55     |         |  |  |
|                  |           | FIELD BOLTS                                                     |             |                                     |                                             |        |         |  |  |
| 2                |           | 3/4 Dia HILTI KWIK HUS-EZ                                       |             | 0 7                                 | (3 <sup>1</sup> / <sub>4</sub> " EMBEDMENT) |        |         |  |  |
|                  |           | SCREW ANCHOR                                                    |             |                                     |                                             |        |         |  |  |


Total weight : 3052

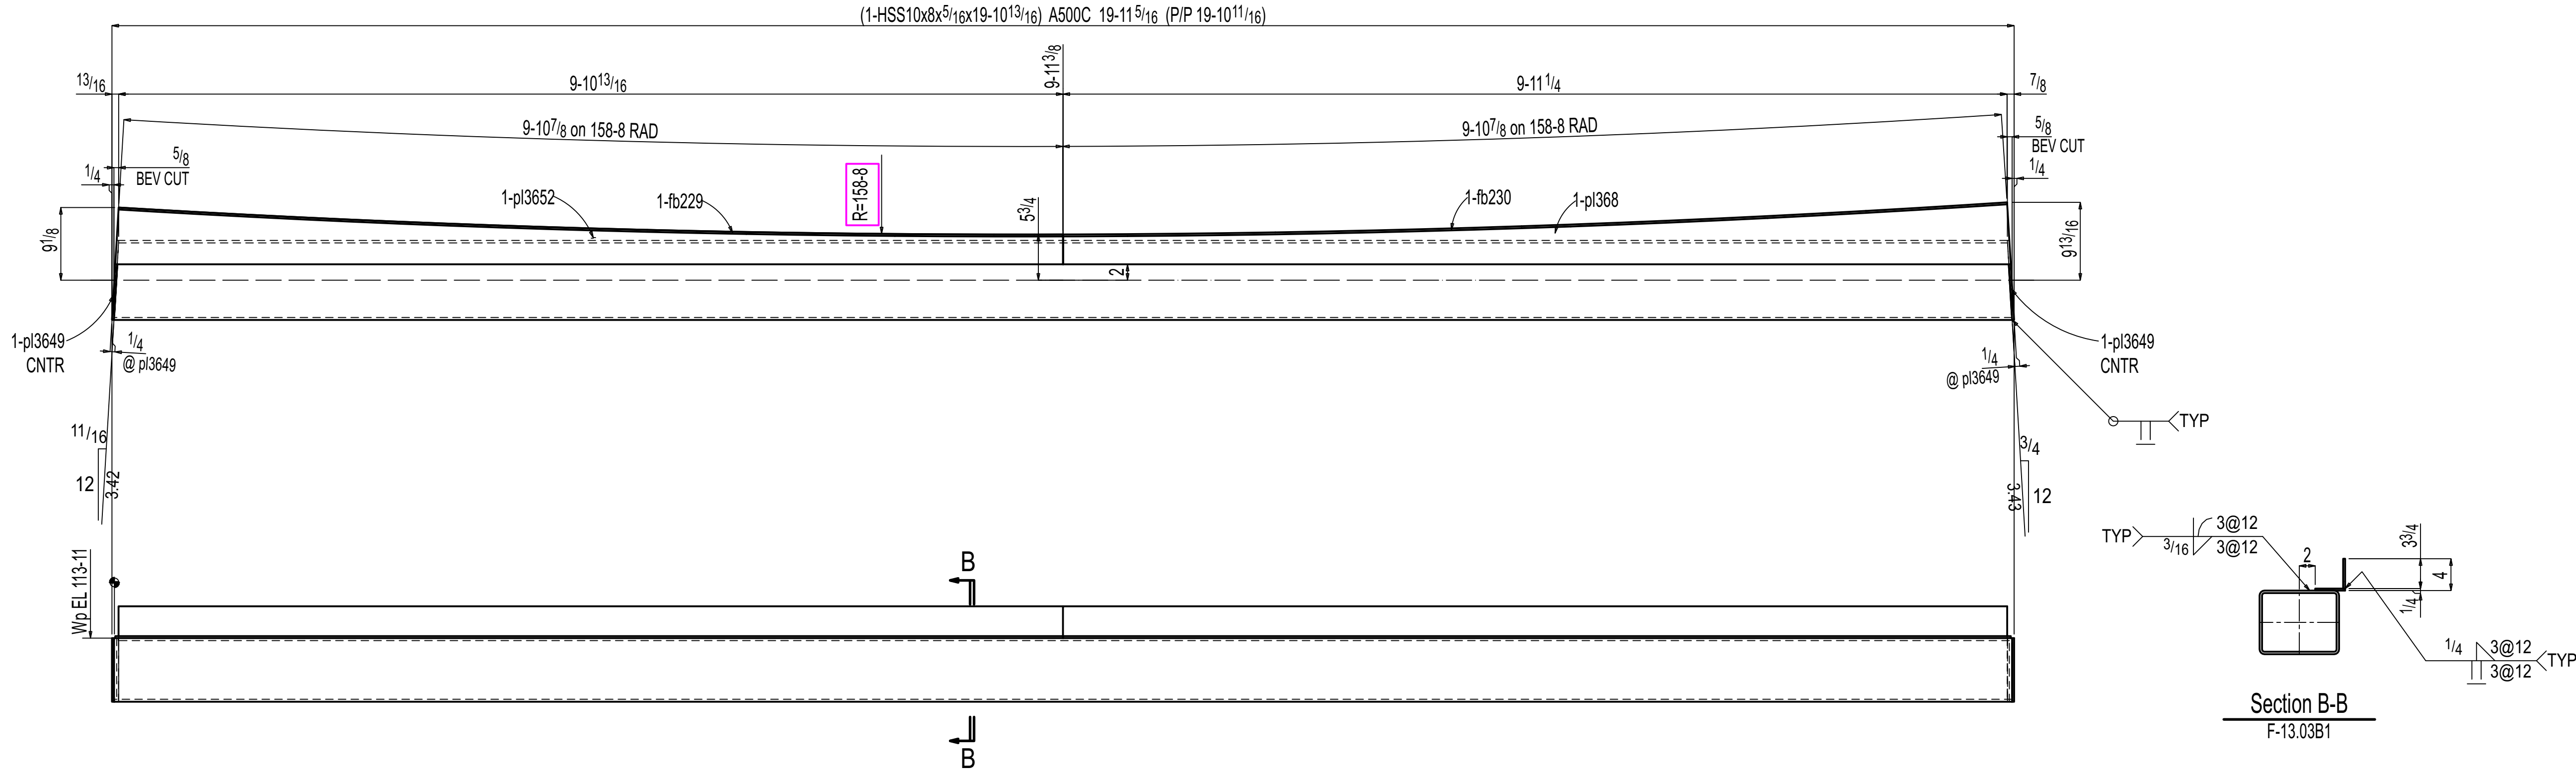


ONE BEAM F-13.03B1

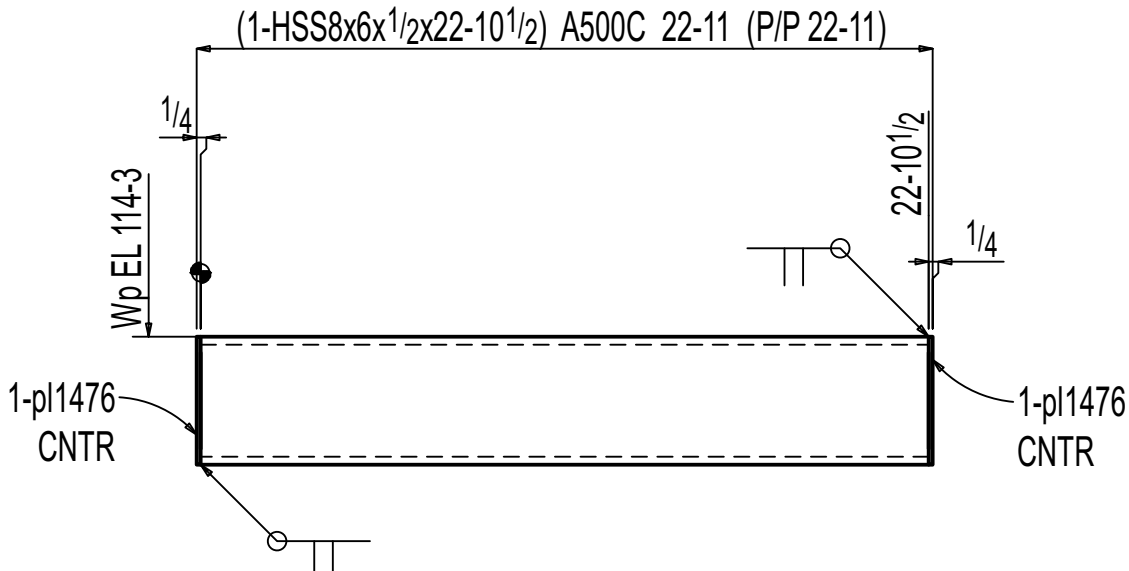


ONE BEAM F-13.03B2

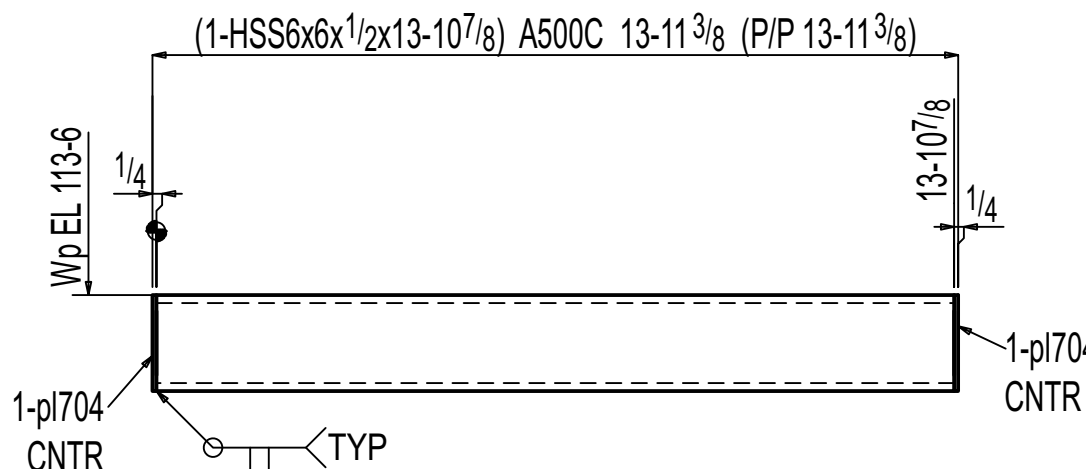


ONE BEAM F-13.03B3

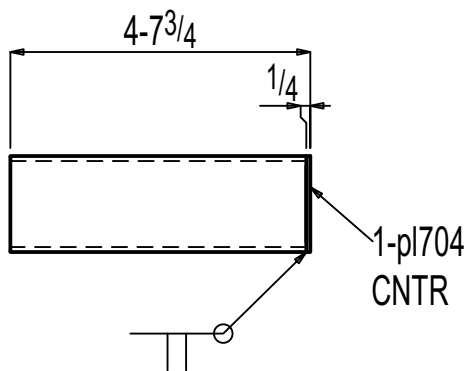


ONE HSS F-13.03M1

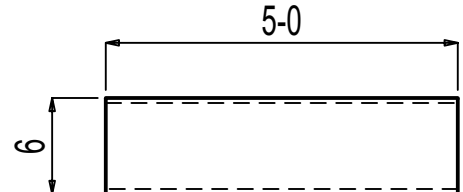


ONE HSS F-13.03M2

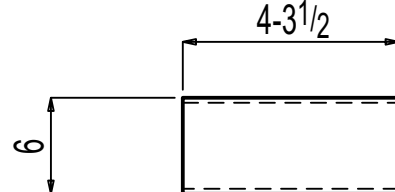


2 HSS F-13.03M3

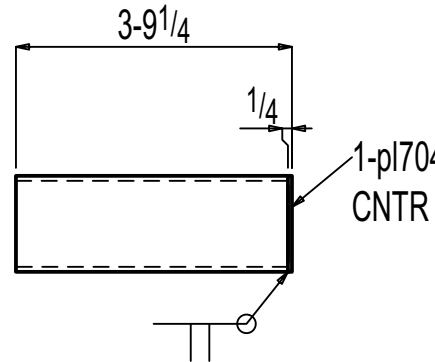

2 HSS F-13.03M4

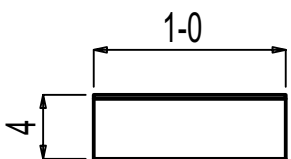

ONE ANGLE F-13.03A1

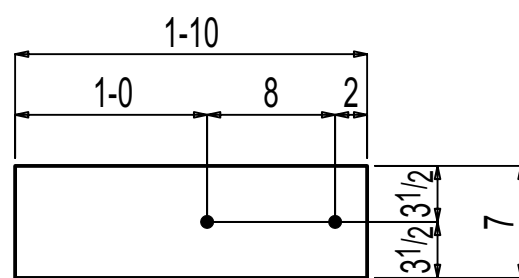

ONE PLATE F-13.03P2

PAINT PREPARATION :NO PAINT :SSPC-SP3

| General Notes                                                             |                 |                 |            |
|---------------------------------------------------------------------------|-----------------|-----------------|------------|
| *Structural steel shall conform to ASTM-A992.                             |                 |                 |            |
| *Structural SQR/RND,tubing conform to ASTM A500 Grade C                   |                 |                 |            |
| *Pipe shall conform to ASTM A53, Grade B.                                 |                 |                 |            |
| *Channels, Angles and plates shall conform to A36.                        |                 |                 |            |
| *All bolts shall be 3/4" High strength in accordance with ASTM A325 (UNO) |                 |                 |            |
| *Welding Electrodes for Carbon steel :E70xx                               |                 |                 |            |
| 5                                                                         | 0               | For Fabrication | 11-17-2025 |
| 4                                                                         | D               | For Re-Approval | 10-24-2025 |
| 3                                                                         | C               | For Re-Approval | 09-19-2025 |
| 2                                                                         | B               | For Re-Approval | 06-23-2025 |
| 1                                                                         | A               | For Approval    | 02-11-2025 |
| # of Copies                                                               | Revision/ Issue | Destination     | Date       |

IRON FABRICATION SERVICES, LLC.

3029 M. Street, NW, Suite 202  
Washington, DC 20007  
Tel: 202-800-5599  
Fax: 202-478-0303

Project Name and Address  
**MARYLAND AVENUE**  
Location: **1250 MARYLAND AVENUE SW WASHINGTON, DC 20024**

Contractor:  
**BALFOUR BEATTY**

Approved for Fabrication by: Signature

Contract # **224009** Drawing # **F-13.03**  
Contract Item: **FRAME**  
Ref:  
**SOW - 13: E-13.00 - E-13.02**

Date **01/ 23/ 2025** Drawing Title:  
Scale **VARIES** **BEAM & MISCELLANEOUS DETAIL**