
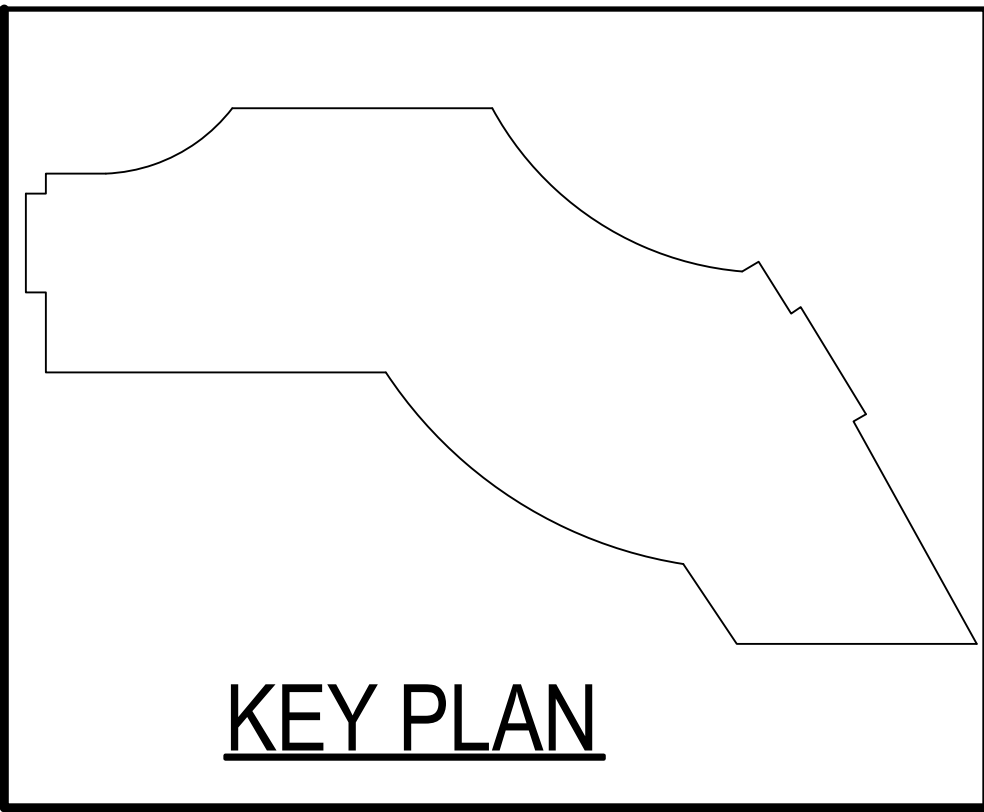


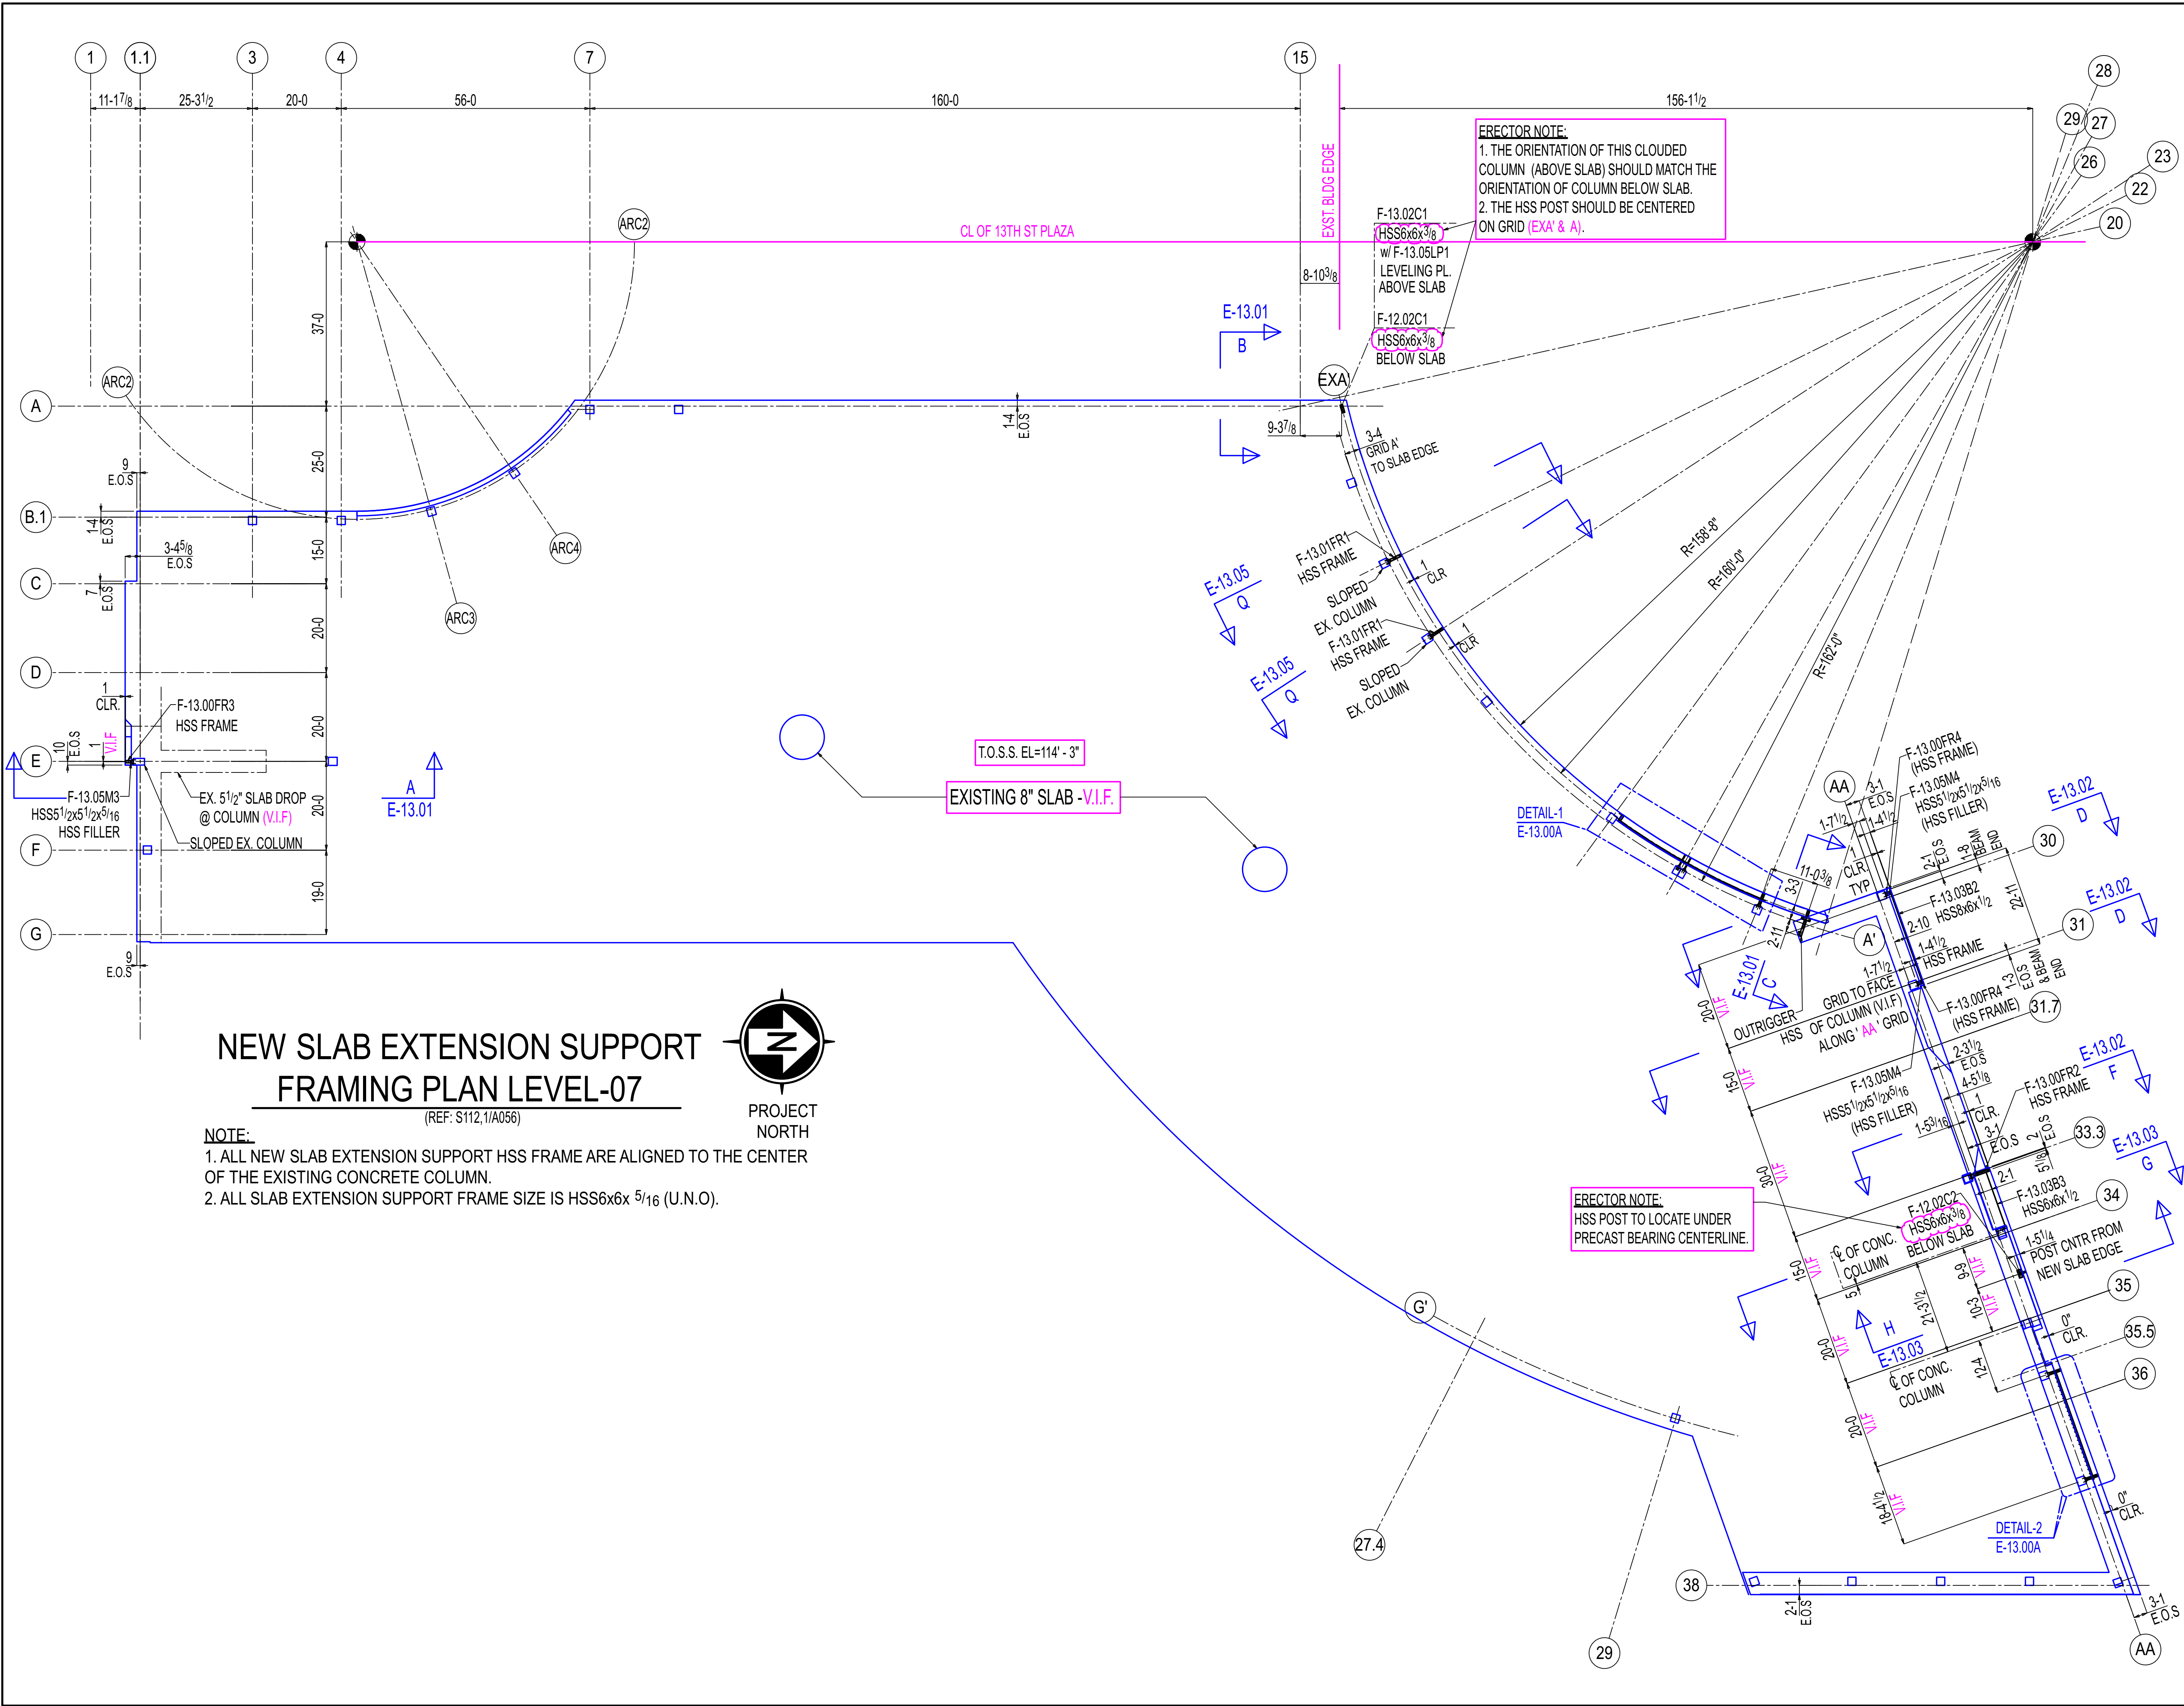


NEW SLAB EXTENSION SUPPORT FRAMING PLAN LEVEL-07

(REF: S112,1/A056)

NOTE:

1. ALL NEW SLAB EXTENSION SUPPORT HSS FRAME ARE ALIGNED TO THE CENTER OF THE EXISTING CONCRETE COLUMN.
2. ALL SLAB EXTENSION SUPPORT FRAME SIZE IS HSS6x6x 5/16 (U.N.O).

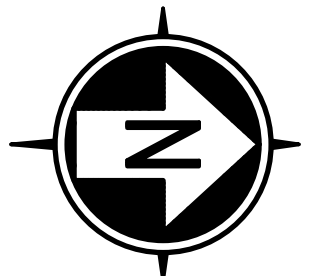

PROJECT
NORTH

General Notes

- *Structural steel shall conform to ASTM-A992.
- *Structural SQR/RND,tubing conform to ASTM A500 Grade C
- *Pipe shall conform to ASTM A53, Grade B.
- *Channels, Angles and plates shall conform to A36.
- *All bolts shall be 3/4" High strength in accordance with ASTM A325 (UNO)
- *Welding Electrodes for Carbon steel :E70xx

# of Copies	Revision/ Issue	Destination	Date
5	0	For Construction	11-17-2025
4	D	For Re-Approval	10-24-2025
3	C	For Re-Approval	09-19-2025
2	B	For Re-Approval	06-23-2025
1	A	For Approval	02-25-2025

IRON FABRICATION SERVICES, LLC.

3029 M. Street, NW, Suite 202
Washington, DC 20007
Tel: 202-800-5599
Fax: 202-478-0303

Project Name and Address
MARYLAND AVENUE

Location: **1250 MARYLAND AVENUE SW
WASHINGTON, DC 20024**

Contractor:
BALFOUR BEATTY

Approved for Fabrication by:	Signature

Contract # **224009** Drawing # **E-13.00**

Contract Item: **LEVEL-07
SLAB EXTENSION**

Ref: **SOW-13: (S112,1/A056)**

Date 01/20/2025	Drawing Title: SOW #13 LEVEL-07 NEW SLAB EXTENSION SUPPORT FRAMING PLAN
Scale VARIES	