
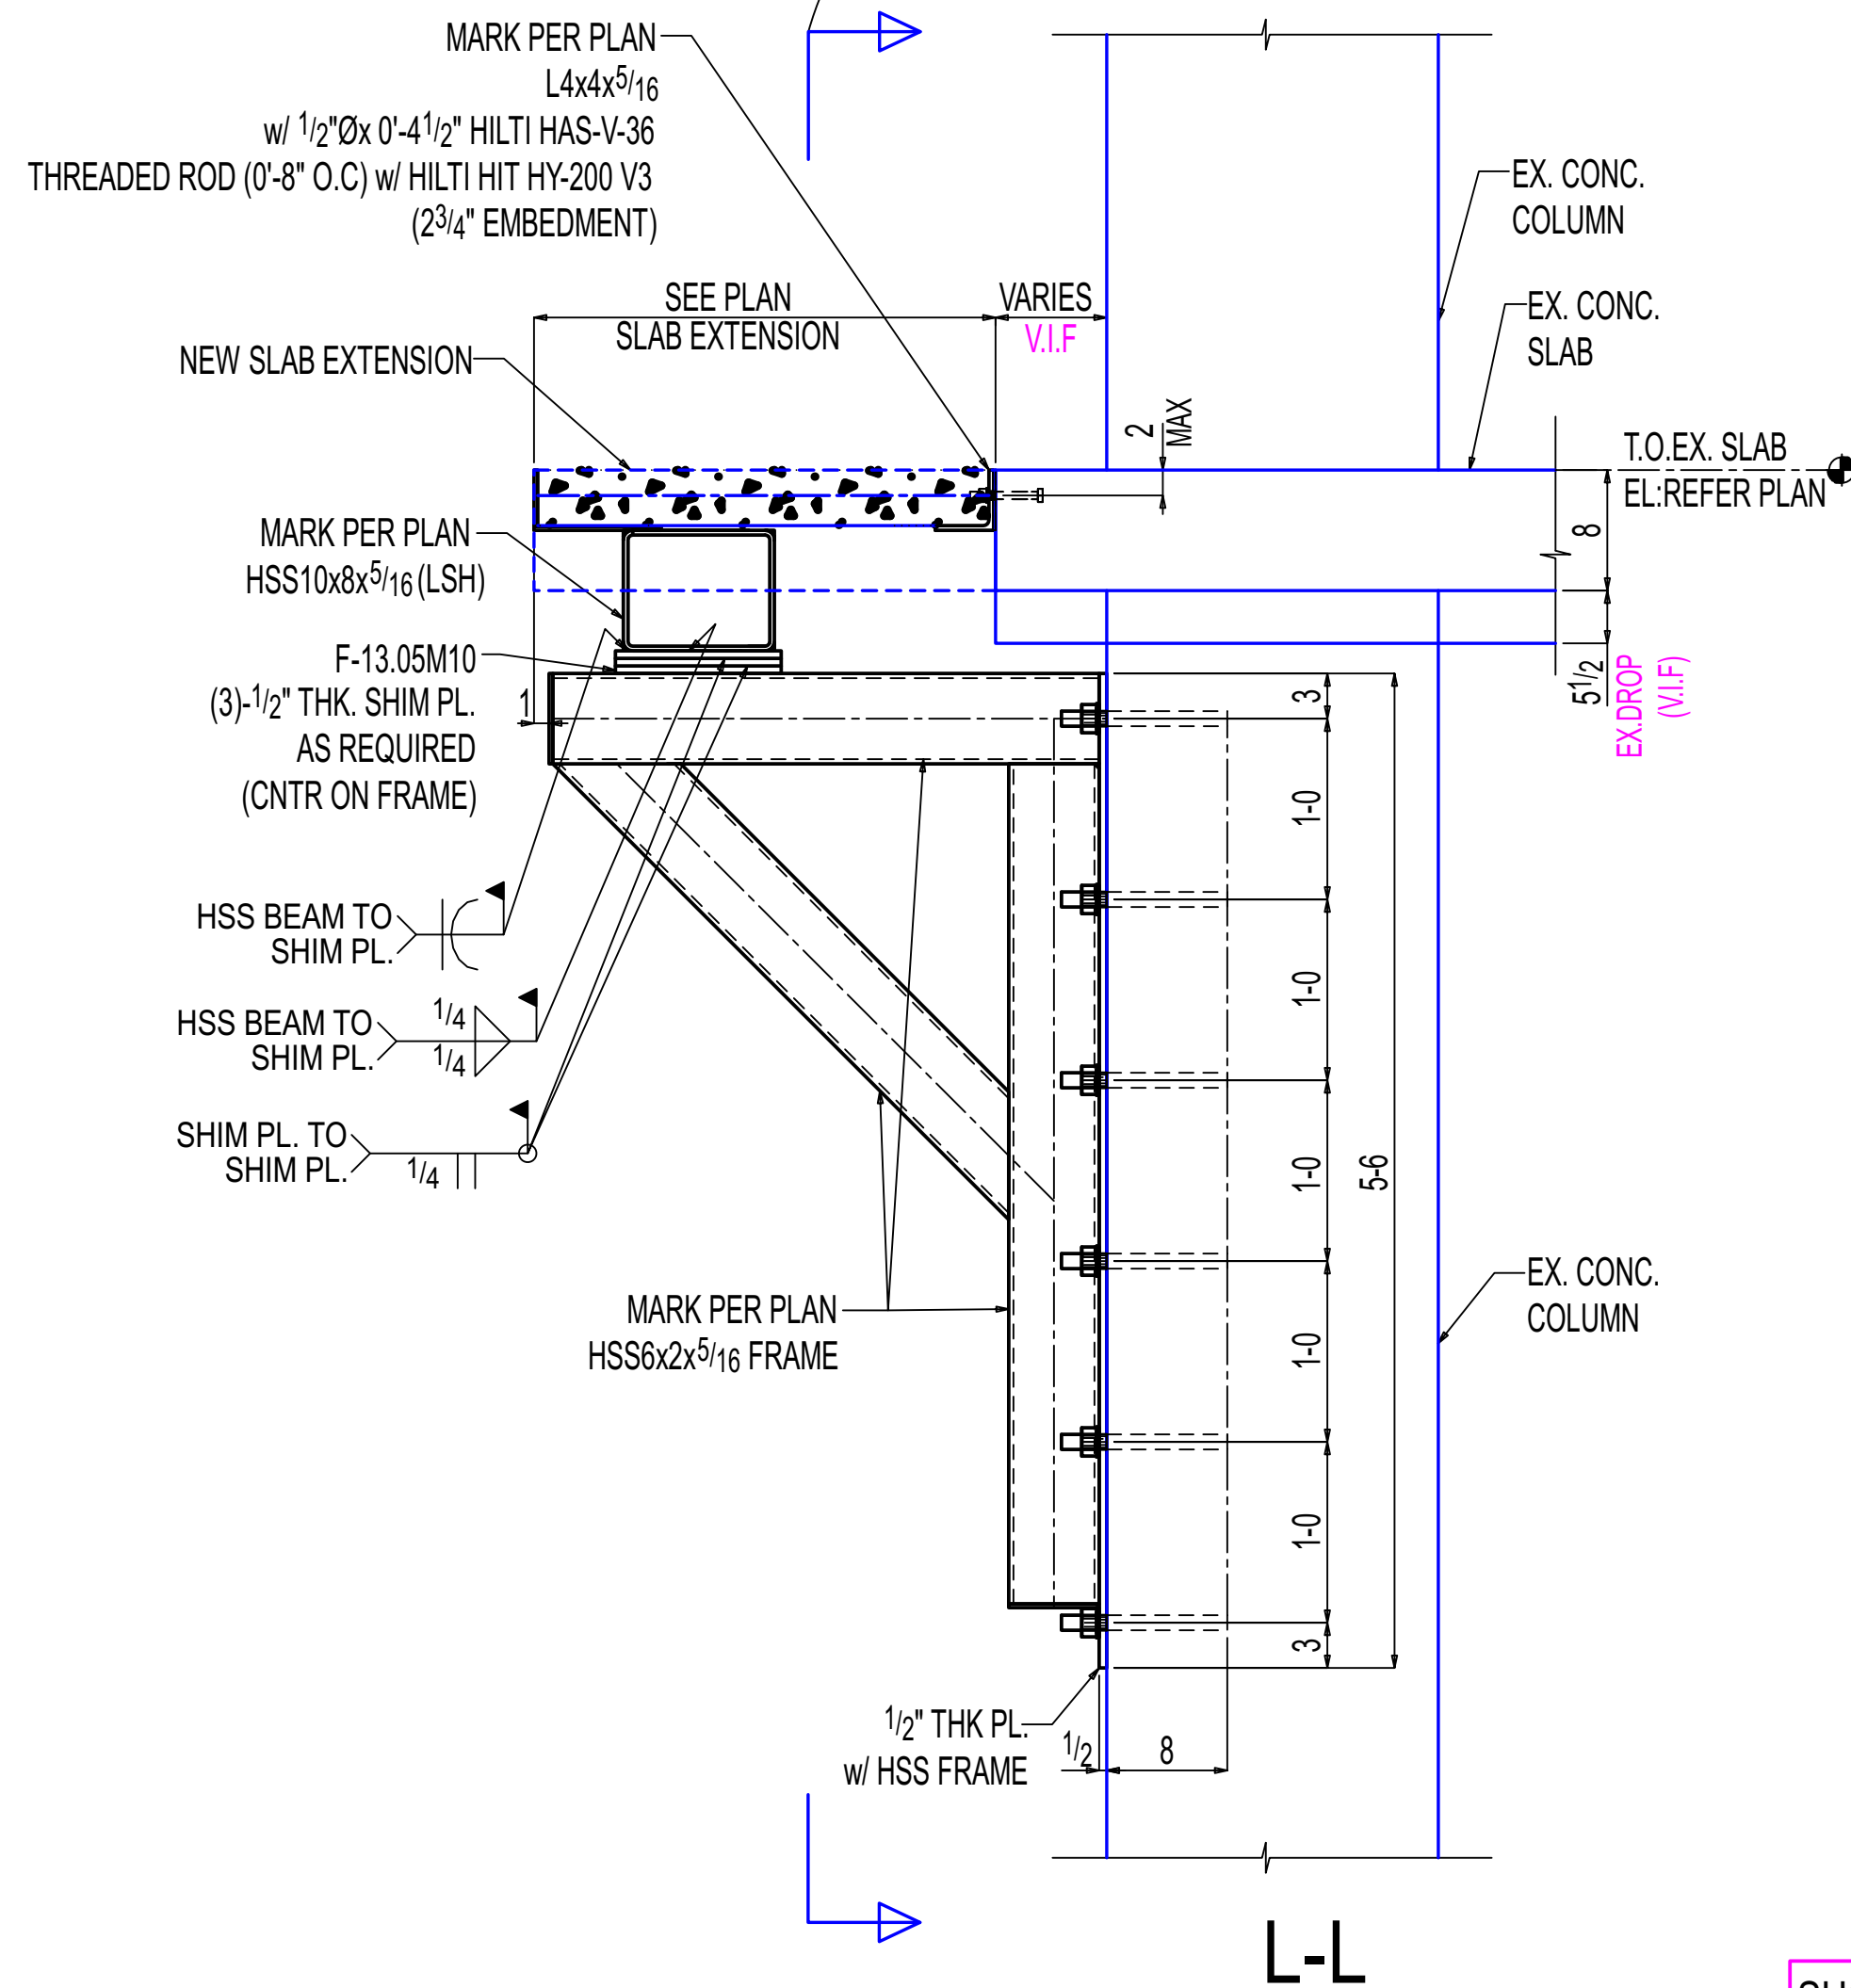


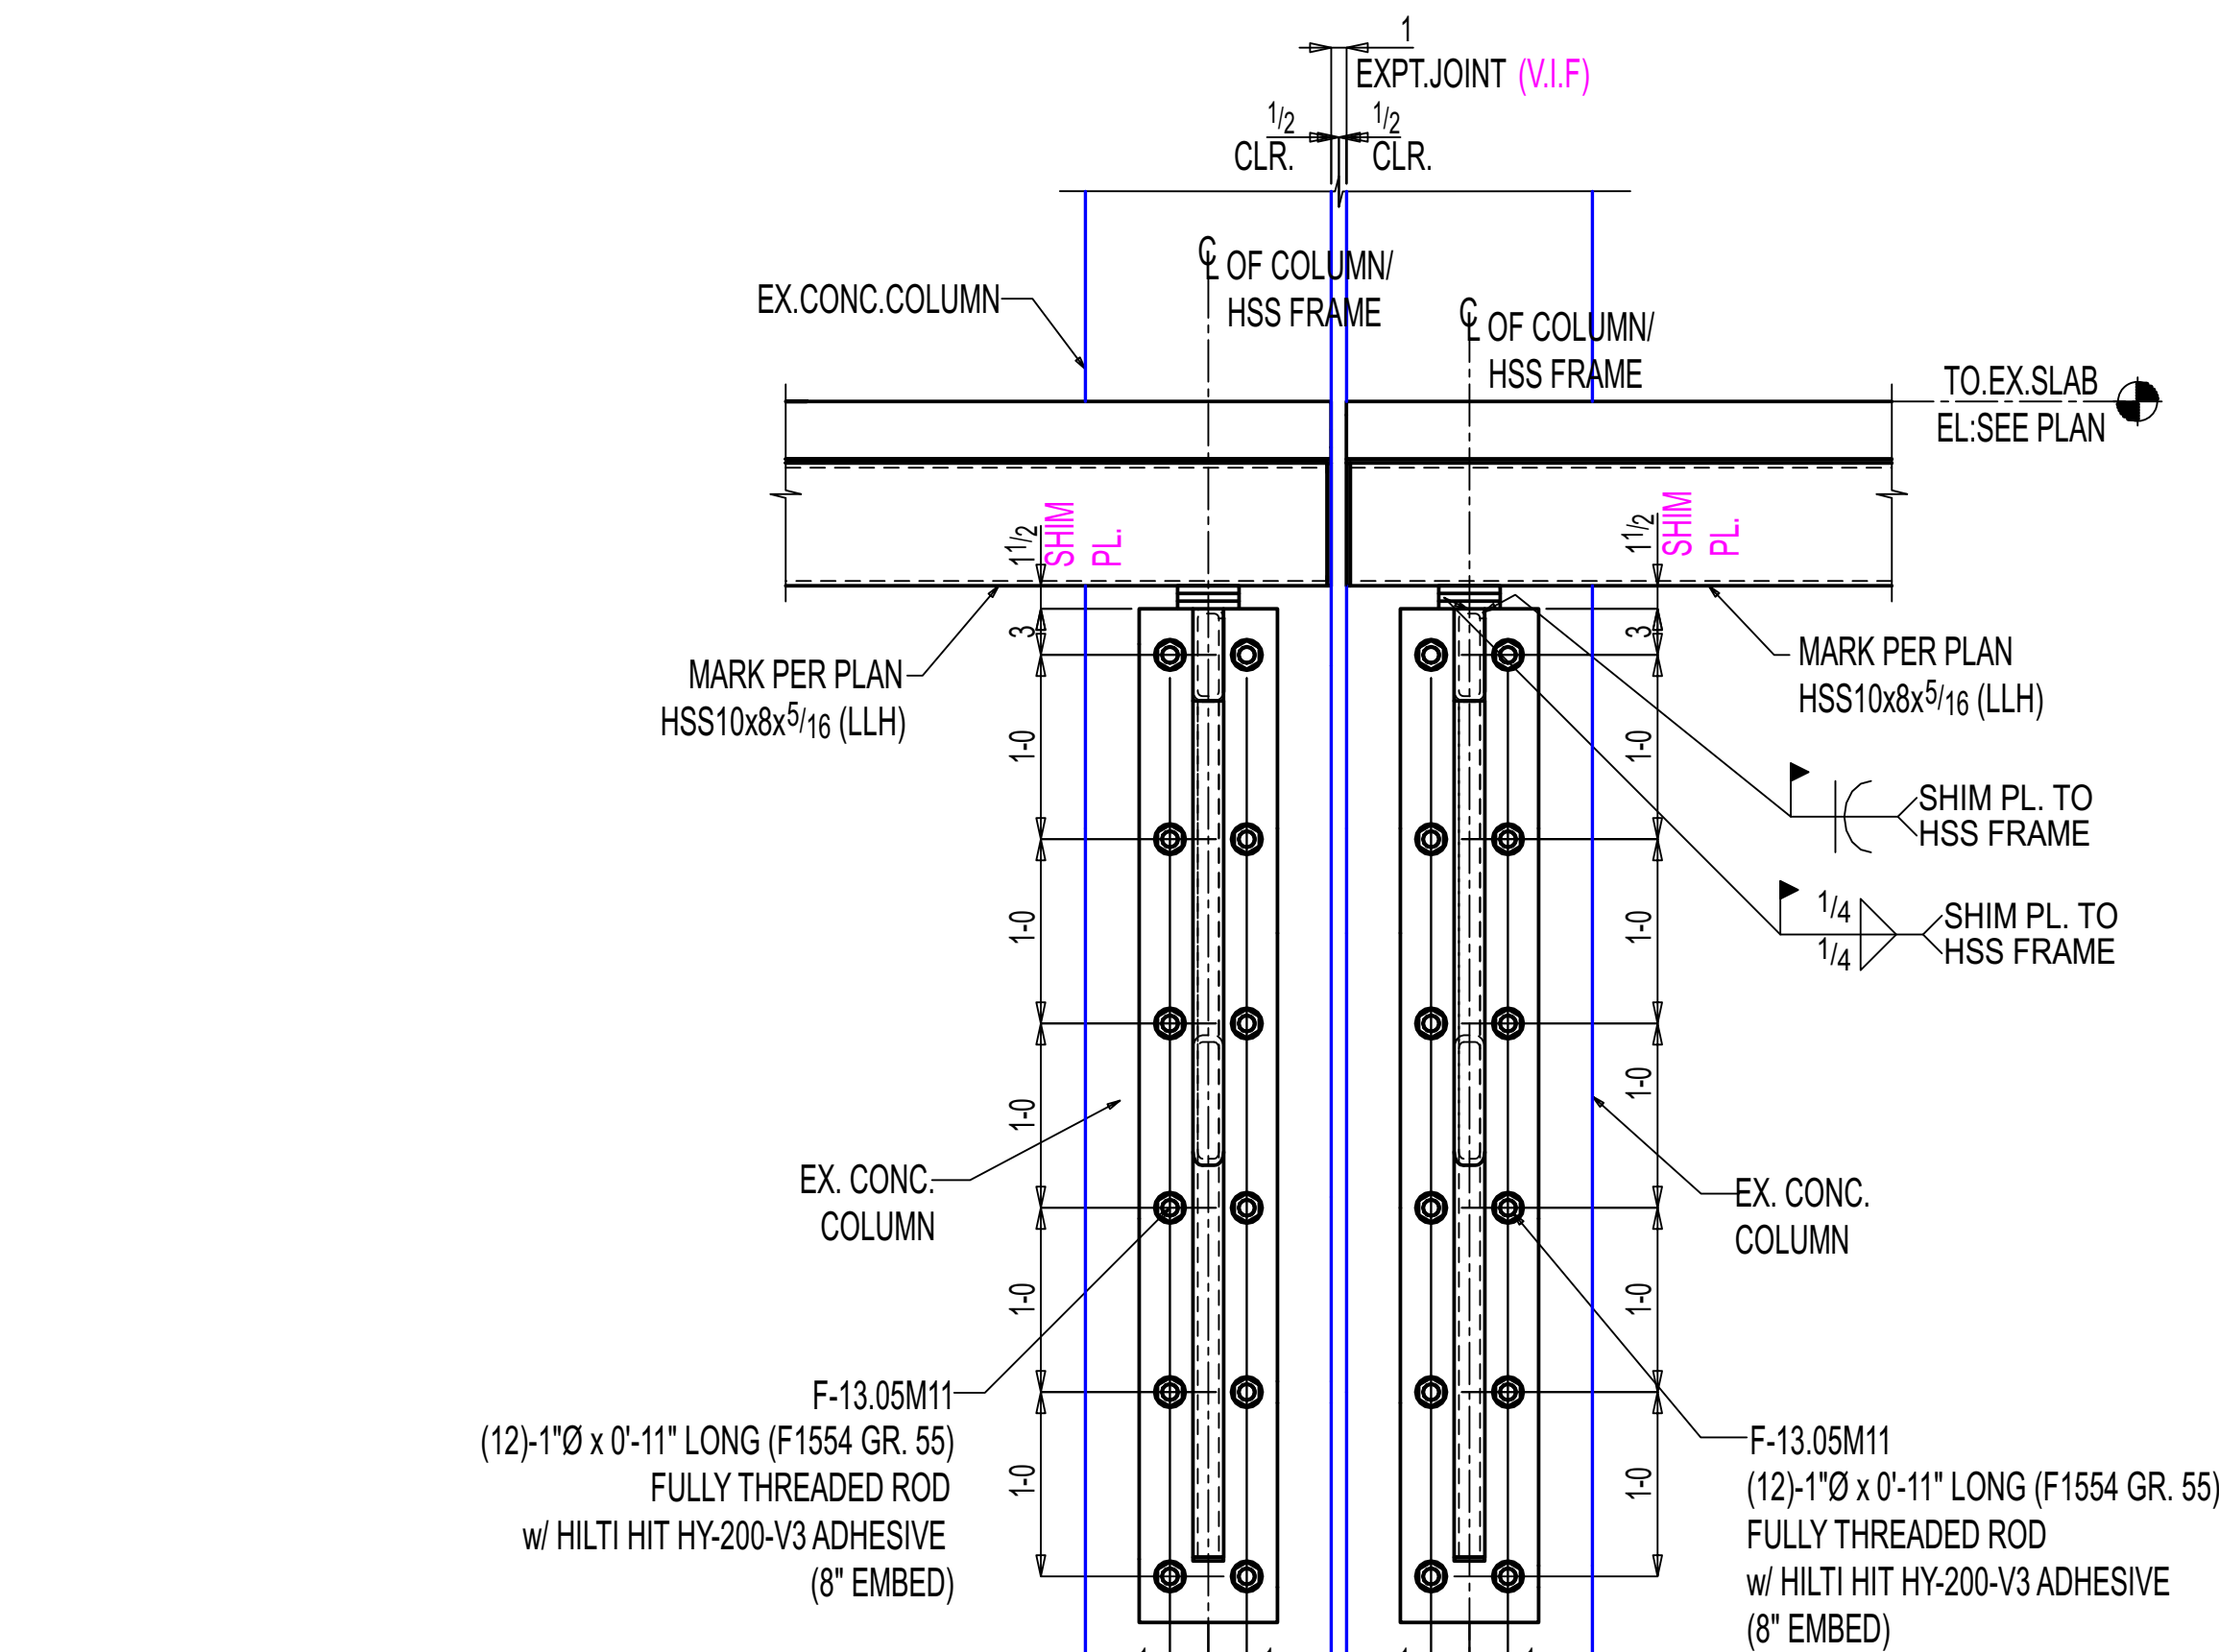


L-L

E-13.00A
(REF: 18/S205)

OTHERS NOT SHOWN FOR CLARITY


SHOP / ERECTOR NOTE:
LOCATE EXISTING REBAR PRIOR TO FABRICATION OF PLATE.
DO NOT DRILL THROUGH REBAR.

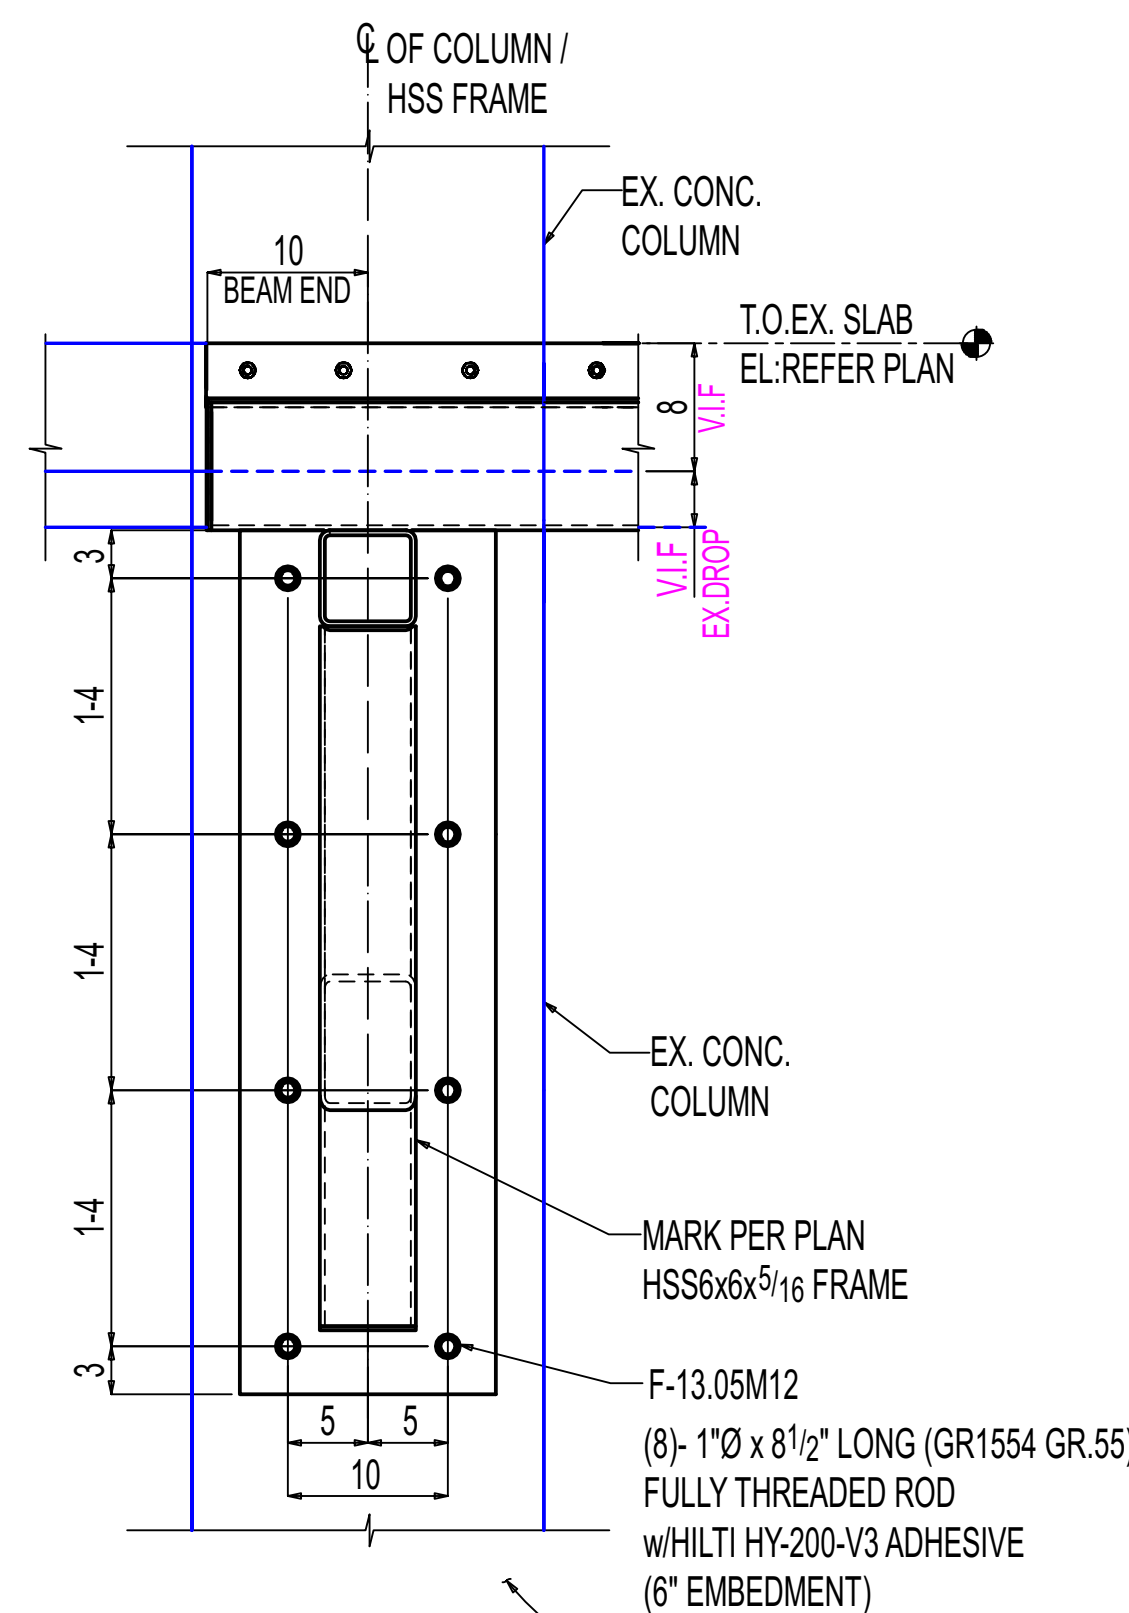

M-M

E-13.00A
(REF: 4/S316)


OTHERS NOT SHOWN FOR CLARITY

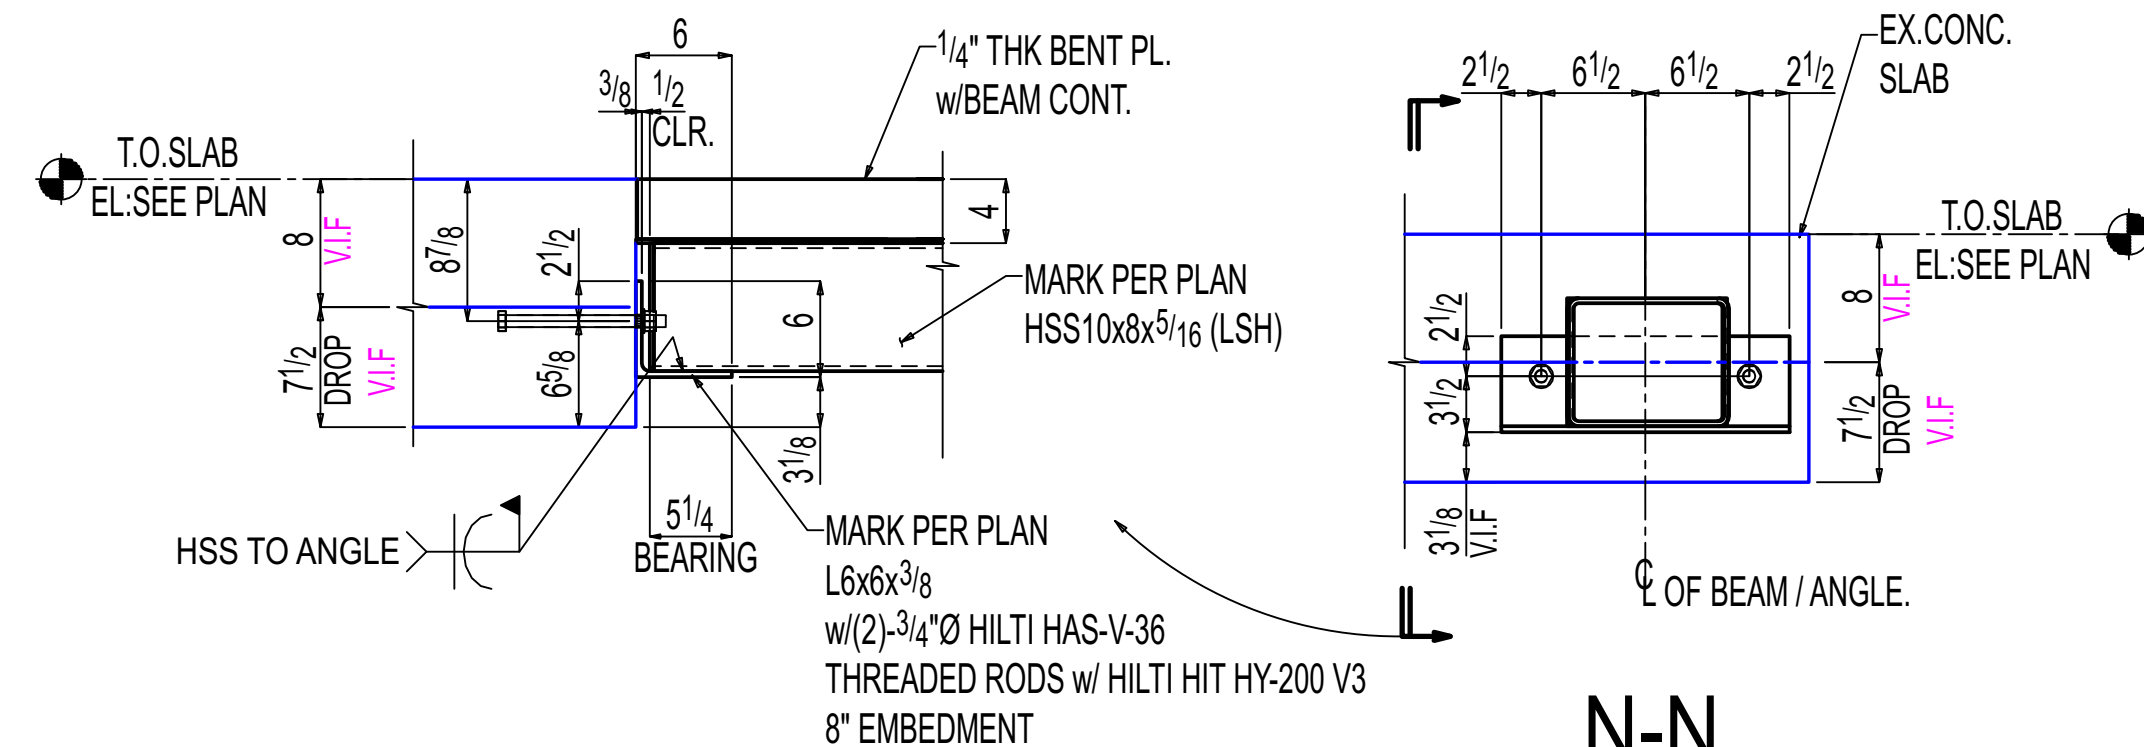

N-N

E-13.00A
(REF: 2 & 2A/S316)

OTHERS NOT SHOWN FOR CLARITY

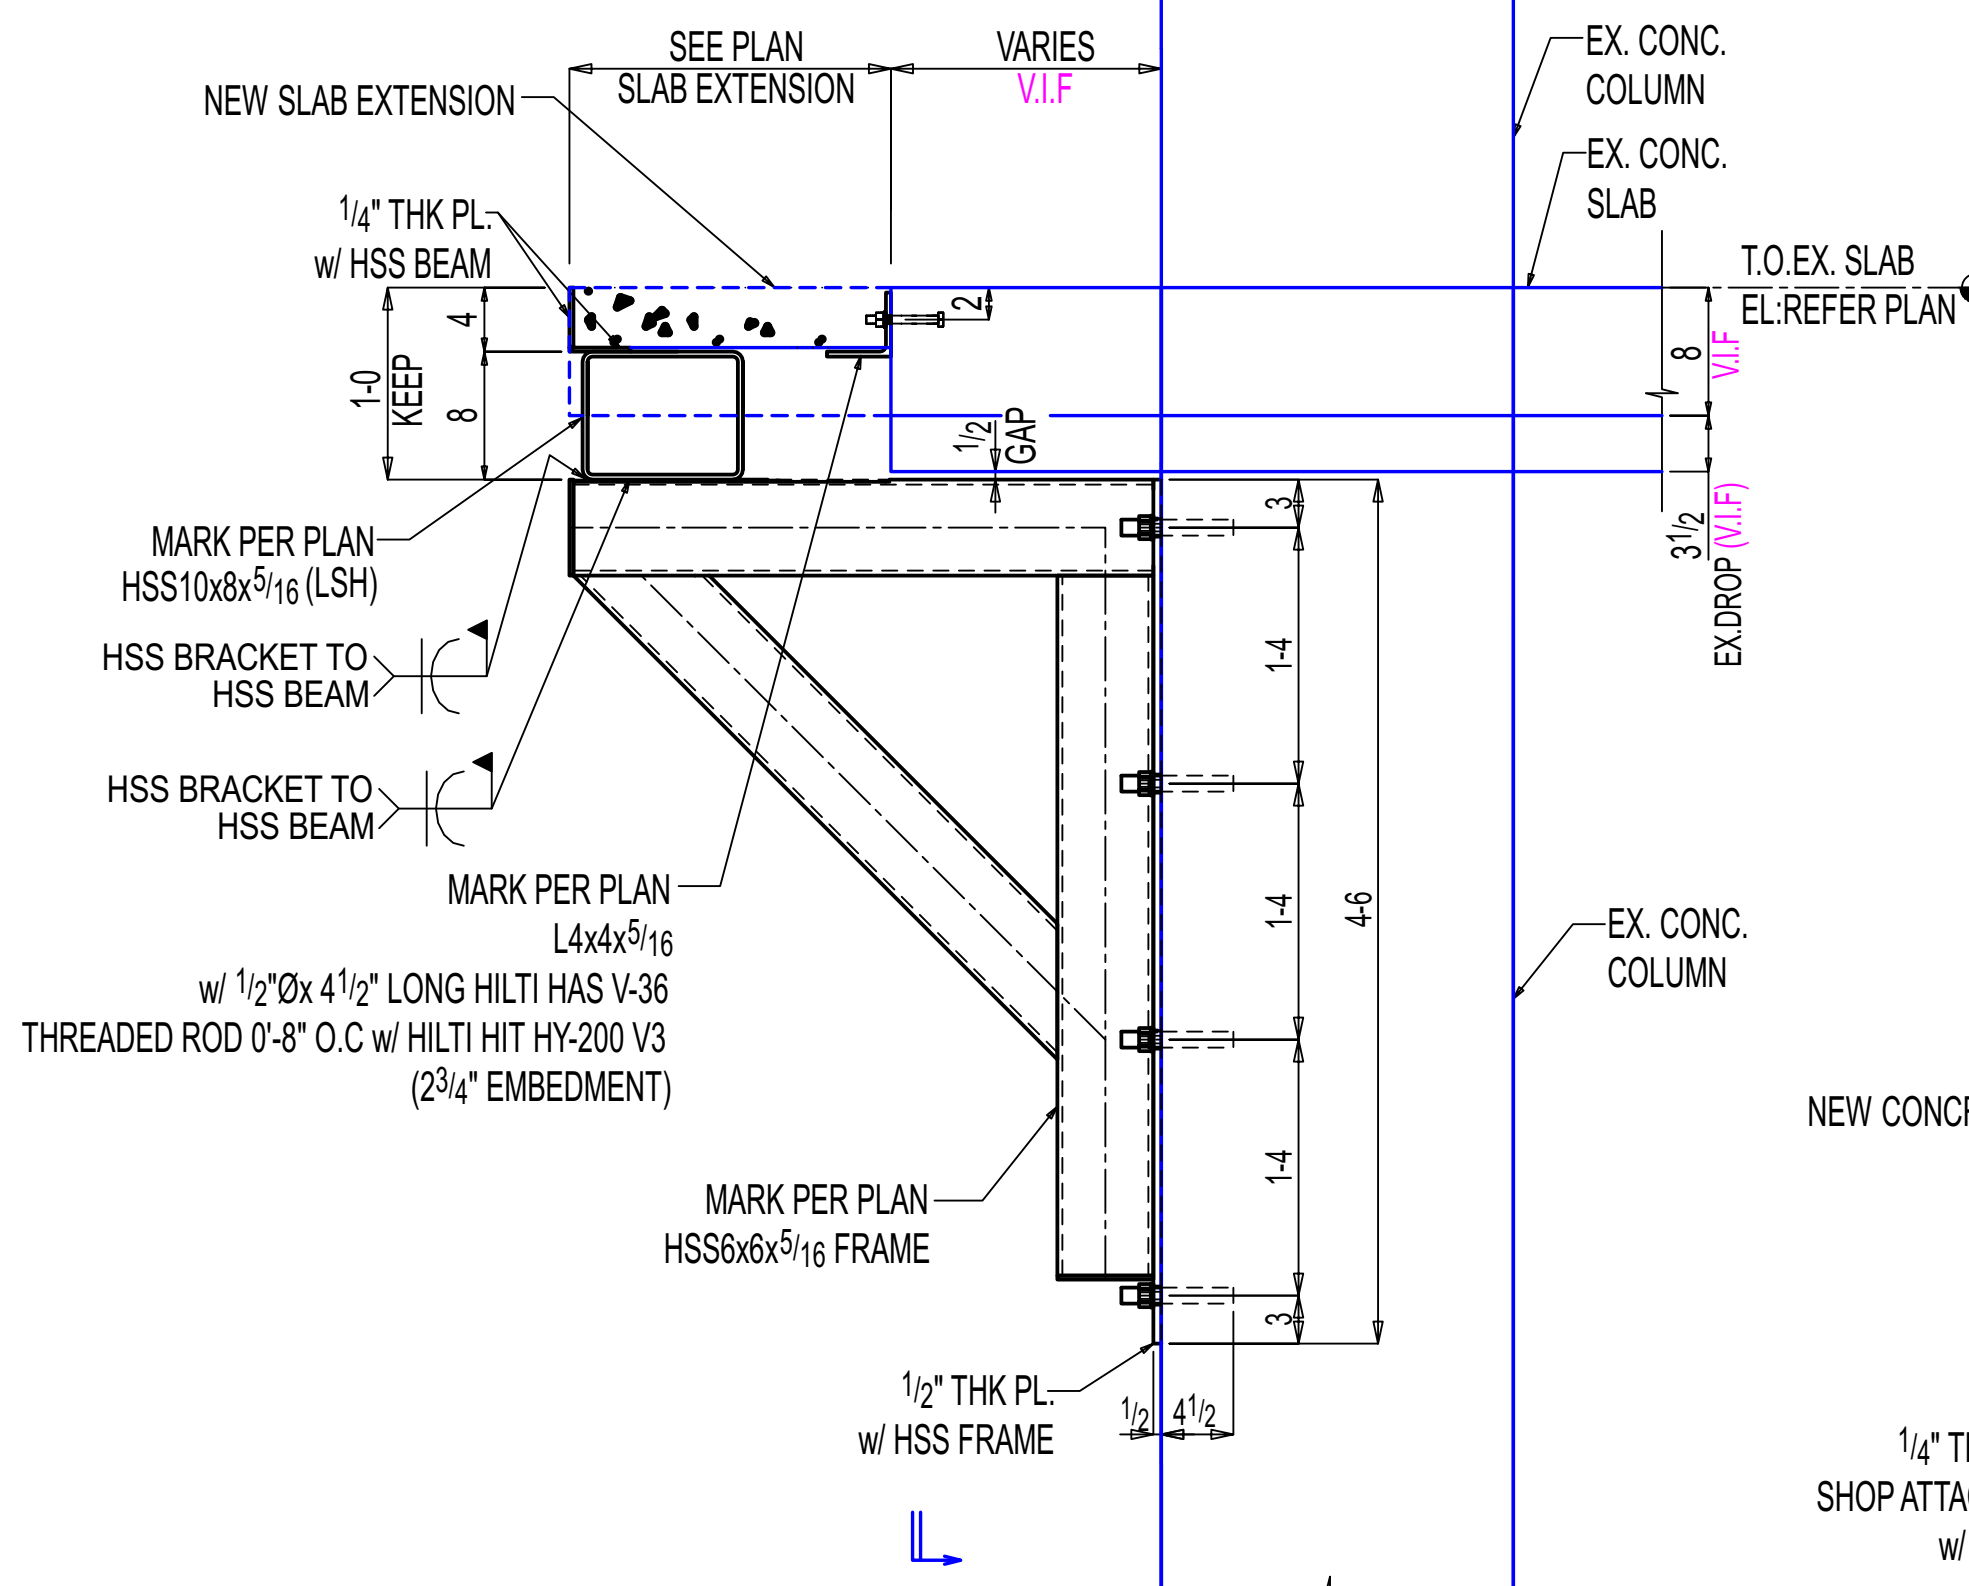

P-P

E-13.00A
(REF: 8/S315)

OTHERS NOT SHOWN FOR CLARITY

General Notes

- *Structural steel shall conform to ASTM-A992.
- *Structural SQR/RND.tubing conform to ASTM A500 Grade C
- *Pipe shall conform to ASTM A53, Grade B.
- *Channels, Angles and plates shall conform to A36.
- *All bolts shall be 3/4" High strength in accordance with ASTM A325 (UNO)
- *Welding Electrodes for Carbon steel :E70xx

# of Copies	Revision/ Issue	Destination	Date
3	0	For Construction	11-17-2025
2	B	For Re-Approval	10-24-2025
1	A	For Approval	09-19-2025

IRON FABRICATION SERVICES, LLC.

3029 M. Street, NW, Suite 202
Washington, DC 20007
Tel: 202-800-5599
Fax: 202-478-0303

Project Name and Address

MARYLAND AVENUE
Location: **1250 MARYLAND AVENUE SW**
WASHINGTON, DC 20024

Contractor:

BALFOUR BEATTY

Approved for Fabrication by:

Signature

Contract

224009

Drawing

E-13.04

Contract Item:

LEVEL-07
SLAB EXTENSION

Ref:

SOW-13: 3,4,5&6 / S307

Date

01/20/2025

Scale

VARIES

Drawing Title:

SOW #13 LEVEL-07 NEW
SLAB EXTENSION SUPPORT
SECTIONS