


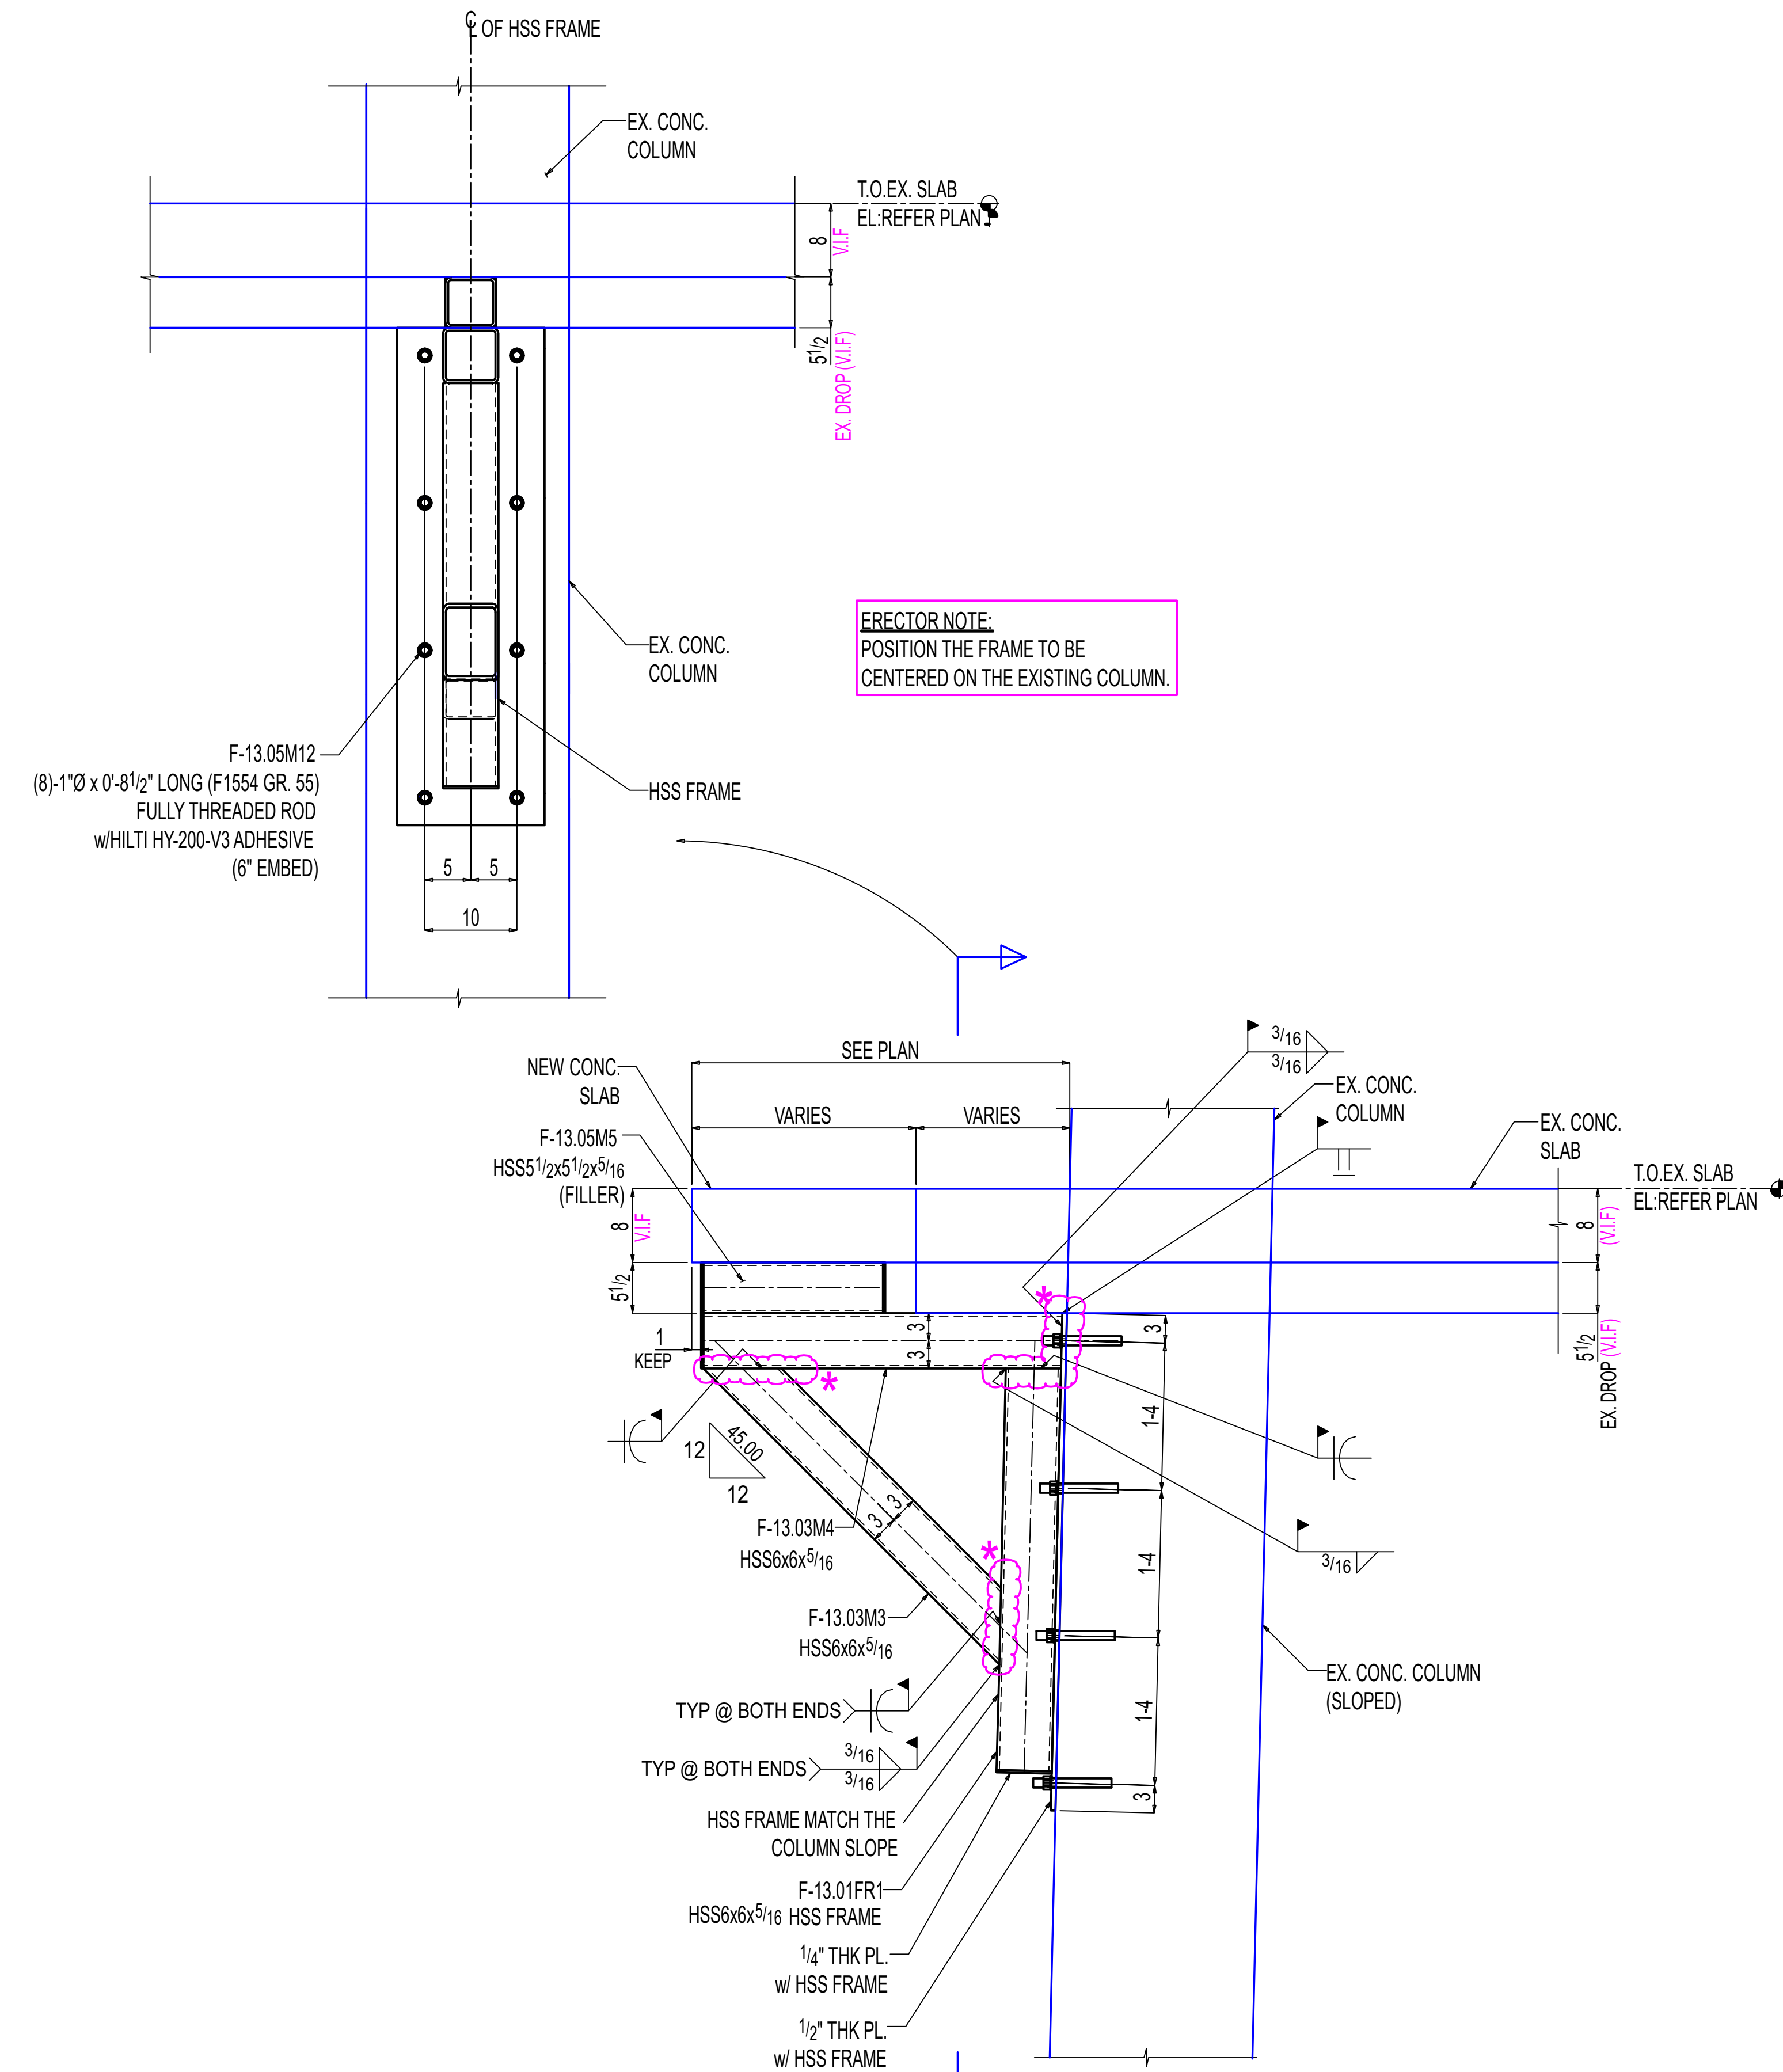

*-ERECTOR NOTE:
FIELD CUT HSS6x6x ENDS TO SUIT AT EXISTING COLUMN SLOPE.

OTHERS NOT SHOWN FOR CLARITY

SHOP / ERECTOR NOTE:
LOCATE EXISTING REBAR PRIOR TO FABRICATION OF PLATE.
DO NOT DRILL THROUGH REBAR.

General Notes

*Structural steel shall conform to ASTM-A992.
*Structural SQR/RND.tubing conform to ASTM A500 Grade C
*Pipe shall conform to ASTM A53, Grade B.
*Channels, Angles and plates shall conform to A36.
*All bolts shall be 3/4" High strength in accordance with ASTM A325 (UNO)
*Welding Electrodes for Carbon steel :E70xx

# of Copies	Revision/ Issue	For Construction Destination	11-17-2025 Date
1	0		

IRON FABRICATION SERVICES, LLC.

3029 M. Street, NW, Suite 202
Washington, DC 20007
Tel: 202-800-5599
Fax: 202-478-0303

Project Name and Address

MARYLAND AVENUE

Location: **1250 MARYLAND AVENUE SW
WASHINGTON, DC 20024**

Contractor:

BALFOUR BEATTY

Approved for Fabrication by:

Signature

Contract # **224009**

Drawing # **E-13.05**

Contract Item: **LEVEL-07
SLAB EXTENSION**

Ref: **SOW-13: 3,4,5&6 / S307**

Date
01/ 20/ 2025

Drawing Title:

**SOW #13 LEVEL-07 NEW
SLAB EXTENSION SUPPORT
SECTIONS**