


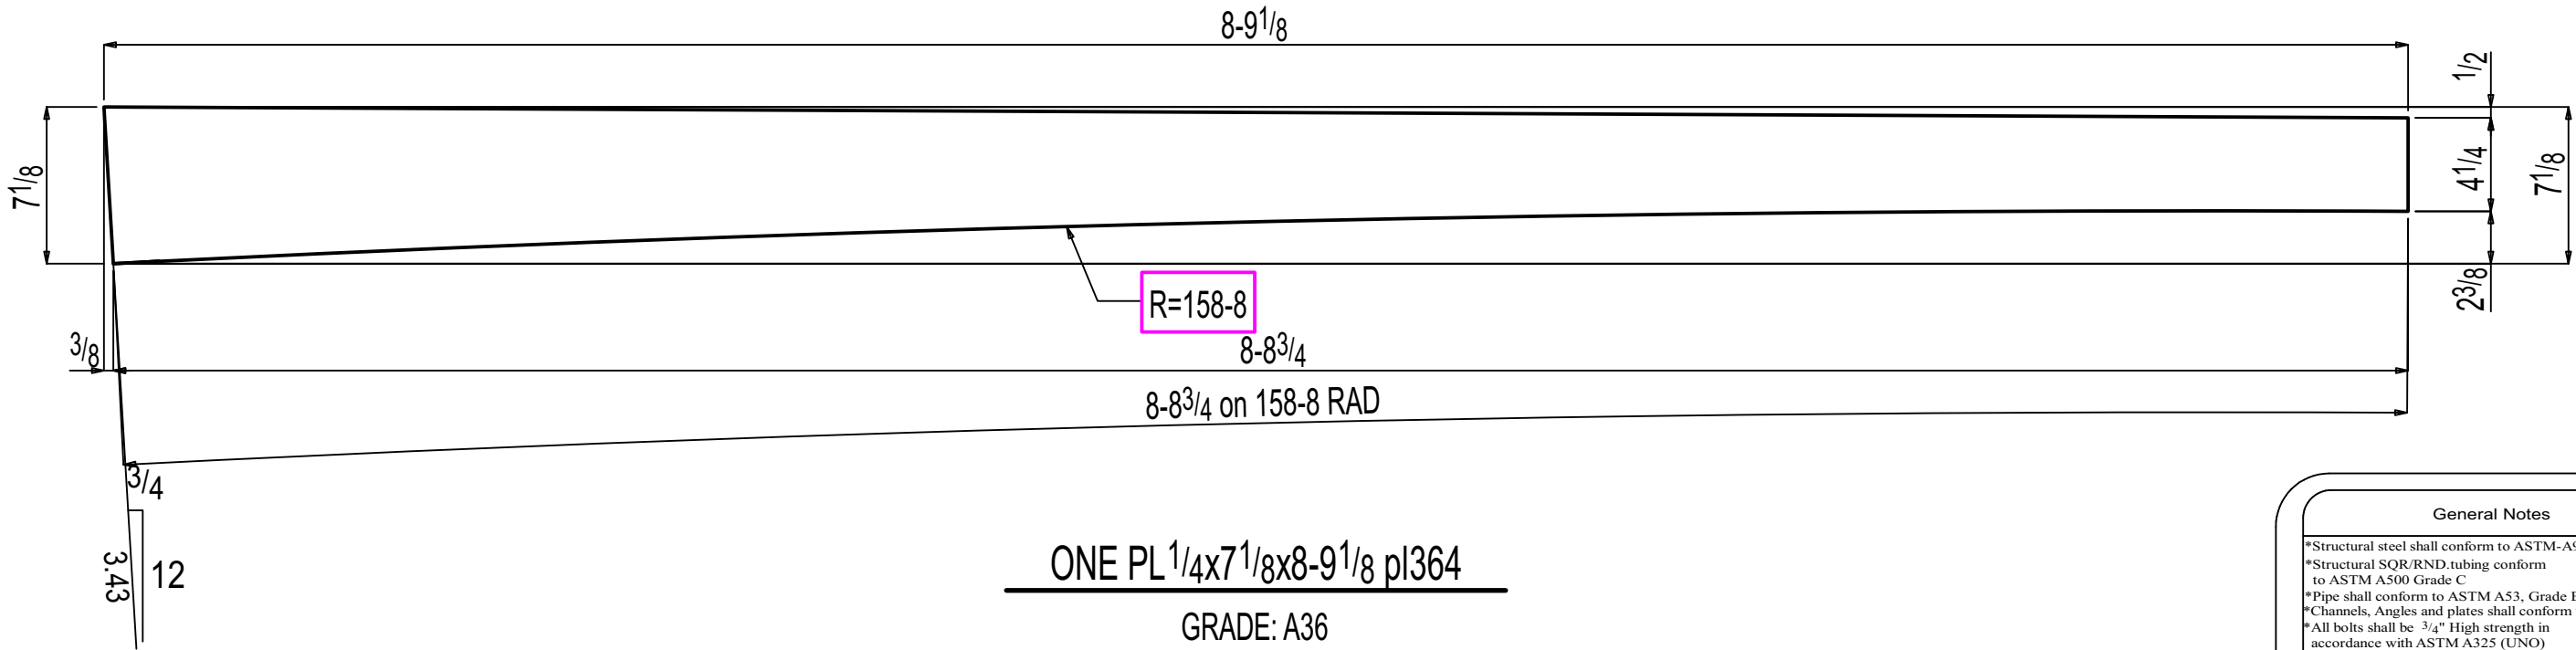

ONE PL 1/4x7 1/8x8-9 1/8 pl364
GRADE: A36

General Notes

*Structural steel shall conform to ASTM-A992.

*Structural SQR/RND.tubing conform to ASTM A500 Grade C

*Pipe shall conform to ASTM A53, Grade B.

*Channels, Angles and plates shall conform to A36.

*All bolts shall be 3/4" High strength in accordance with ASTM A325 (UNO)

*Welding Electrodes for Carbon steel :E70xx

*Structural members are to be shop primer (U.N.O).

*Surface Preparation-SSPC-SP3 UNO.

*If welds exposed to view, should be ground smooth.

1	0	FOR FABRICATION	11-17-2025
# of Copies	Revision/ Issue	Destination	Date

IRON FABRICATION SERVICES, LLC.

3029 M. Street, NW, Suite 202
Washington, DC 20007
Tel: 202-800-5599
Fax: 202-478-0303

Project Name and Address

MARYLAND AVENUE

Location: 1250 MARYLAND AVENUE SW
WASHINGTON, DC 20024

Contractor:

BALFOUR BEATTY

Approved for Fabrication by:	Signature

Contract #	224009	Drawing #	pl364
Contract Item: PLATE			
Ref: SOW -13:F-13.00-F-13.05			
Date 01/ 23/ 2025	Drawing Title: PLATE		
Scale VARIES			

HOLE:13/16 Ø (U.N.O)