


BILL OF MATERIAL									
ASSEMBLY MARK	TOTAL QTY	SUB-PIECE MARK	UNIT QTY	MATERIAL DESCRIPTION		LENGTH		REMARKS	UNIT WEIGHT
						FT	IN		
07GR1006	ONE			GUARDRAIL				PNT	213
	1	07GR1006	1	PIPE 1½ SCH40		19	4½	A53 GR B (TYPE-S)	53
	4	p40197	4	PIPE 1½ SCH40		3	7¾	A53 GR B (TYPE-S)	10
	4	p4063	4	PIPE 1½ SCH40		3	5	A53 GR B (TYPE-S)	9
	1	p40177	1	PIPE 1½ SCH40		0	11¾	A53 GR B (TYPE-S)	3
	5	pl658	5	PL ½x5		0	8	A36	6
	1	pl667	1	PL 1¼x4		7	10	A36	27
	1	pl1476	1	PL 1¼x4		7	6	A36	26
				FIELD BOLTS					
	10	m206		½ Dia HILTI KB-T22		0	¾	+1HD WASH	
				EXPANSION ANCHOR					

Total weight : 213

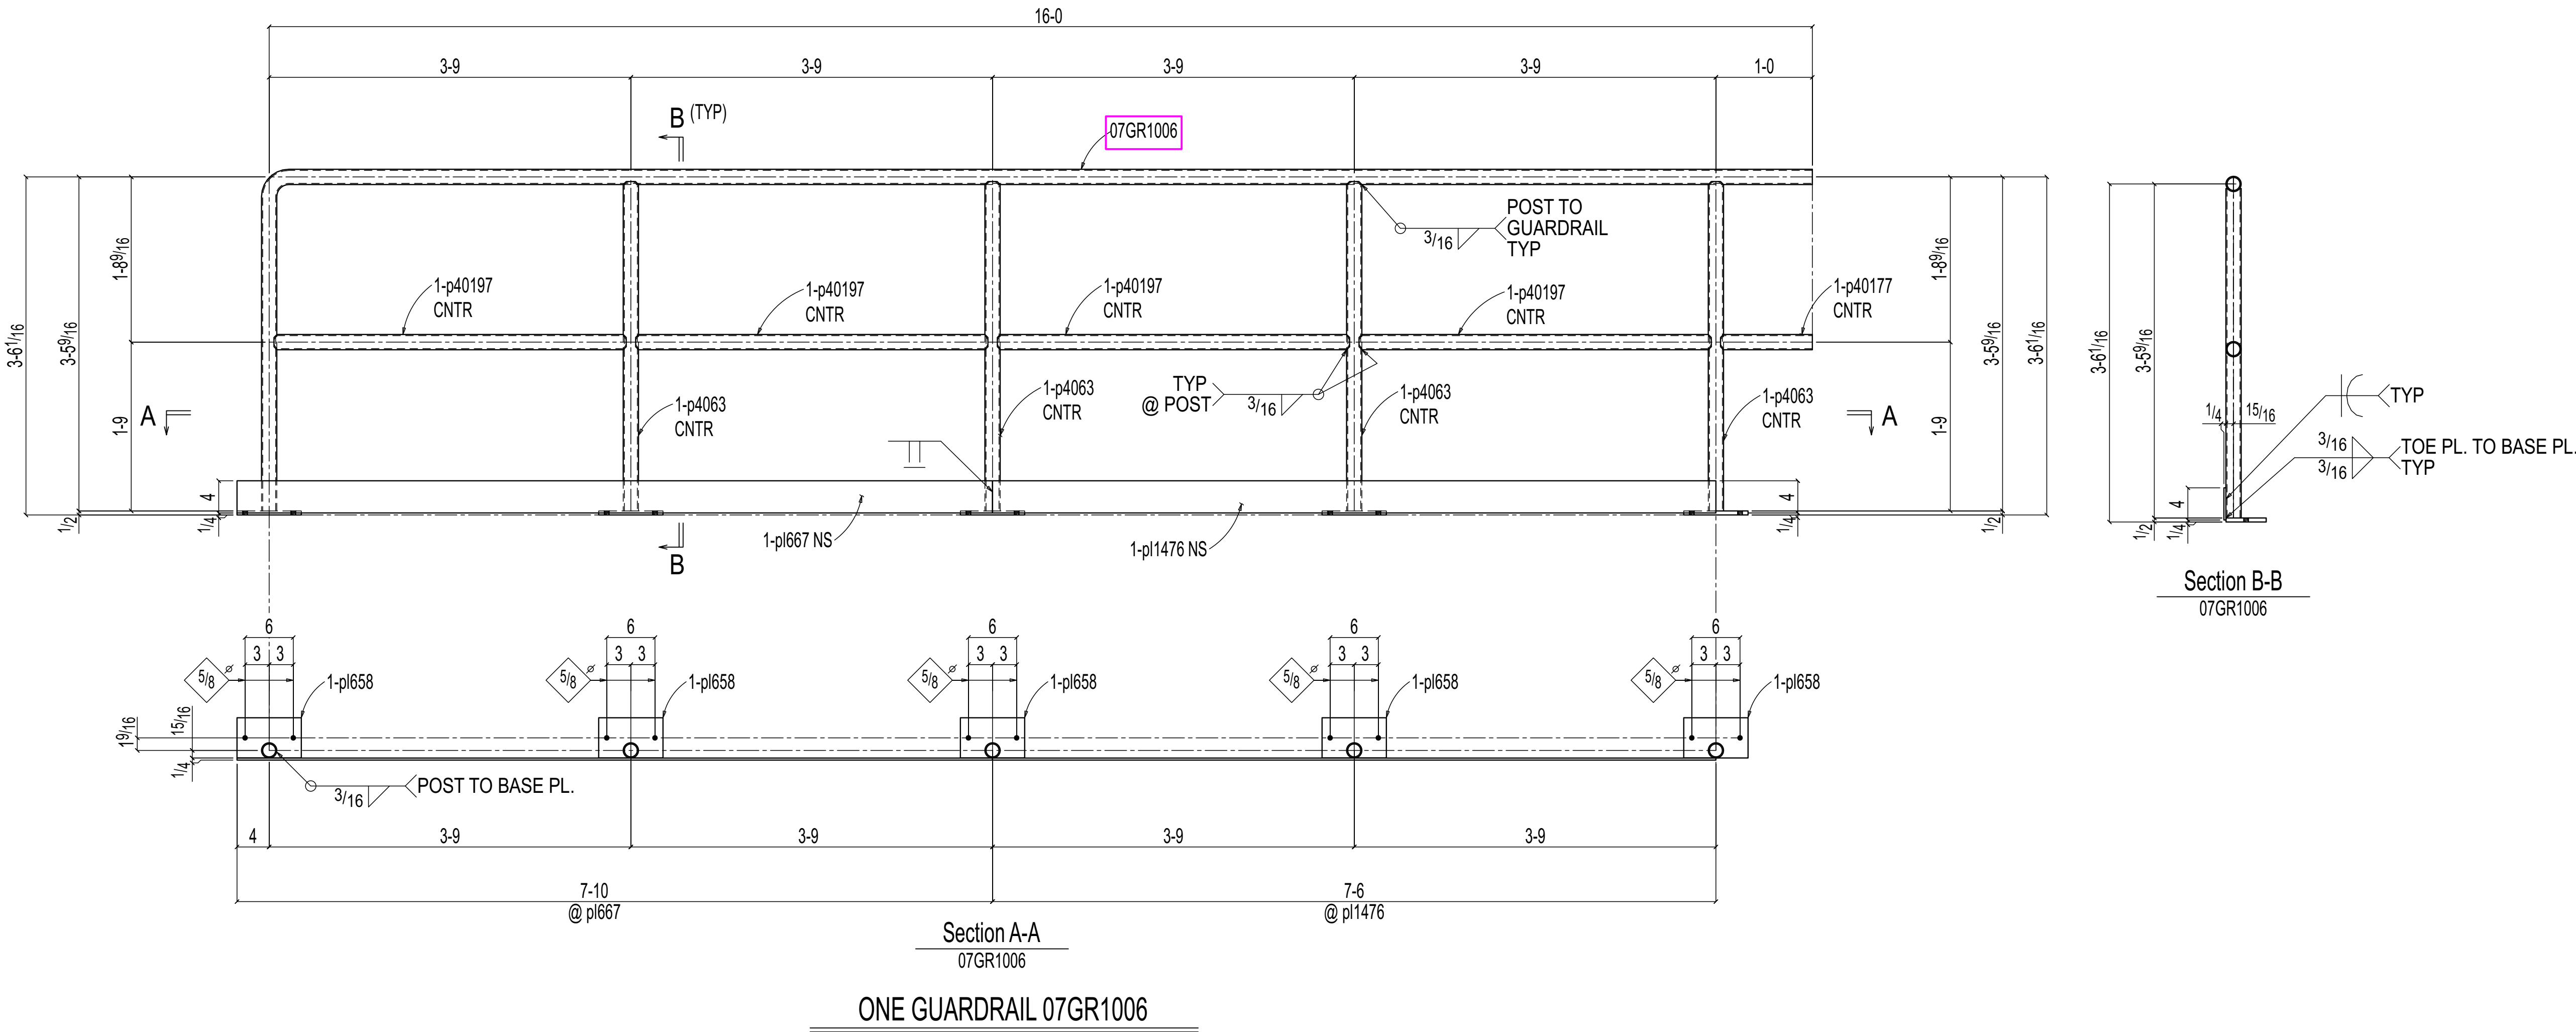


ALL RE-ENTRANT CUT
TO BE 1/2" RADIUS (U.N.O)
WELDS : E70XX
HOLES : 13/16" DIA (U.N.O)
MAT'L : A36 (U.N.O)
CLEAN : SSPC-SP3
PAINT : SHOP PRIMER

REVISIONS

REV	DWN BY	DATE	DESCRIPTION
A	GSV	Jun 16 2025	ISSUED FOR APPROVAL
0	GSV	Jan 27 2026	ISSUED FOR FABRICATION
1	GSV	Feb 5 2026	ISSUED FOR FABRICARION

THE INFORMATION NOTED HEREON THIS DRAWING IS THE
PROPERTY OF STEEL FAB ENTERPRISES, INC. AND SHALL
NOTED BE USED WITHOUT WRITTEN CONSENT.

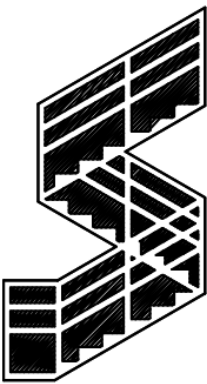

STEEL FAB
ENTERPRISES, LLC

MISCELLANEOUS METALS FABRICATOR AND ERECTORS
623 BAUMGARDNER ROAD, LANCASTER, PA 17603
TEL. (717)464-0330 FAX (717)464-9464
WWW.STEELFABENTERPRISES.COM



PROJECT OWNER : CK CAPITAL, LLC
PROJECT DESCRIPTION : CLEVELAND BROTHERS-MILESBURG
PROJECT ADDRESS : 1025N. EAGLE VALLY ROAD, HOWARD, PA 16841

CONTRACTOR : KINSLEY CONSTRUCTION, INC.			
DRAWN BY : BAS	DATE : 06-07-2025	PROJ. NO. : 25012	REV # 
CHECKED BY : GSV	DATE : 06-09-2025	DWG NO. : 07GR1006	
DWG DESCRIPTION : GUARDRAIL DETAIL			

DWG DESCRIPTION : GUARDRAIL DETAIL