



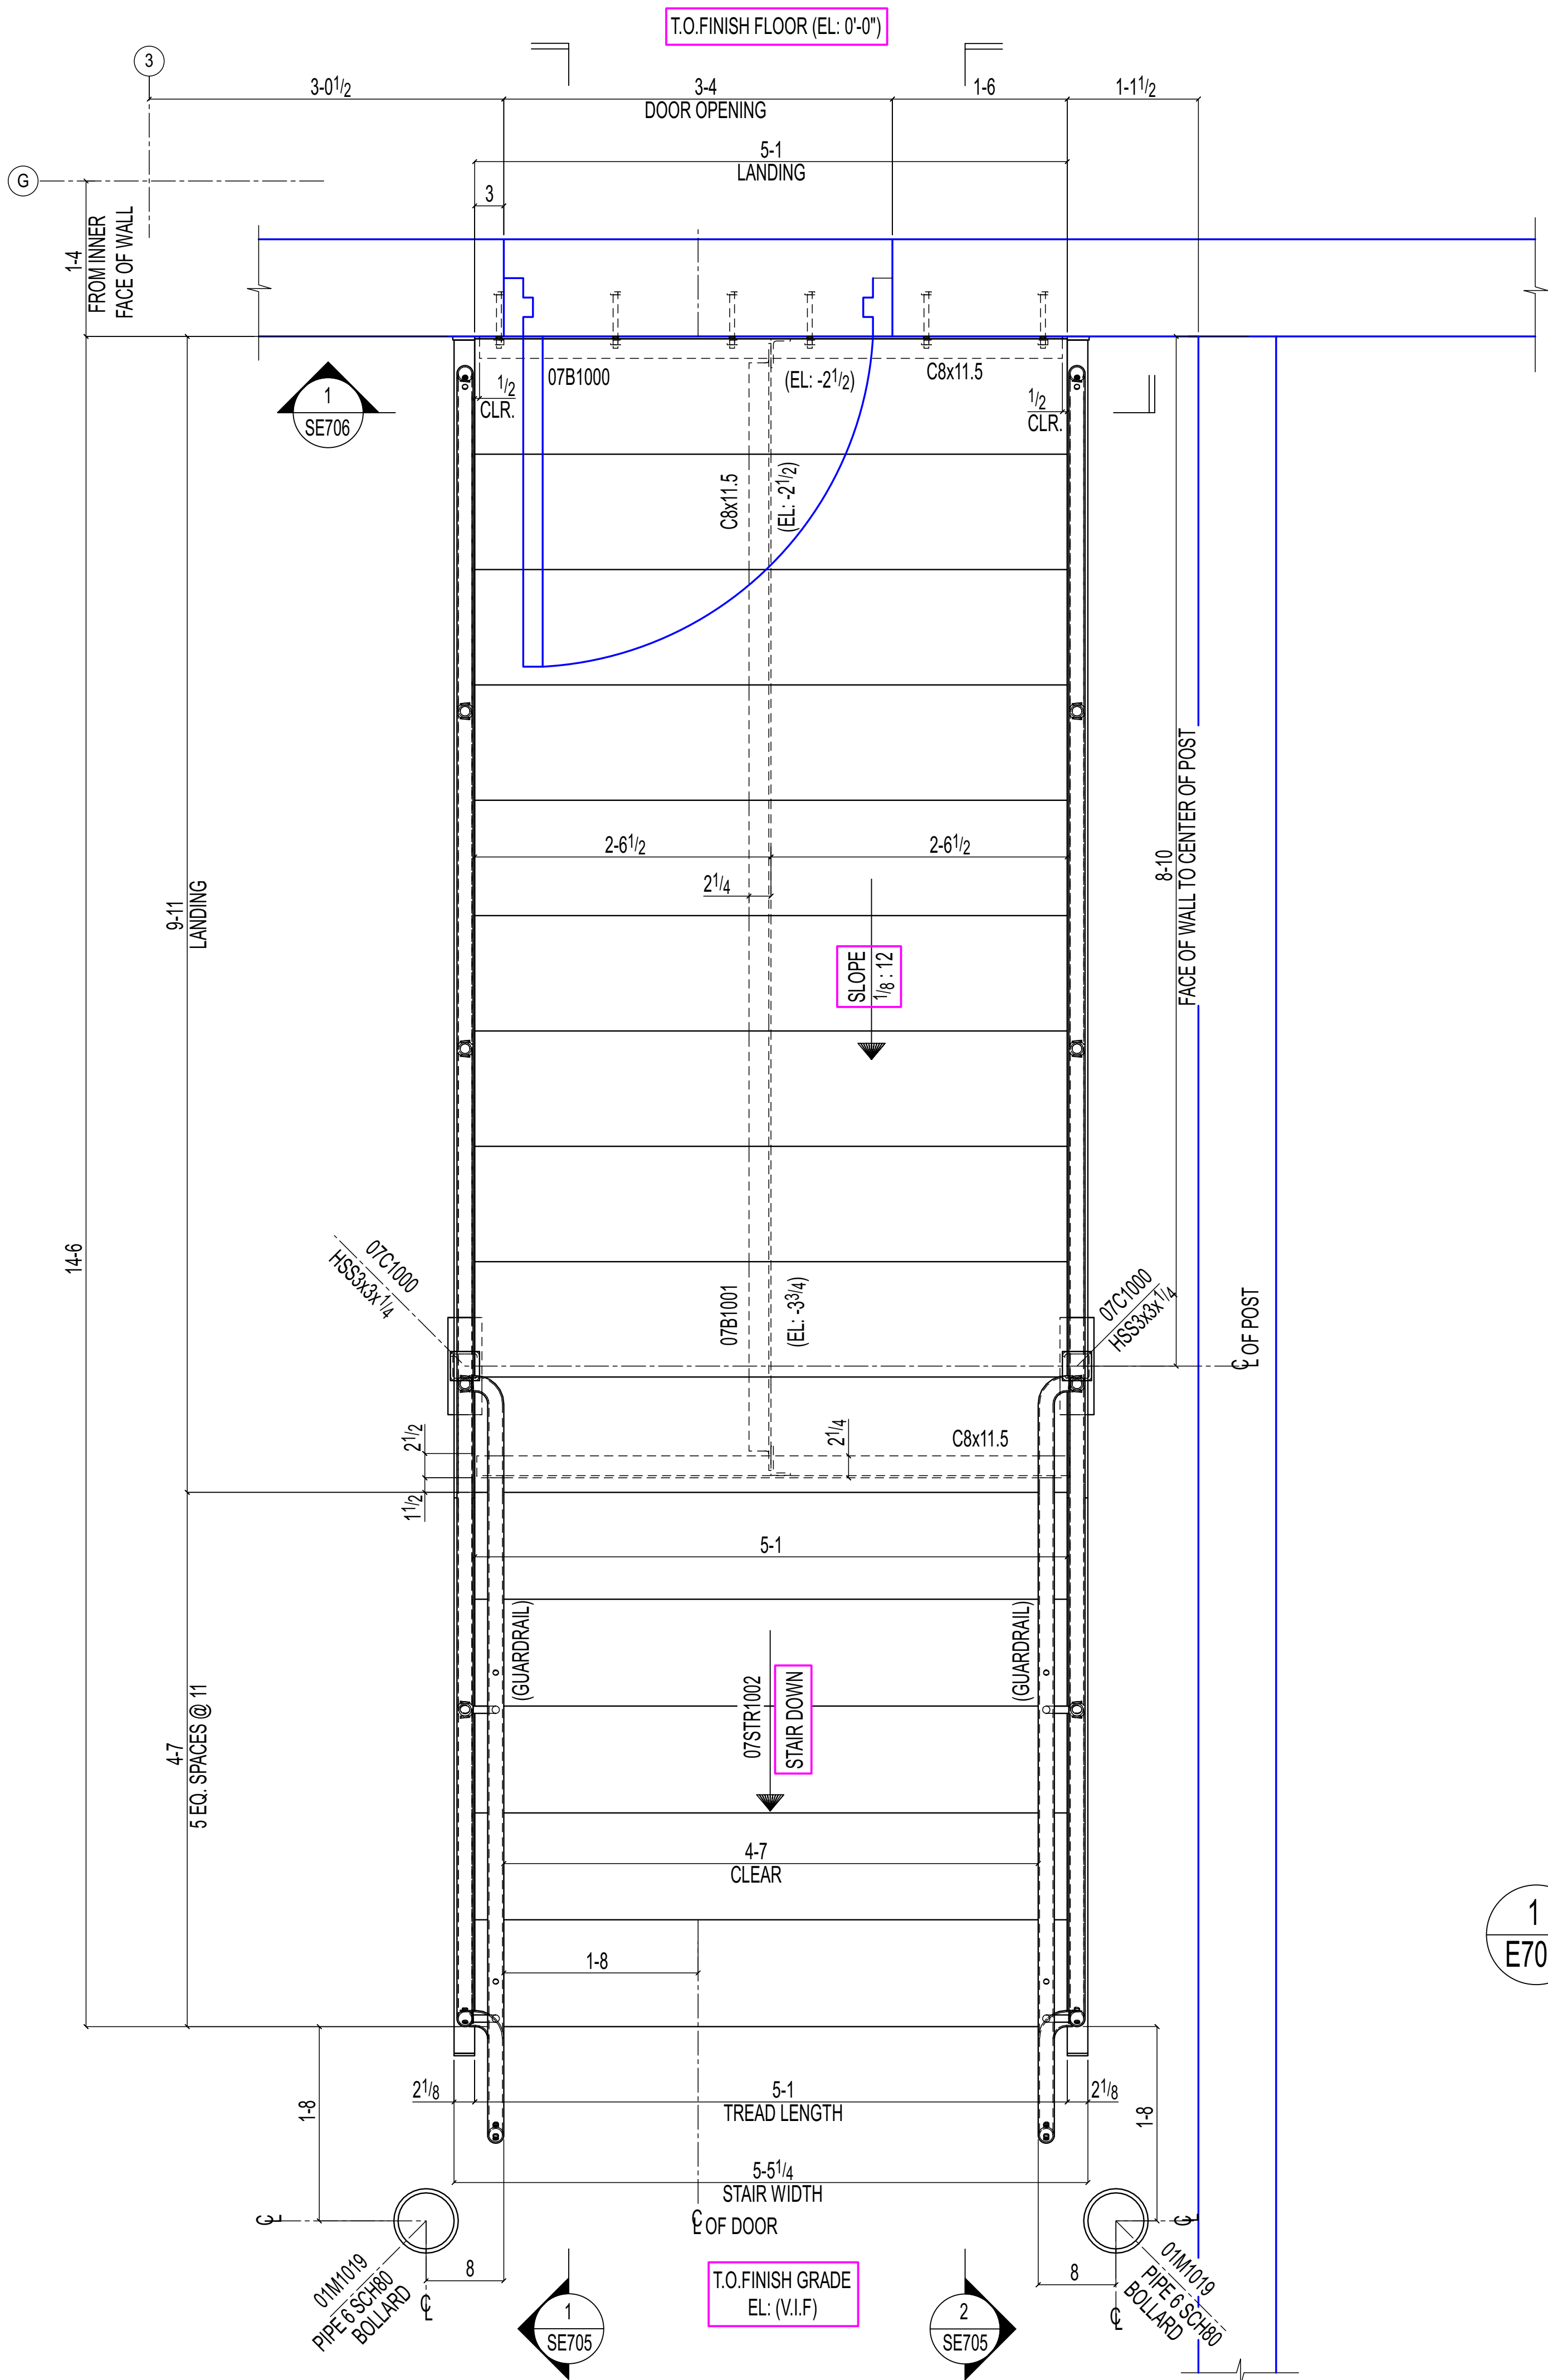


1 DOCK STAIR FRAMING PLAN
(REF: 1/A101,14/A380)


NOTE:
1. TOP OF SLAB REFERENCED FROM THE FINISHED FLOOR EL: [0'-0"] = DATUM EL: 100'-0" (U.N.O).
2. ALL STEELS ARE GALVANIZED (U.N.O)

2 DOCK STAIR PARTIAL FRAMING PLAN
(REF: 1/A101,14/A380)

OTHERS NOT SHOWN FOR CLARITY

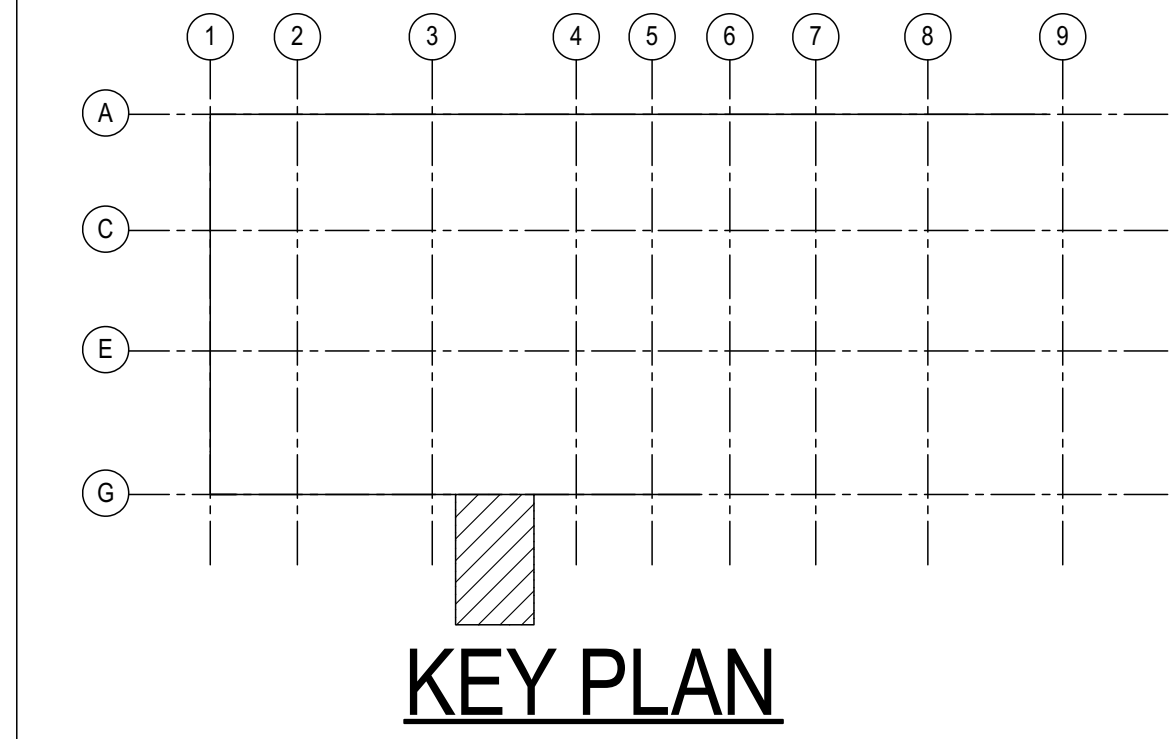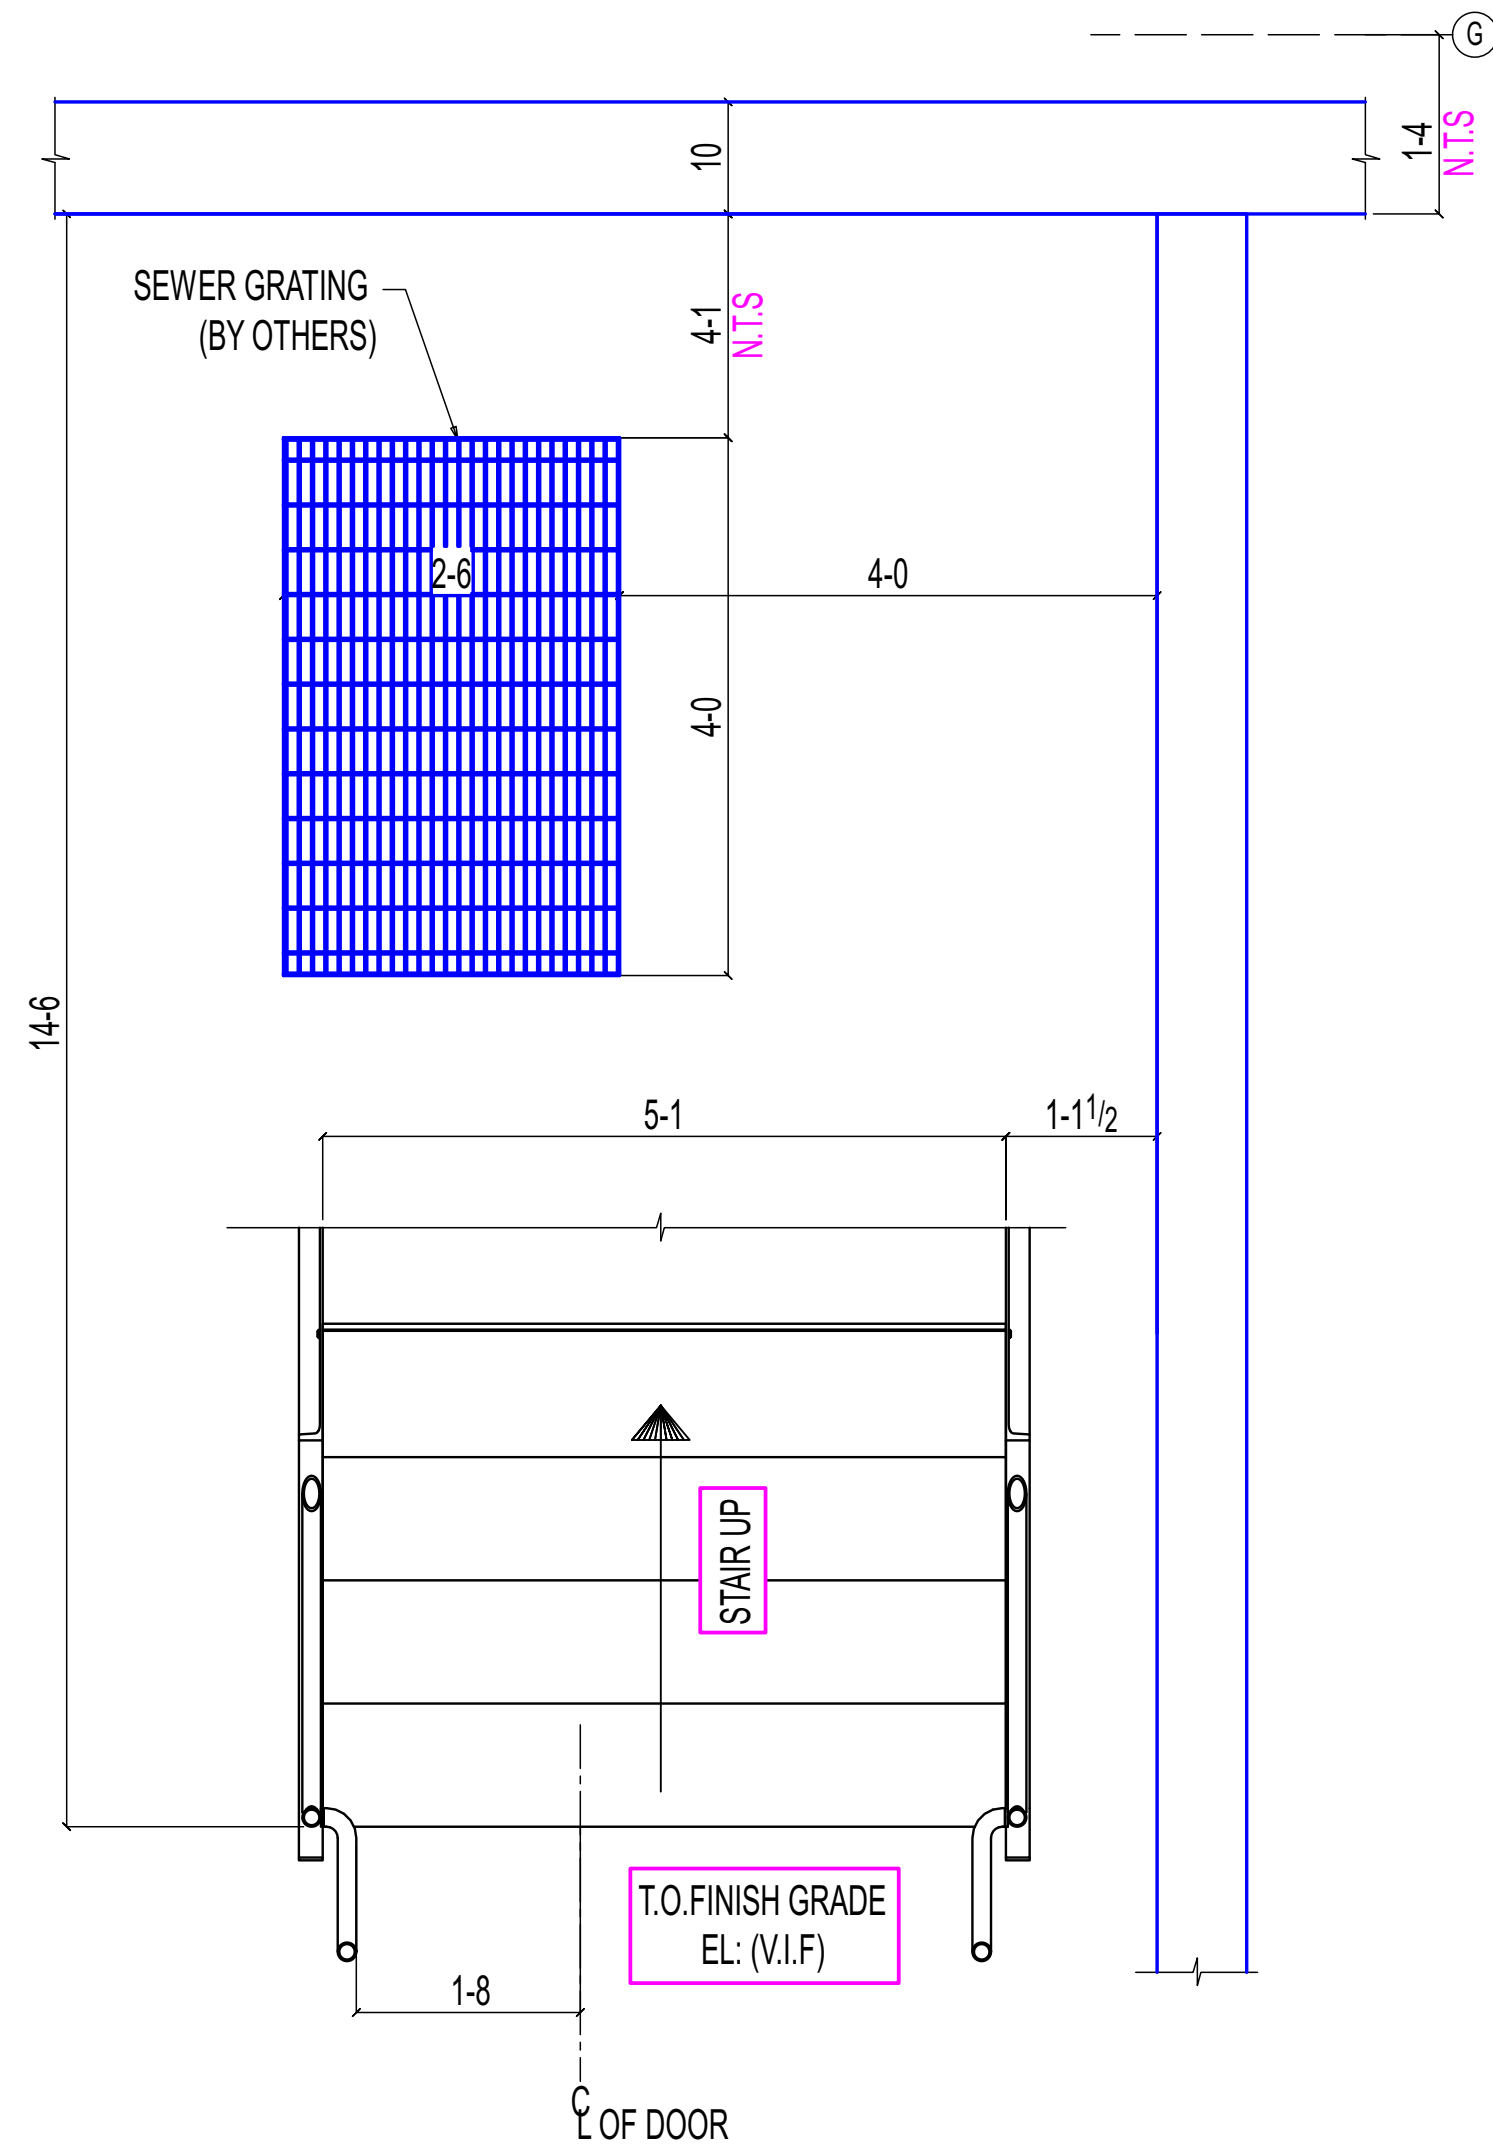


DESCRIPTION	SECTION SIZE
STAIR STRINGER	MC12x14.3
GUARDRAIL	PIPE 1 1/4 SCH40
HANDRAIL	PIPE 1 1/4 SCH40
GUARDRAIL POST	PIPE 1 1/4 SCH80

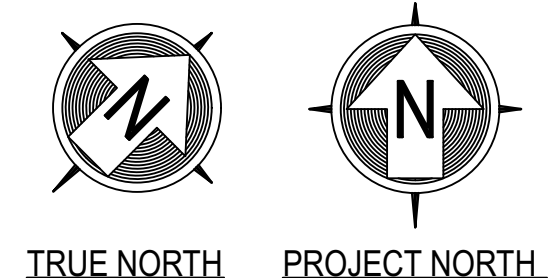

REVISIONS			
REV#	DWN BY	DESCRIPTION	DATE
A	SRP	ISSUED FOR APPROVAL	Jun 16 2025
B	SRP	ISSUED FOR RE-APPROVAL	Feb 18 2026

THE INFORMATION NOTED HEREON THIS DRAWING IS THE PROPERTY OF STEEL FAB ENTERPRISES, INC. AND SHALL NOTED BE USED WITHOUT WRITTEN CONSENT.

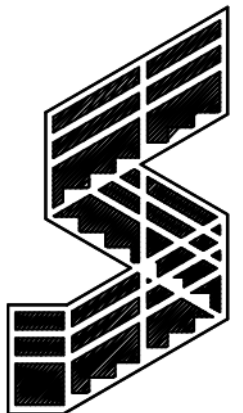

STEEL FAB ENTERPRISES, LLC
MISCELLANEOUS METALS FABRICATOR AND ERECTORS
623 BAUMGARDNER ROAD, LANCASTER, PA 17603
TEL. (717)464-0330 FAX (717)464-9464
WWW.STEELFABENTERPRISES.COM



CERTIFIED FABRICATOR AND DIRECTOR

PROJECT OWNER : CK CAPITAL, LLC
PROJECT DESCRIPTION : CLEVELAND BROTHERS-MILESBURG
PROJECT ADDRESS : 4025N. EAGLE VALLEY ROAD, HOWARD, PA 16841
CONTRACTOR : KINSLEY CONSTRUCTION, INC.

DRAWN BY : BAS	DATE : 5-20-25	PROJ. NO. : 25012	REV # B
CHECKED BY : SRP	DATE : 5-20-25	DWG NO. : E702	

DWG DESCRIPTION : DOCK STAIR FRAMING PLAN