



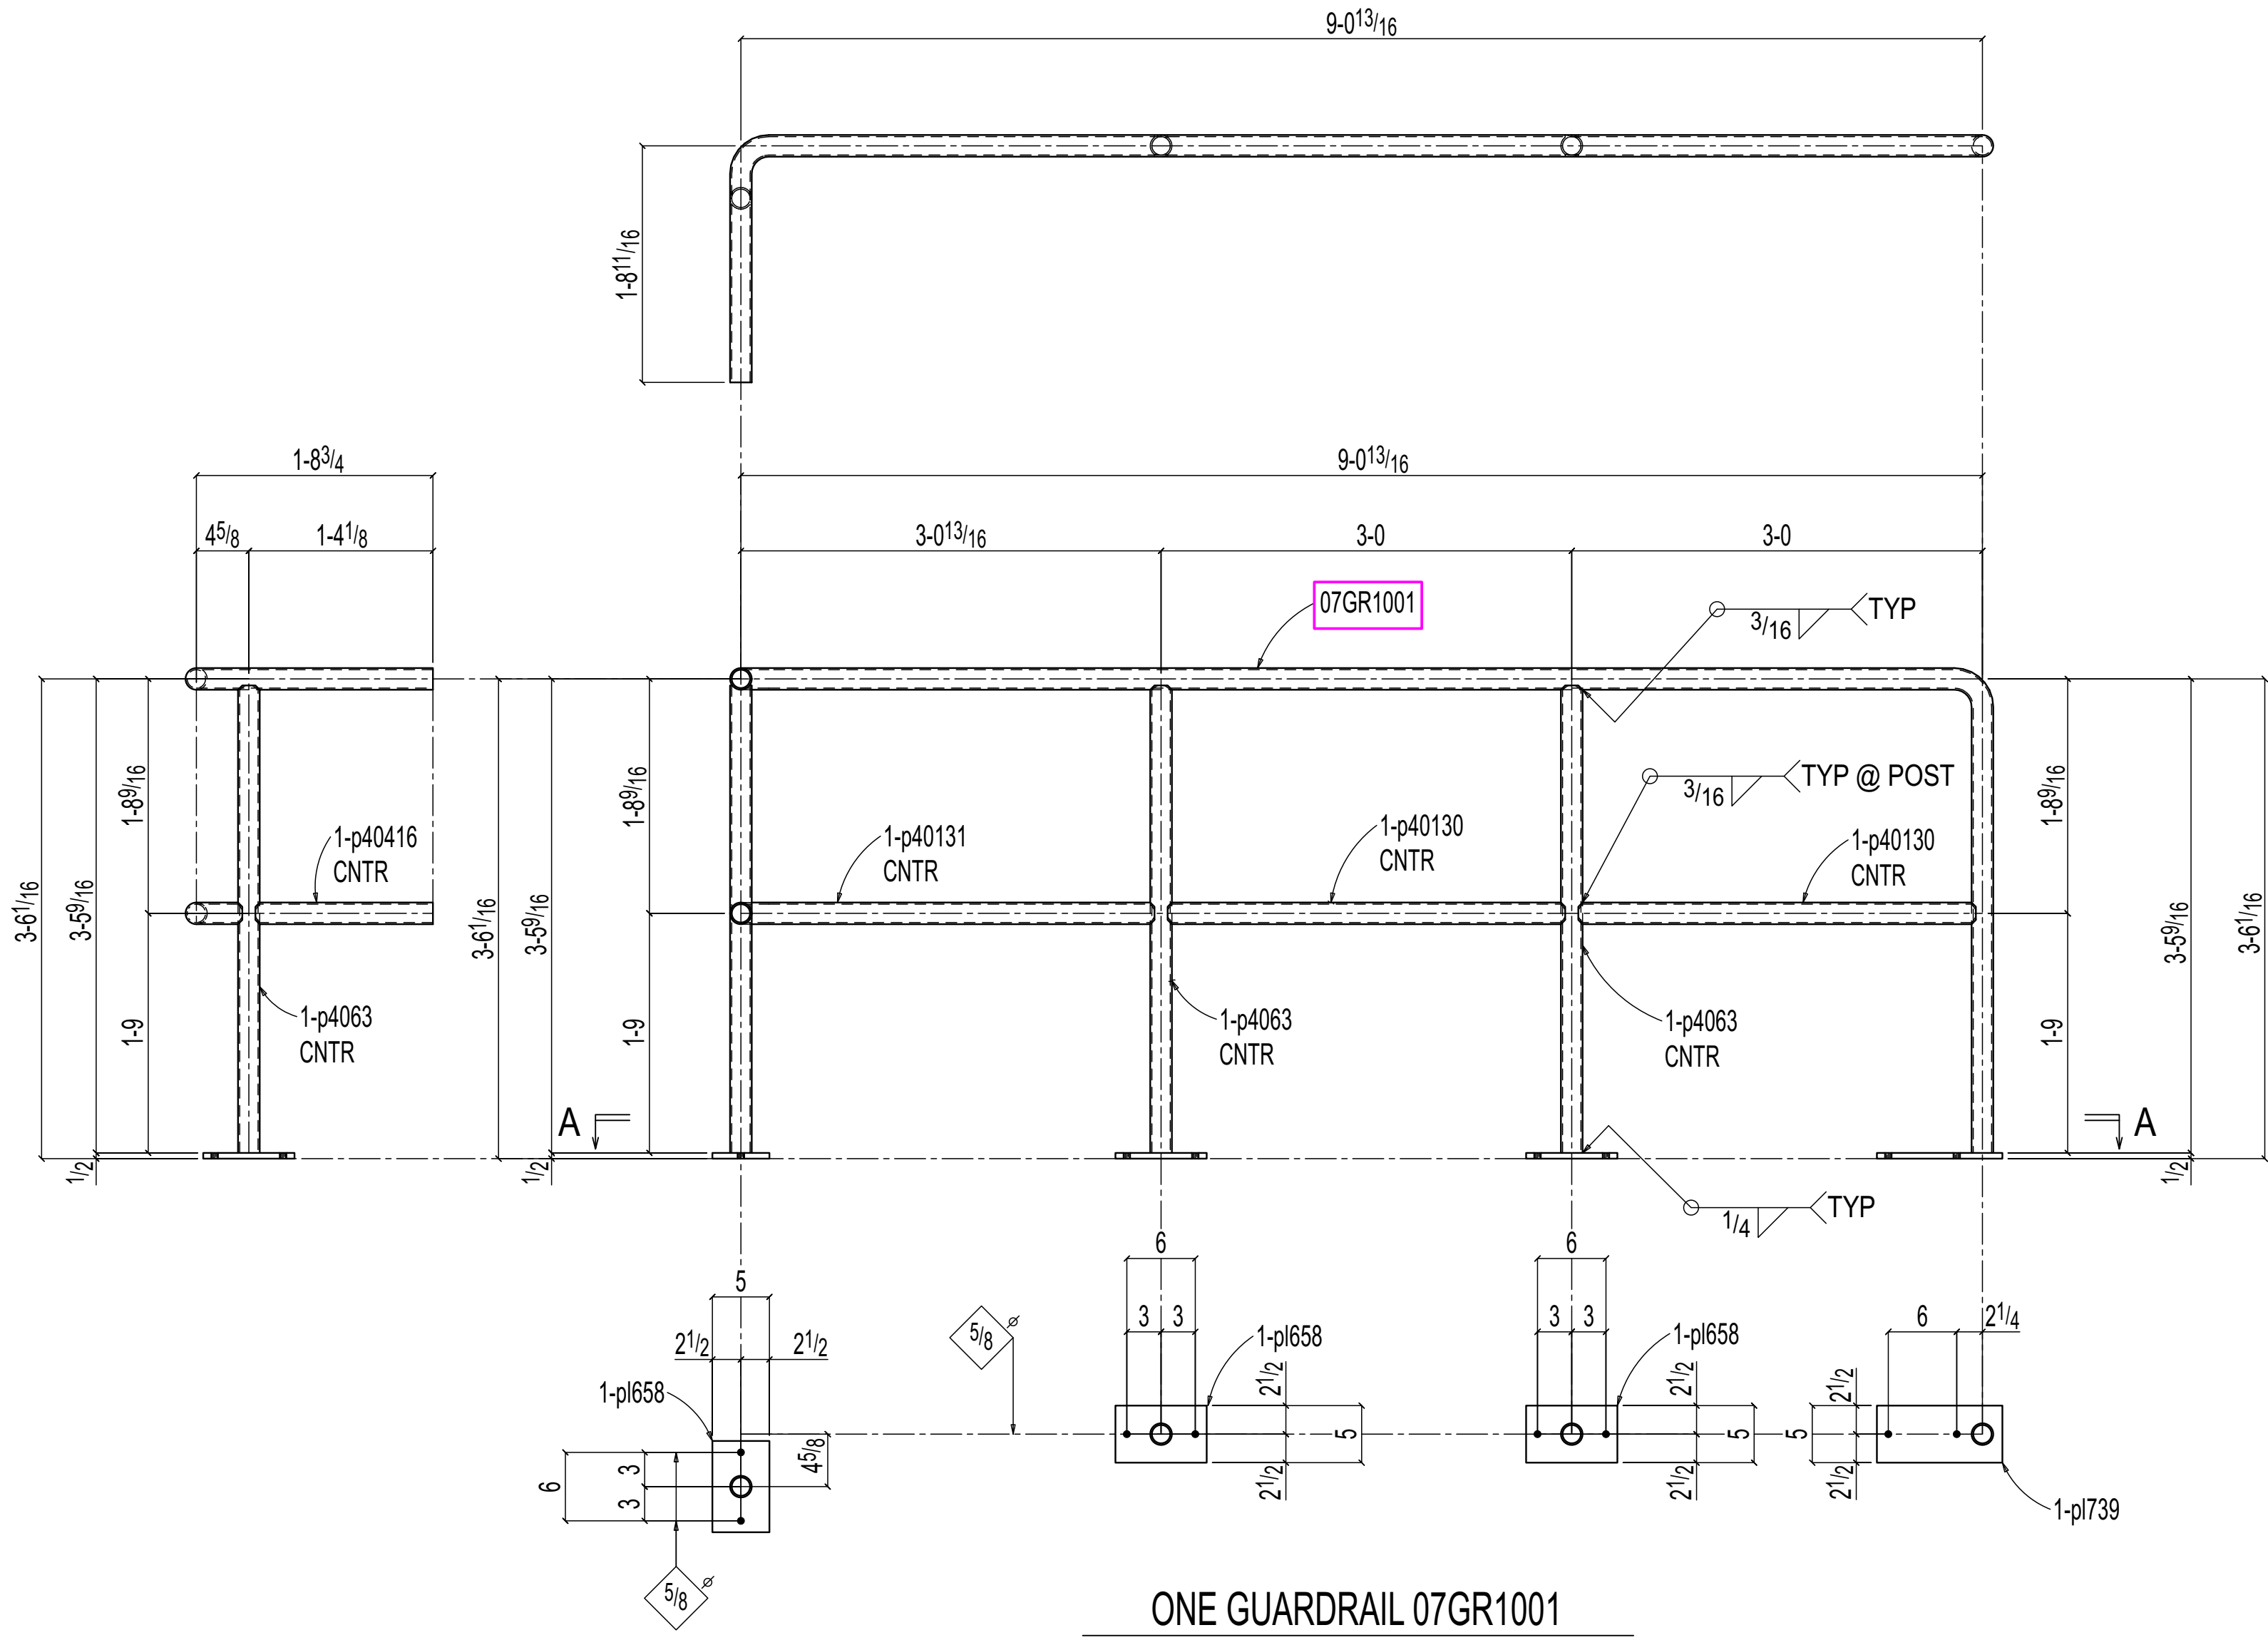

BILL OF MATERIAL									
ASSEMBLY	TOTAL	SUB-PIECE	UNIT	MATERIAL	LENGTH		REMARKS	UNIT	TOTAL
MARK	QTY	MARK	QTY	DESCRIPTION	FT	IN		WEIGHT	WEIGHT
07GR1001	ONE			GUARDRAIL			PNT	119	119
	1	07GR1001	1	PIPE 1 1/2 SCH40	14	1	A53 GR B (TYPE-S)	38	38
	3	p4063	3	PIPE 1 1/2 SCH40	3	5	A53 GR B (TYPE-S)	9	28
	1	p40131	1	PIPE 1 1/2 SCH40	3	3 1/4	A53 GR B (TYPE-S)	9	9
	2	p40130	2	PIPE 1 1/2 SCH40	2	10 7/8	A53 GR B (TYPE-S)	8	16
	1	p40416	1	PIPE 1 1/2 SCH40	1	39 1/16	A53 GR B	4	4
	1	p1739	1	PL 1/2x5	0	11	A36	8	8
	3	p1658	3	PL 1/2x5	0	8	A36	6	17
				FIELD BOLTS					
	8	m206		1/2 Dia HILTI KB-T22	0	33 3/4	+1HD WASH		
				EXPANSION ANCHOR					

Total weight : 119

THE INFORMATION NOTED HEREON THIS DRAWING IS THE
PROPERTY OF STEEL FAB ENTERPRISES, INC. AND SHALL
NOTED BE USED WITHOUT WRITTEN CONSENT.

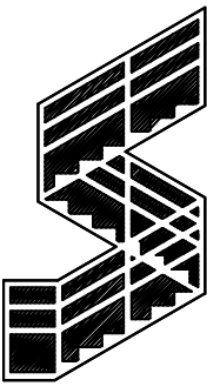

**STEEL FAB
ENTERPRISES, LLC**



MISCELLANEOUS METALS FABRICATOR AND ERECTORS
623 BAUMGARDNER ROAD, LANCASTER, PA 17603
TEL. (717)464-0330 FAX (717)464-9464
WWW.STEELFABENTERPRISES.COM

PROJECT OWNER : CK CAPITAL, LLC			
PROJECT DESCRIPTION : CLEVELAND BROTHERS-MILESBURG			
PROJECT ADDRESS : 1025N. EAGLE VALLY ROAD, HOWARD, PA 16841			
CONTRACTOR : KINSLEY CONSTRUCTION, INC.			
DRAWN BY : BAS	DATE : 06-07-2025	PROJ. NO. : 25012	REV # 
CHECKED BY : GSV	DATE : 06-09-2025	DWG NO. : 07GR1001	
DWG DESCRIPTION : GUARDRAIL DETAIL			

ALL RE-ENTRANT CUT
TO BE 1/2" RADIUS (U.N.O)
WELDS : E70XX
HOLES : 13/16" DIA (U.N.O)
MAT'L : A36 (U.N.O)
CLEAN : SSPC-SP3
PAINT : SHOP PRIMER

REVISIONS

REV	DWN BY	DATE	DESCRIPTION
A	GSV	Jun 16 2025	ISSUED FOR APPROVAL
0	GSV	Jan 27 2026	ISSUED FOR FABRICATION
B	GSV	Feb 23 2026	ISSUED FOR RE-APPROVAL
1	GSV	Mar 11 2026	ISSUED FOR FABRICATION