


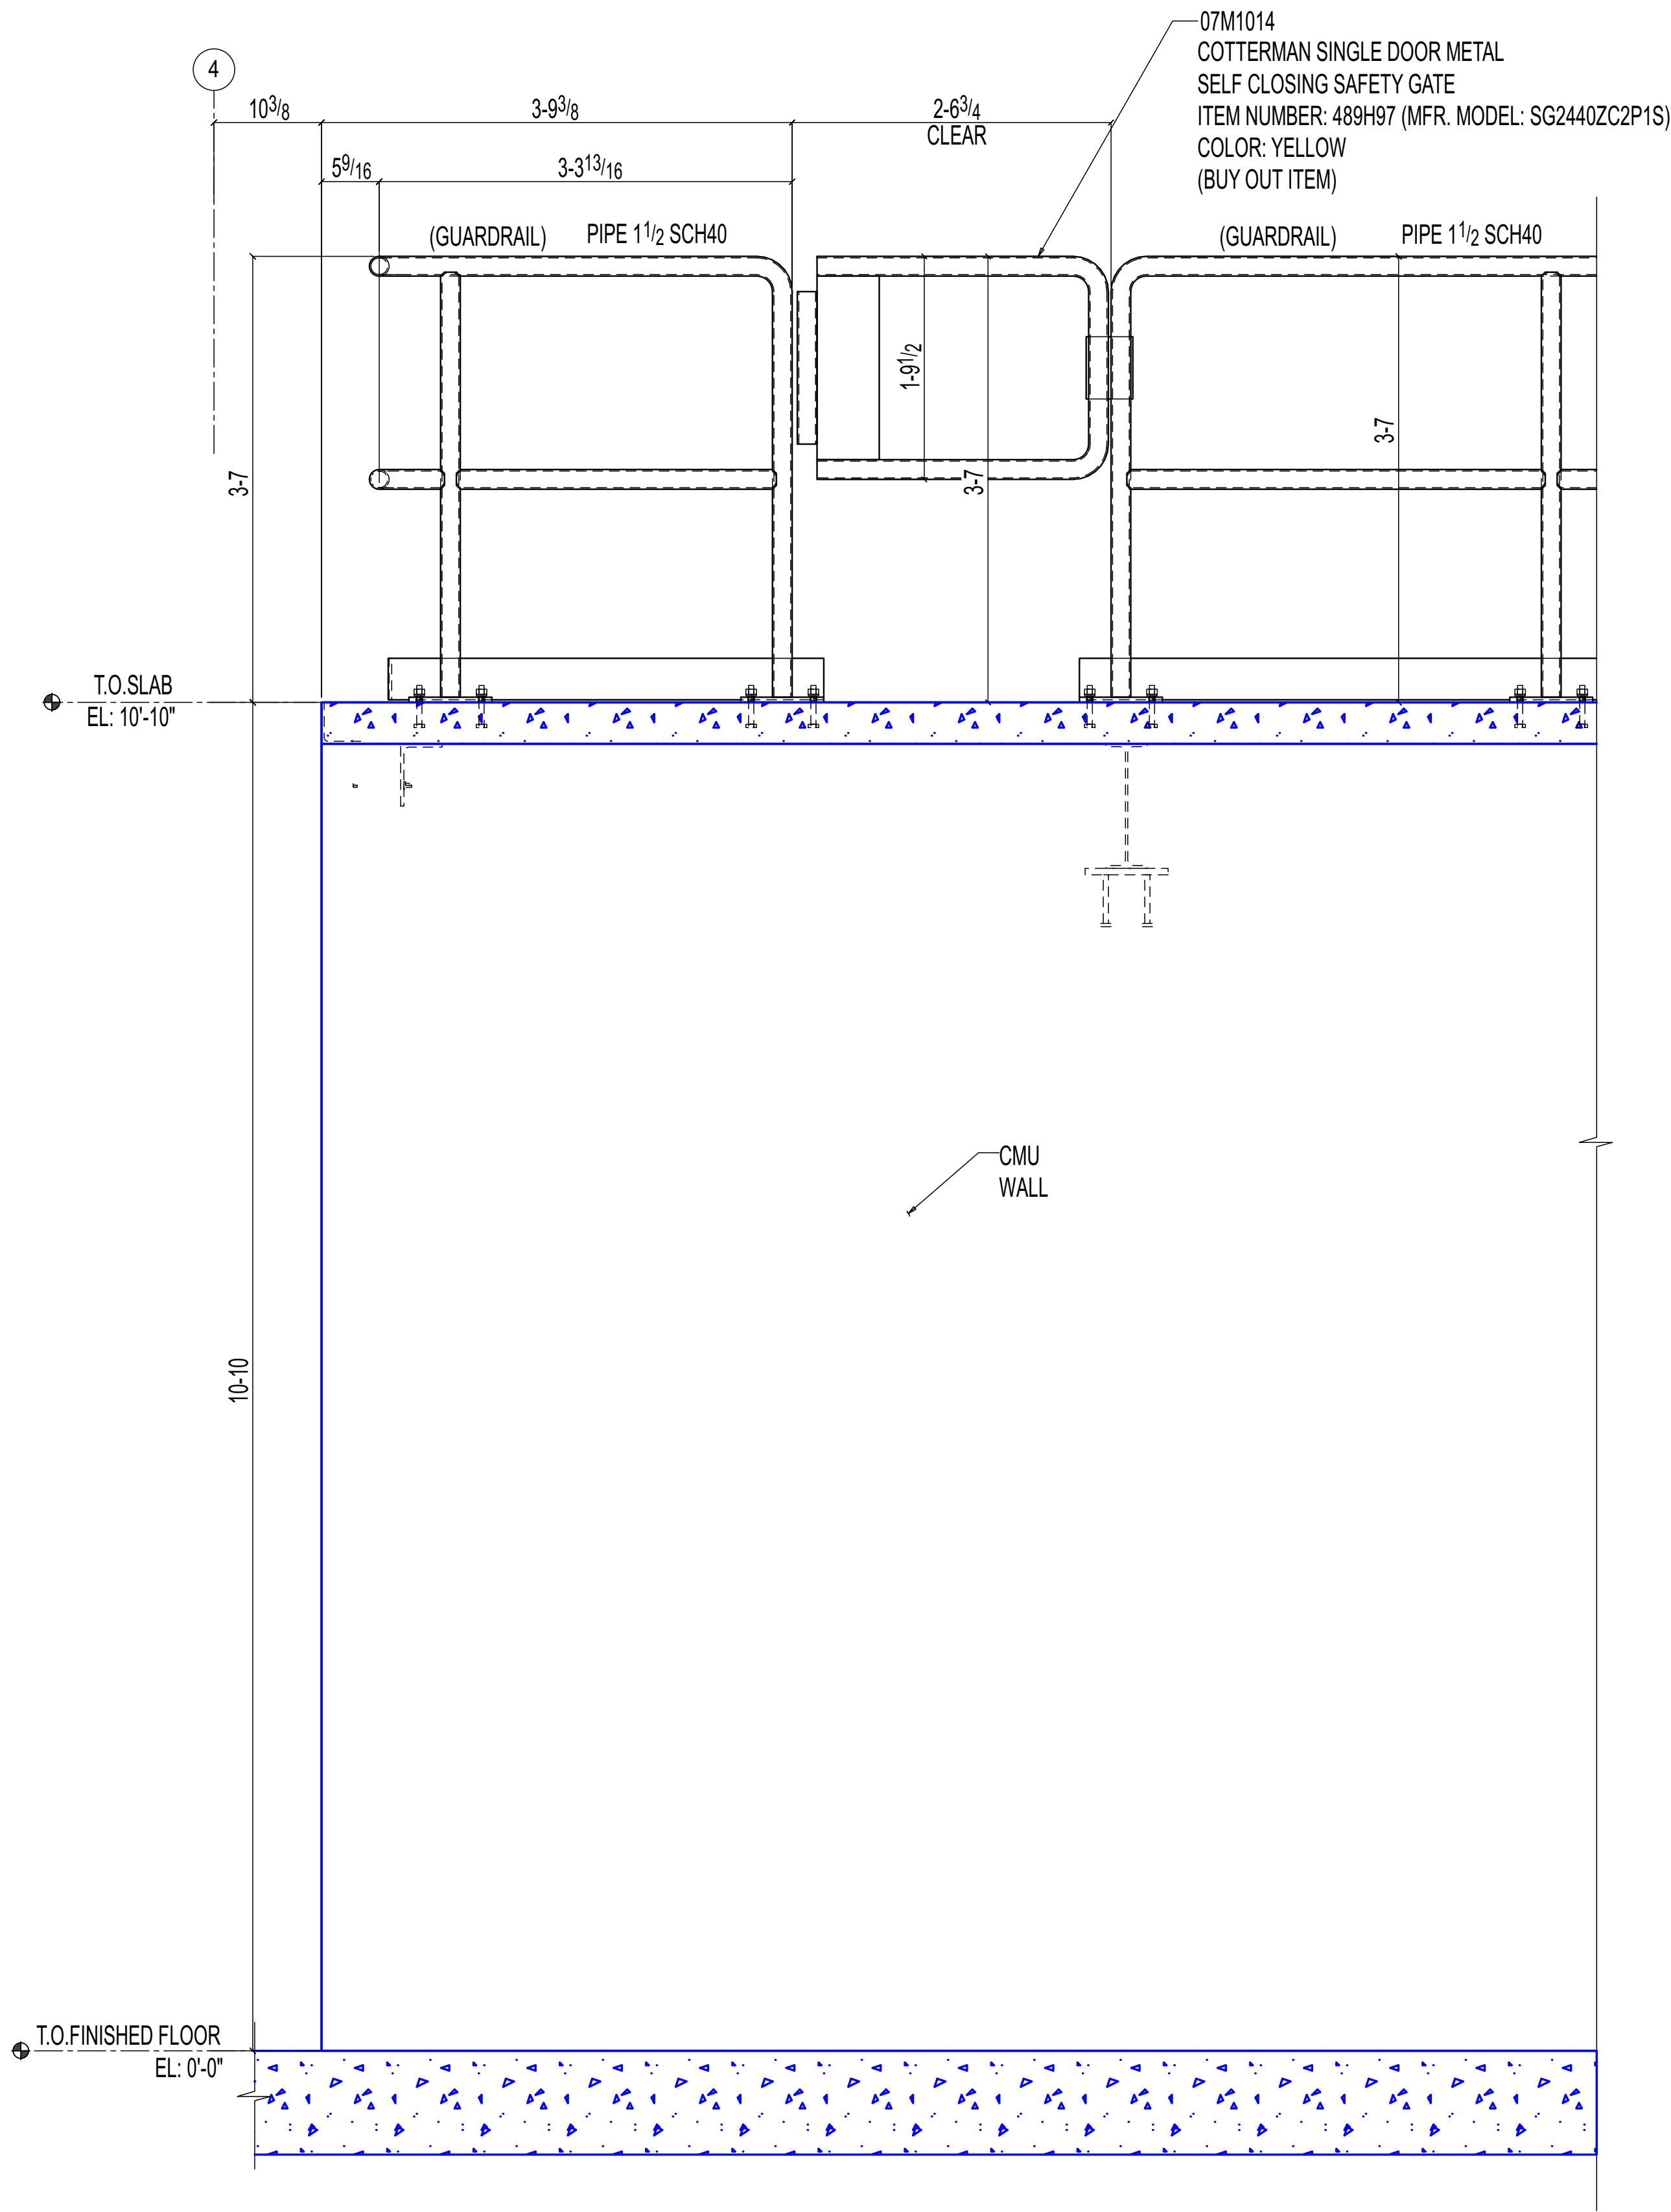


1 ELEVATION
SE713 OTHERS NOT SHOWN FOR CLARITY

NOT IN USE

2 SECTION
SE713 OTHERS NOT SHOWN FOR CLARITY

REVISIONS			
REV#	DWN BY	DESCRIPTION	DATE
A	SRP	ISSUED FOR APPROVAL	Jun 16 2025
0	GSV	ISSUED FOR CONSTRUCTION	Jan 27 2026
1	GSV	REVISED AS NOTED	Mar 6 2026

THE INFORMATION NOTED HEREON THIS DRAWING IS THE PROPERTY OF STEEL FAB ENTERPRISES, INC. AND SHALL NOTED BE USED WITHOUT WRITTEN CONSENT.

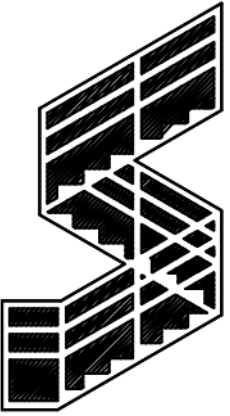

STEEL FAB ENTERPRISES, LLC

MISCELLANEOUS METALS FABRICATOR AND ERECTORS
623 BAUMGARDNER ROAD, LANCASTER, PA 17603
TEL. (717)464-0330 FAX (717)464-9464
WWW.STEELFABENTERPRISES.COM



CERTIFIED FABRICATOR AND ERECTOR

PROJECT OWNER : CK CAPITAL, LLC			
PROJECT DESCRIPTION : CLEVELAND BROTHERS-MILESBURG			
PROJECT ADDRESS : 4025N. EAGLE VALLEY ROAD, HOWARD, PA 16841			
CONTRACTOR : KINSLEY CONSTRUCTION, INC.			
DRAWN BY : BAS	DATE : 5-20-25	PROJ. NO. : 25012	REV # 
CHECKED BY : SRP	DATE : 5-20-25	DWG NO. : SE713	
DWG DESCRIPTION : LADDER ELEVATION VIEW			