

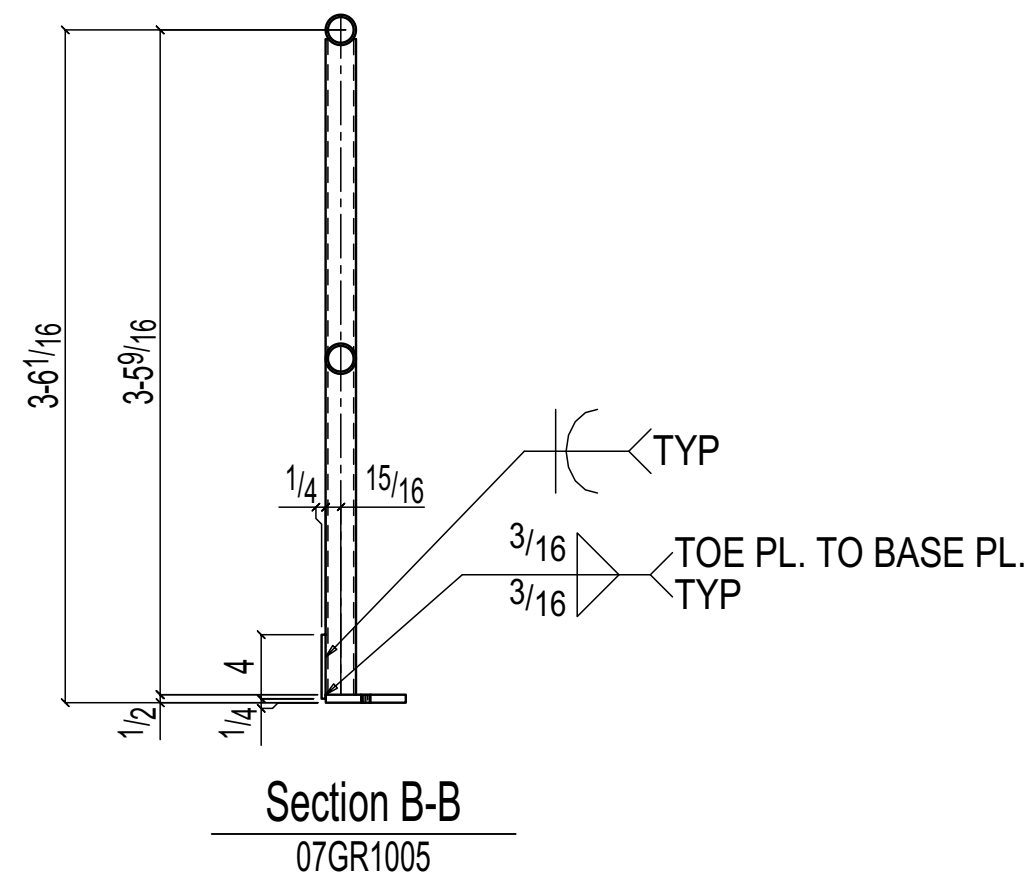


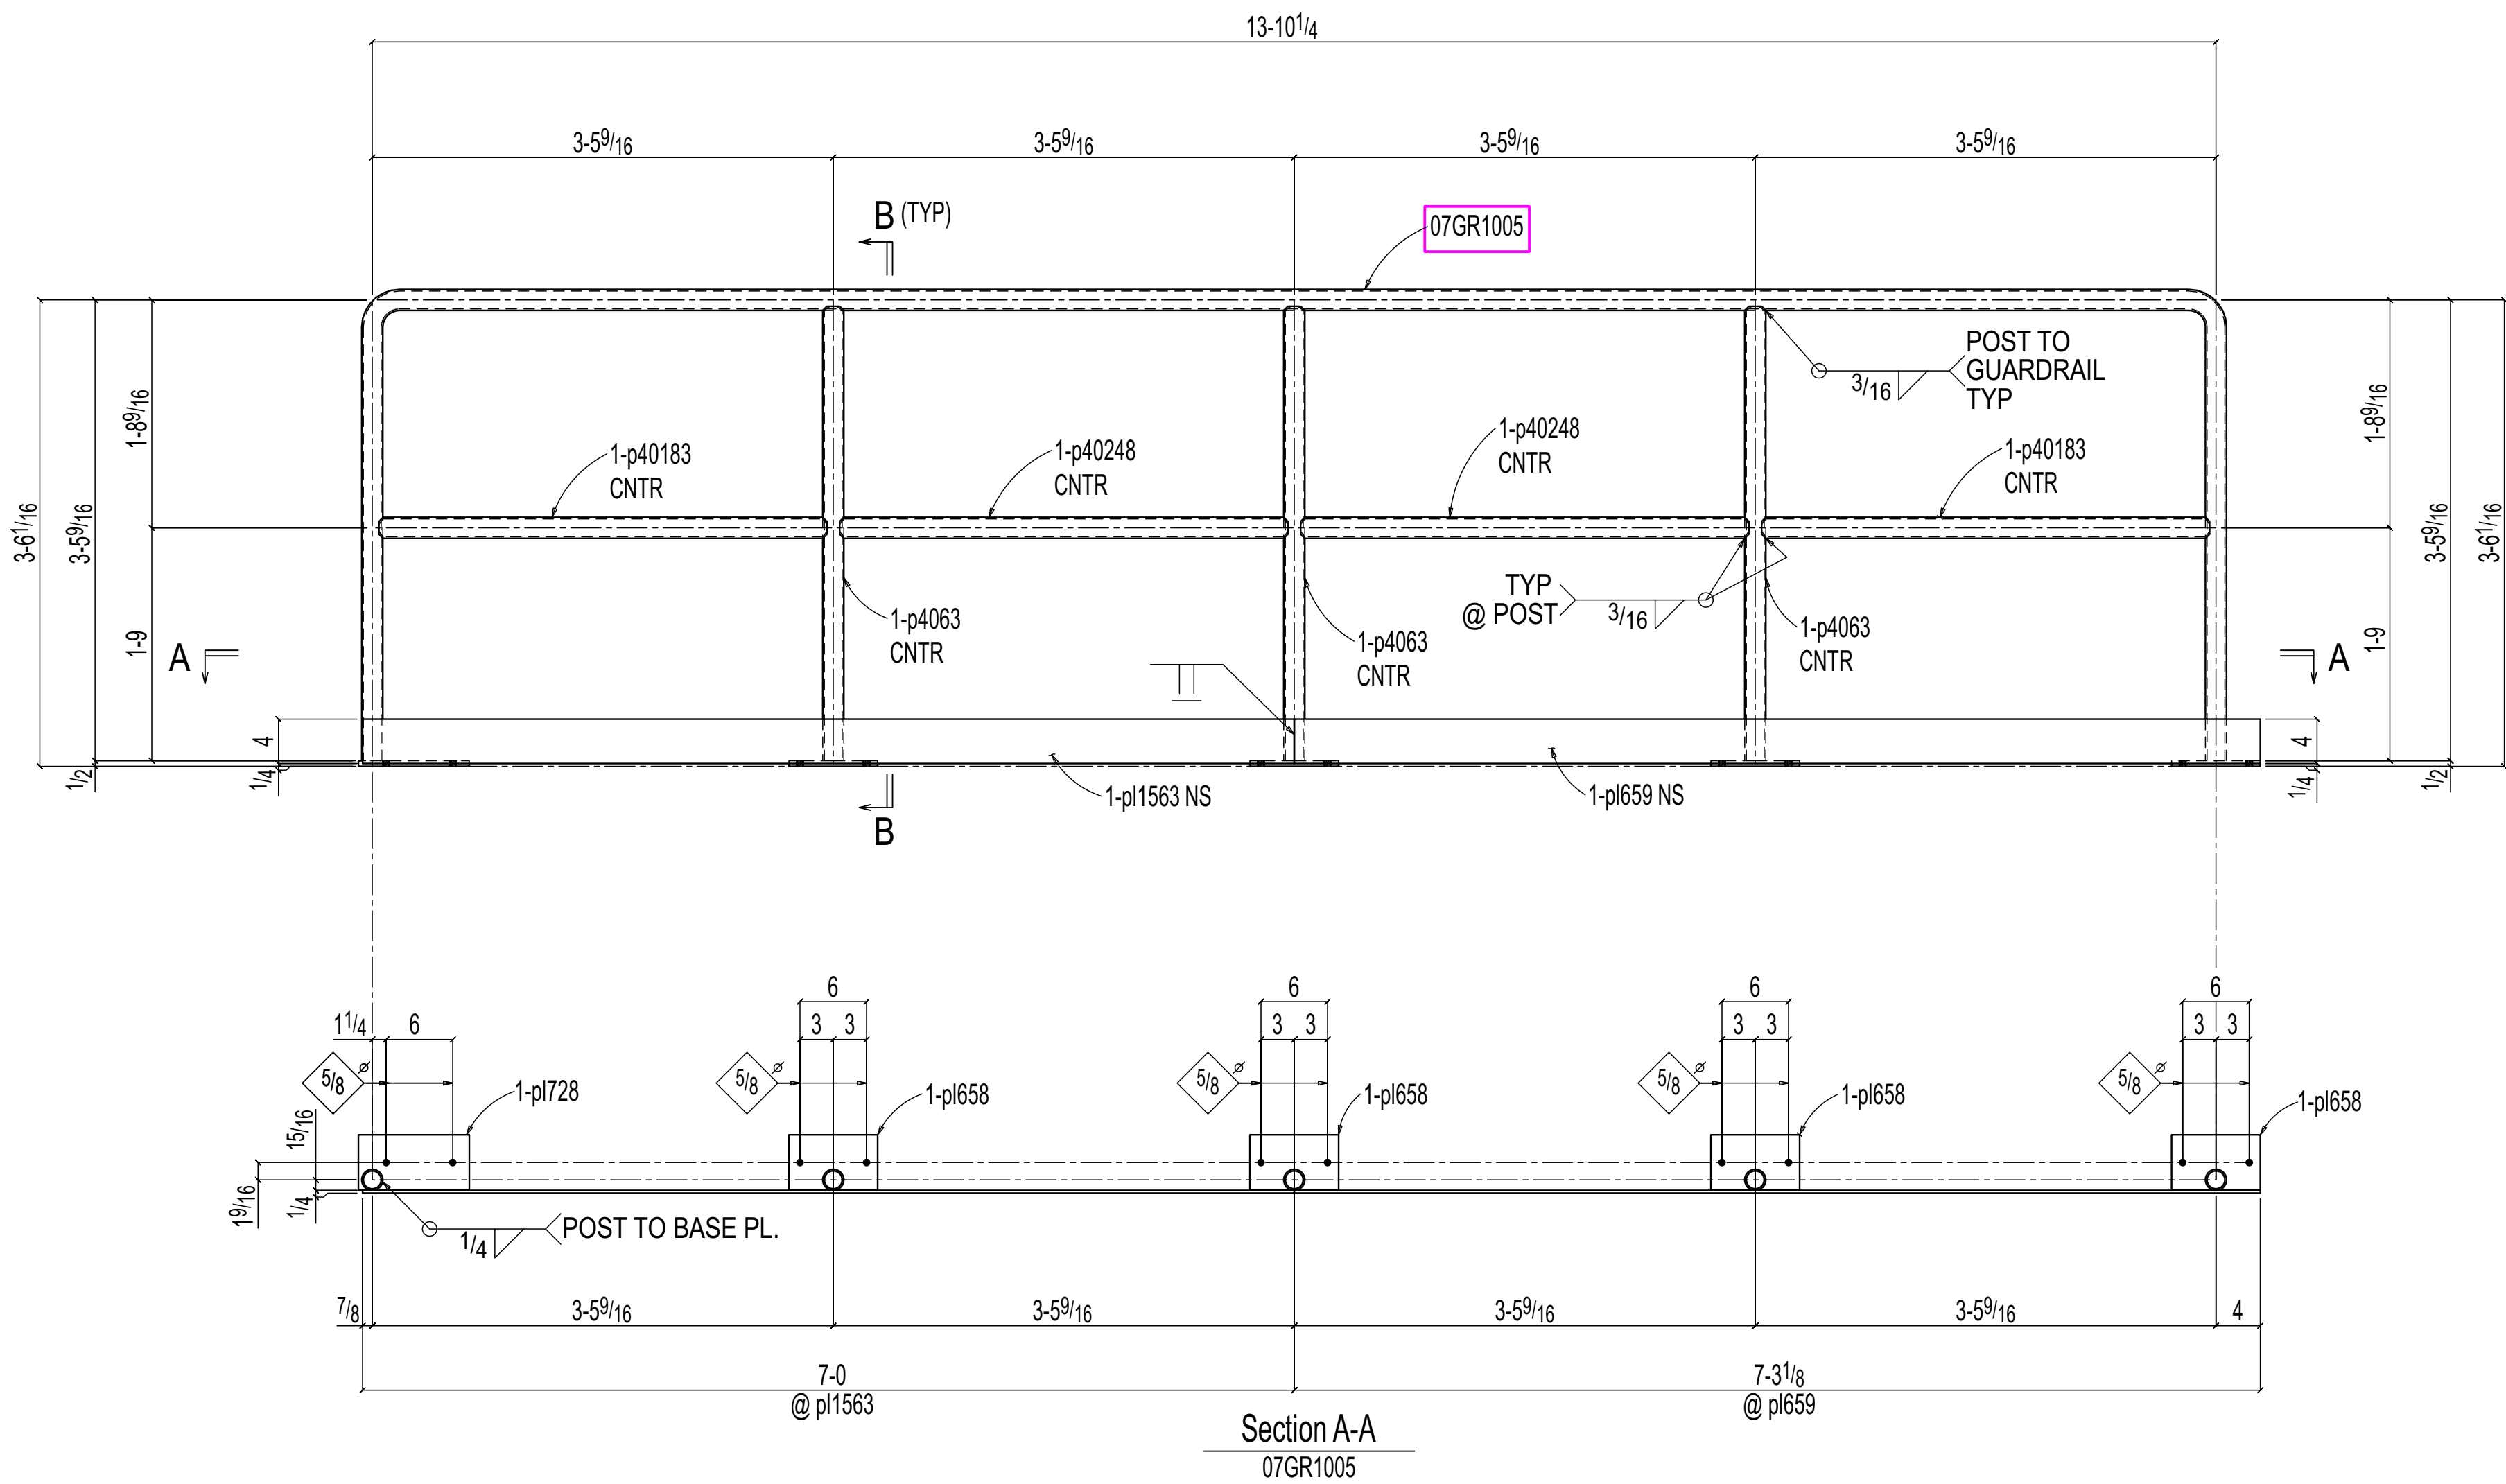

| BILL OF MATERIAL |       |           |      |                      |        |        |                   |        |        |
|------------------|-------|-----------|------|----------------------|--------|--------|-------------------|--------|--------|
| ASSEMBLY         | TOTAL | SUB-PIECE | UNIT | MATERIAL             | LENGTH |        | REMARKS           | UNIT   | TOTAL  |
| MARK             | QTY   | MARK      | QTY  | DESCRIPTION          | FT     | IN     |                   | WEIGHT | WEIGHT |
| 07GR1005         | ONE   |           |      | GUARDRAIL            |        |        | PNT               | 199    | 199    |
|                  | 1     | 07GR1005  | 1    | PIPE 1 1/2 SCH40     | 20     | 7 3/16 | A53 GR B (TYPE-S) | 56     | 56     |
|                  | 3     | p4083     | 3    | PIPE 1 1/2 SCH40     | 3      | 5      | A53 GR B (TYPE-S) | 9      | 28     |
|                  | 2     | p40248    | 2    | PIPE 1 1/2 SCH40     | 3      | 47/16  | A53 GR B (TYPE-S) | 9      | 18     |
|                  | 2     | p40183    | 2    | PIPE 1 1/2 SCH40     | 3      | 43/8   | A53 GR B (TYPE-S) | 9      | 18     |
|                  | 1     | p728      | 1    | PL 1/2x5             | 0      | 10     | A36               | 7      | 7      |
|                  | 4     | p658      | 4    | PL 1/2x5             | 0      | 8      | A36               | 6      | 23     |
|                  | 1     | p659      | 1    | PL 1/4x4             | 7      | 3 1/8  | A36               | 25     | 25     |
|                  | 1     | p1563     | 1    | PL 1/4x4             | 7      | 0      | A36               | 24     | 24     |
|                  |       |           |      | FIELD BOLTS          |        |        |                   |        |        |
|                  | 10    | m206      |      | 1/2 Dia HILTI KB-T22 | 0      | 3 3/4  | +1HD WASH         |        |        |
|                  |       |           |      | EXPANSION ANCHOR     |        |        |                   |        |        |

Total weight : 199

THE INFORMATION NOTED HEREON THIS DRAWING IS THE PROPERTY OF STEEL FAB ENTERPRISES, INC. AND SHALL NOTED BE USED WITHOUT WRITTEN CONSENT.

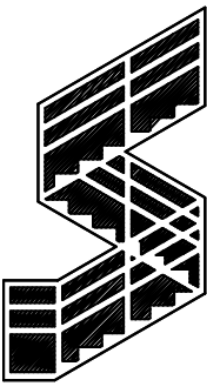

STEEL FAB  
ENTERPRISES, LLC

MISCELLANEOUS METALS FABRICATOR AND ERECTORS  
623 BAUMGARDNER ROAD, LANCASTER, PA 17603  
TEL. (717)464-0330      FAX (717)464-9464  
WWW.STEELFABENTERPRISES.COM



PROJECT OWNER : CK CAPITAL, LLC  
PROJECT DESCRIPTION : CLEVELAND BROTHERS-MILESBURG  
PROJECT ADDRESS : 1025N. EAGLE VALLY ROAD, HOWARD, PA 16841

|                                         |  |                   |  |                  |                                                                                                |
|-----------------------------------------|--|-------------------|--|------------------|------------------------------------------------------------------------------------------------|
| CONTRACTOR : KINSLEY CONSTRUCTION, INC. |  |                   |  |                  |                                                                                                |
| DRAWN BY : BAS                          |  | DATE : 06-07-2025 |  | PROJ. NO.: 25012 | REV #<br> |
| CHECKED BY : GSV                        |  | DATE : 06-09-2025 |  |                  |                                                                                                |
| DWG DESCRIPTION : GUARDRAIL DETAIL      |  |                   |  |                  |                                                                                                |

ALL RE-ENTRANT CUT  
TO BE 1/2" RADIUSED (U.N.O)  
WELDS : E70XX  
HOLES : 13/16" DIA (U.N.O)  
MAT'L : A36 (U.N.O)  
CLEAN : SSPC-SP3  
PAINT : SHOP PRIMER

REVISIONS

| REV | DWN BY | DATE        | DESCRIPTION            |
|-----|--------|-------------|------------------------|
| A   | GSV    | Jun 16 2025 | ISSUED FOR APPROVAL    |
| 0   | GSV    | Jan 27 2026 | ISSUED FOR FABRICATION |
| 1   | GSV    | Feb 5 2026  | ISSUED FOR FABRICARION |
|     |        |             |                        |
|     |        |             |                        |