




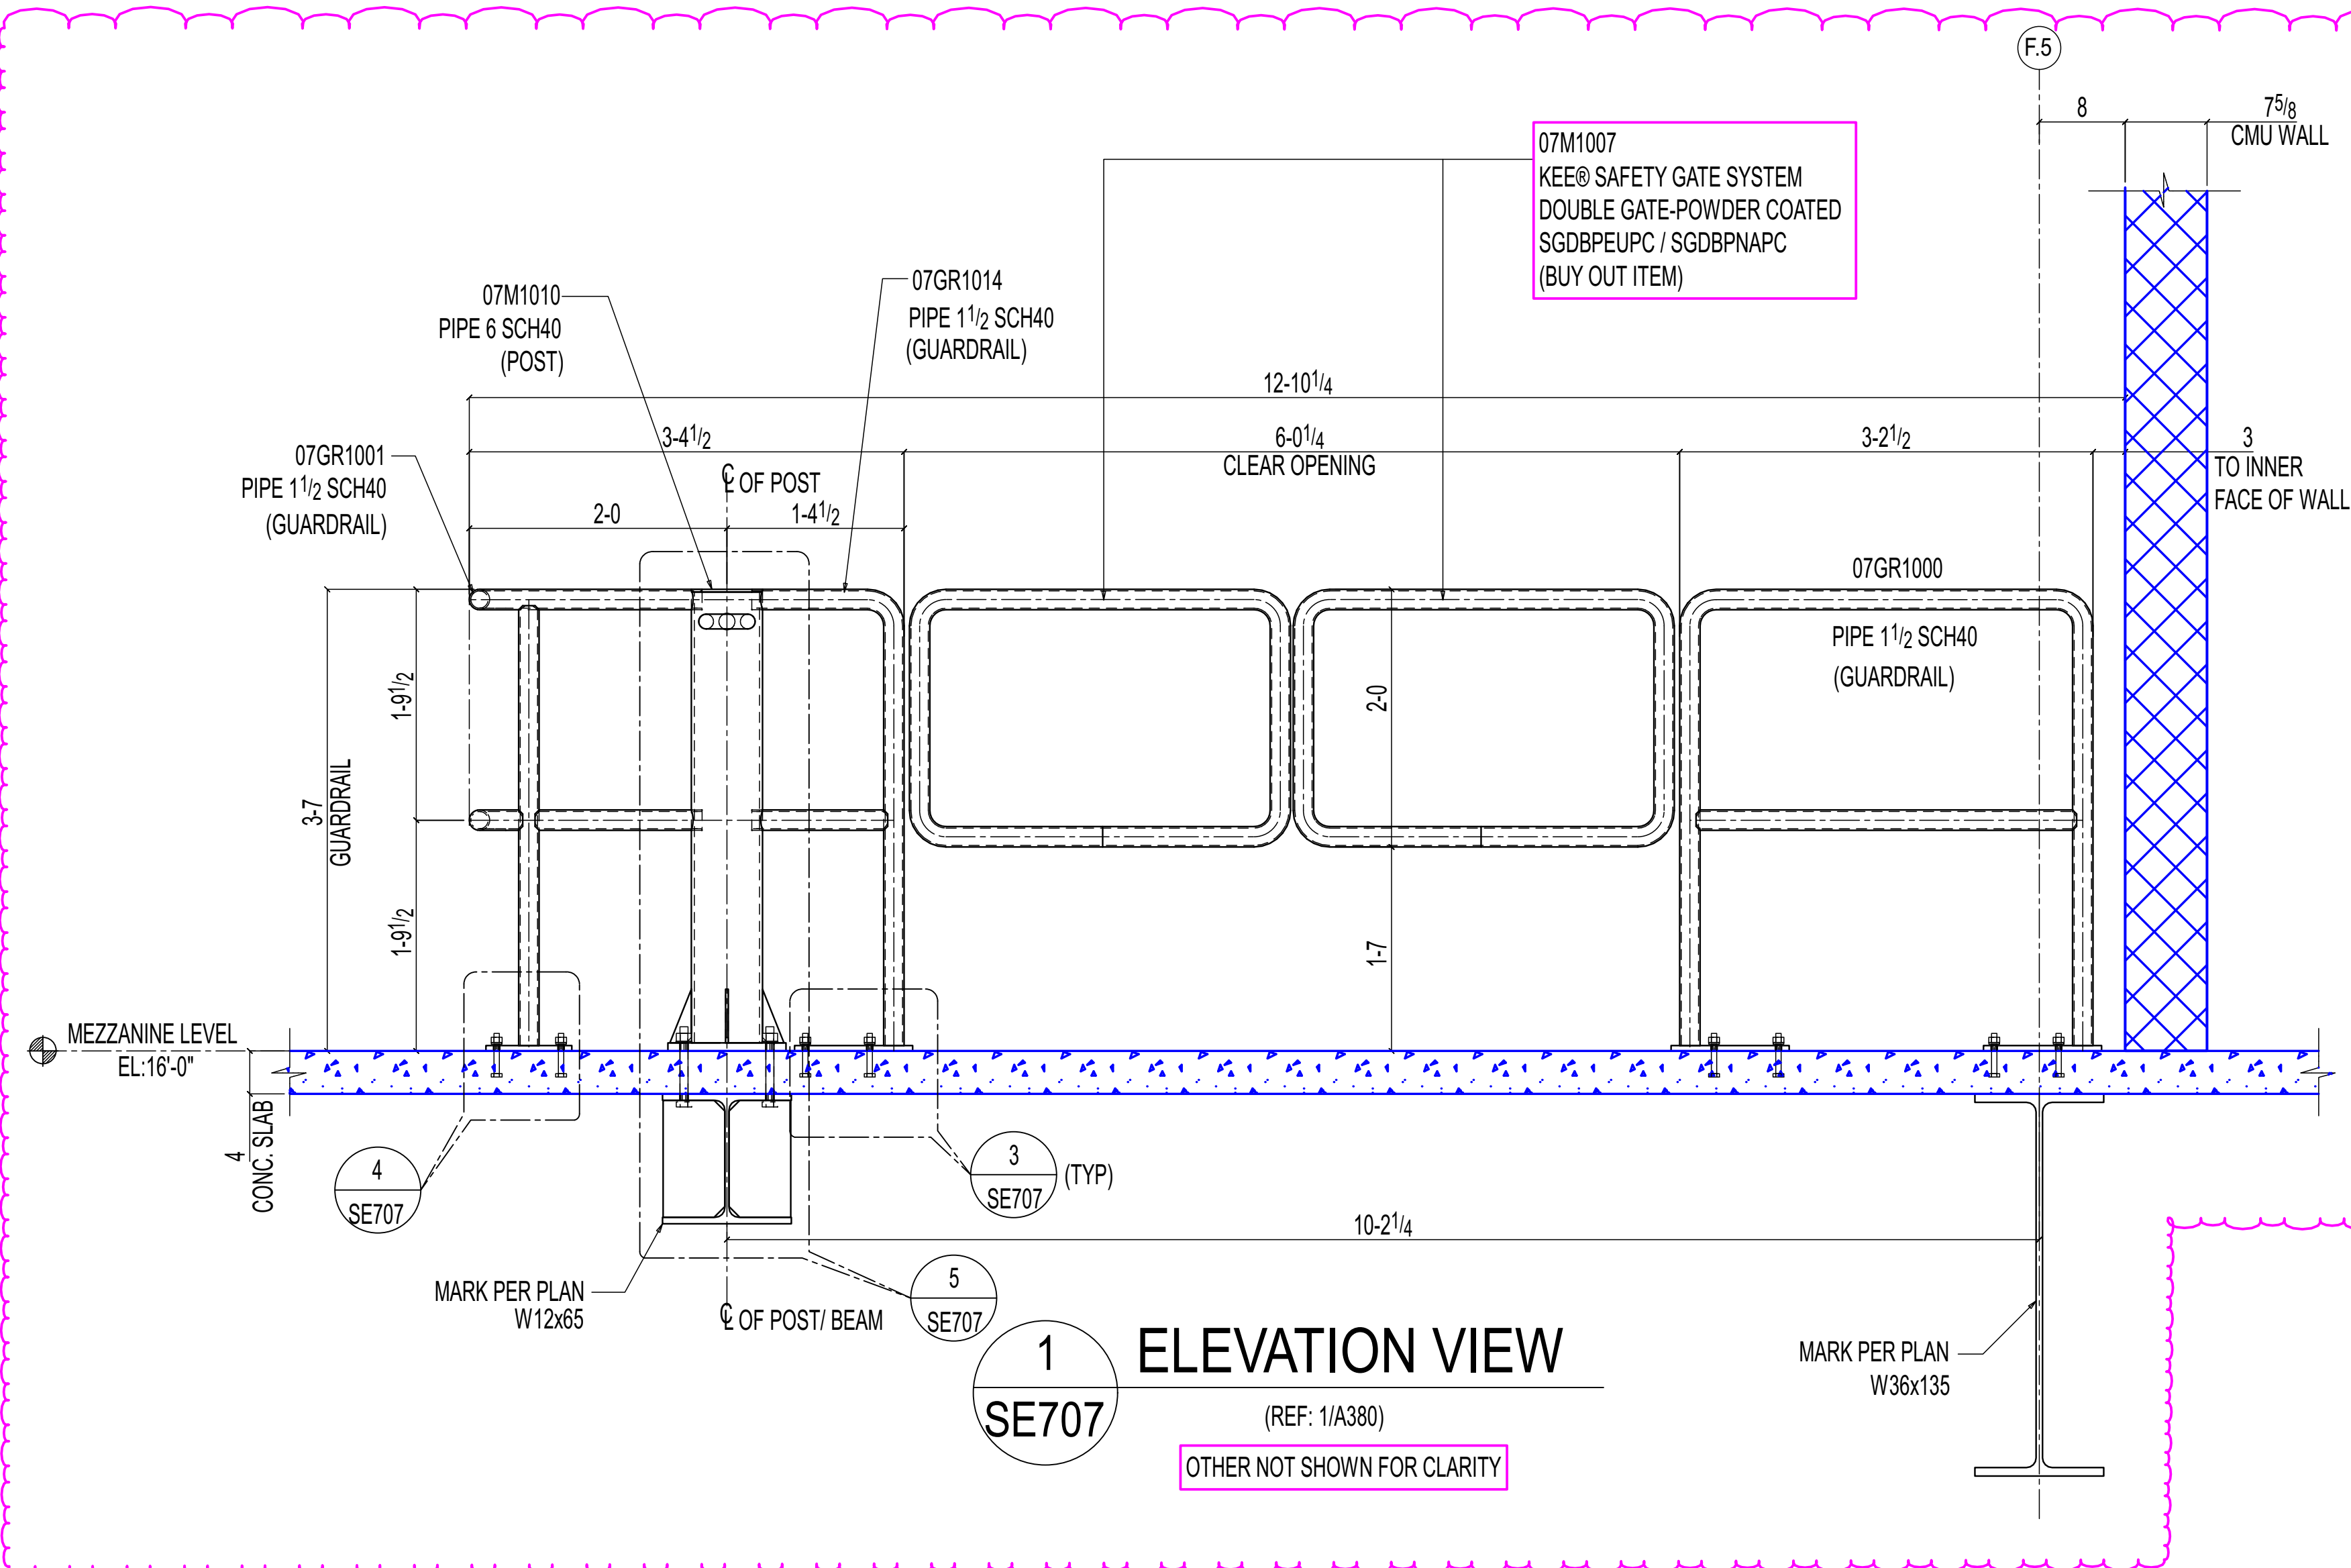


1 ELEVATION VIEW
(REF: 1/A380)
OTHER NOT SHOWN FOR CLARITY

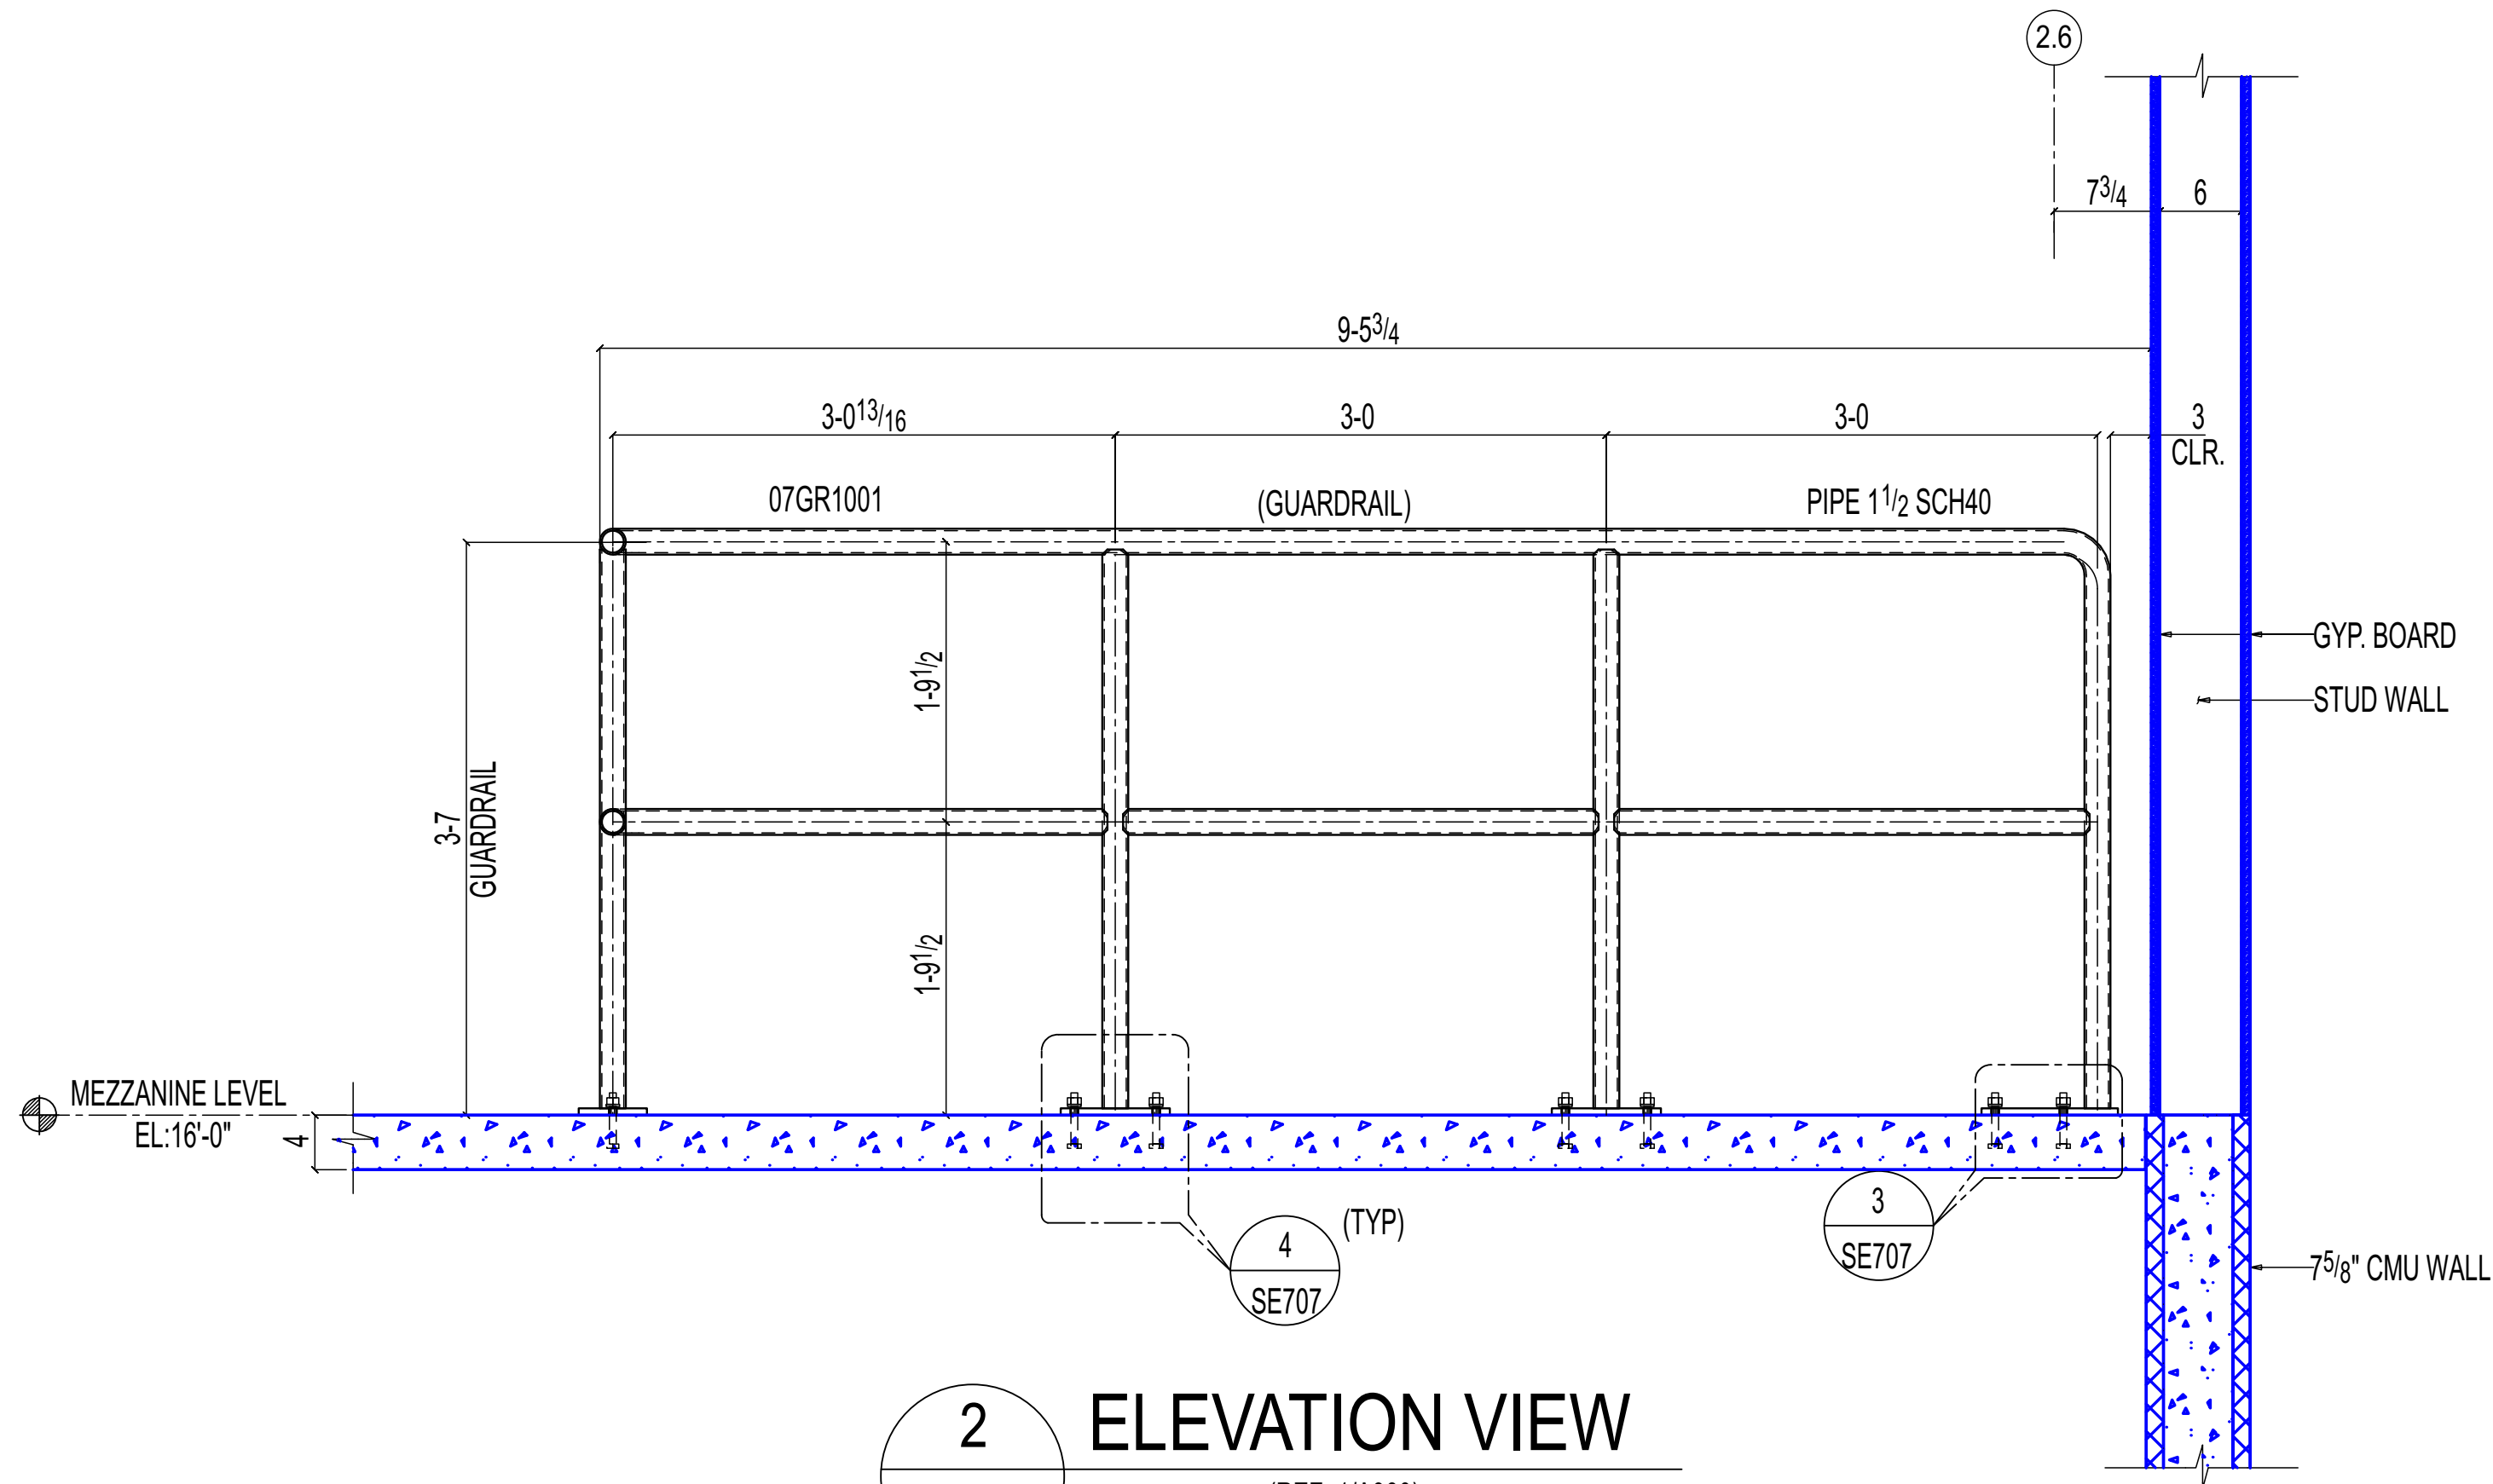


2 ELEVATION VIEW
(REF: 1/A380)
OTHER NOT SHOWN FOR CLARITY

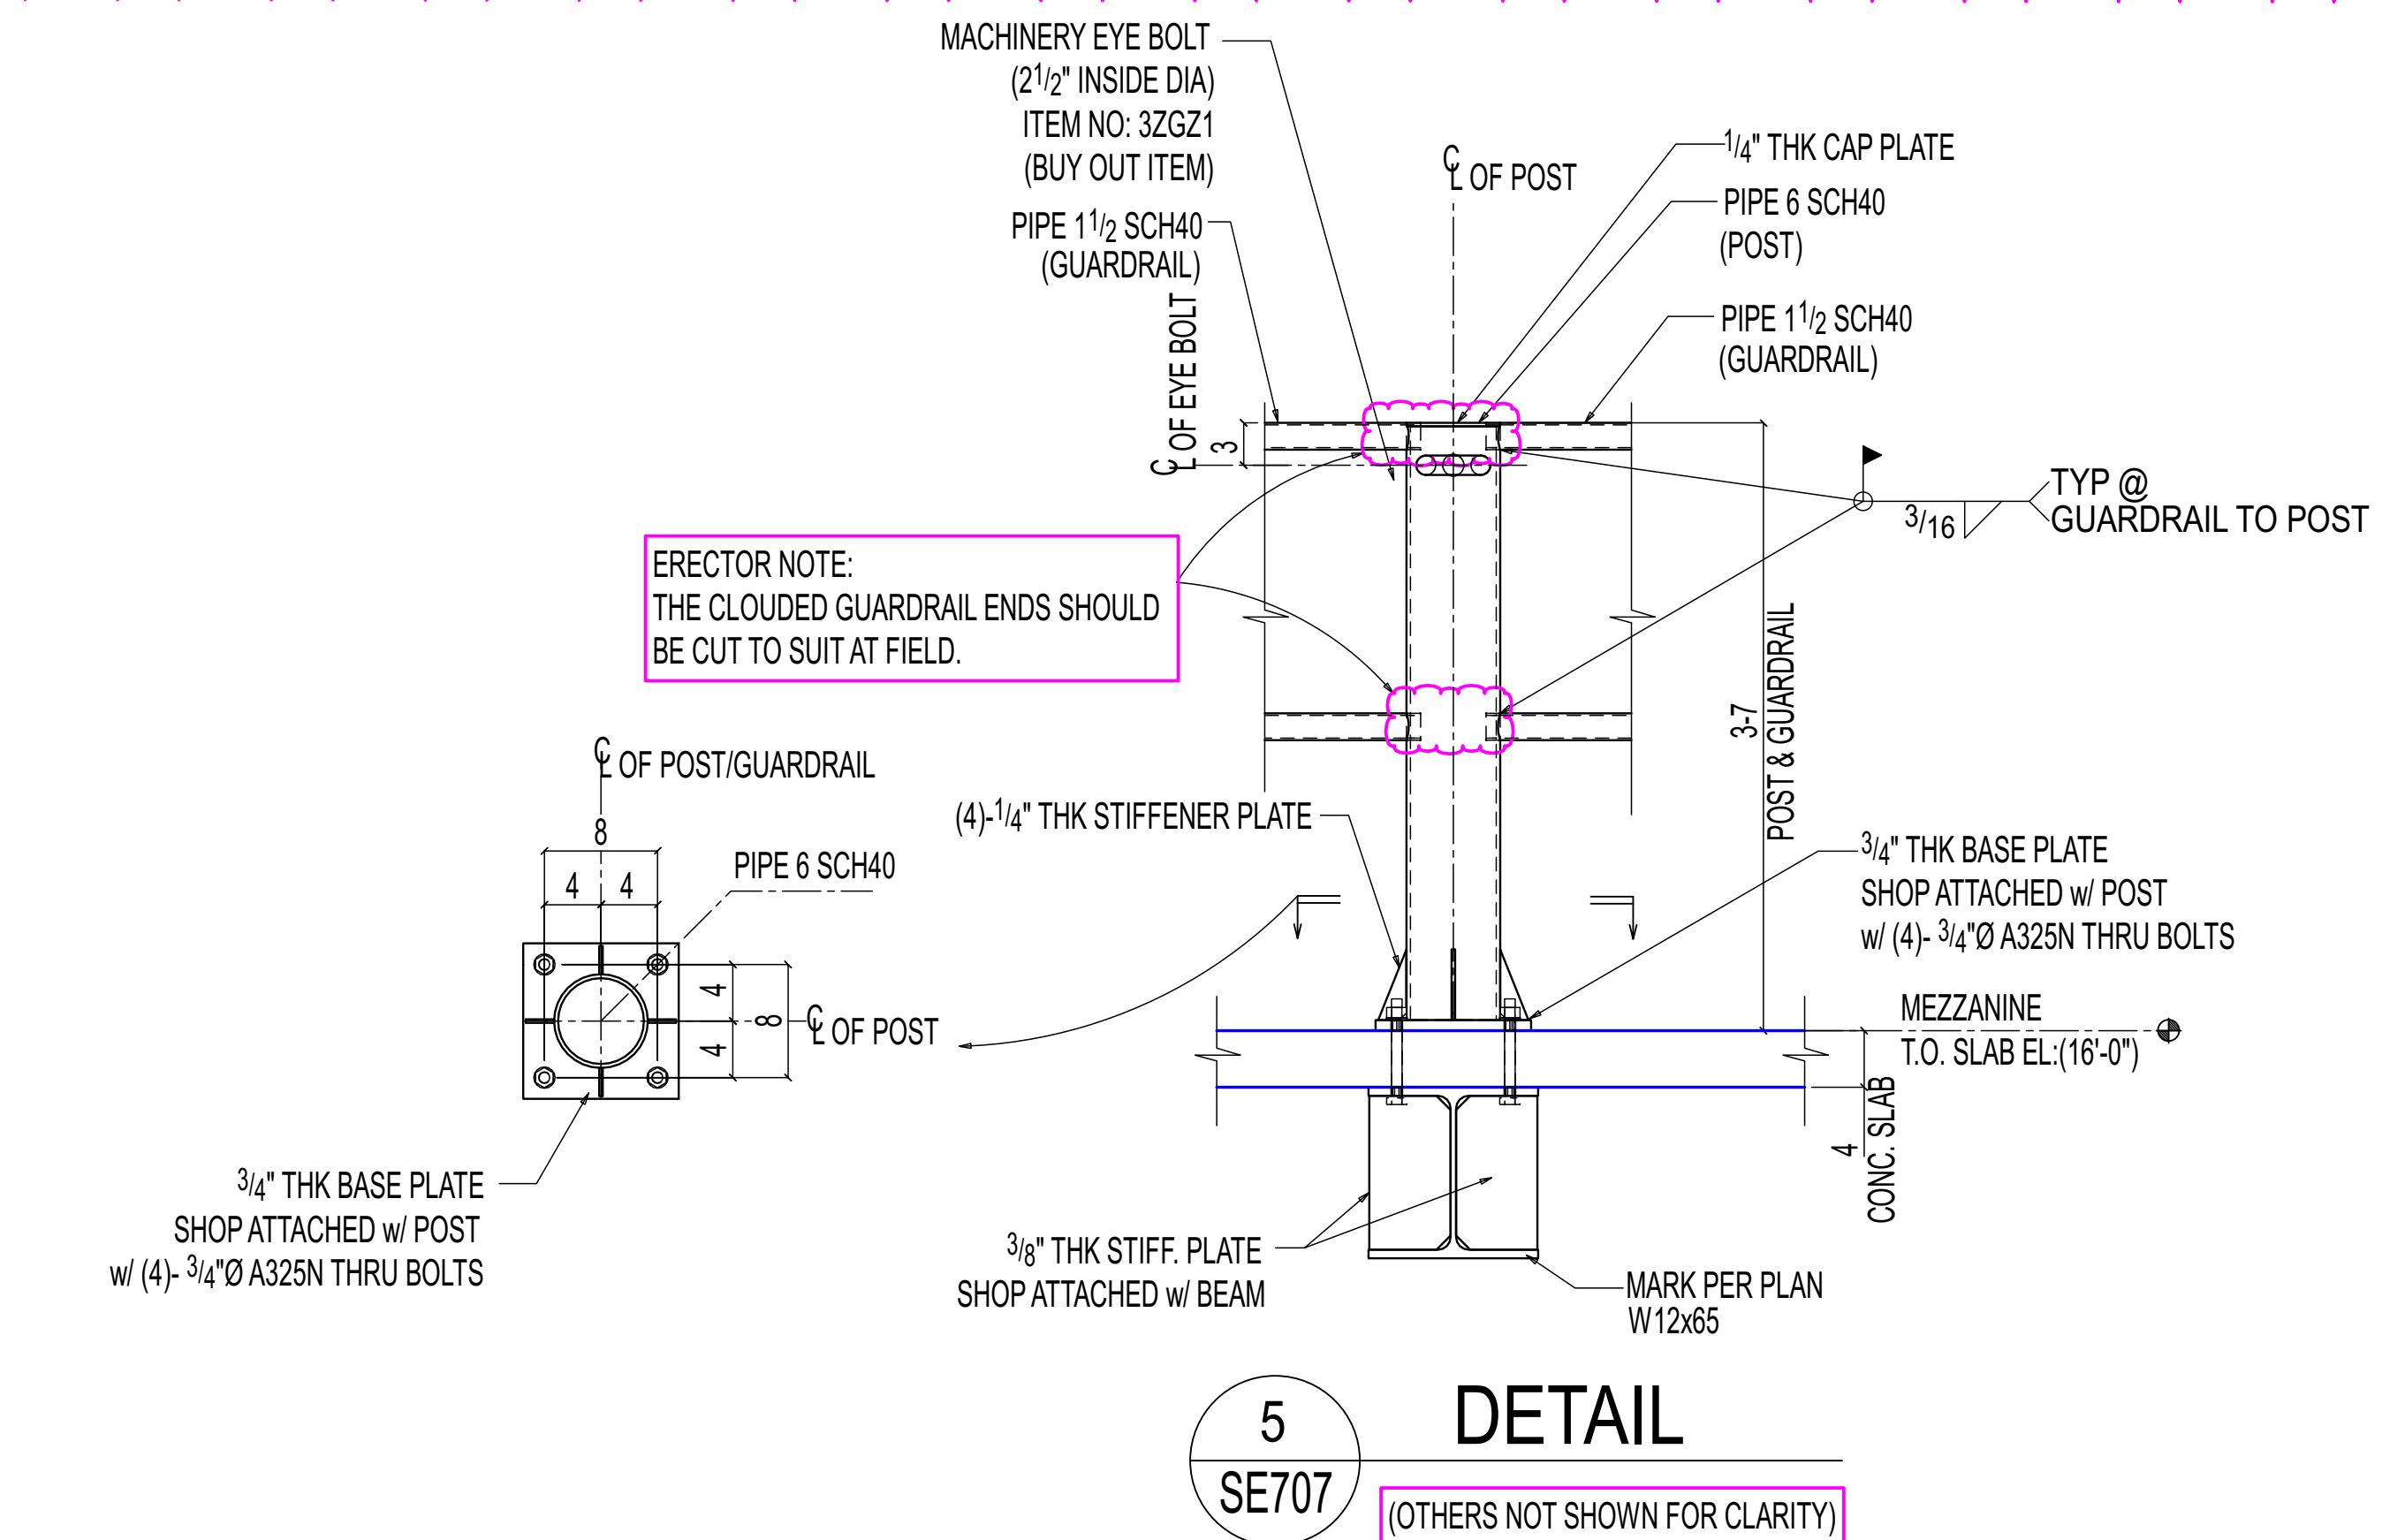

5 DETAIL
SE707
(OTHERS NOT SHOWN FOR CLARITY)

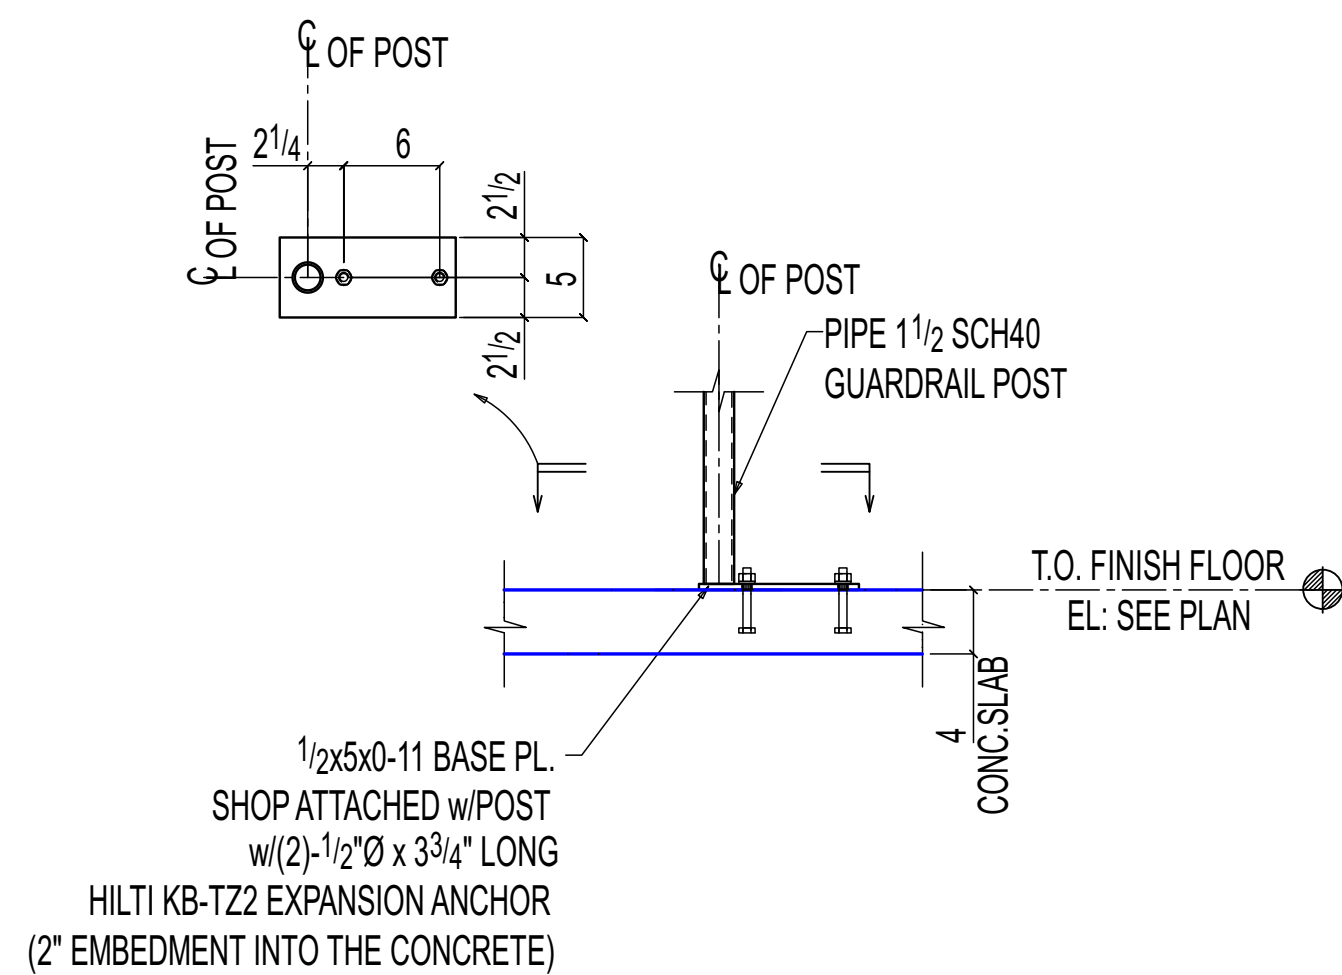


3 DETAIL
SE707
(OTHERS NOT SHOWN FOR CLARITY)

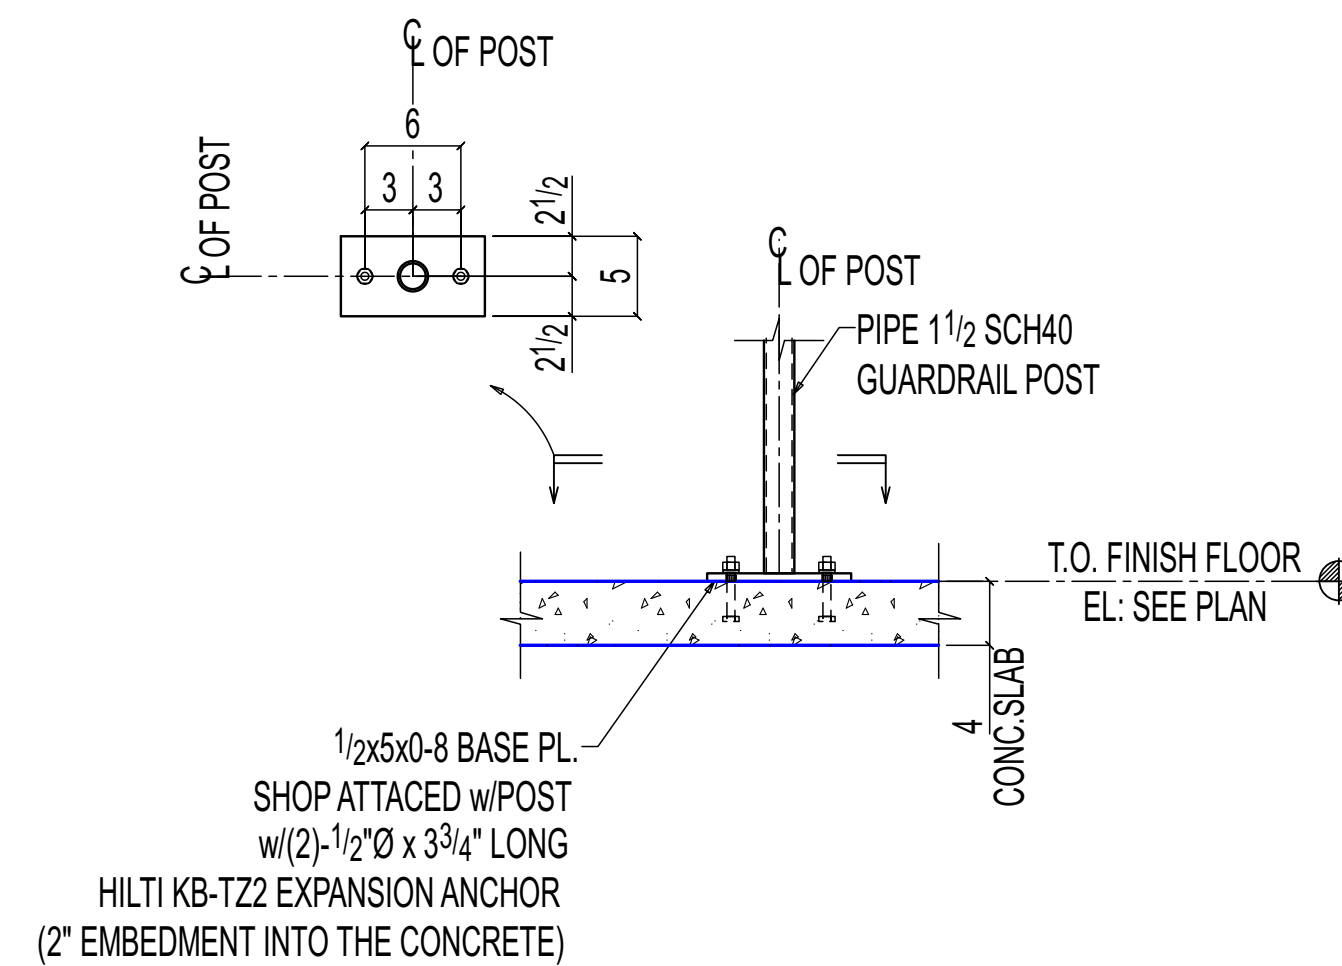

4 DETAIL
SE707
(OTHERS NOT SHOWN FOR CLARITY)

REVISIONS			
REV#	DWN BY	DESCRIPTION	DATE
A	SRP	ISSUED FOR APPROVAL	Jun 16 2025
0	GSV	ISSUED FOR CONSTRUCTION	Jan 27 2026
B	GSV	ISSUED FOR RE-APPROVAL	Feb 23 2026
1	GSV	ISSUED FOR CONSTRUCTION	Mar 11 2026

THE INFORMATION NOTED HEREON THIS DRAWING IS THE PROPERTY OF STEEL FAB ENTERPRISES, INC. AND SHALL NOTED BE USED WITHOUT WRITTEN CONSENT.

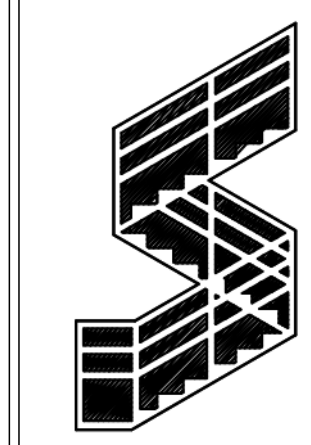

STEEL FAB ENTERPRISES, LLC

MISCELLANEOUS METALS FABRICATOR AND ERECTORS
623 BAUMGARDNER ROAD, LANCASTER, PA 17603
TEL. (717)464-0330 FAX (717)464-9464
WWW.STEELFABENTERPRISES.COM



CERTIFIED FABRICATOR AND ERECTOR

PROJECT OWNER : CK CAPITAL, LLC			
PROJECT DESCRIPTION : CLEVELAND BROTHERS-MILESBURG			
PROJECT ADDRESS : 4025N. EAGLE VALLEY ROAD, HOWARD, PA 16841			
CONTRACTOR : KINSLEY CONSTRUCTION, INC.			
DRAWN BY : BAS	DATE : 5-20-25	PROJ. NO. : 25012	REV # 
CHECKED BY : SRP	DATE : 5-20-25	DWG NO. : SE707	
DWG DESCRIPTION : GUARDRAIL ELEVATION VIEW			