


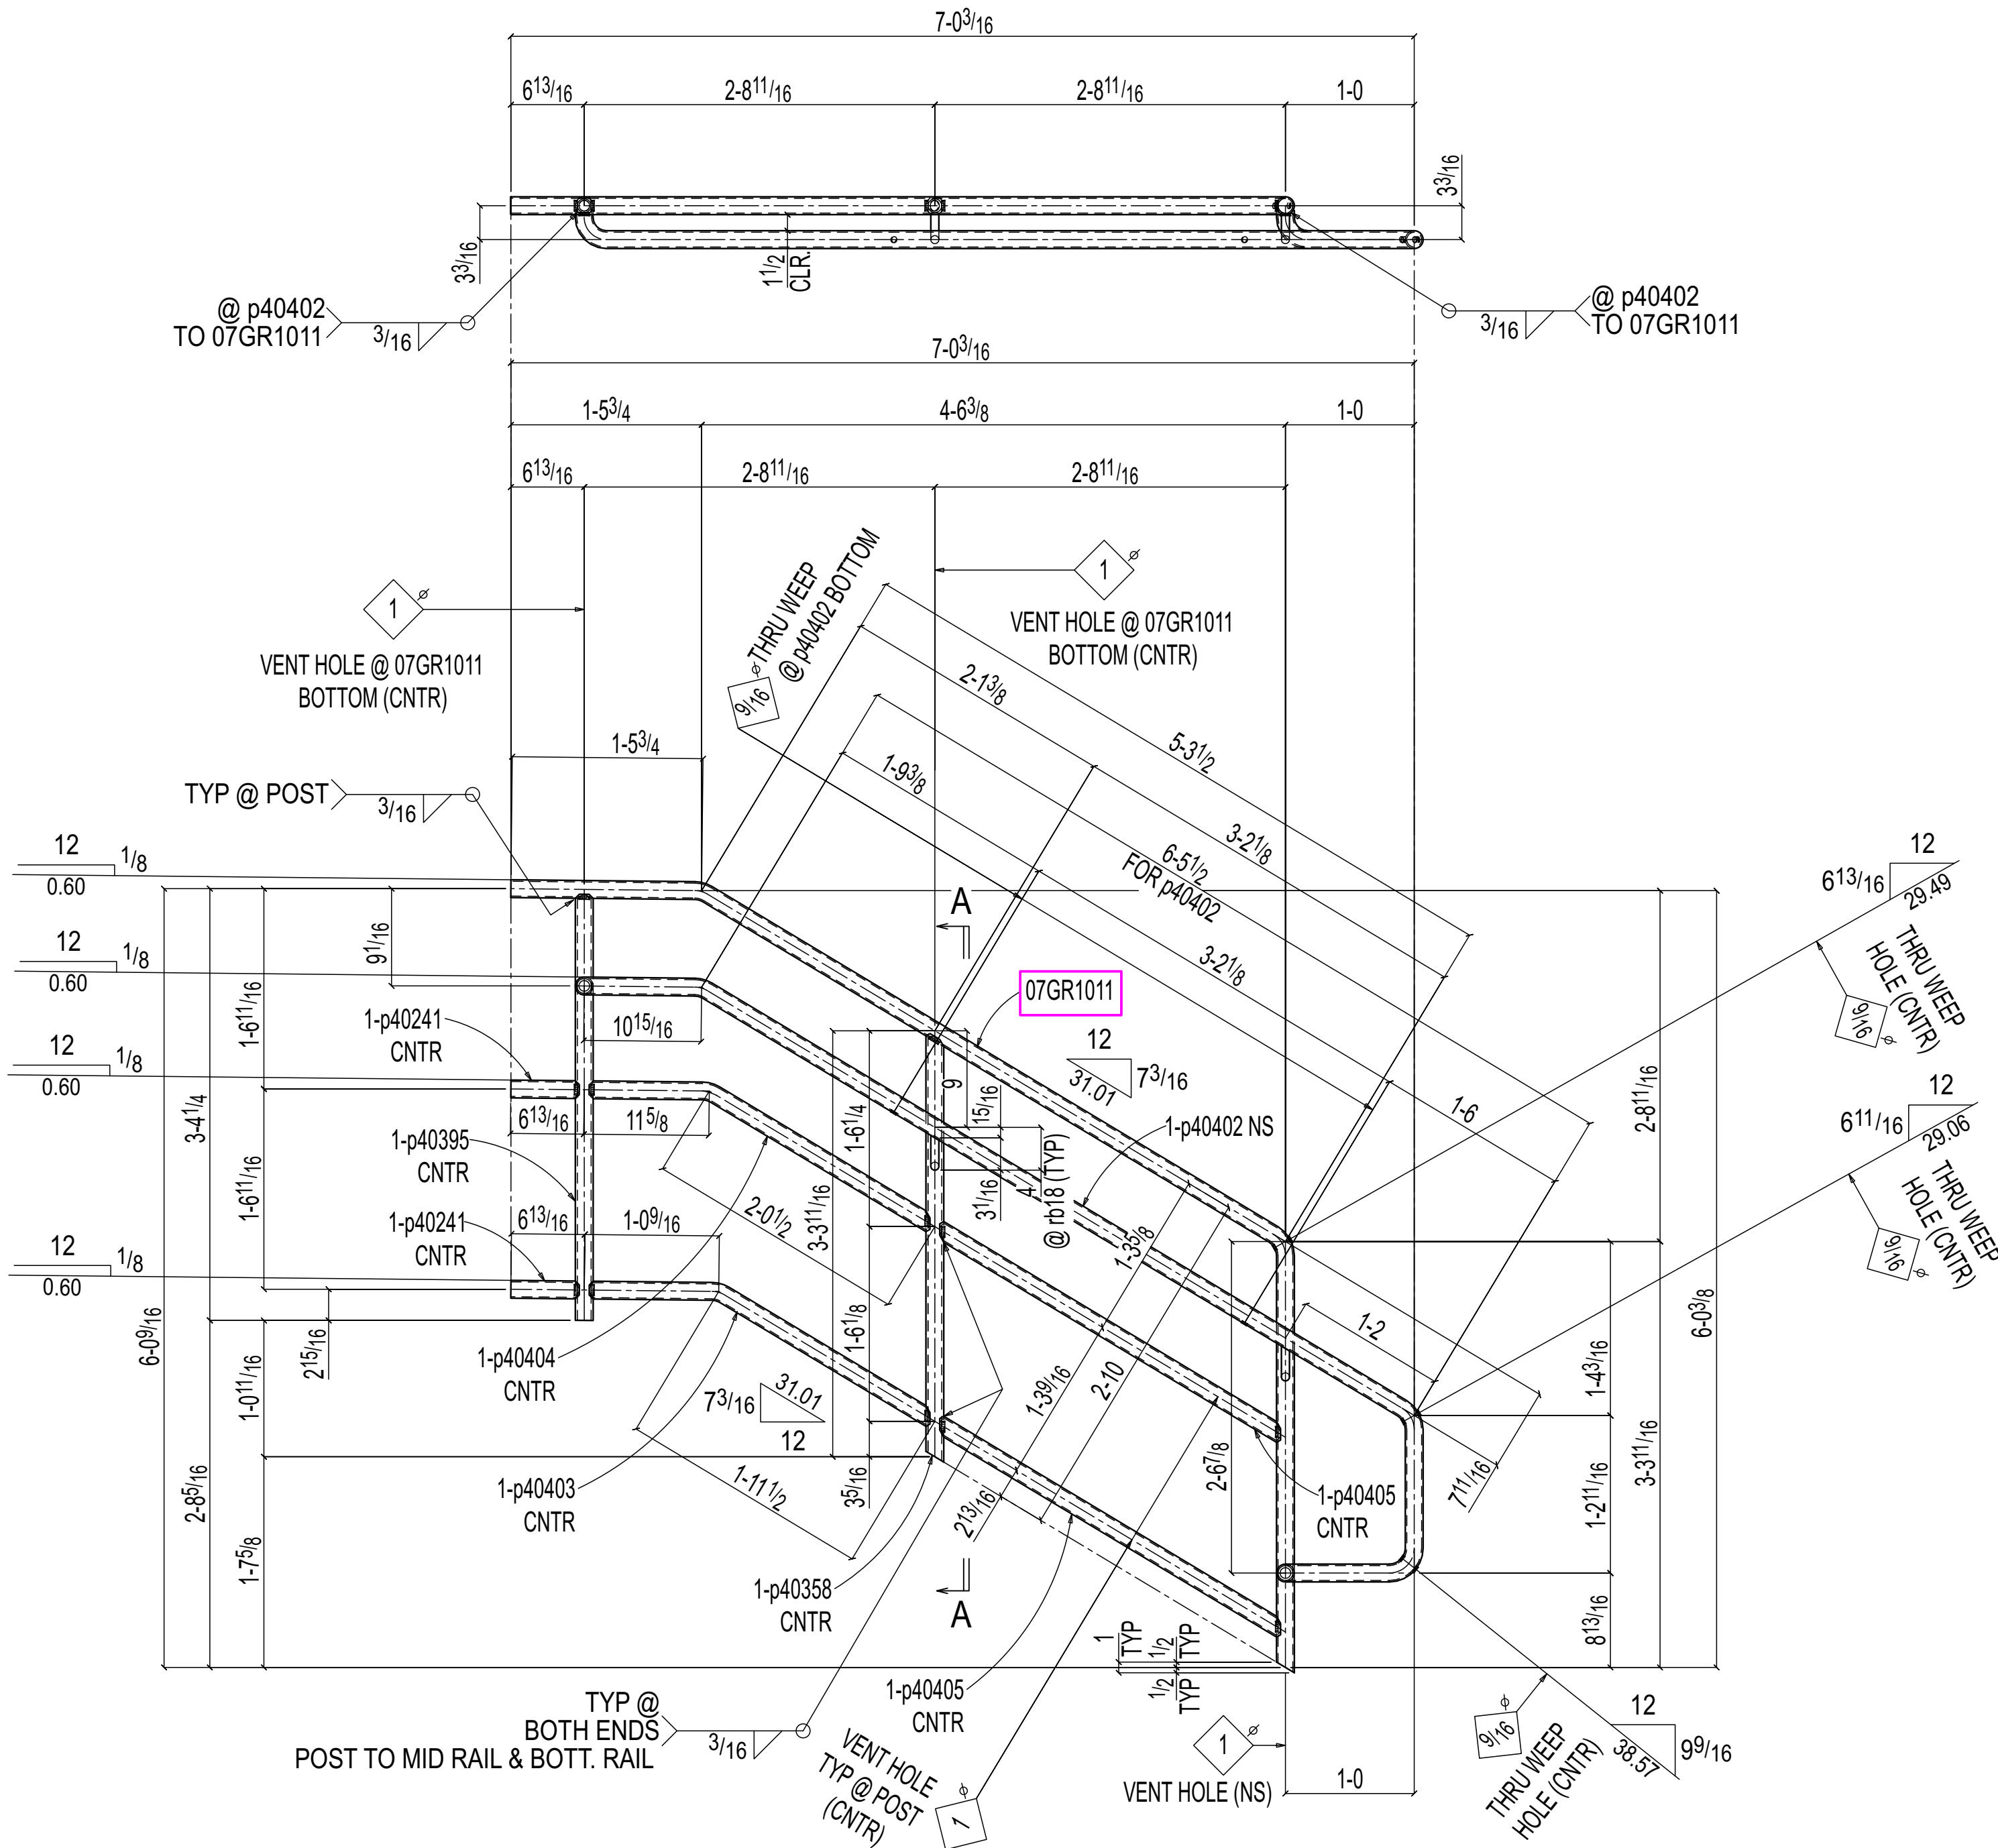

ONE GUARDRAIL 07GR1011

GALVANIZED

APPROVER,
PLEASE CONFIRM CLOUDED FINISH.

SHOP NOTE:
FINISH: NOMMA FINISH #3
1. PARTIALLY DRESSED WELD WITH SPATTER REMOVED.
2. GRIND SMOOTH GRABRAIL SPLICES.

SHOP NOTE:
1. ALL WEEP HOLES WILL BE 9/16" Ø (U.N.O)
2. PLUG ALL WEEP HOLES AFTER GALVANIZED


ALL RE-ENTRANT CUT
TO BE 1/2" RADIUS (U.N.O)
WELDS : E70XX
HOLES : 13/16" DIA (U.N.O)
MAT'L : A36 (U.N.O)
CLEAN : -
PAINT : GALVANIZED

REVISIONS

REV	DWN BY	DATE	DESCRIPTION
A	GSV	Jun 16 2025	ISSUED FOR APPROVAL
B	GSV	Feb 18 2026	ISSUED FOR RE-APPROVAL

BILL OF MATERIAL								
ASSEMBLY MARK	TOTAL QTY	SUB-PIECE MARK	UNIT QTY	MATERIAL DESCRIPTION	LENGTH		REMARKS	UNIT WEIGHT
					FT	IN		TOTAL WEIGHT
07GR1011	ONE			GUARDRAIL			Galv	96
	1	07GR1011	1	PIPE 1 1/4 SCH40	10	13 1/8	A53 GR B	23
	1	p40358	1	PIPE 1 1/4 SCH80	3	3 15/16	A53 GR B	10
	1	p40395	1	PIPE 1 1/4 SCH80	3	3 3/4	A53 GR B	10
	1	p40402	1	PIPE 1 1/4 SCH40	9	9 7/16	A53 GR B	22
	2	p40405	2	PIPE 1 1/4 SCH40	3	1 5/8	A53 GR B	7
	1	p40404	1	PIPE 1 1/4 SCH40	2	11 7/16	A53 GR B	7
	1	p40403	1	PIPE 1 1/4 SCH40	2	11 1/4	A53 GR B	7
	2	p40241	2	PIPE 1 1/4 SCH40	0	6 3/8	A53 GR B	1
	2	rb18	2	3/4" Ø ROUND BAR	0	5 1/8	A36	1

Total weight : 96

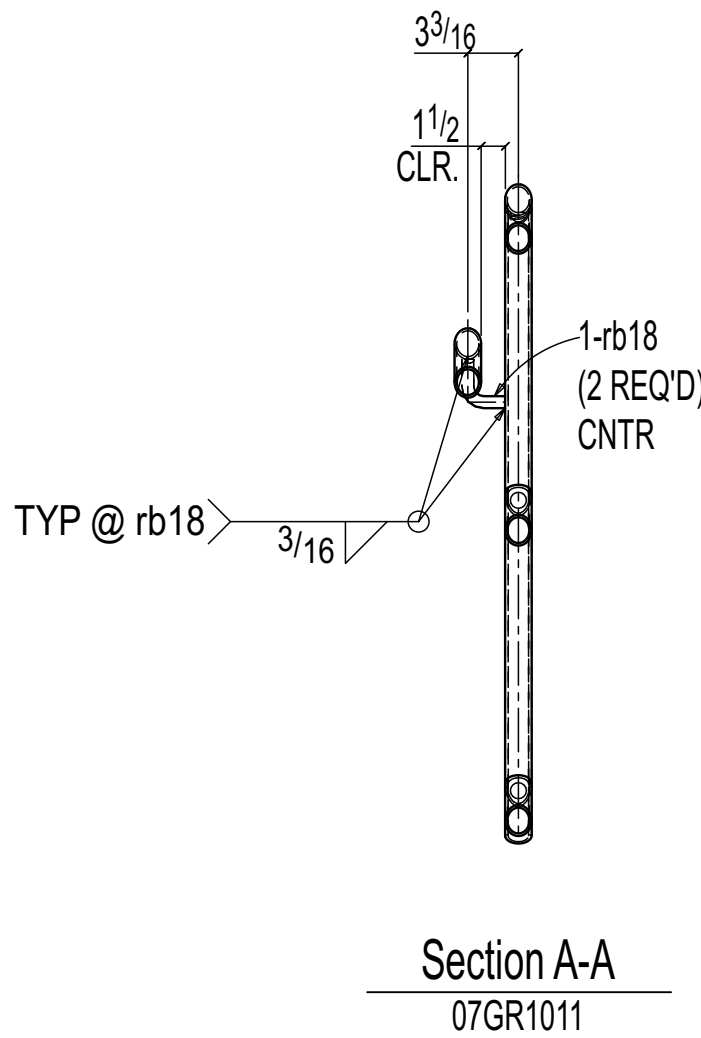

THE INFORMATION NOTED HEREON THIS DRAWING IS THE
PROPERTY OF STEEL FAB ENTERPRISES, INC. AND SHALL
NOTED BE USED WITHOUT WRITTEN CONSENT.



STEEL FAB
ENTERPRISES, LLC

MISCELLANEOUS METALS FABRICATOR AND ERECTORS
623 BAUMGARDNER ROAD, LANCASTER, PA 17603
TEL. (717)464-0330 FAX (717)464-9464
WWW.STEELFABENTERPRISES.COM



PROJECT OWNER : CK CAPITAL, LLC
PROJECT DESCRIPTION : CLEVELAND BROTHERS-MILESBURG
PROJECT ADDRESS : 1025N. EAGLE VALLY ROAD, HOWARD, PA 16841

CONTRACTOR : KINSLEY CONSTRUCTION, INC.			
DRAWN BY: BAS	DATE : 06-07-2025	PROJ. NO. : 25012	REV # 
CHECKED BY: GSV	DATE : 06-09-2025	DWG NO. : 07GR1011	
DWG DESCRIPTION : GUARDRAIL DETAIL			